



NAMA PROYEK	RUMAH TINGGAL 2 LANTAI	
LOKASI PROYEK	-	
PENANGGUNG JAWAB	-	
DIGAMBAR	PELAKSANA	
DISETUJUI	PEMILIK	
CATATAN	<p>1. PELAKSANA ATAU SUBKON WAJIB MEMERIKSA KEMBALI KESESUAIN GAMBAR DENGAN KONDISI LAPANGAN</p>	
JUDUL GAMBAR	SKALA	
1. ARS	1 : 100	
TANGGAL :	REVISI :	
5 AGUSTUS 2024	R1	
KODE GAMBAR	ARS-01-01	
NO. LBR	JUMLAH LBR	
00	00	

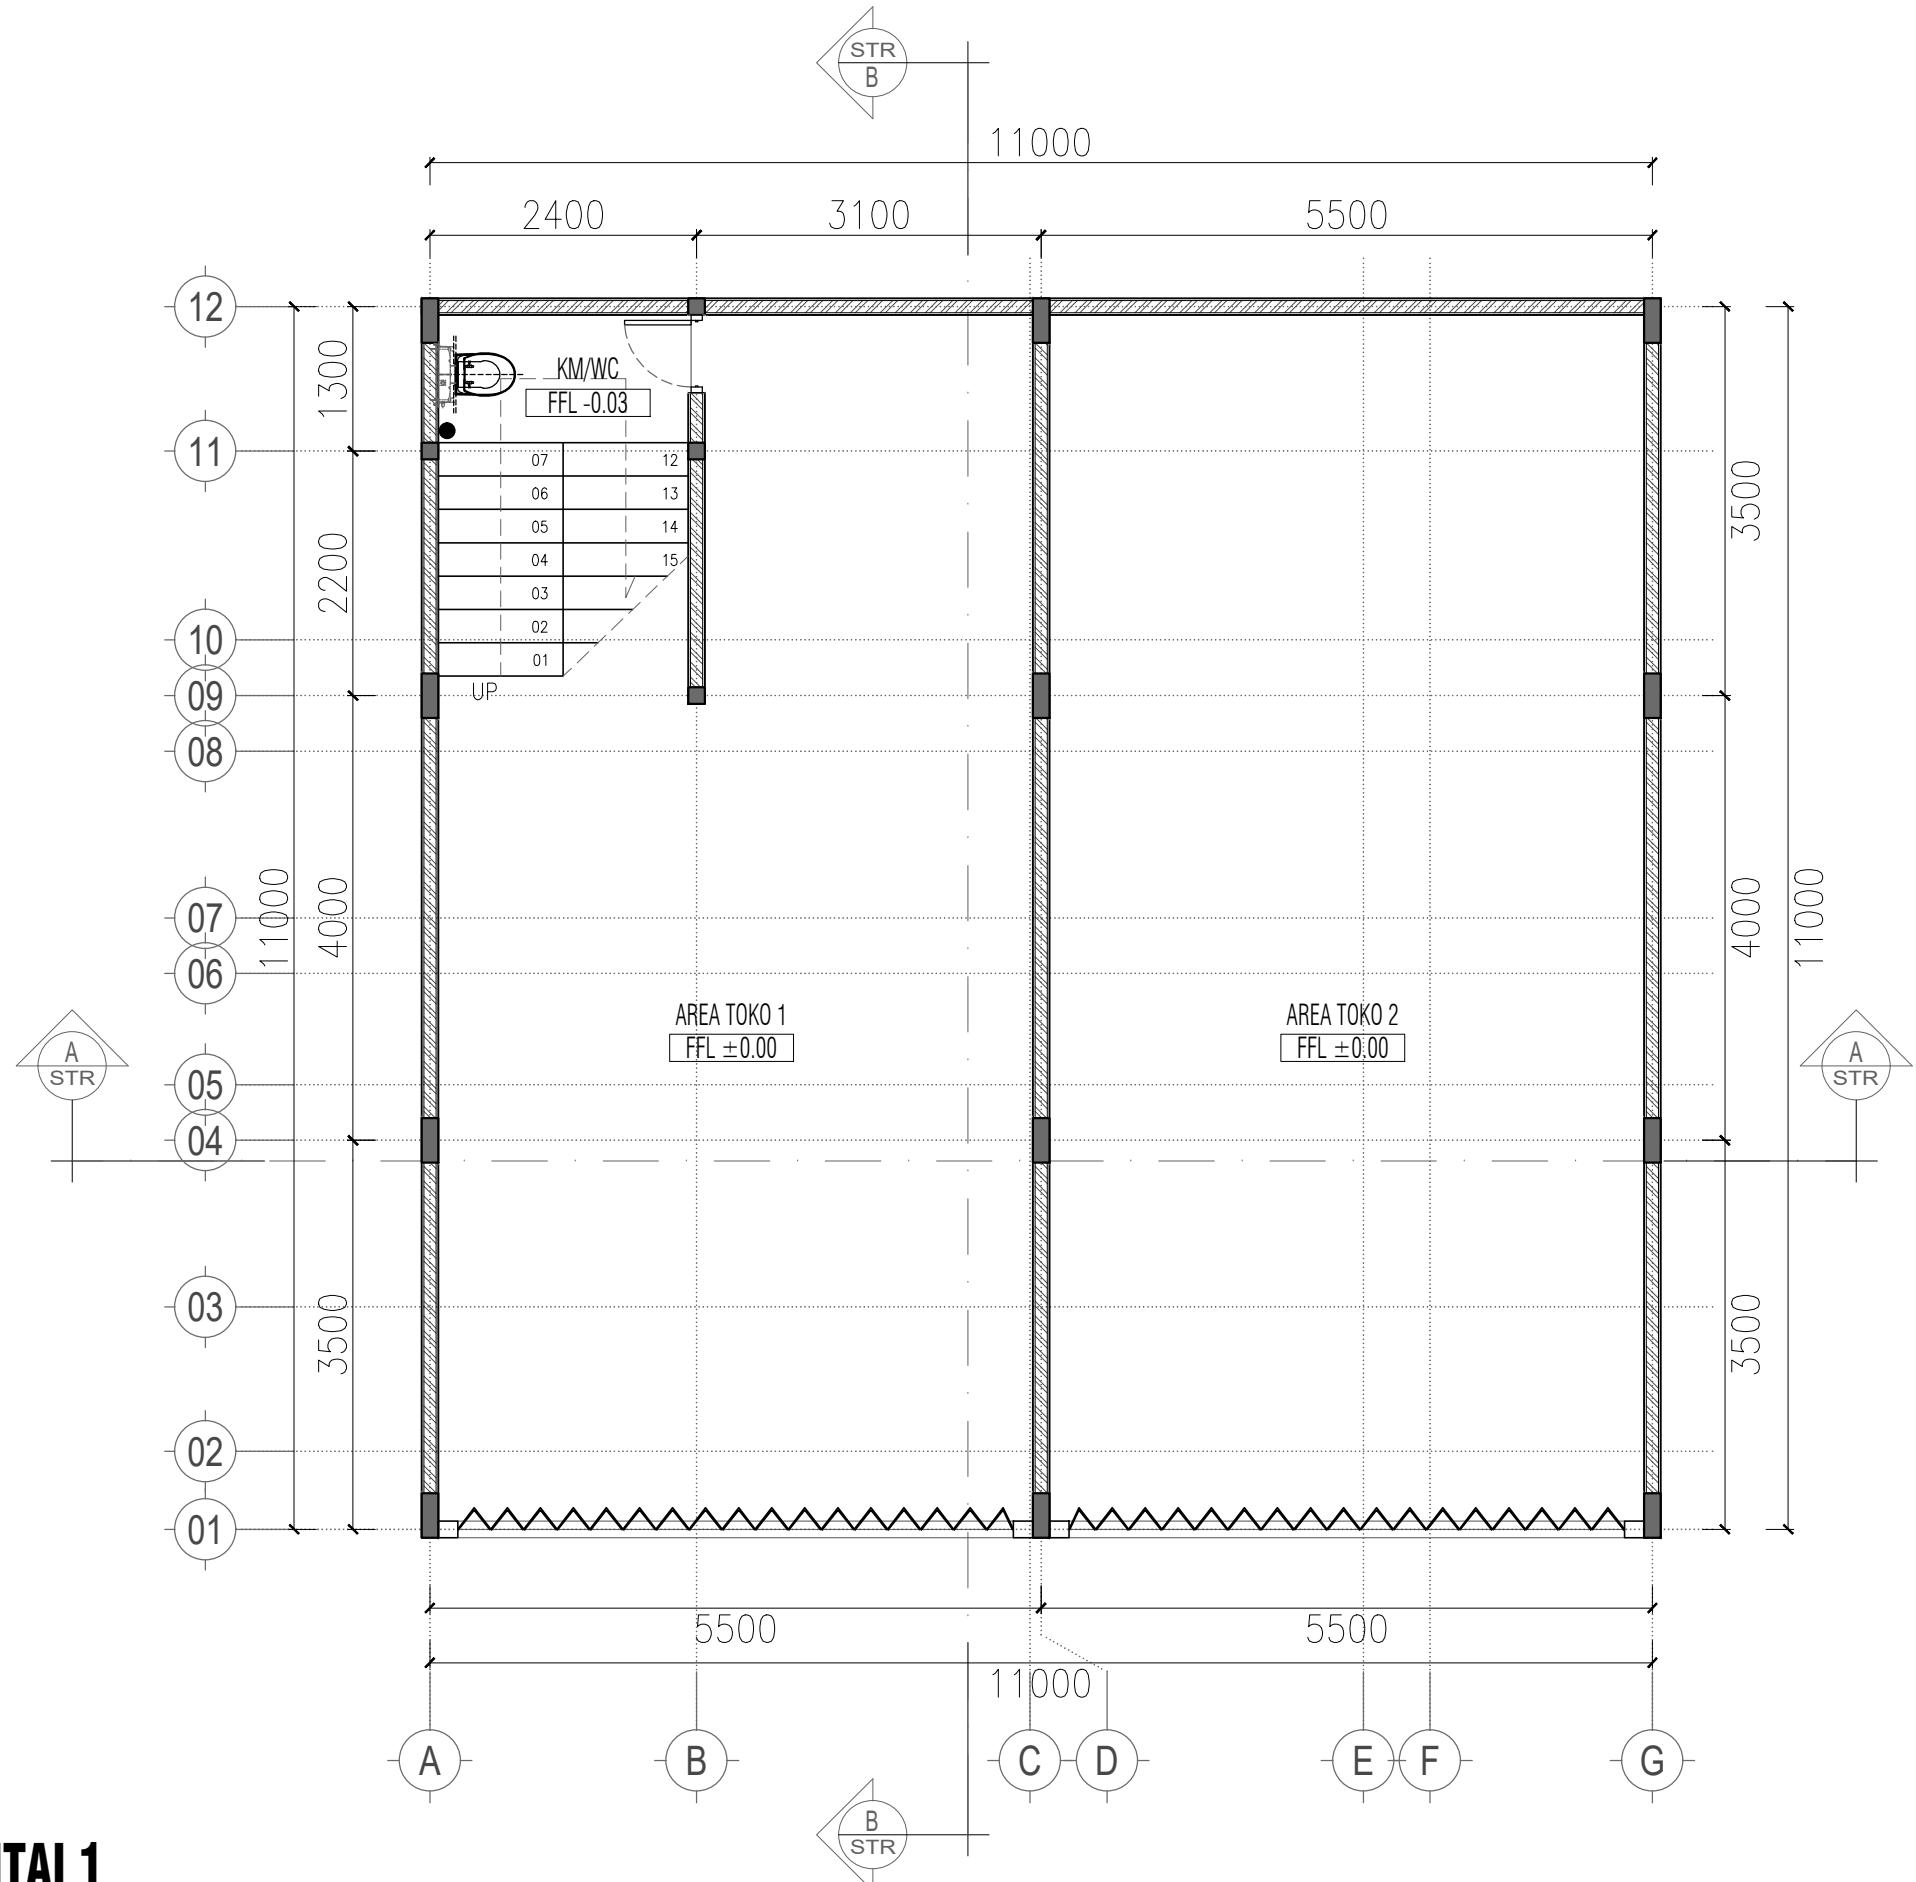


DENAH LANTAI 1  
SKALA 1 : 100

NAMA PROYEK	RUMAH TINGGAL 2 LANTAI
LOKASI PROYEK	-
PENANGGUNG JAWAB	
DIGAMBAR	PELAKSANA
DISETUJUI	PEMILIK
CATATAN	<p>1. PELAKSANA ATAU SUBKON WAJIB MEMERIKSA KEMBALI KESESUAIN GAMBAR DENGAN KONDISI LAPANGAN</p>
JUDUL GAMBAR	SKALA
1. ARS	1 : 100
TANGGAL :	REVISI :
5 AGUSTUS 2024	R1
KODE GAMBAR	
ARS-01-01	
NO. LBR	JUMLAH LBR
00	00

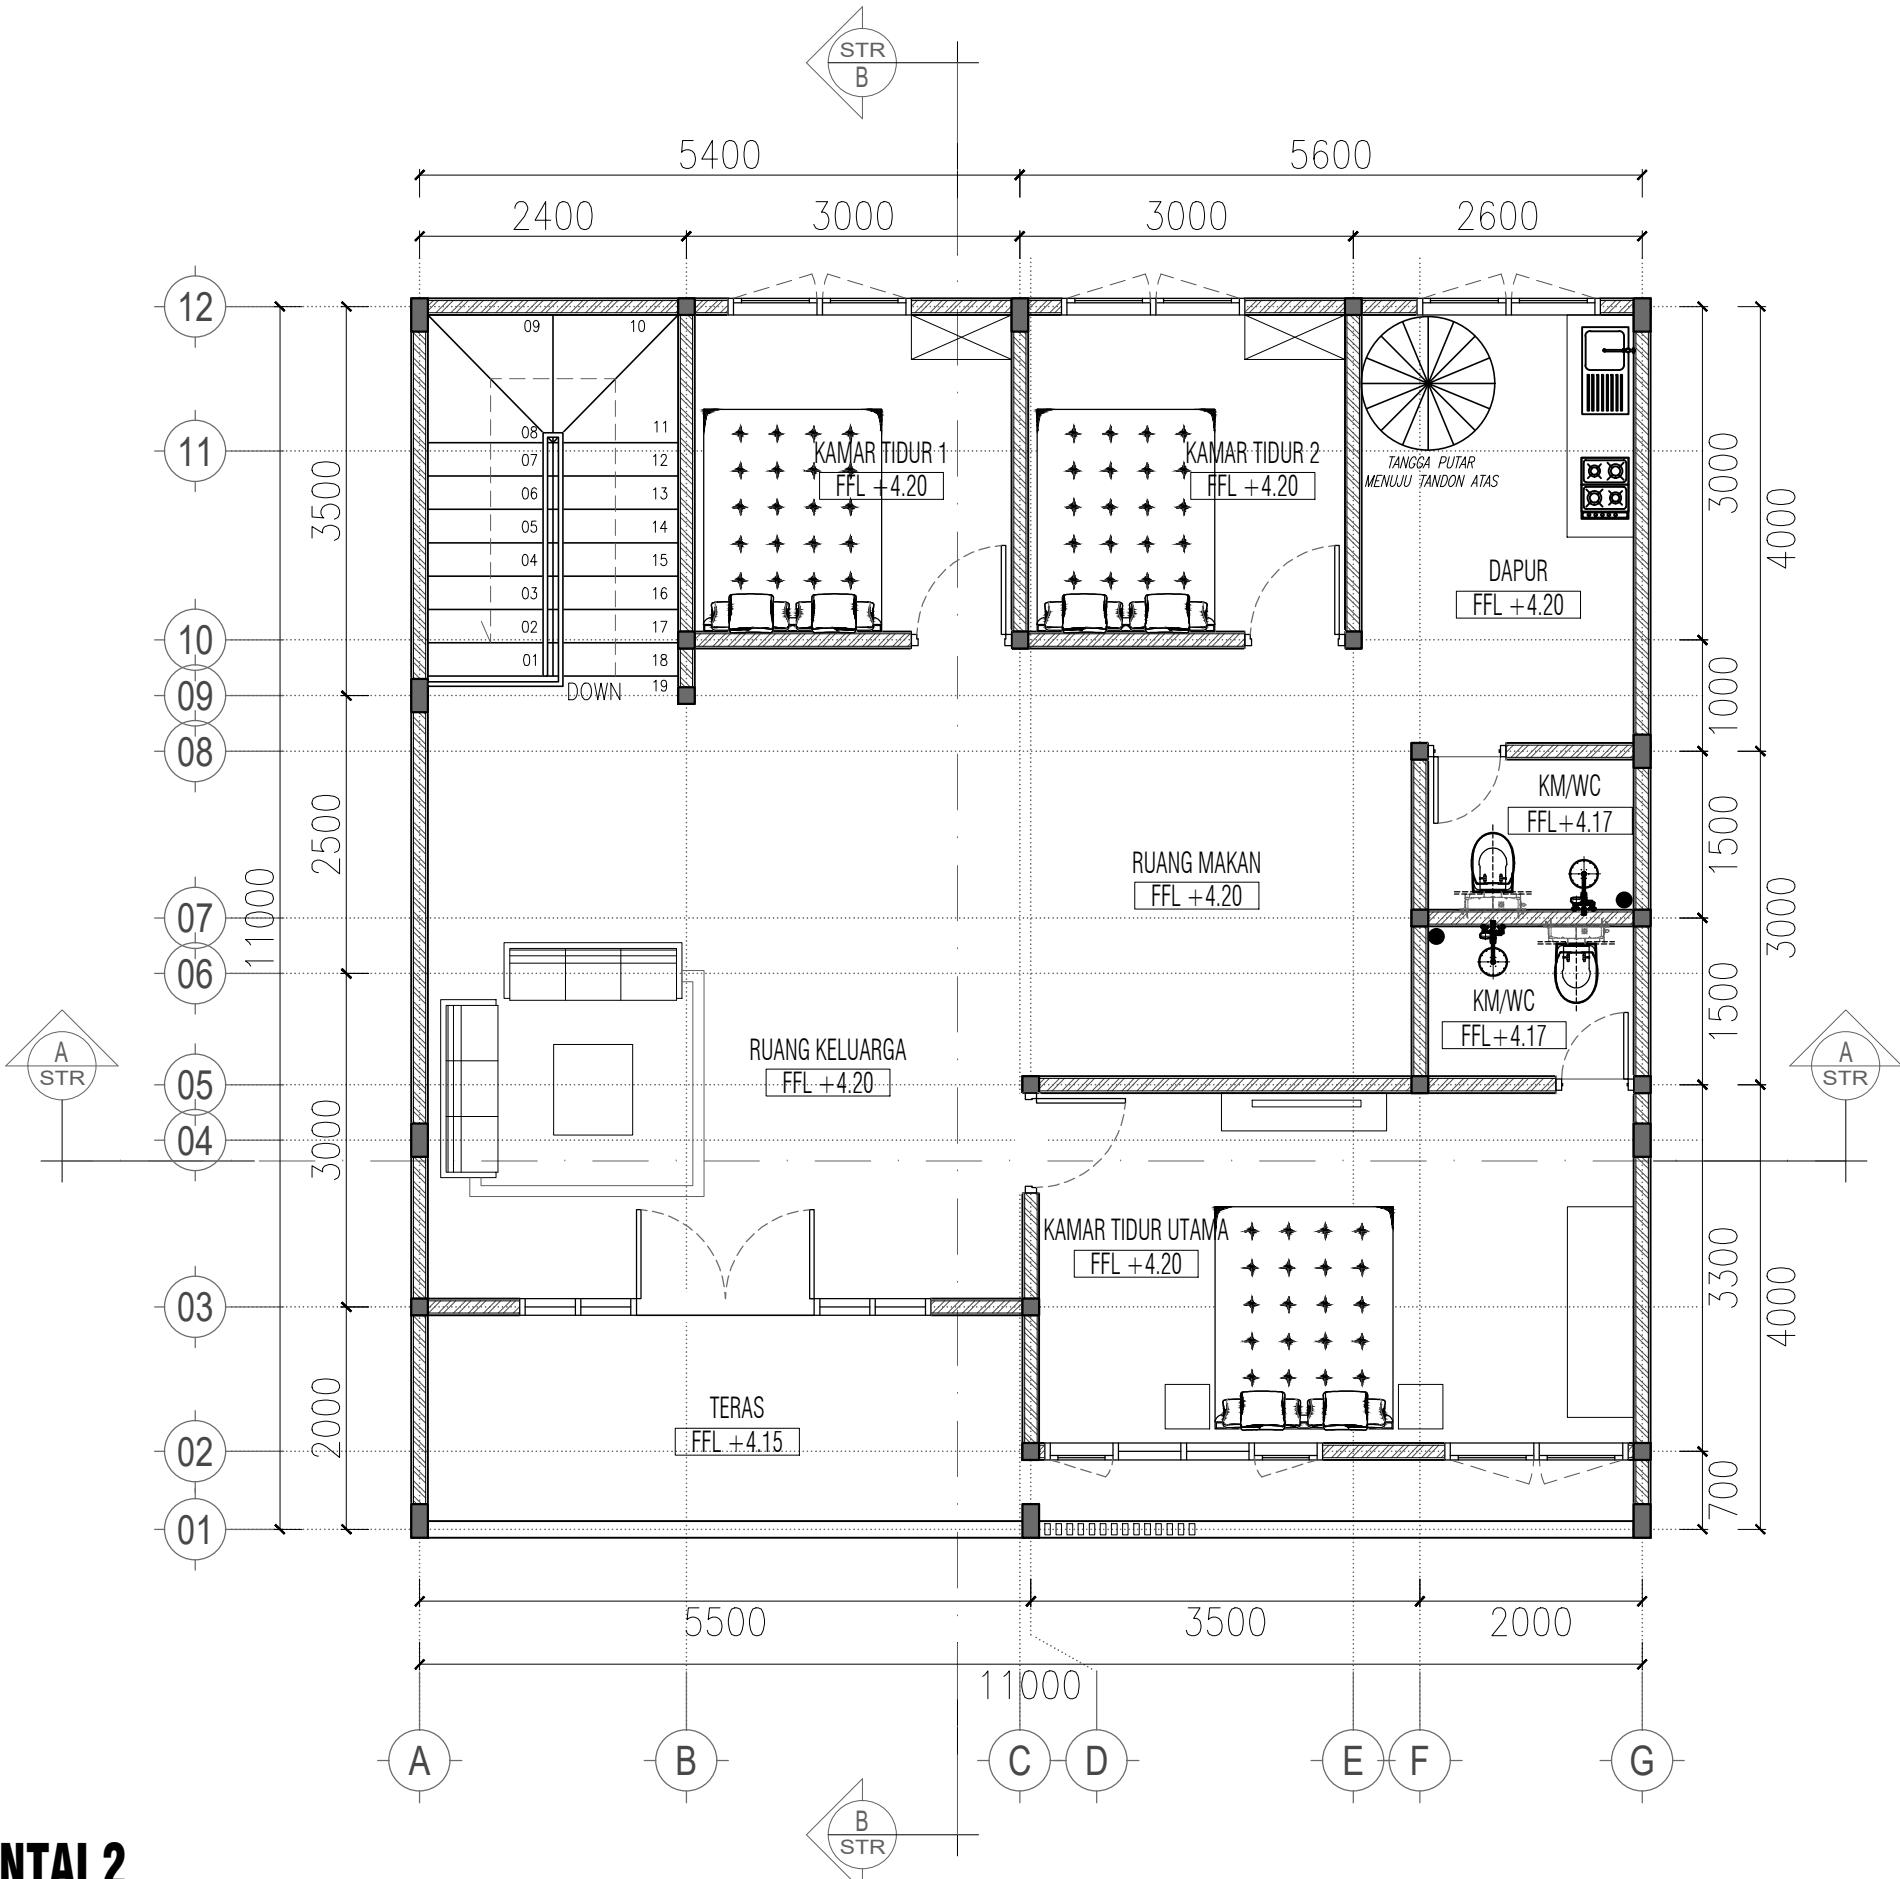


**DENAH LANTAI 2**  
SKALA 1 : 100

NAMA PROYEK	
<b>RUMAH TINGGAL 2 LANTAI</b>	
LOKASI PROYEK	
-	-
PENANGGUNG JAWAB	
DIGAMBAR	PELAKSANA
DISETUJUI	PEMILIK
CATATAN	
1. PELAKSANA ATAU SUBKON WAJIB MEMERIKSA KEMBALI KESESUAIN GAMBAR DENGAN KONDISI LAPANGAN	
JUDUL GAMBAR	SKALA
1. ARS	1 : 100
TANGGAL :	REVISI :
5 AGUSTUS 2024	<b>R1</b>
KODE GAMBAR	
ARS-01-01	
NO. LBR	JUMLAH LBR
00	00

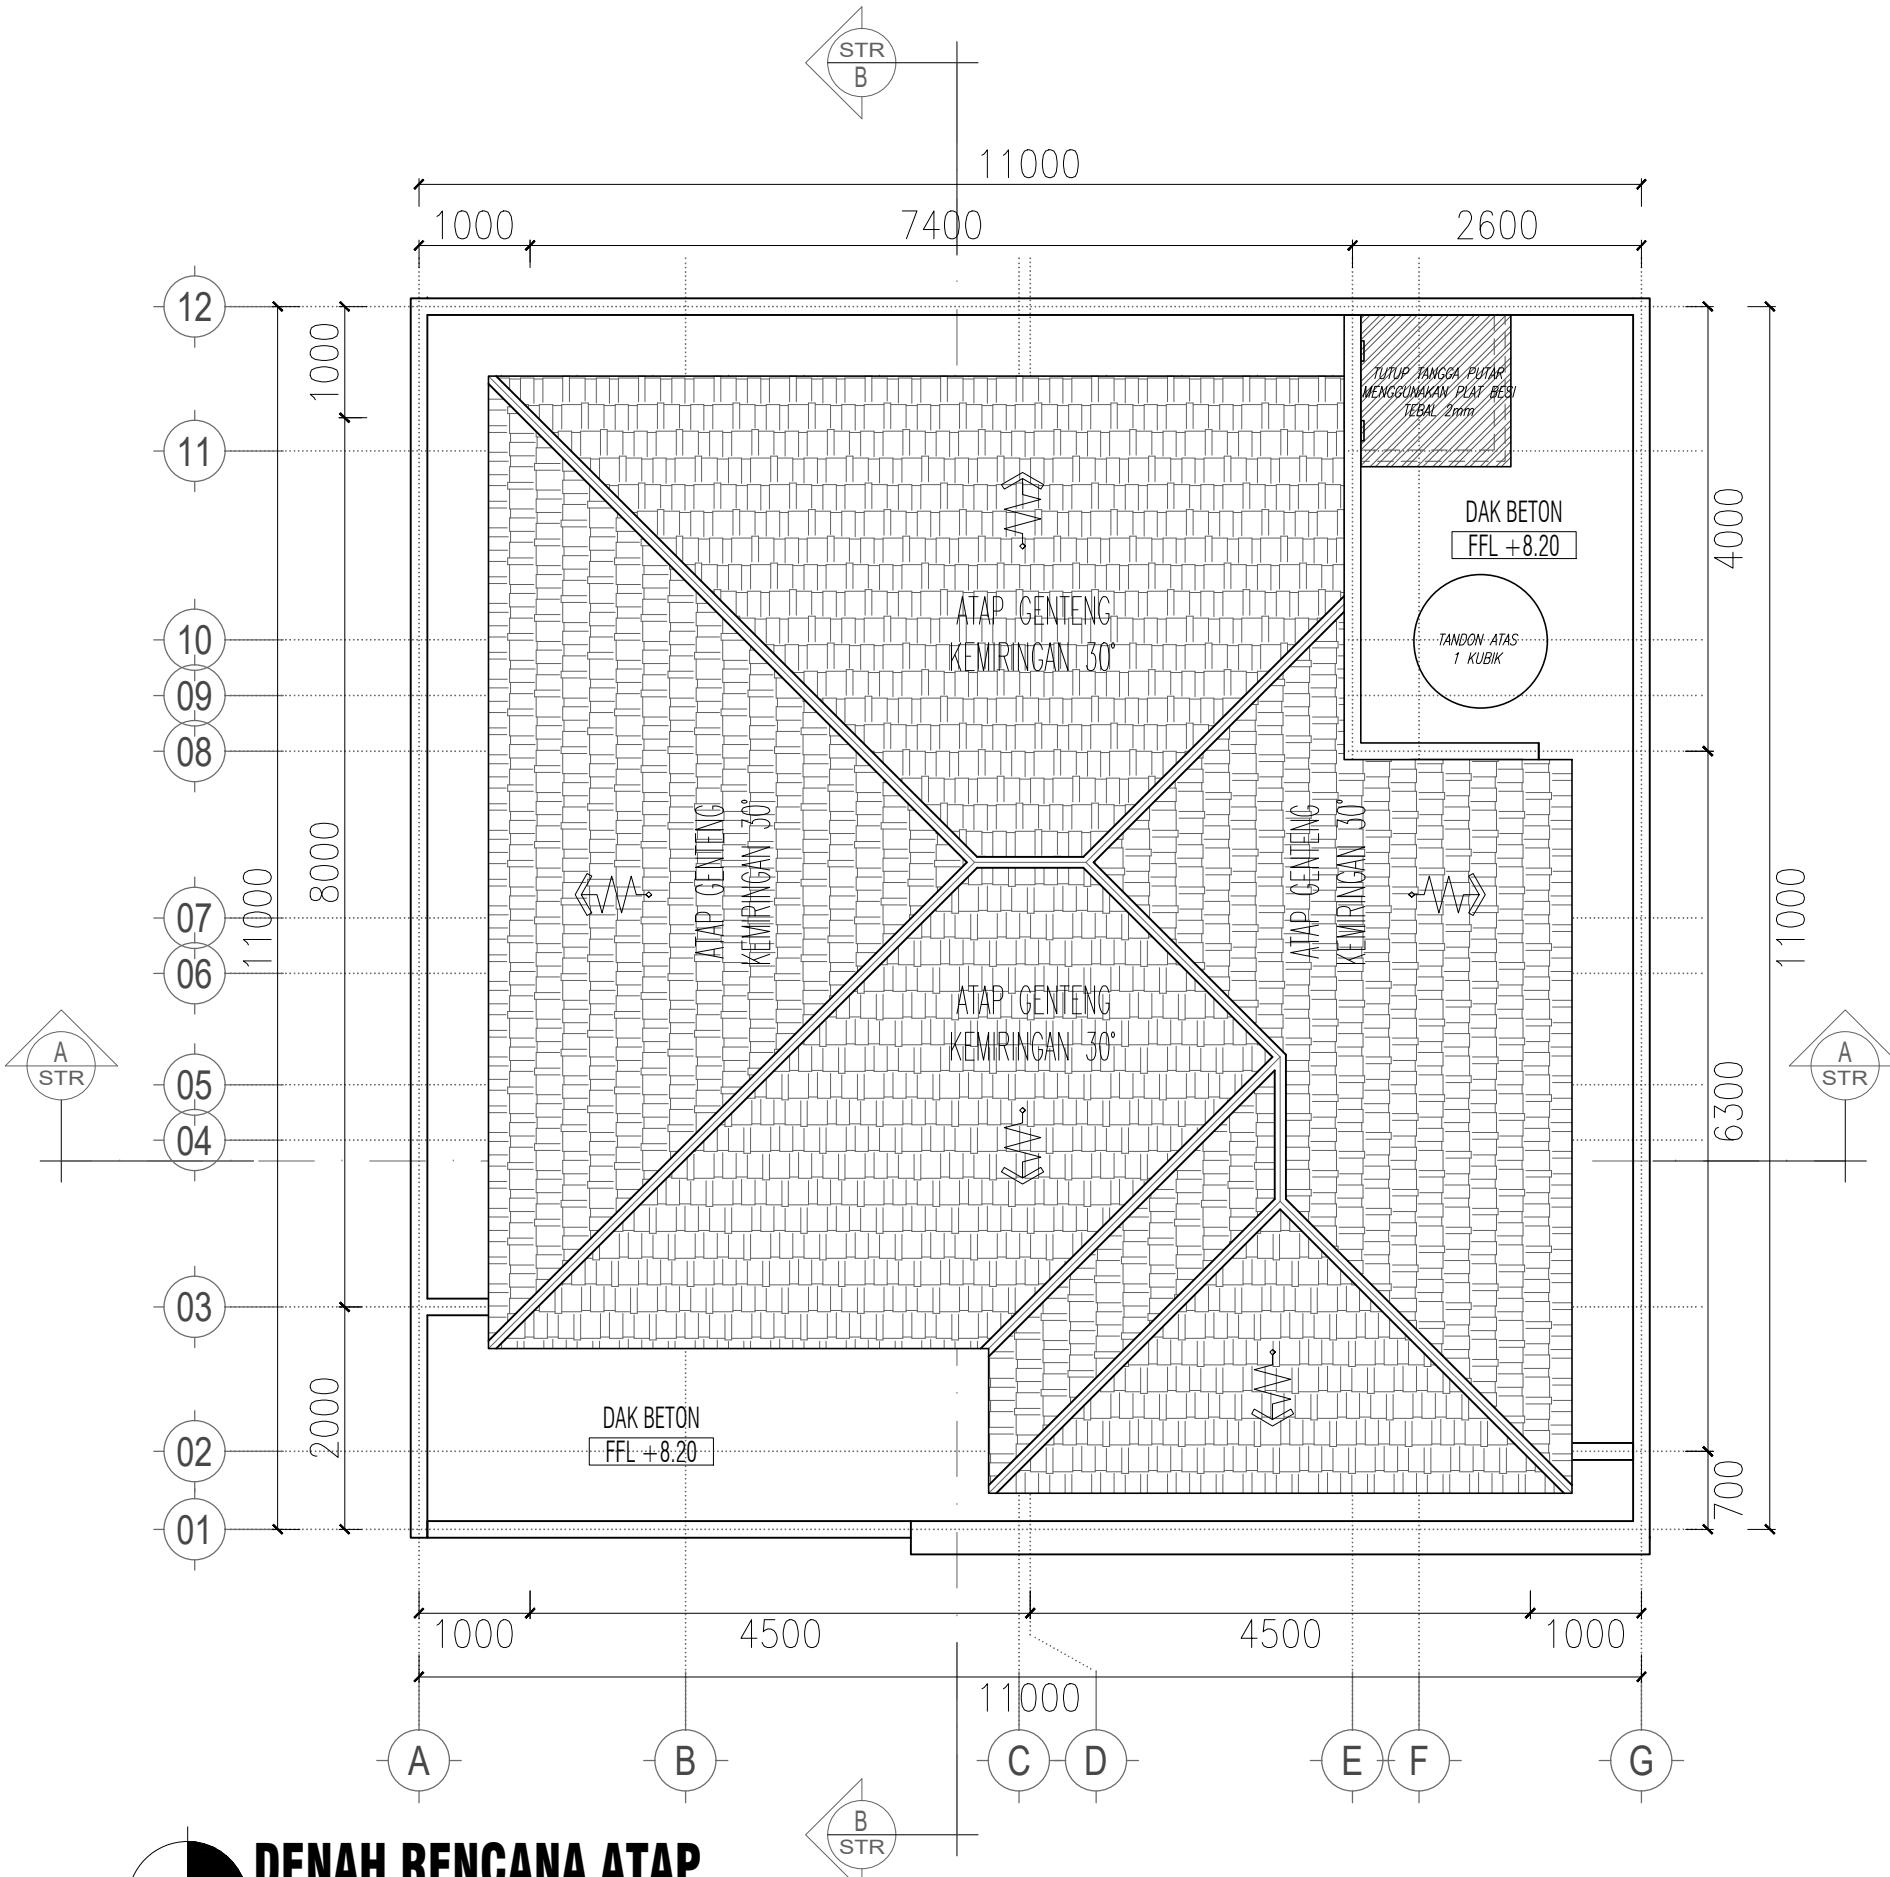


NAMA PROYEK	
<b>RUMAH TINGGAL 2 LANTAI</b>	
LOKASI PROYEK	
-	
-	
PENANGGUNG JAWAB	
DIGAMBAR	PELAKSANA
DISETUJUI	PEMILIK
CATATAN	
<p>1. PELAKSANA ATAU SUBKON WAJIB MEMERIKSA KEMBALI KESESUAIN GAMBAR DENGAN KONDISI LAPANGAN</p>	
JUDUL GAMBAR	
SKALA	
1. ARS	1 : 100
TANGGAL :	
REVISI :	
5 AGUSTUS 2024 R1	
KODE GAMBAR	
ARS-01-01	
NO. LBR	JUMLAH LBR
00	00

NAMA PROYEK	
<b>RUMAH TINGGAL 2 LANTAI</b>	
LOKASI PROYEK	
-	-
PENANGGUNG JAWAB	
DIGAMBAR	PELAKSANA
DISETUJUI	PEMILIK
CATATAN	
1. PELAKSANA ATAU SUBKON WAJIB MEMERIKSA KEMBALI KESESUAIN GAMBAR DENGAN KONDISI LAPANGAN	
JUDUL GAMBAR	SKALA
1. ARS	1 : 100
TANGGAL :	REVISI :
5 AGUSTUS 2024	<b>R1</b>
KODE GAMBAR	
ARS-01-01	
NO. LBR	JUMLAH LBR
00	00

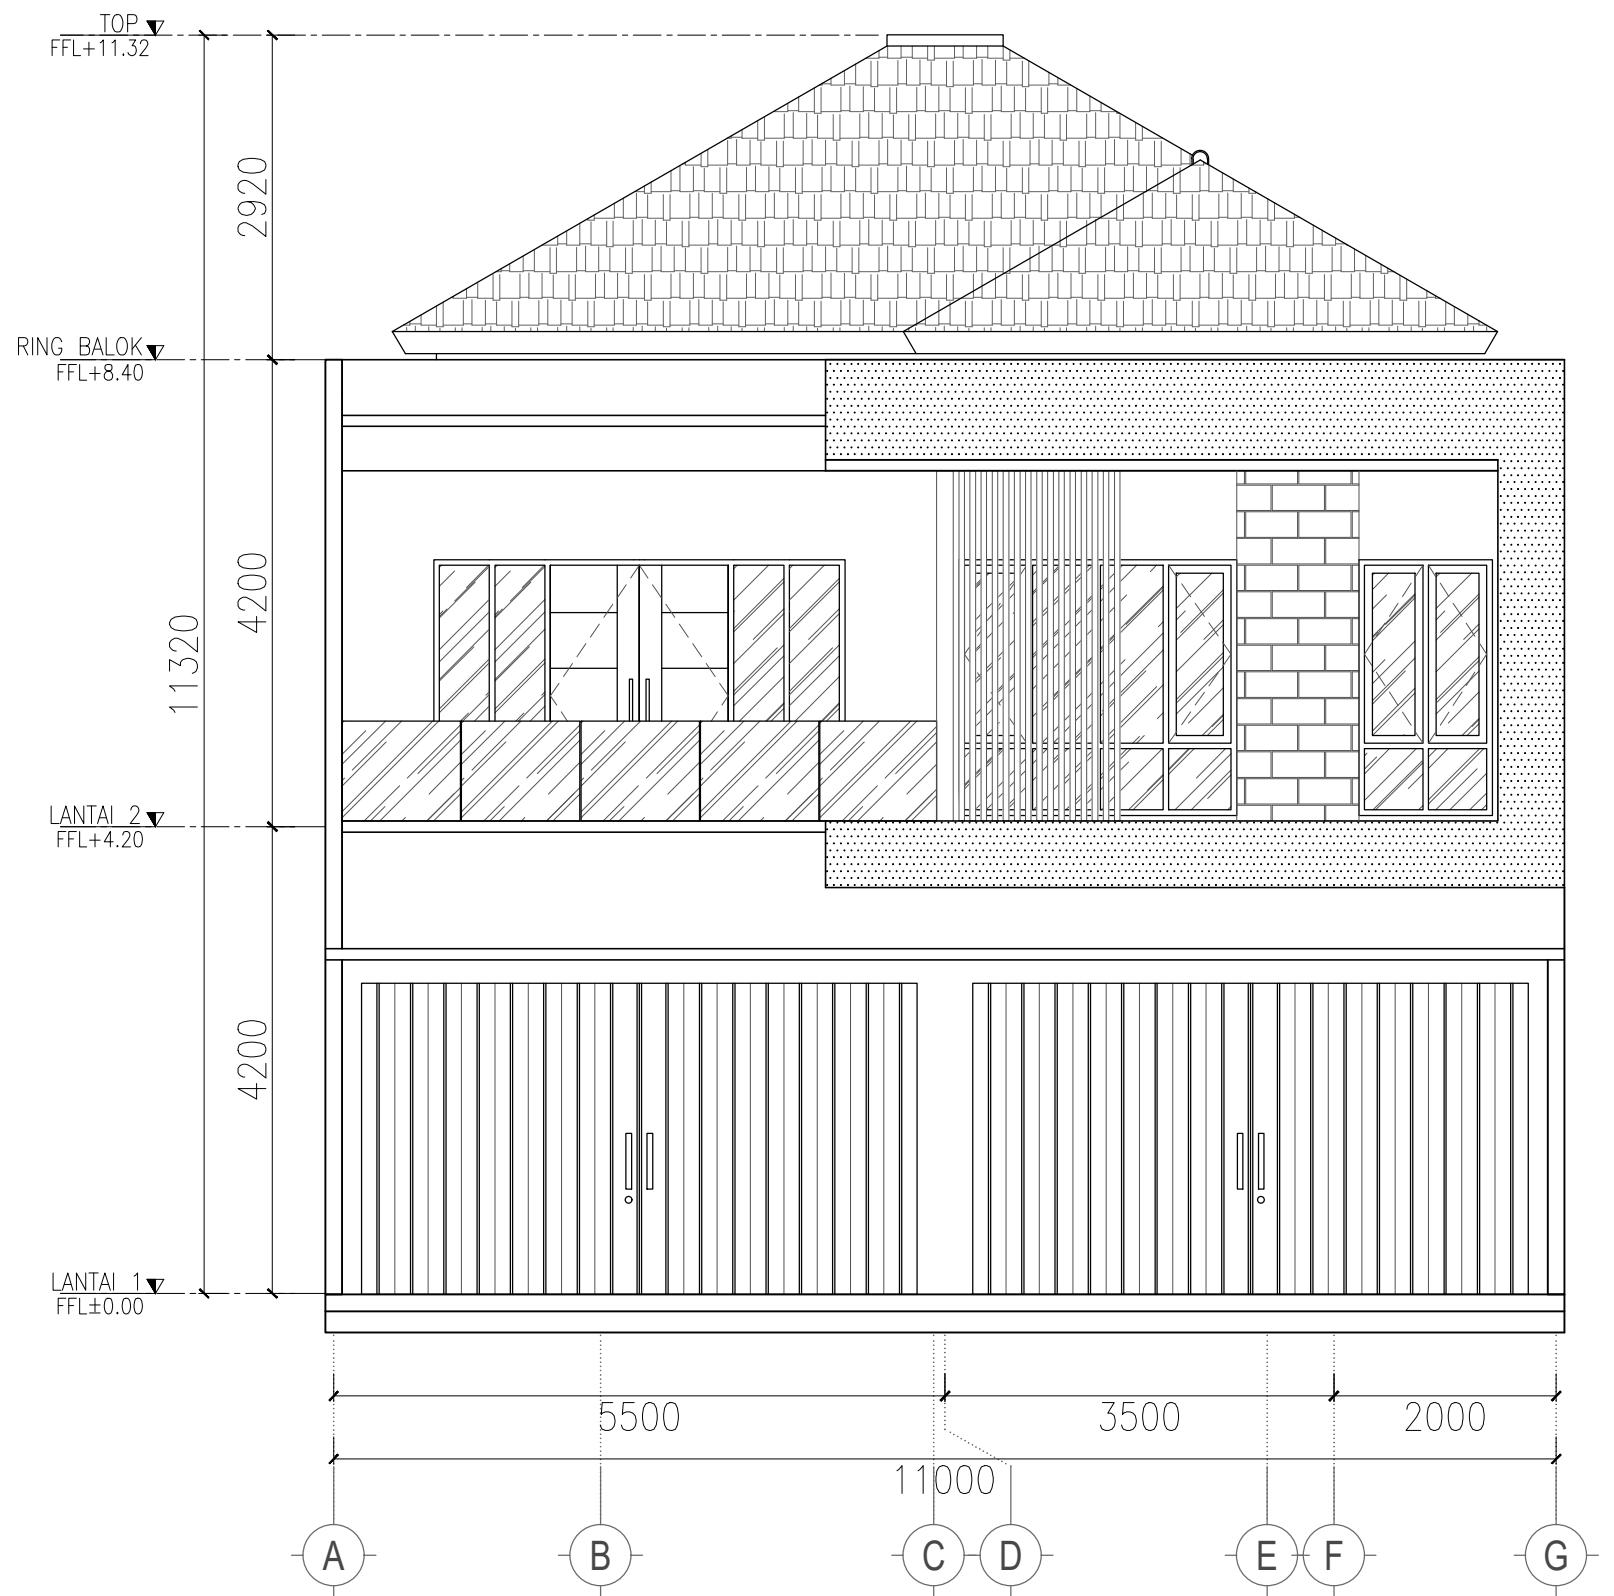


**TAMPAK DEPAN**  
SKALA 1 : 100

NAMA PROYEK	
<b>RUMAH TINGGAL 2 LANTAI</b>	
LOKASI PROYEK	
-	-
PENANGGUNG JAWAB	
DIGAMBAR	PELAKSANA
DISETUJUI	PEMILIK
CATATAN	
1. PELAKSANA ATAU SUBKON WAJIB MEMERIKSA KEMBALI KESESUAIN GAMBAR DENGAN KONDISI LAPANGAN	
JUDUL GAMBAR	SKALA
1. ARS	1 : 100
TANGGAL :	REVISI :
5 AGUSTUS 2024	<b>R1</b>
KODE GAMBAR	
ARS-01-01	
NO. LBR	JUMLAH LBR
00	00

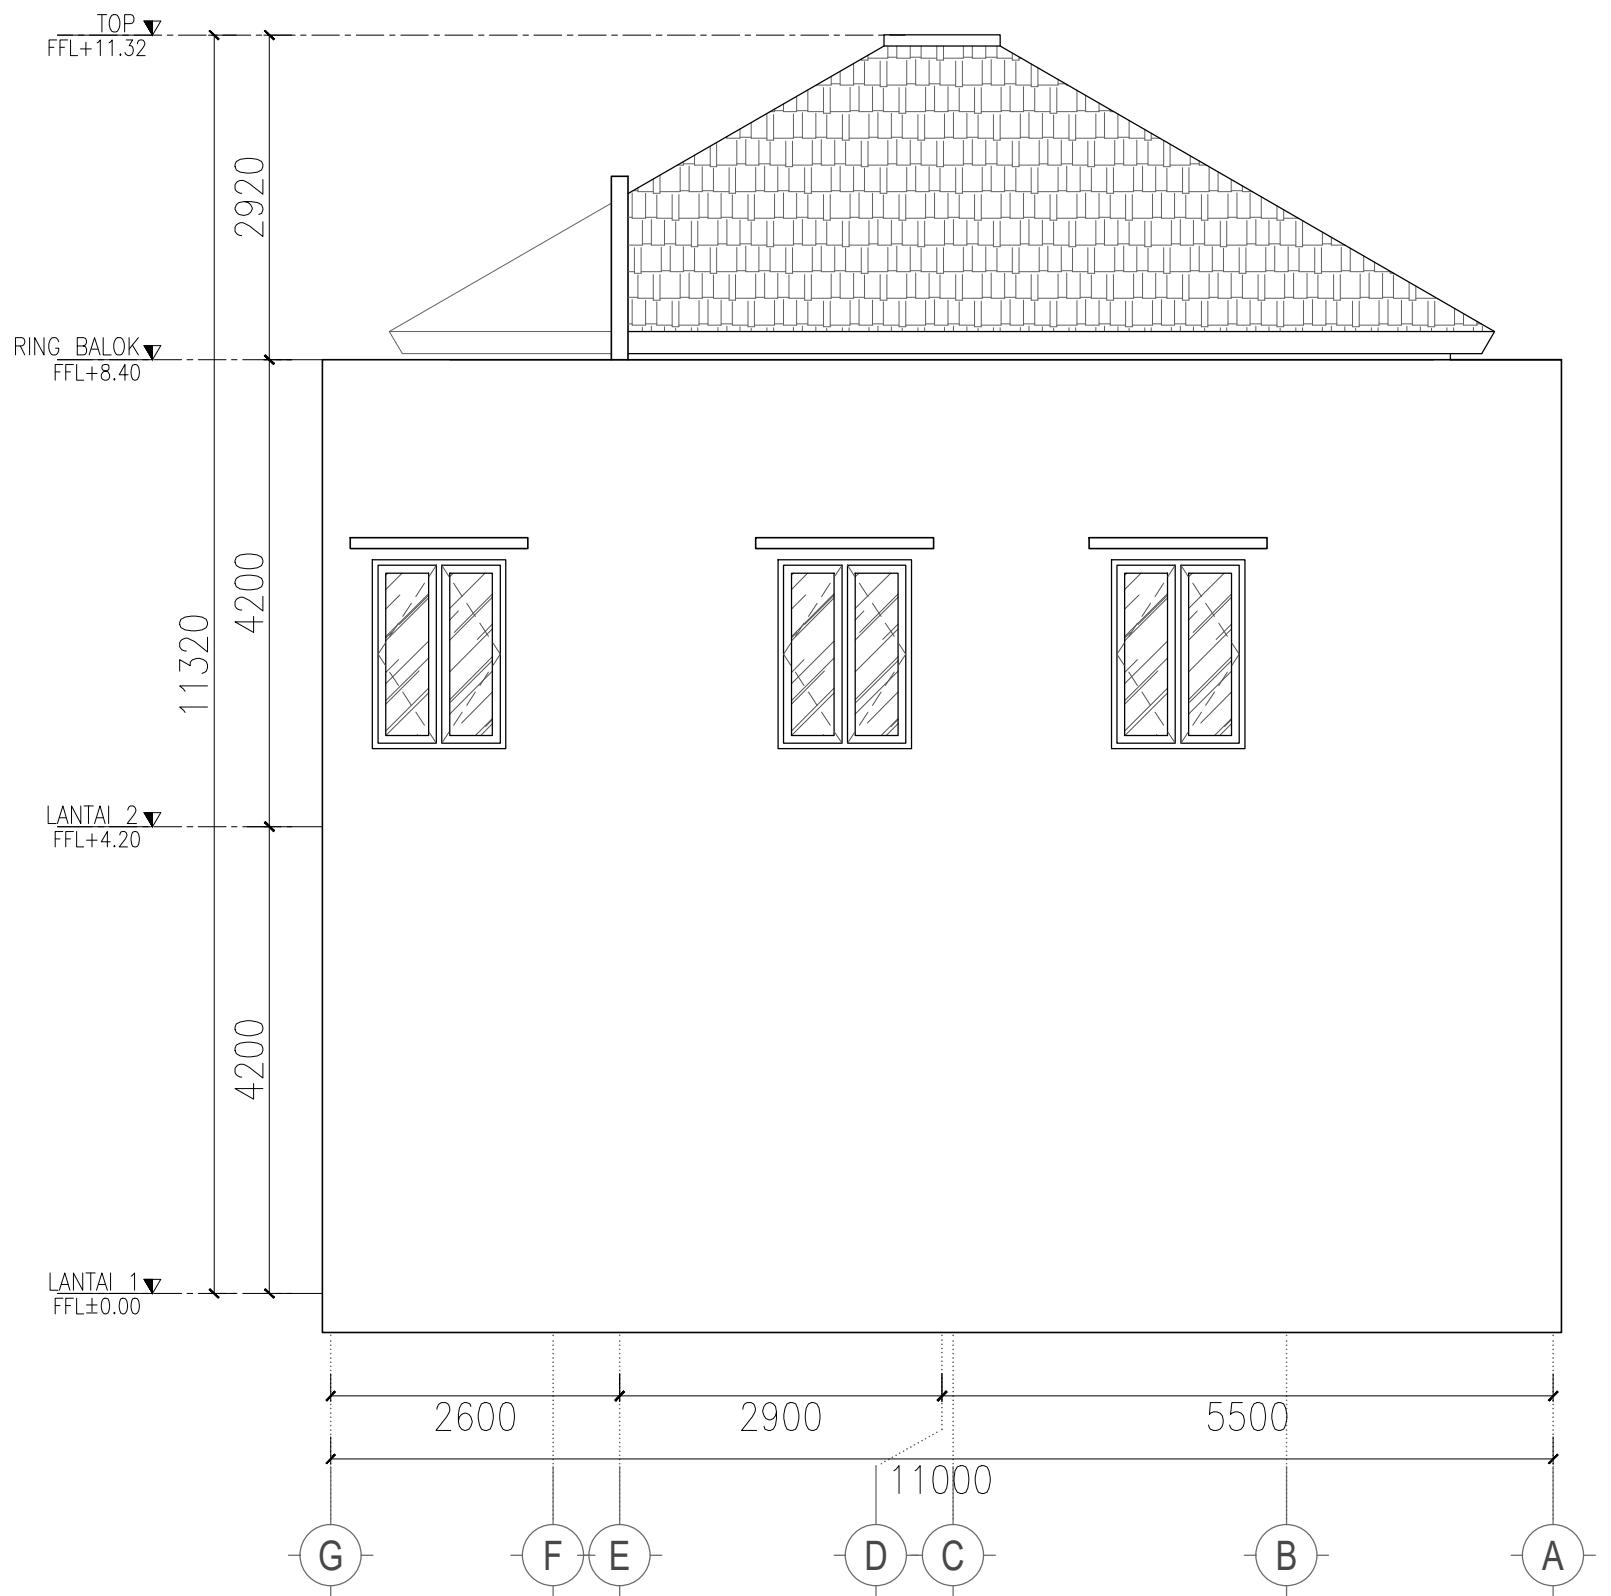


**TAMPAK BELAKANG**  
SKALA 1 : 100


NAMA PROYEK	
<b>RUMAH TINGGAL 2 LANTAI</b>	
LOKASI PROYEK	
-	-
PENANGGUNG JAWAB	
DIGAMBAR	PELAKSANA
DISETUJUI	PEMILIK
CATATAN	
1. PELAKSANA ATAU SUBKON WAJIB MEMERIKSA KEMBALI KESESUAIN GAMBAR DENGAN KONDISI LAPANGAN	
JUDUL GAMBAR	SKALA
1. ARS	1 : 100
TANGGAL :	REVISI :
5 AGUSTUS 2024	<b>R1</b>
KODE GAMBAR	
ARS-01-01	
NO. LBR	JUMLAH LBR
00	00

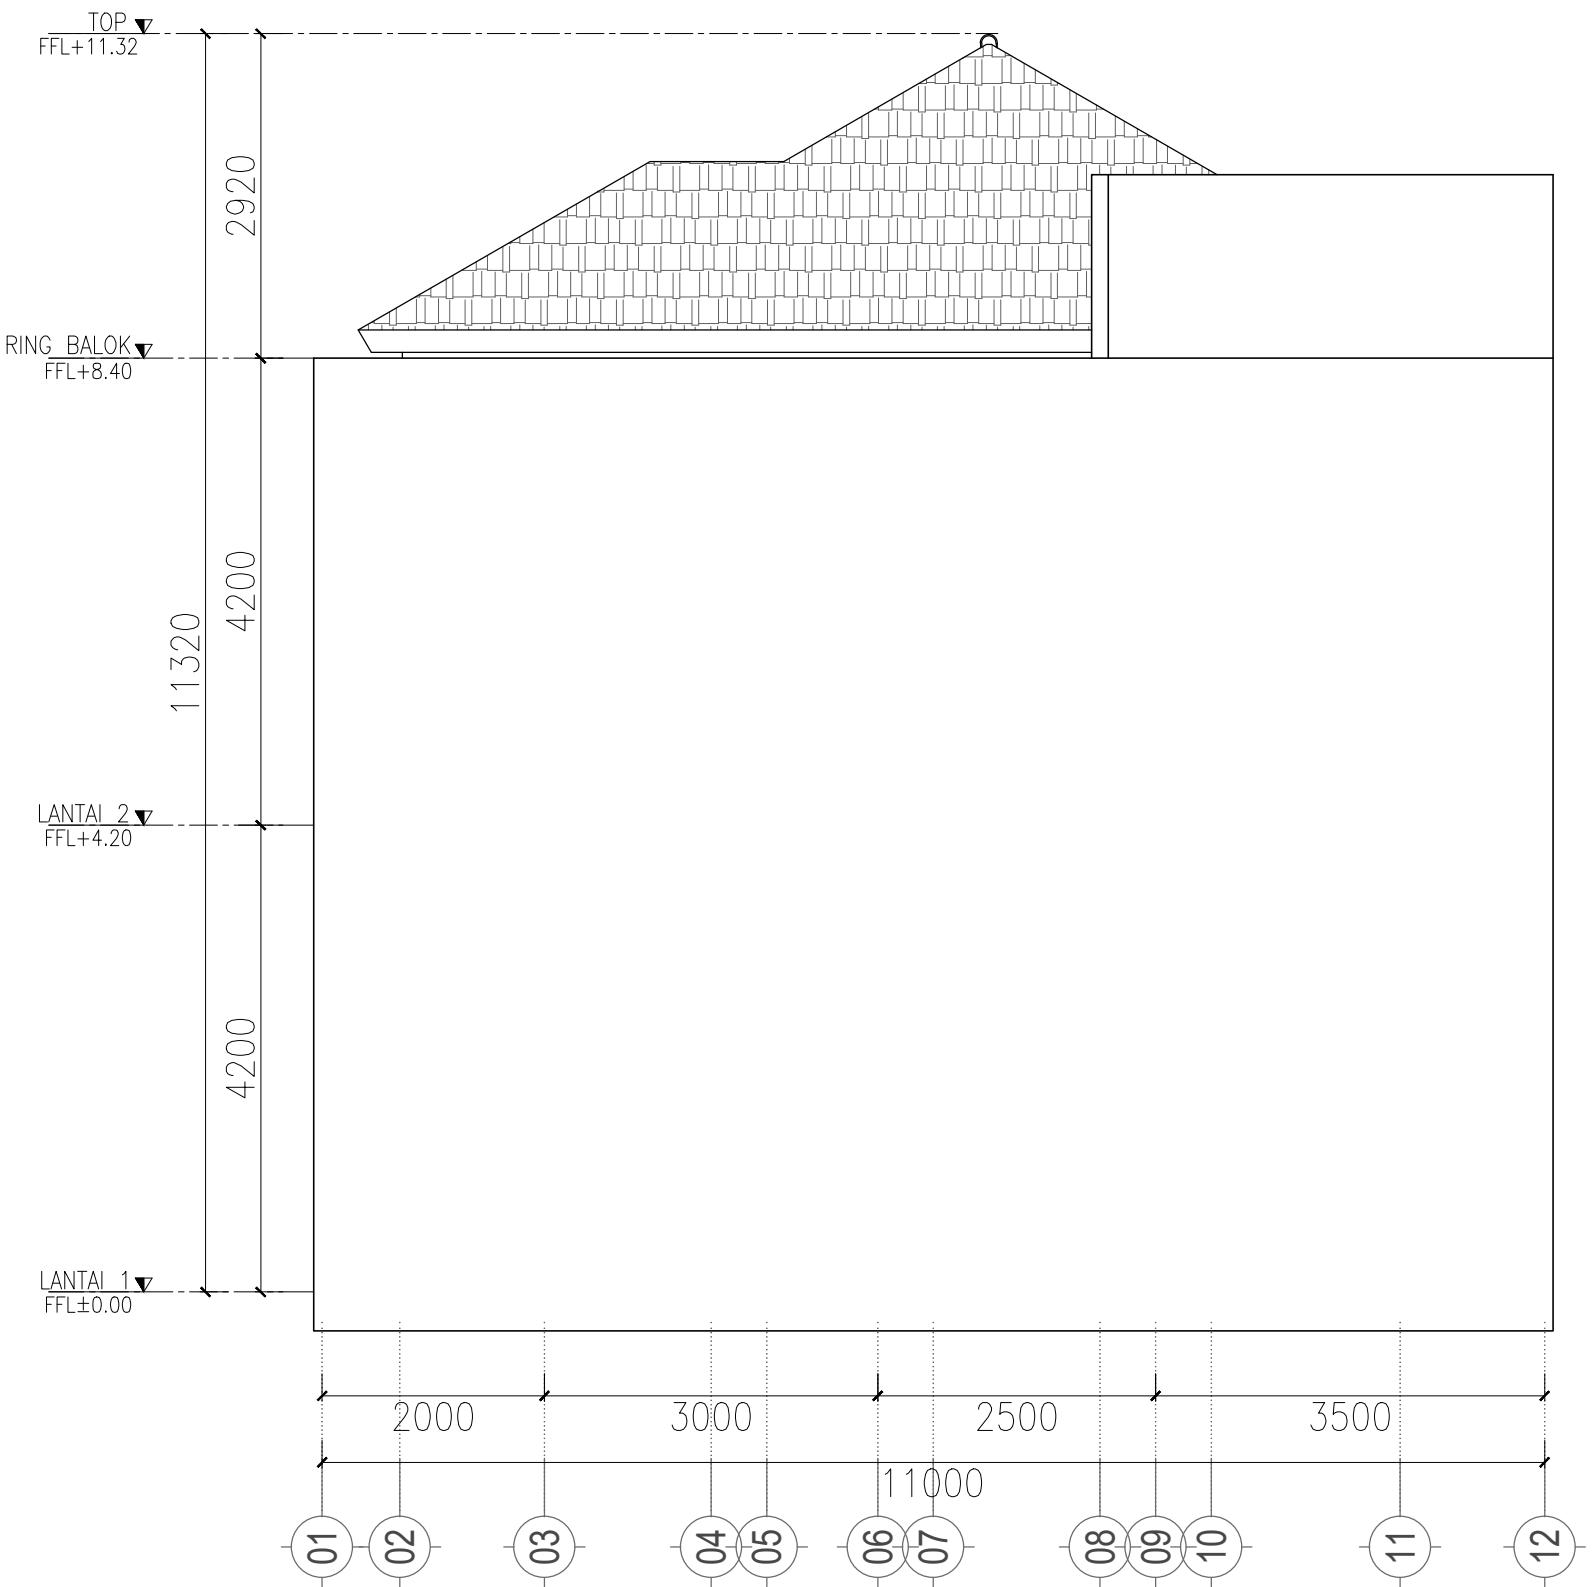


**TAMPAK SAMPING KANAN**  
SKALA 1 : 100

NAMA PROYEK	
<b>RUMAH TINGGAL 2 LANTAI</b>	
LOKASI PROYEK	
-	-
PENANGGUNG JAWAB	
DIGAMBAR	PELAKSANA
DISETUJUI	PEMILIK
CATATAN	
1. PELAKSANA ATAU SUBKON WAJIB MEMERIKSA KEMBALI KESESUAIN GAMBAR DENGAN KONDISI LAPANGAN	
JUDUL GAMBAR	SKALA
1. ARS	1 : 100
TANGGAL :	REVISI :
5 AGUSTUS 2024	<b>R1</b>
KODE GAMBAR	
ARS-01-01	
NO. LBR	JUMLAH LBR
00	00

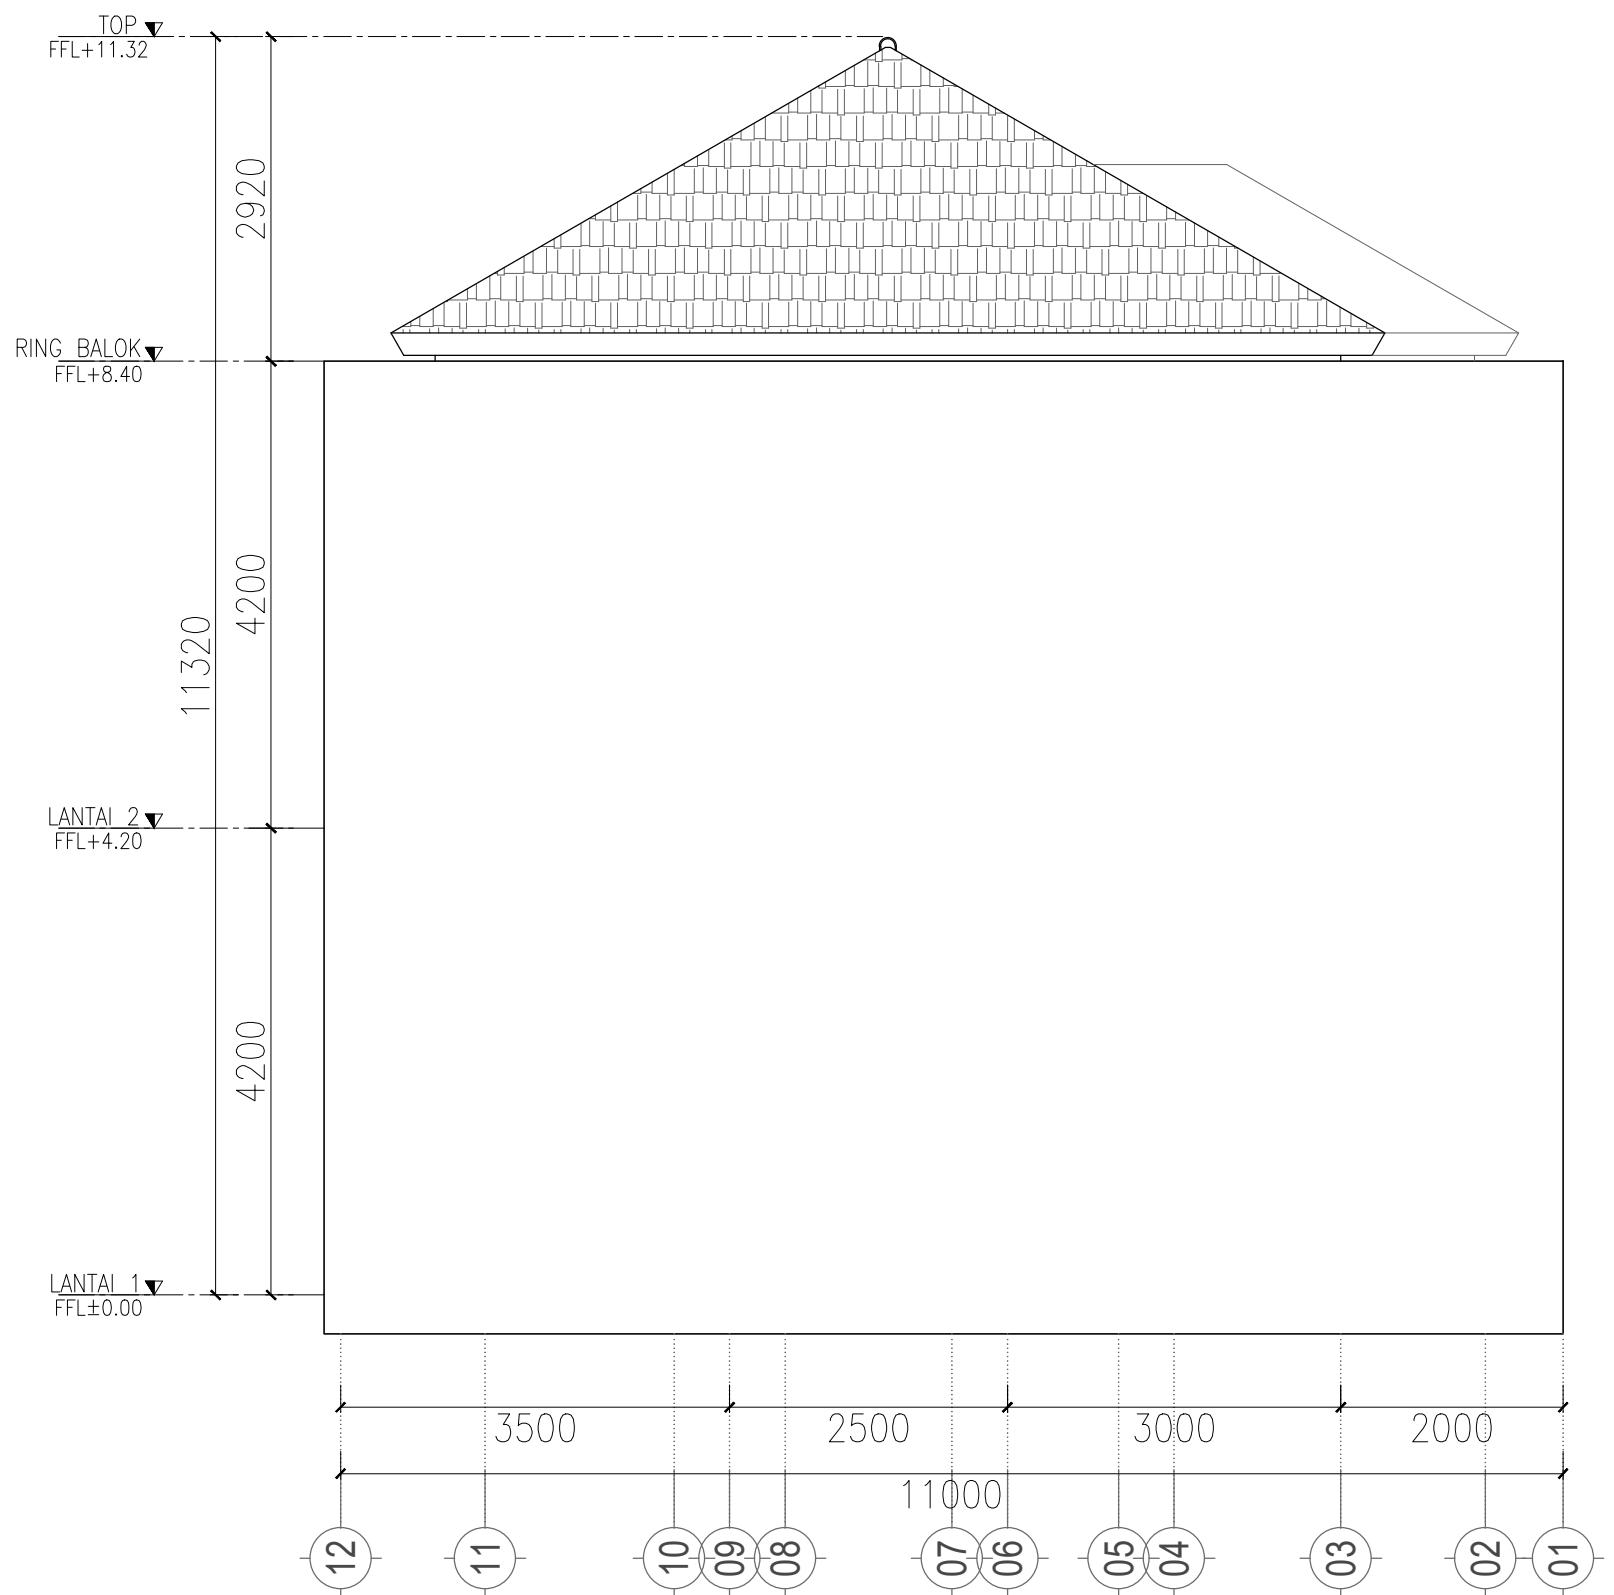


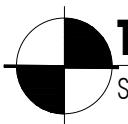 **TAMPAK SAMPING KIRI**  
SKALA 1 : 100



NAMA PROYEK	
<b>RUMAH TINGGAL 2 LANTAI</b>	
LOKASI PROYEK	
-	-
PENANGGUNG JAWAB	
DIGAMBAR	PELAKSANA
DISETUJUI	PEMILIK
CATATAN	
1. PELAKSANA ATAU SUBKON WAJIB MEMERIKSA KEMBALI KESESUAIN GAMBAR DENGAN KONDISI LAPANGAN	
JUDUL GAMBAR	
1. ARS	SKALA
	1 : 100
TANGGAL :	REVISI :
5 AGUSTUS 2024	<b>R1</b>
KODE GAMBAR	
ARS-01-01	
NO. LBR	JUMLAH LBR
00	00

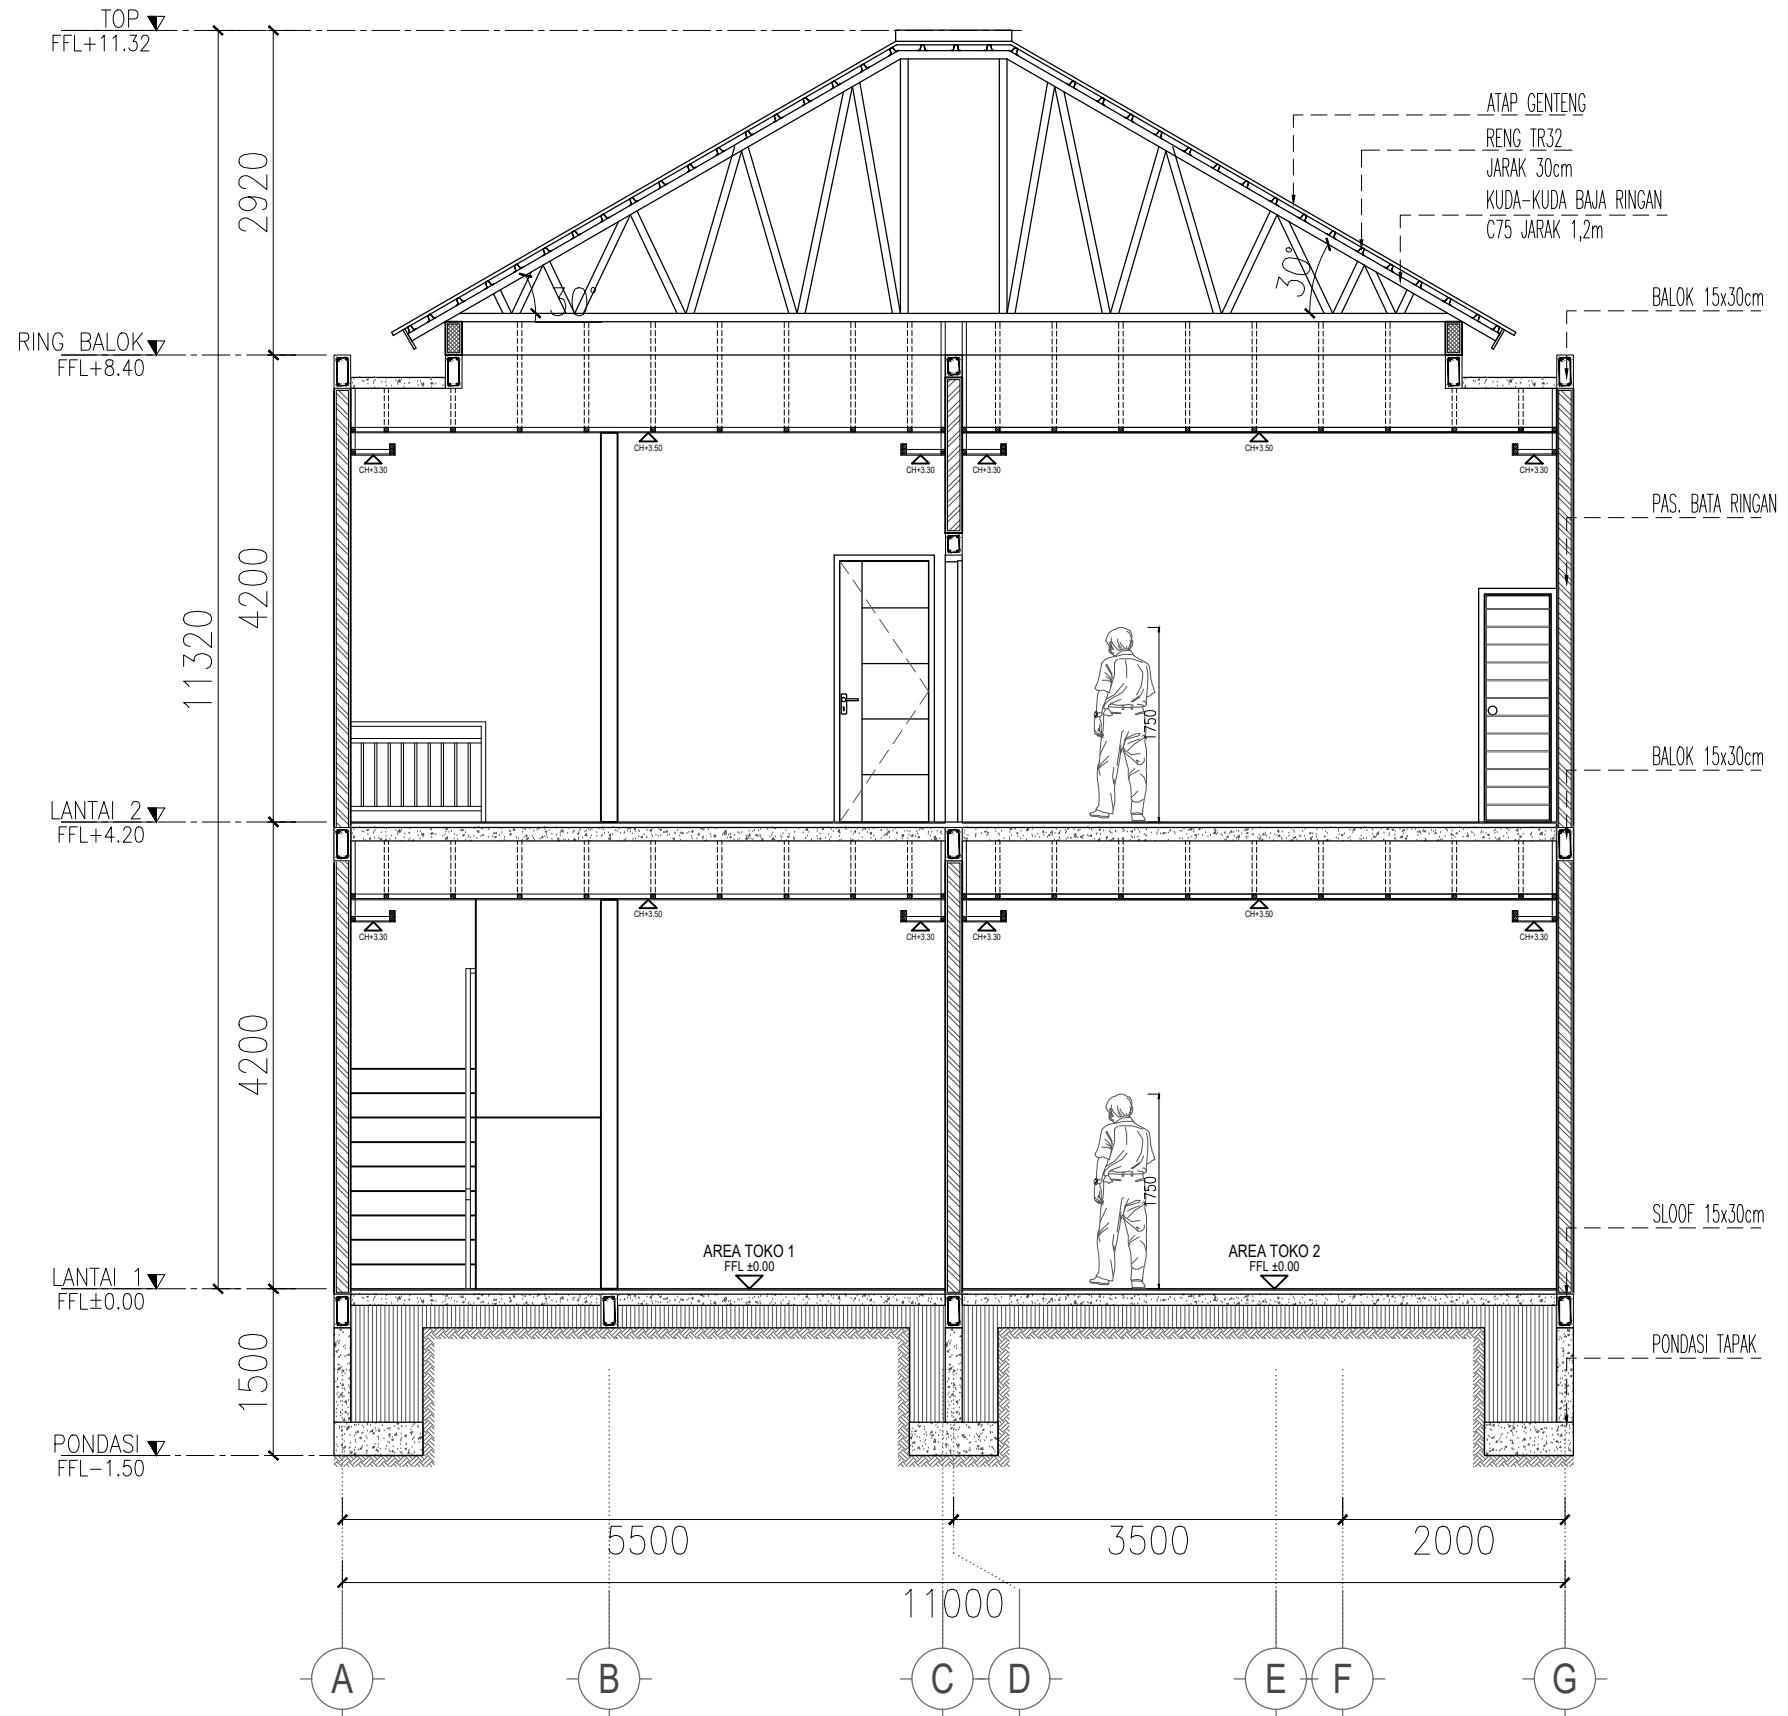

NAMA PROYEK	
<b>RUMAH TINGGAL 2 LANTAI</b>	
LOKASI PROYEK	
-	-
PENANGGUNG JAWAB	
DIGAMBAR	PELAKSANA
DISETUJUI	PEMILIK
CATATAN	
1. PELAKSANA ATAU SUBKON WAJIB MEMERIKSA KEMBALI KESESUAIN GAMBAR DENGAN KONDISI LAPANGAN	
JUDUL GAMBAR	
1. ARS	SKALA 1 : 100
TANGGAL :	REVISI :
5 AGUSTUS 2024	<b>R1</b>
KODE GAMBAR	
ARS-01-01	
NO. LBR	JUMLAH LBR
00	00

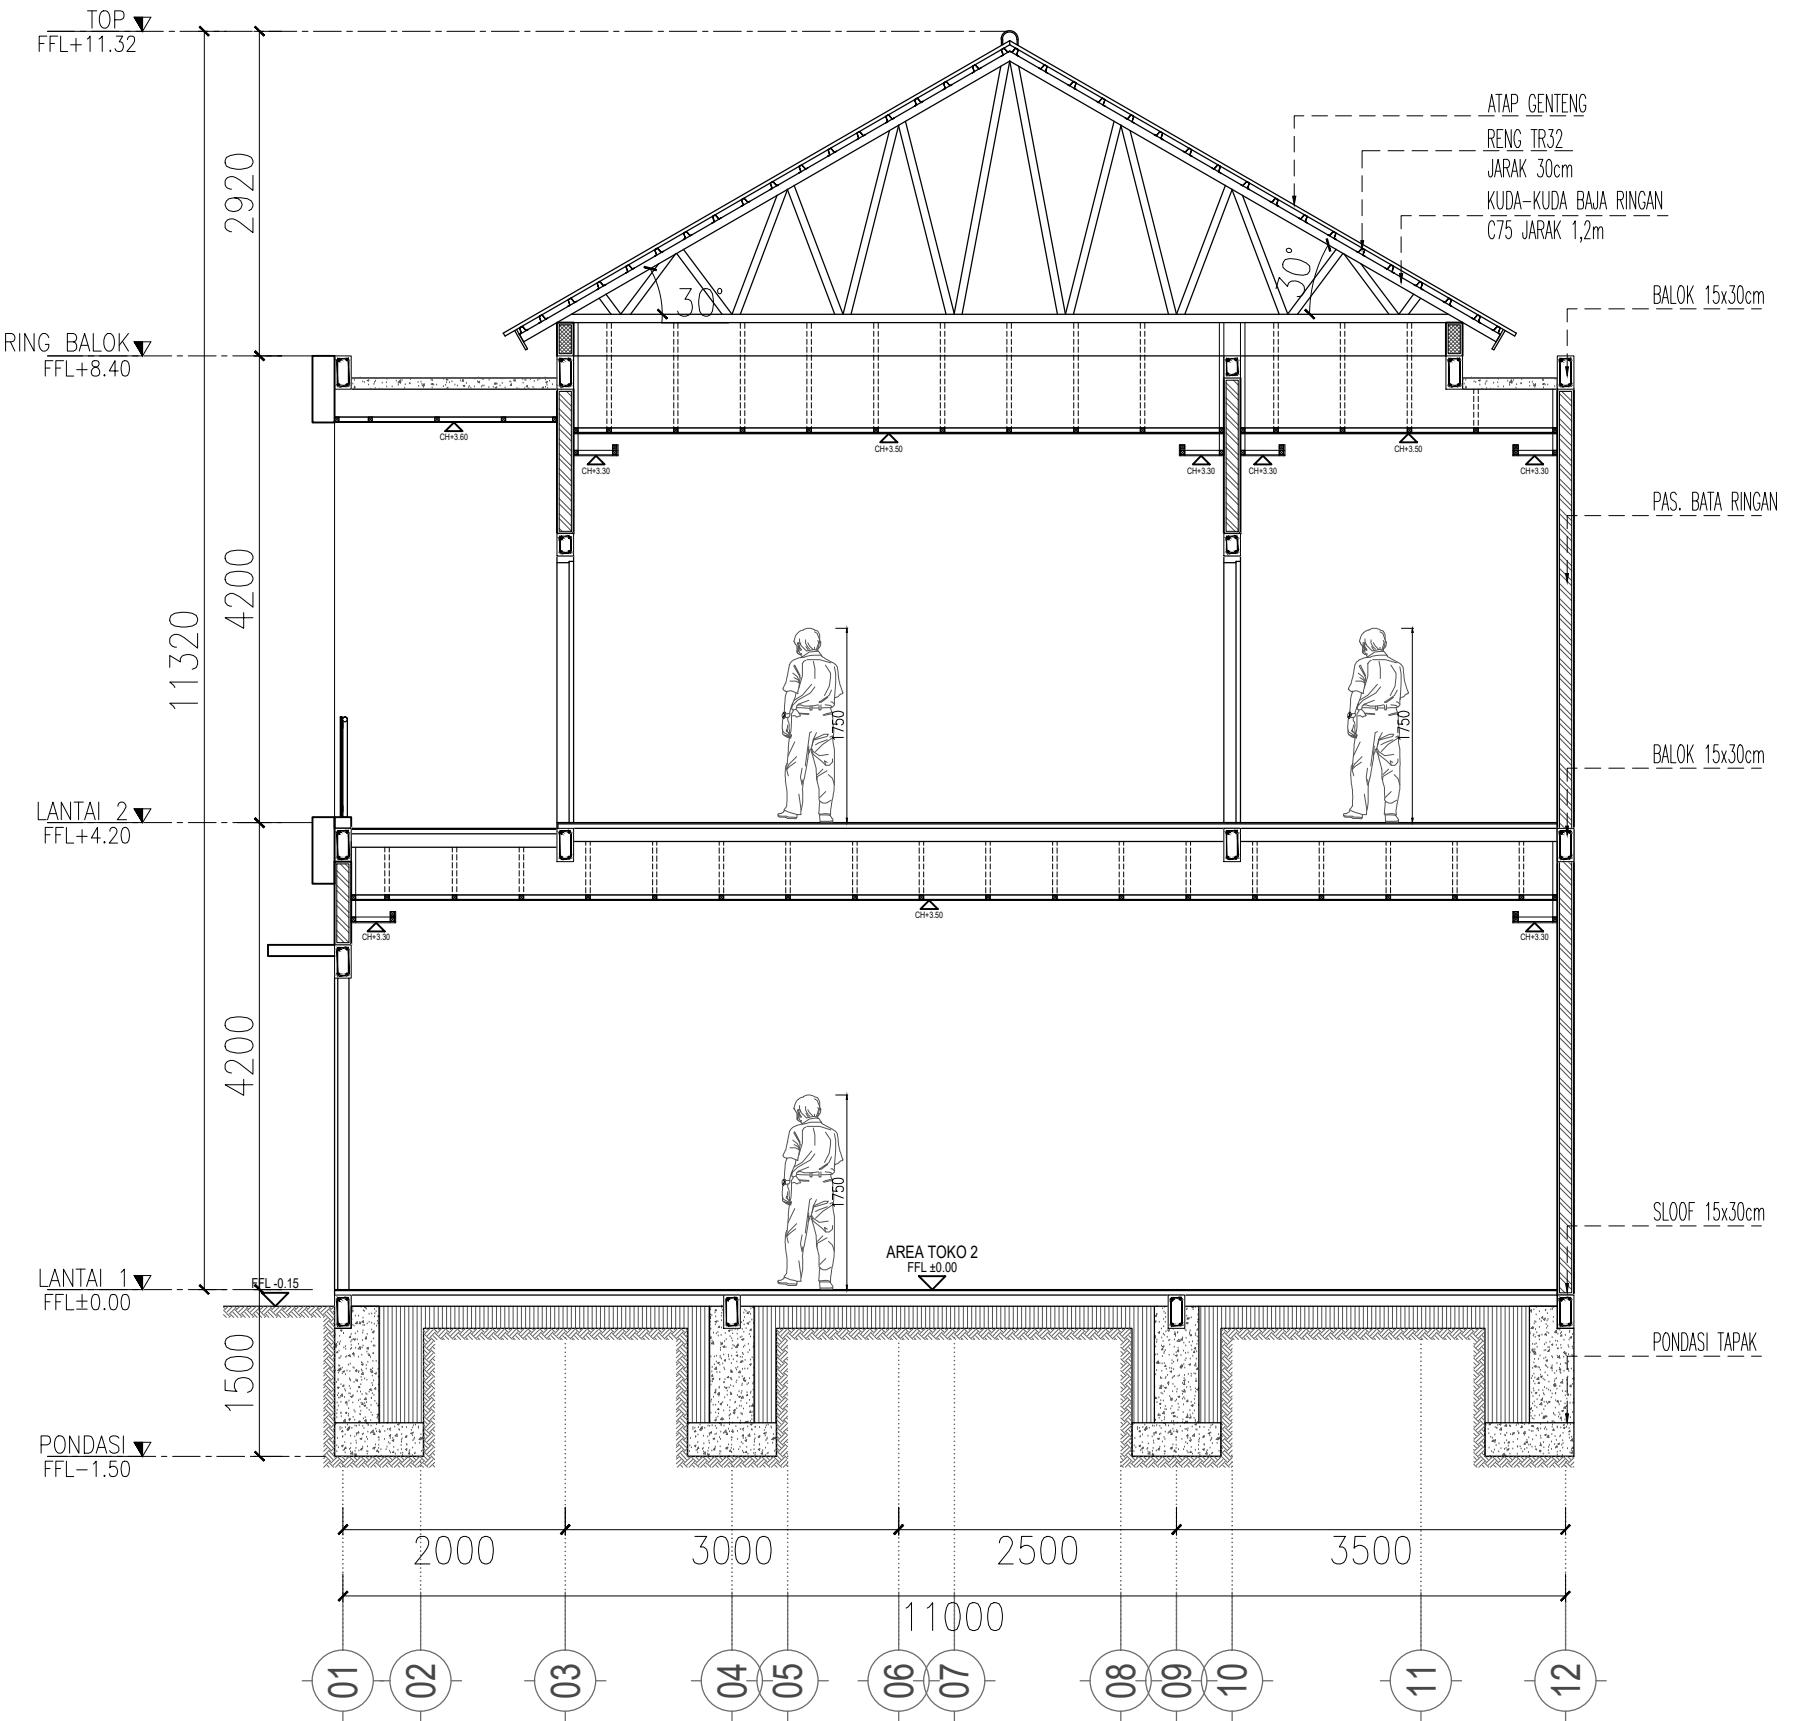

NAMA PROYEK	
<b>RUMAH TINGGAL 2 LANTAI</b>	
LOKASI PROYEK	
-	-
PENANGGUNG JAWAB	
DIGAMBAR	PELAKSANA
DISETUJUI	PEMILIK
CATATAN	
1. PELAKSANA ATAU SUBKON WAJIB MEMERIKSA KEMBALI KESESUAIN GAMBAR DENGAN KONDISI LAPANGAN	
JUDUL GAMBAR	SKALA
1. ARS	1 : 100
TANGGAL :	REVISI :
5 AGUSTUS 2024	<b>R1</b>
KODE GAMBAR	
ARS-01-01	
NO. LBR	JUMLAH LBR
00	00

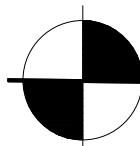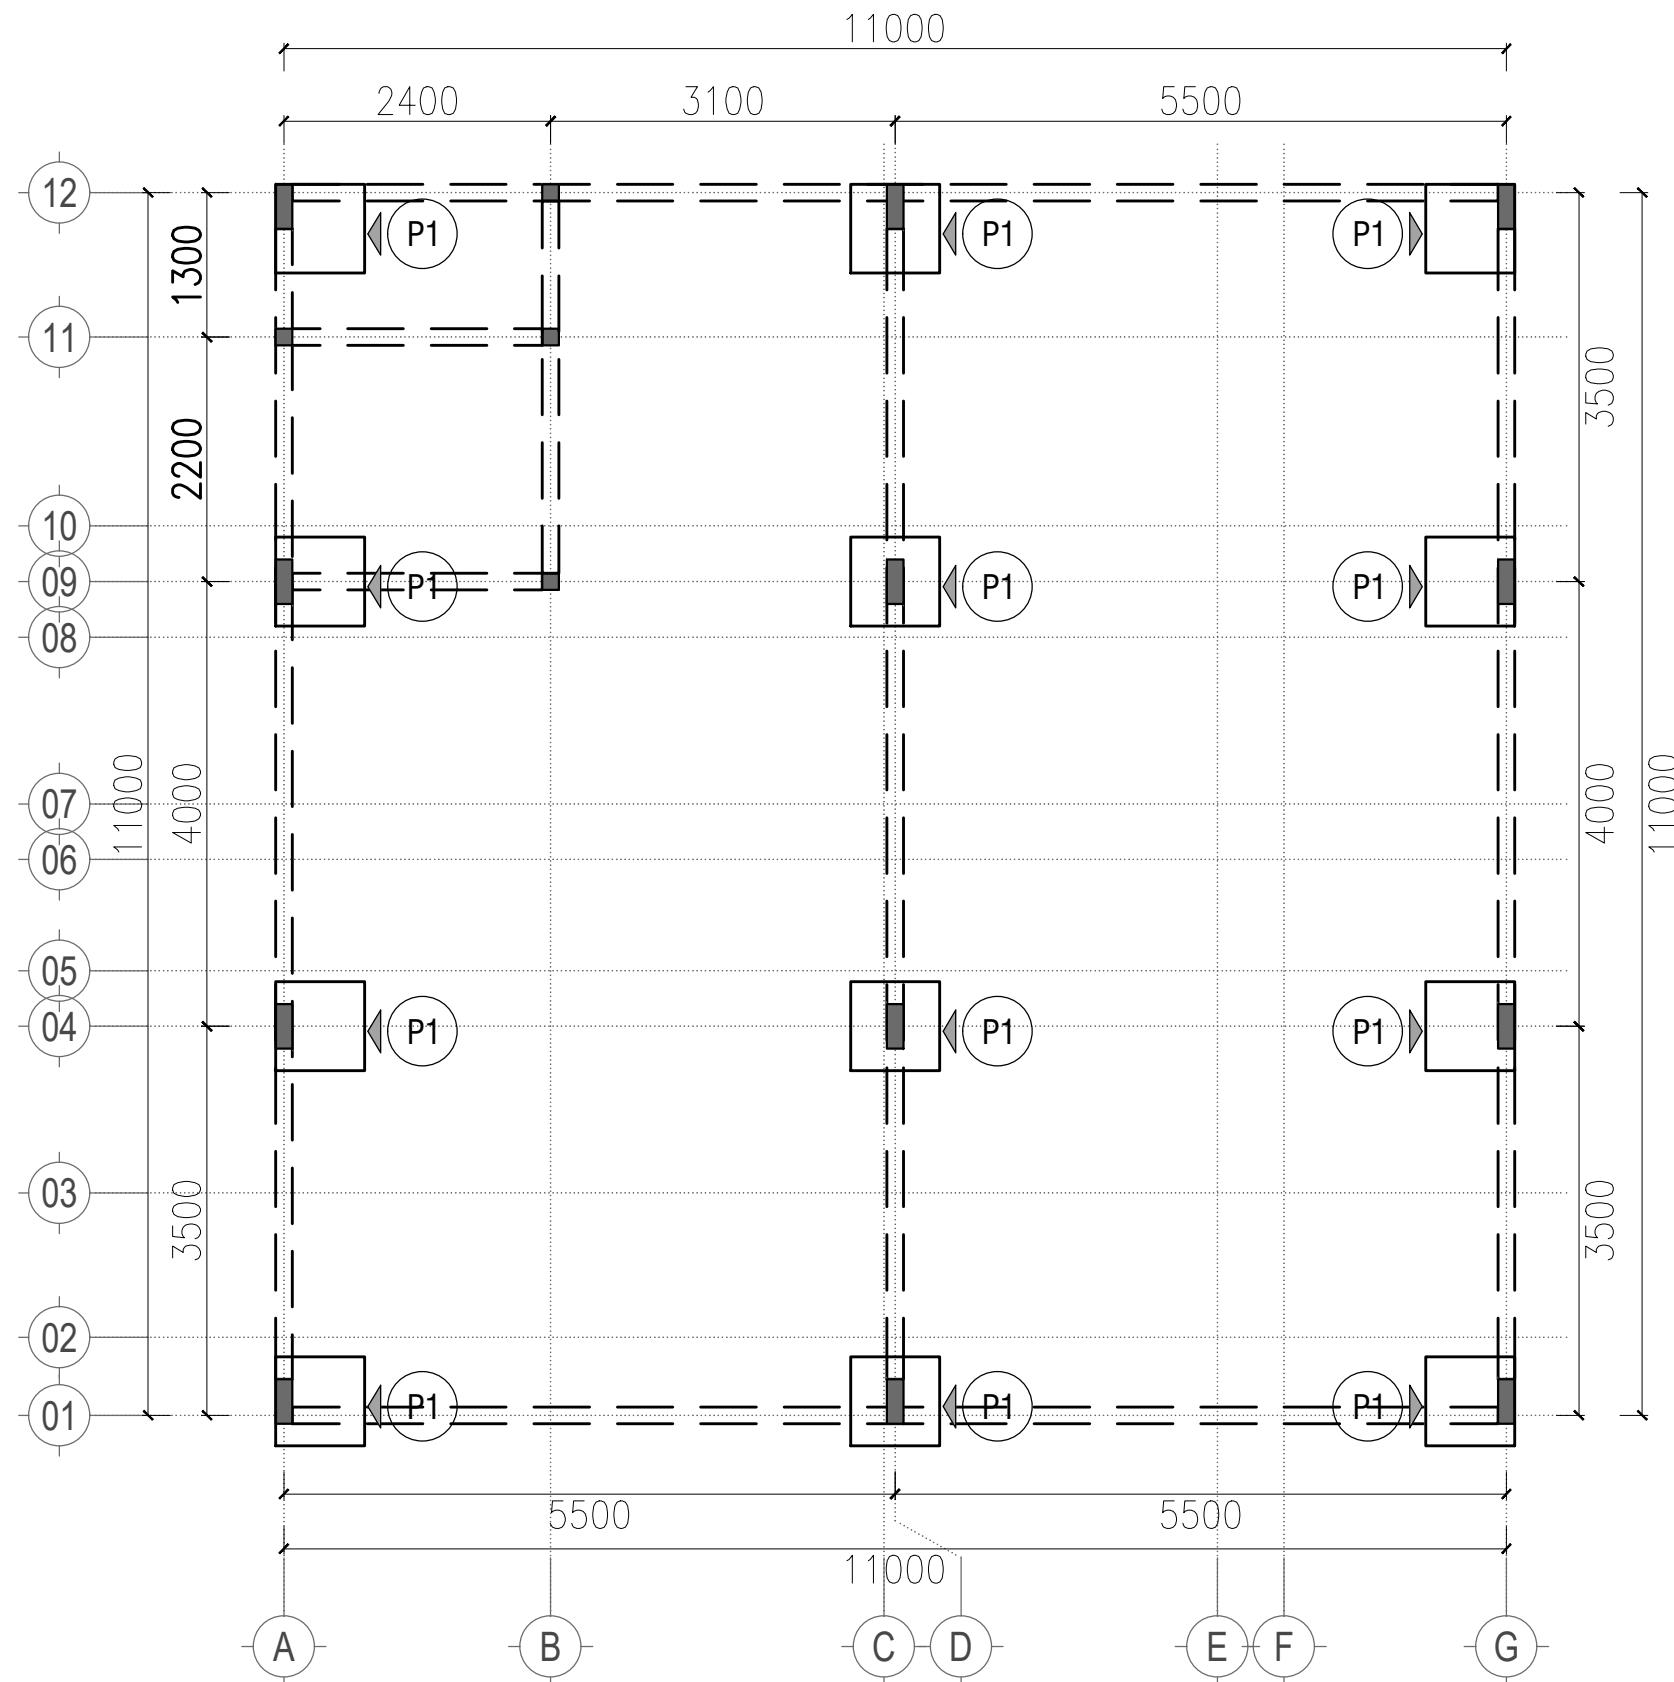


## DENAH PONDASI TAPAK SFL-1.50 (ELEVASI BOTTOM)

SKALA 1 : 100

NOTASI	KETERANGAN JENIS PONDASI	JUMLAH
(P1)	PONDASI TAPAK UK.800x800x300 DALAM 1,5 METER	12


NAMA PROYEK	
<b>RUMAH TINGGAL 2 LANTAI</b>	
LOKASI PROYEK	
-	-
PENANGGUNG JAWAB	
DIGAMBAR	PELAKSANA
DISETUJUI	PEMILIK
CATATAN	
1. PELAKSANA ATAU SUBKON WAJIB MEMERIKSA KEMBALI KESESUAIN GAMBAR DENGAN KONDISI LAPANGAN	
JUDUL GAMBAR	SKALA
1.DETAIL PONDASI PC1	1 : 25
TANGGAL :	REVISI :
5 AGUSTUS 2024	R1
KODE GAMBAR	
STR-03-12	
NO. LBR	JUMLAH LBR
12	00

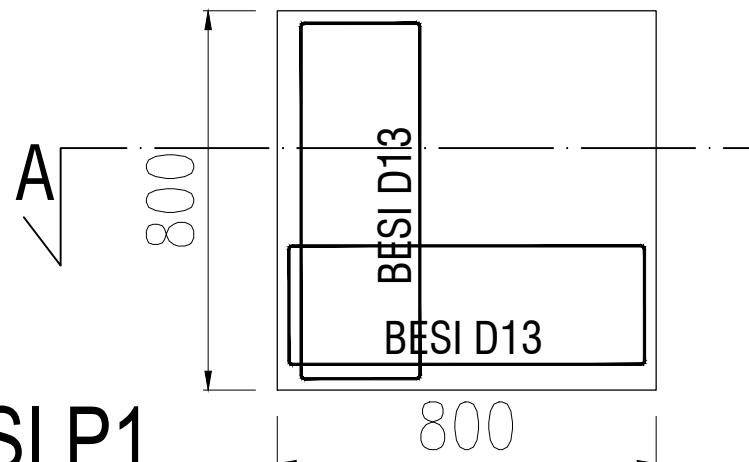


## DENAH PONDASI P1 POSISI TENGAH

01  
AR-00-00

SKALA 1 : 25

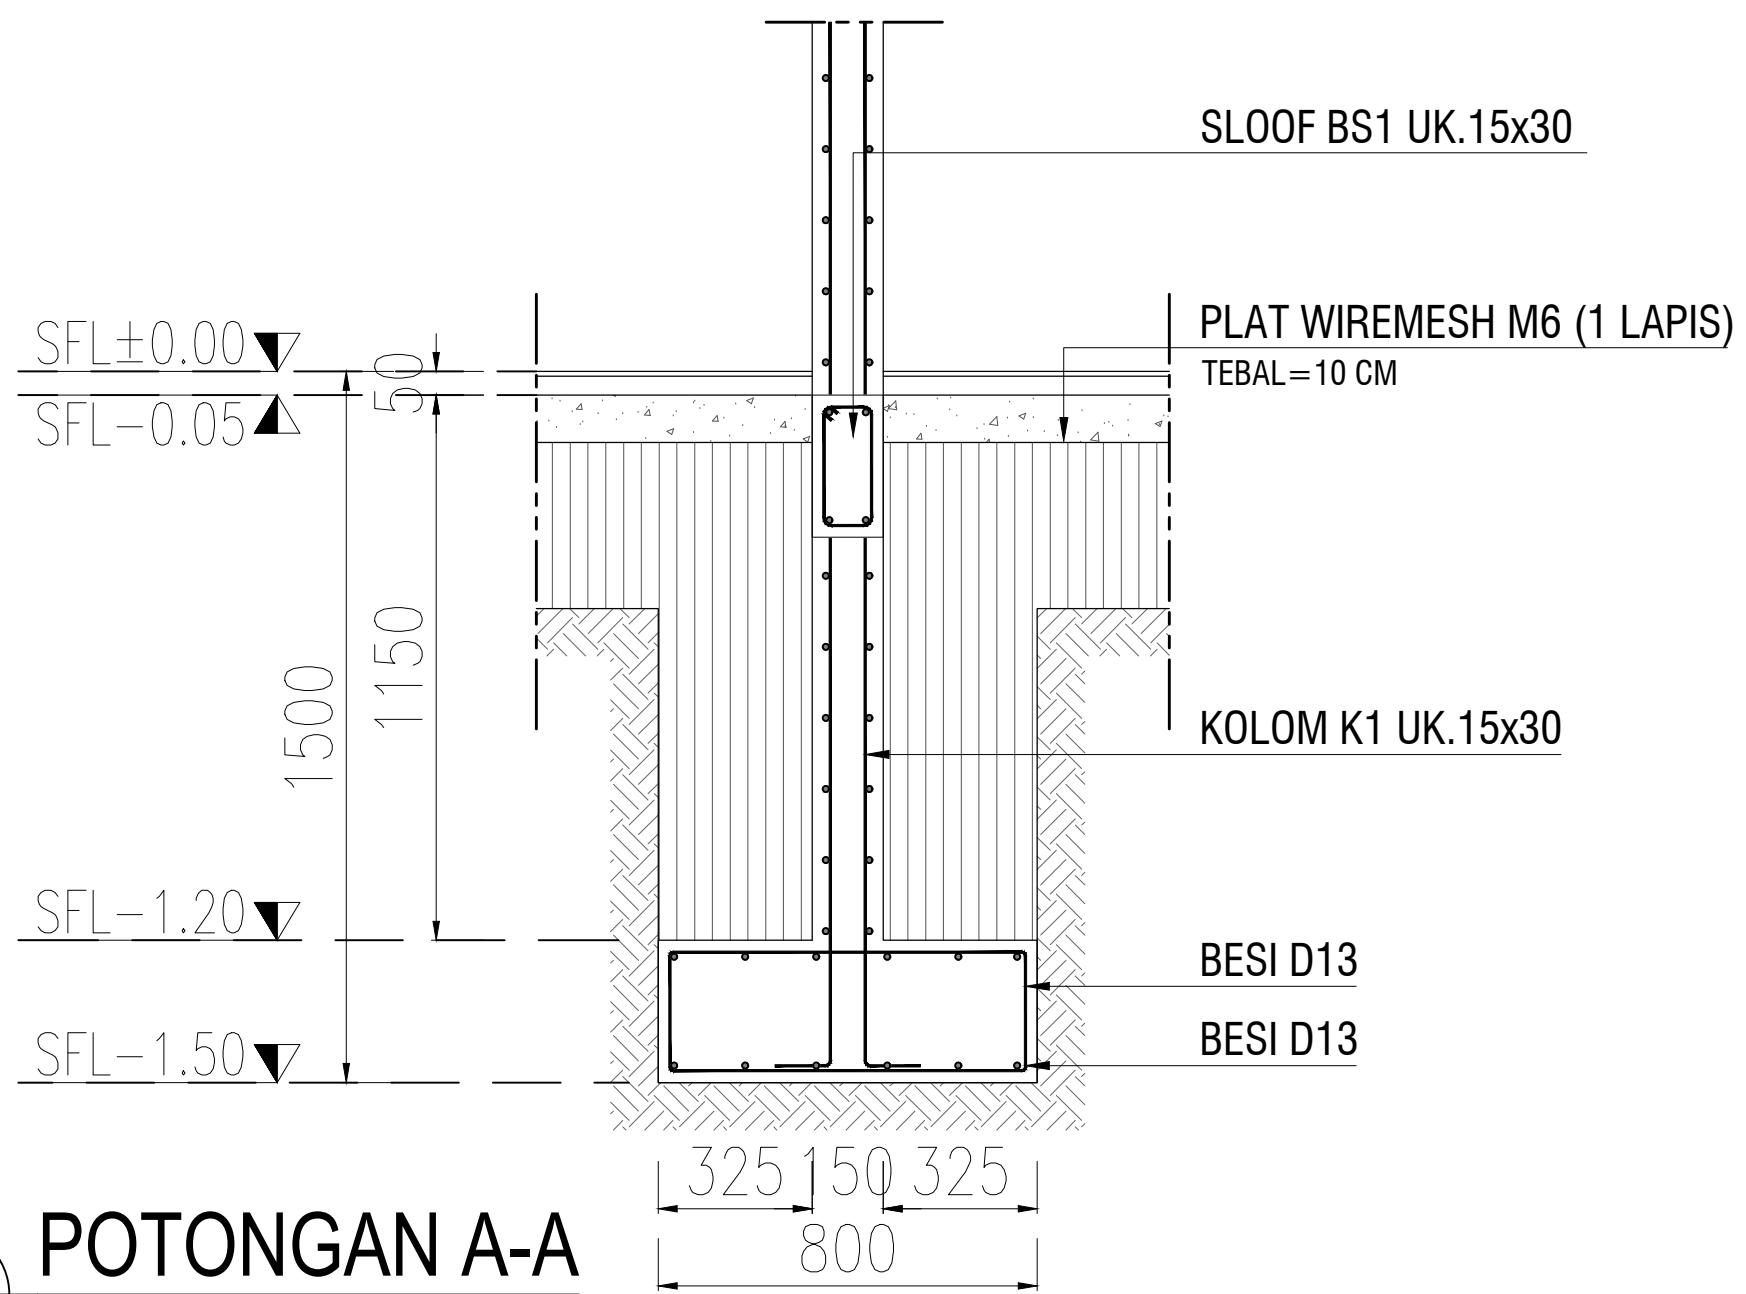


NAMA PROYEK	RUMAH TINGGAL 2 LANTAI	
LOKASI PROYEK	-	
PENANGGUNG JAWAB	-	
DIGAMBAR	PELAKSANA	
DISETUJUI	PEMILIK	
CATATAN	<p>1. PELAKSANA ATAU SUBKON WAJIB MEMERIKSA KEMBALI KESESUAIN GAMBAR DENGAN KONDISI LAPANGAN</p>	
JUDUL GAMBAR	SKALA	
1. ARS	1 : 100	
TANGGAL :	REVISI :	
5 AGUSTUS 2024	R1	
KODE GAMBAR	ARS-01-01	
NO. LBR	JUMLAH LBR	
00	00	

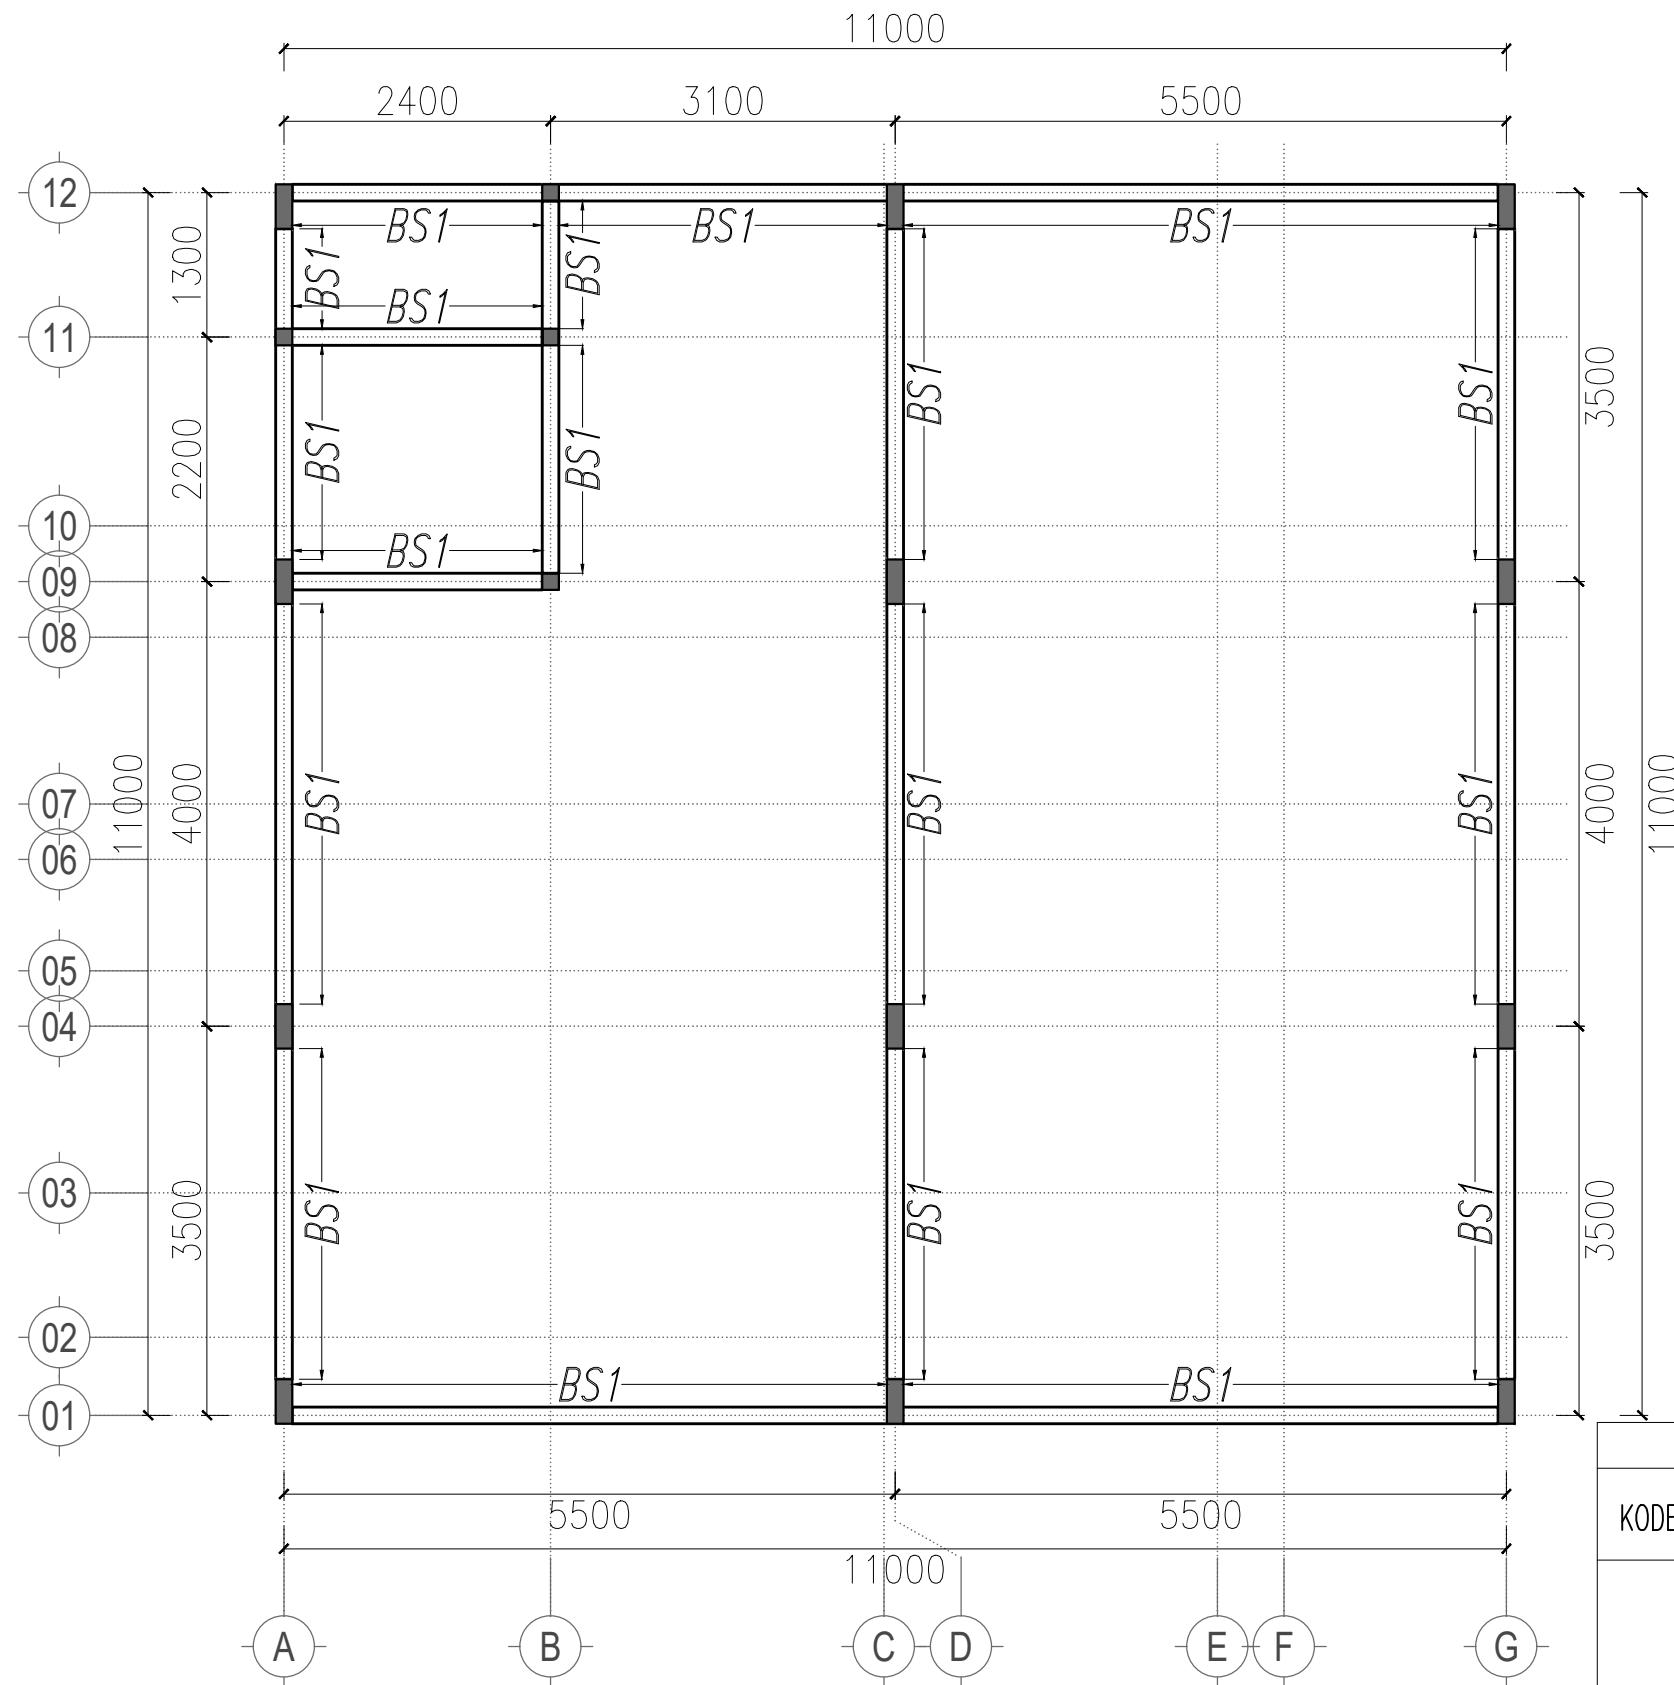


DETAIL PENULANGAN SLOOF		
KODE SLOOF	BS1	
	TUMPUAN	LAPANGAN
DIMENSI	150x300	150x300
TULANGAN ATAS	2D13	2D13
TULANGAN TENGAH	-	-
TULANGAN BAWAH	2D13	2D13
SENGKANG	Ø8-150	Ø8-150

NAMA PROYEK	RUMAH TINGGAL 2 LANTAI
LOKASI PROYEK	-
PENANGGUNG JAWAB	-
DIGAMBAR	PELAKSANA
DISETUJUI	PEMILIK
CATATAN	<p>1. PELAKSANA ATAU SUBKON WAJIB MEMERIKSA KEMBALI KESESUAIN GAMBAR DENGAN KONDISI LAPANGAN</p>
JUDUL GAMBAR	SKALA
1. ARS	1 : 100
TANGGAL :	REVISI :
5 AGUSTUS 2024	R1
KODE GAMBAR	
ARS-01-01	
NO. LBR	JUMLAH LBR
00	00

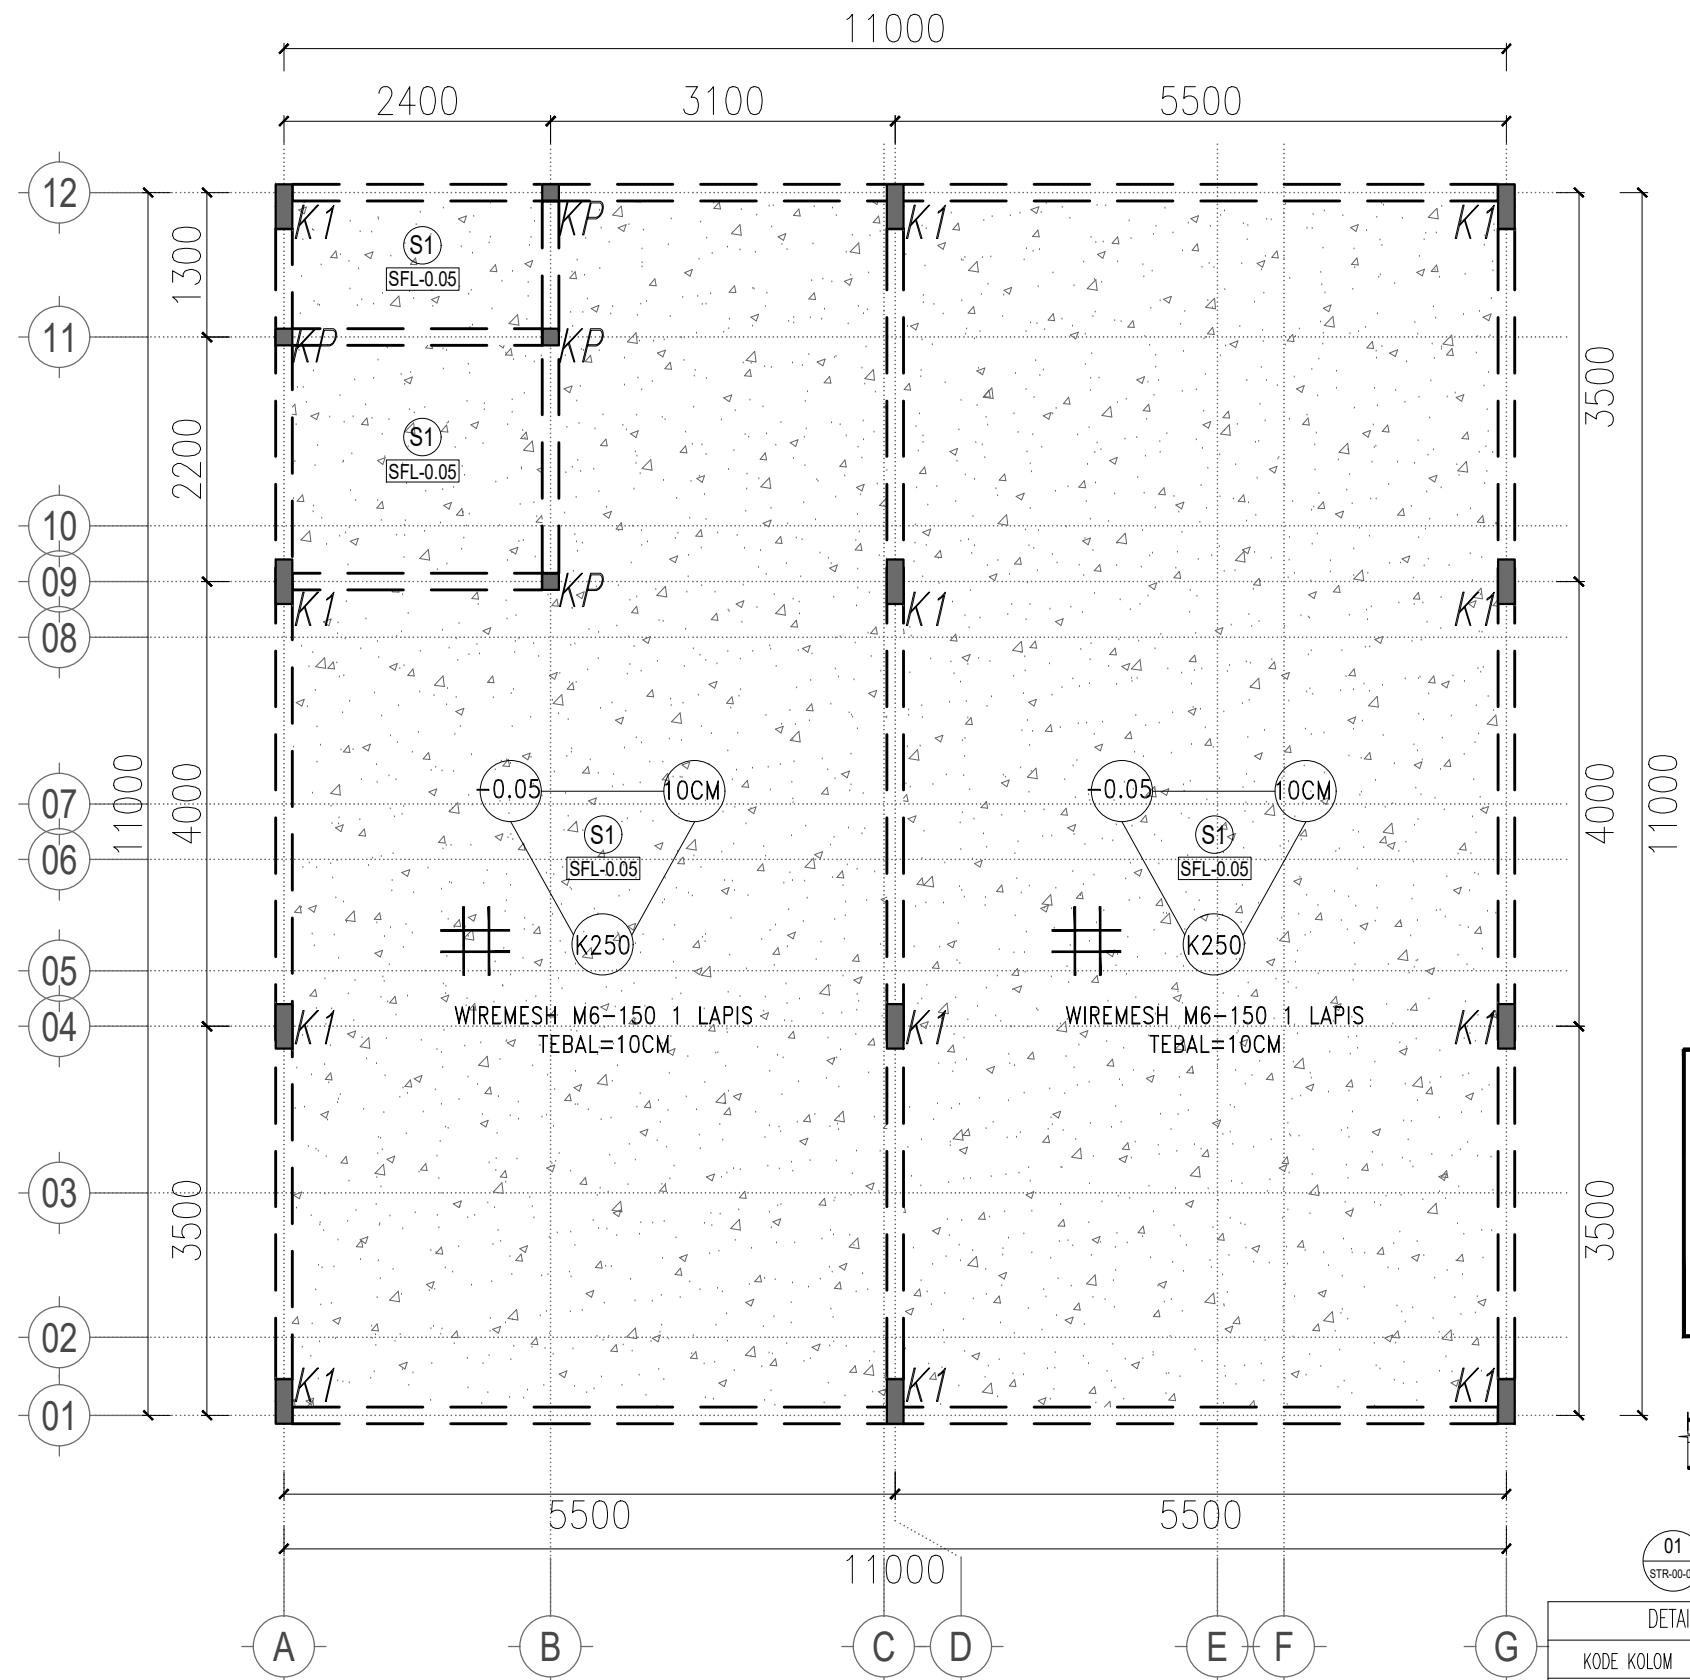


## DENAH PLAT DAN KOLOM LANTAI 1 SFL-0.05

SKALA 1 : 100

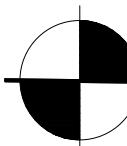

DETAIL PENULANGAN KOLOM			
KODE KOLOM	K1	K2	KP
	400x300 150x150	60x13 150x150	60x13 150x150
DIMENSI	150x400	150x300	150x150
TULANGAN UTAMA	60x13	60x13	4x10
SENGKANG	ø8-150	ø8-150	ø8-150

NAMA PROYEK	RUMAH TINGGAL 2 LANTAI	
LOKASI PROYEK	-	
PENANGGUNG JAWAB	-	
DIGAMBAR	PELAKSANA	
DISETUJUI	PEMILIK	
CATATAN	<p>1. PELAKSANA ATAU SUBKON WAJIB MEMERIKSA KEMBALI KESESUAIN GAMBAR DENGAN KONDISI LAPANGAN</p>	
JUDUL GAMBAR	SKALA	
1. ARS	1 : 100	
TANGGAL :	REVISI :	
5 AGUSTUS 2024	R1	
KODE GAMBAR	ARS-01-01	
NO. LBR	JUMLAH LBR	
00	00	

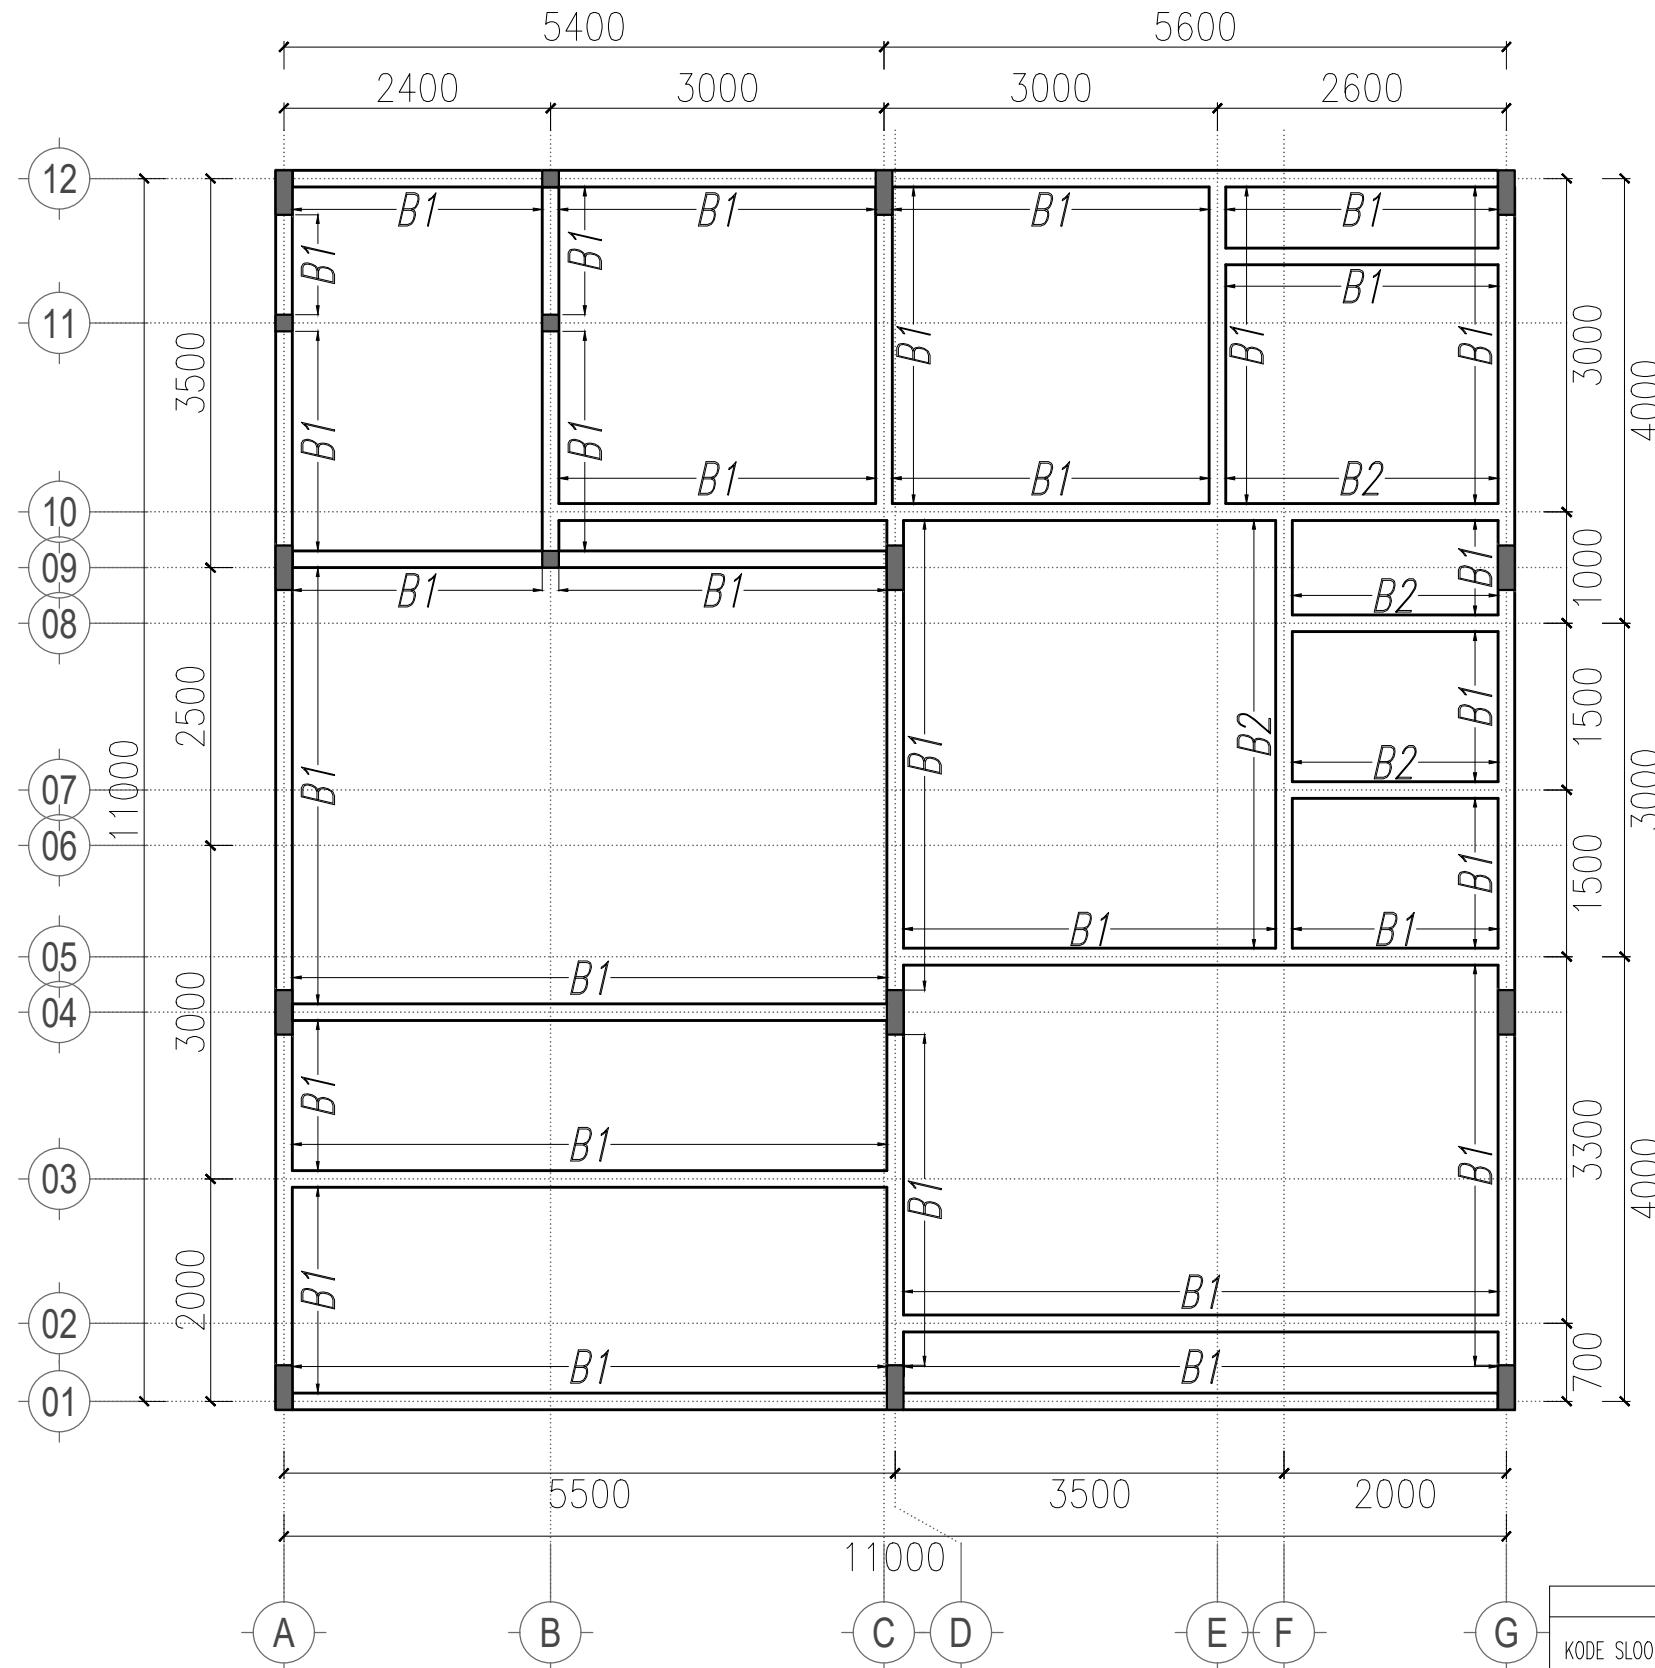


**DENAH BALOK LANTAI 2 SFL+4.15**

SKALA 1 : 100


KODE SLOOF	B1		B2	
	TUMPUAN	LAPANGAN	TUMPUAN	LAPANGAN
	-	-	-	-
DIMENSI	150x300	150x300	150x200	150x200
TULANGAN ATAS	2013	2013	2010	2010
TULANGAN TENGAH	-	-	-	-
TULANGAN BAWAH	2013	2013	2010	2010
SENGKANG	#8-150	#8-150	#8-150	#8-150

NAMA PROYEK	
<b>RUMAH TINGGAL 2 LANTAI</b>	
LOKASI PROYEK	-
PENANGGUNG JAWAB	-
DIGAMBAR	PELAKSANA
DISETUJUI	PEMILIK
CATATAN	
1. PELAKSANA ATAU SUBKON WAJIB MEMERIKSA KEMBALI KESESUAIN GAMBAR DENGAN KONDISI LAPANGAN	
JUDUL GAMBAR	SKALA
1. ARS	1 : 100
TANGGAL :	REVISI :
5 AGUSTUS 2024	R1
KODE GAMBAR	
ARS-01-01	
NO. LBR	JUMLAH LBR
00	00

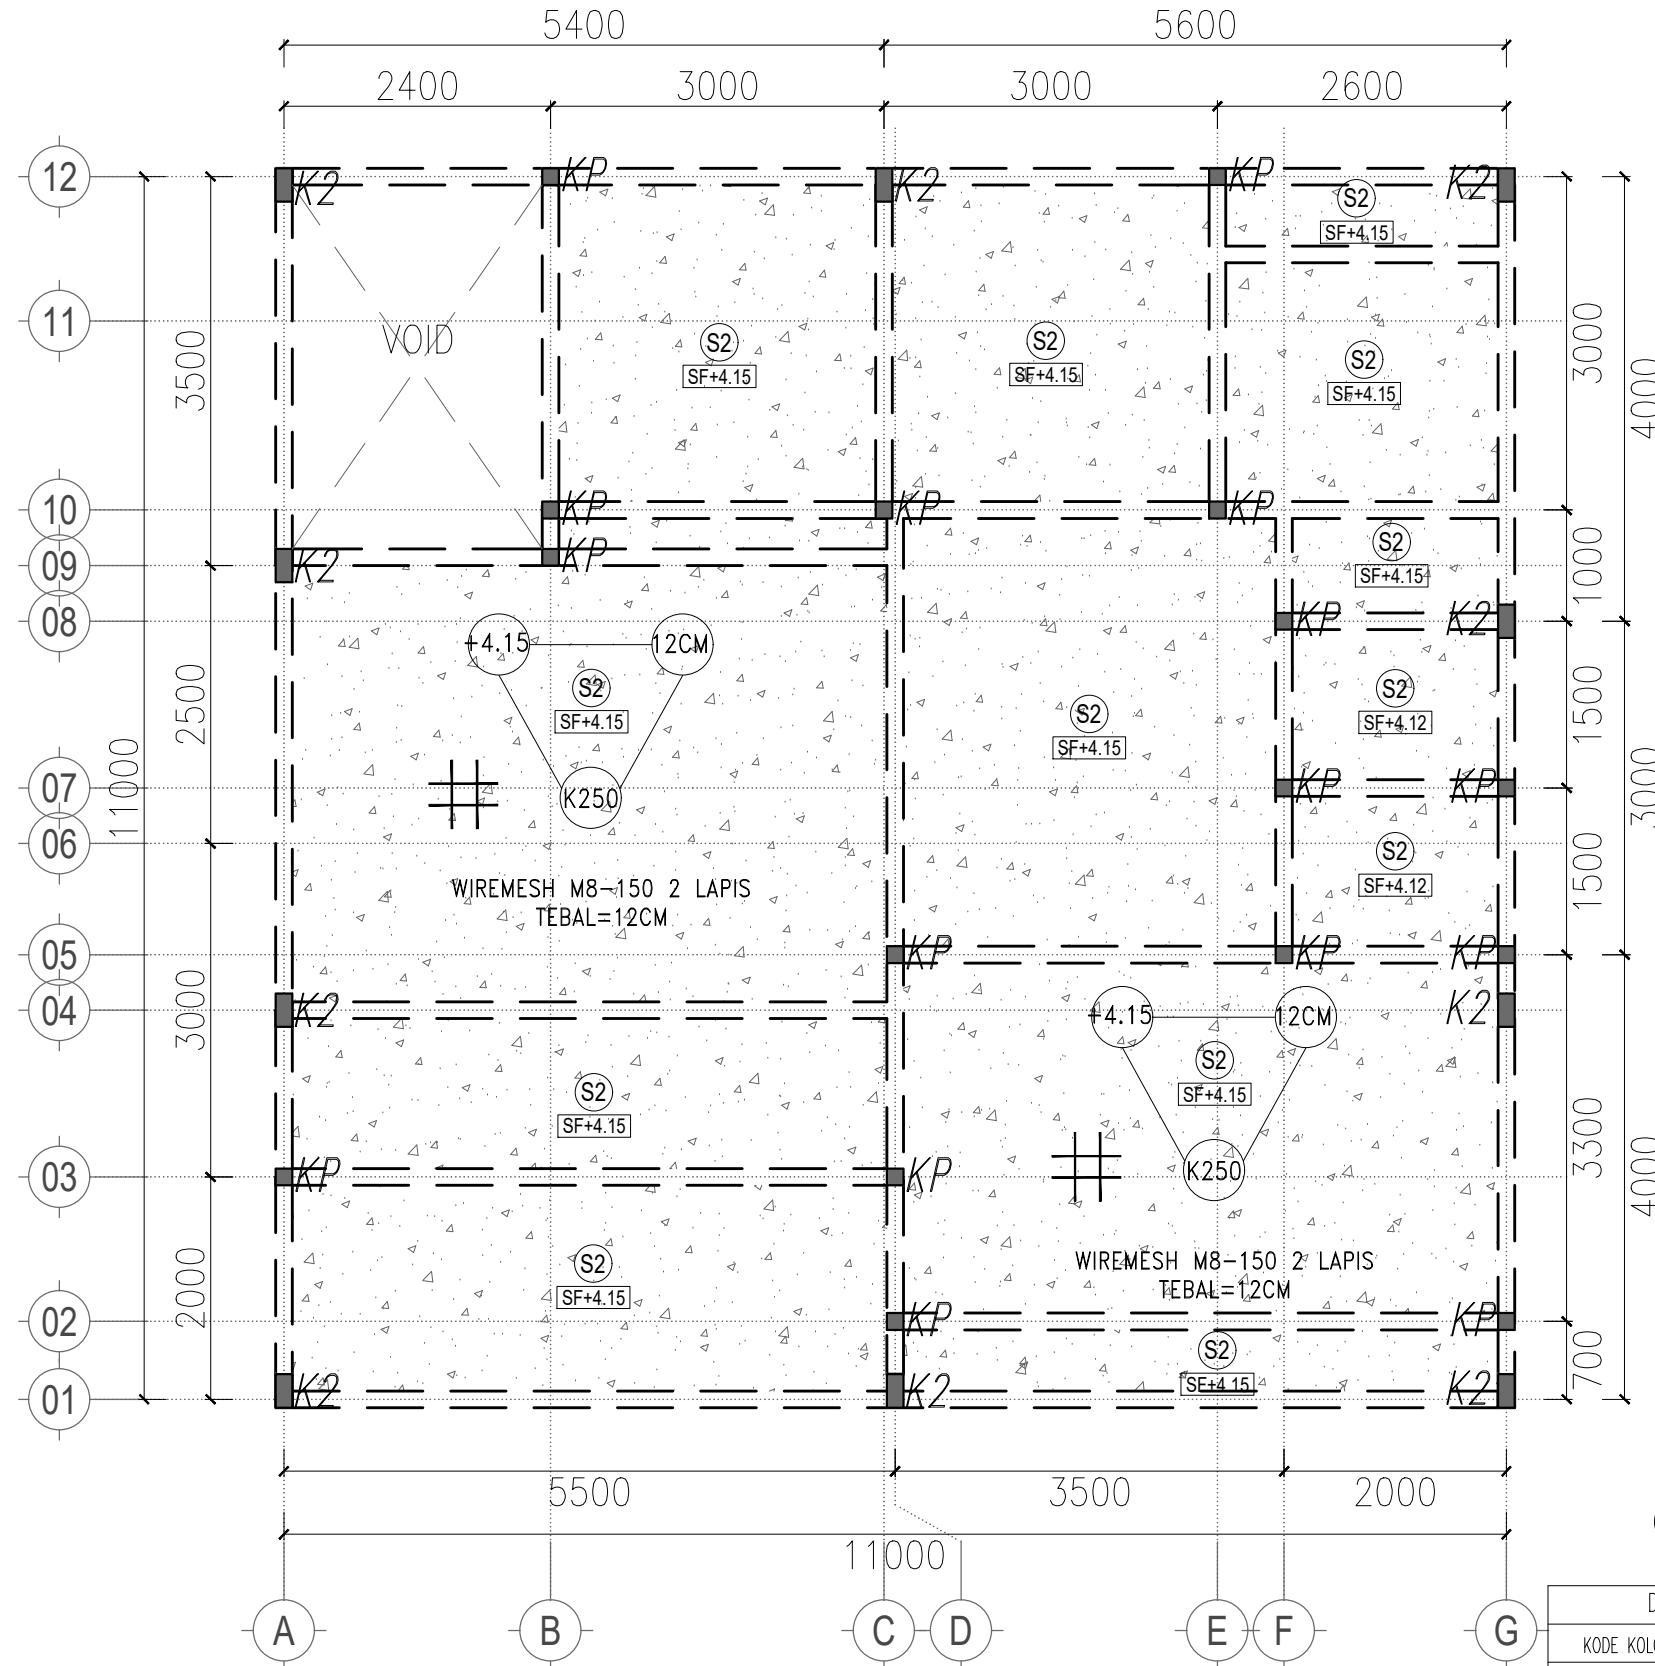

DETAIL PENULANGAN KOLOM			
KODE KOLOM	K1	K2	KP
	400 L150	300 L150	150 L150
DIMENSI	150x400	150x300	150x150
TULANGAN UTAMA	60x13	60x13	4x10
SENGKANG	ø8-150	ø8-150	ø8-150


NAMA PROYEK	
<b>RUMAH TINGGAL 2 LANTAI</b>	
LOKASI PROYEK	
-	-
PENANGGUNG JAWAB	
DIGAMBAR	PELAKSANA
DISETUJUI	PEMILIK
CATATAN	
1. PELAKSANA ATAU SUBKON WAJIB MEMERIKSA KEMBALI KESESUAIN GAMBAR DENGAN KONDISI LAPANGAN	
JUDUL GAMBAR	SKALA
1. ARS	1 : 100
TANGGAL :	REVISI :
5 AGUSTUS 2024	R1
KODE GAMBAR	
ARS-01-01	
NO. LBR	JUMLAH LBR
00	00

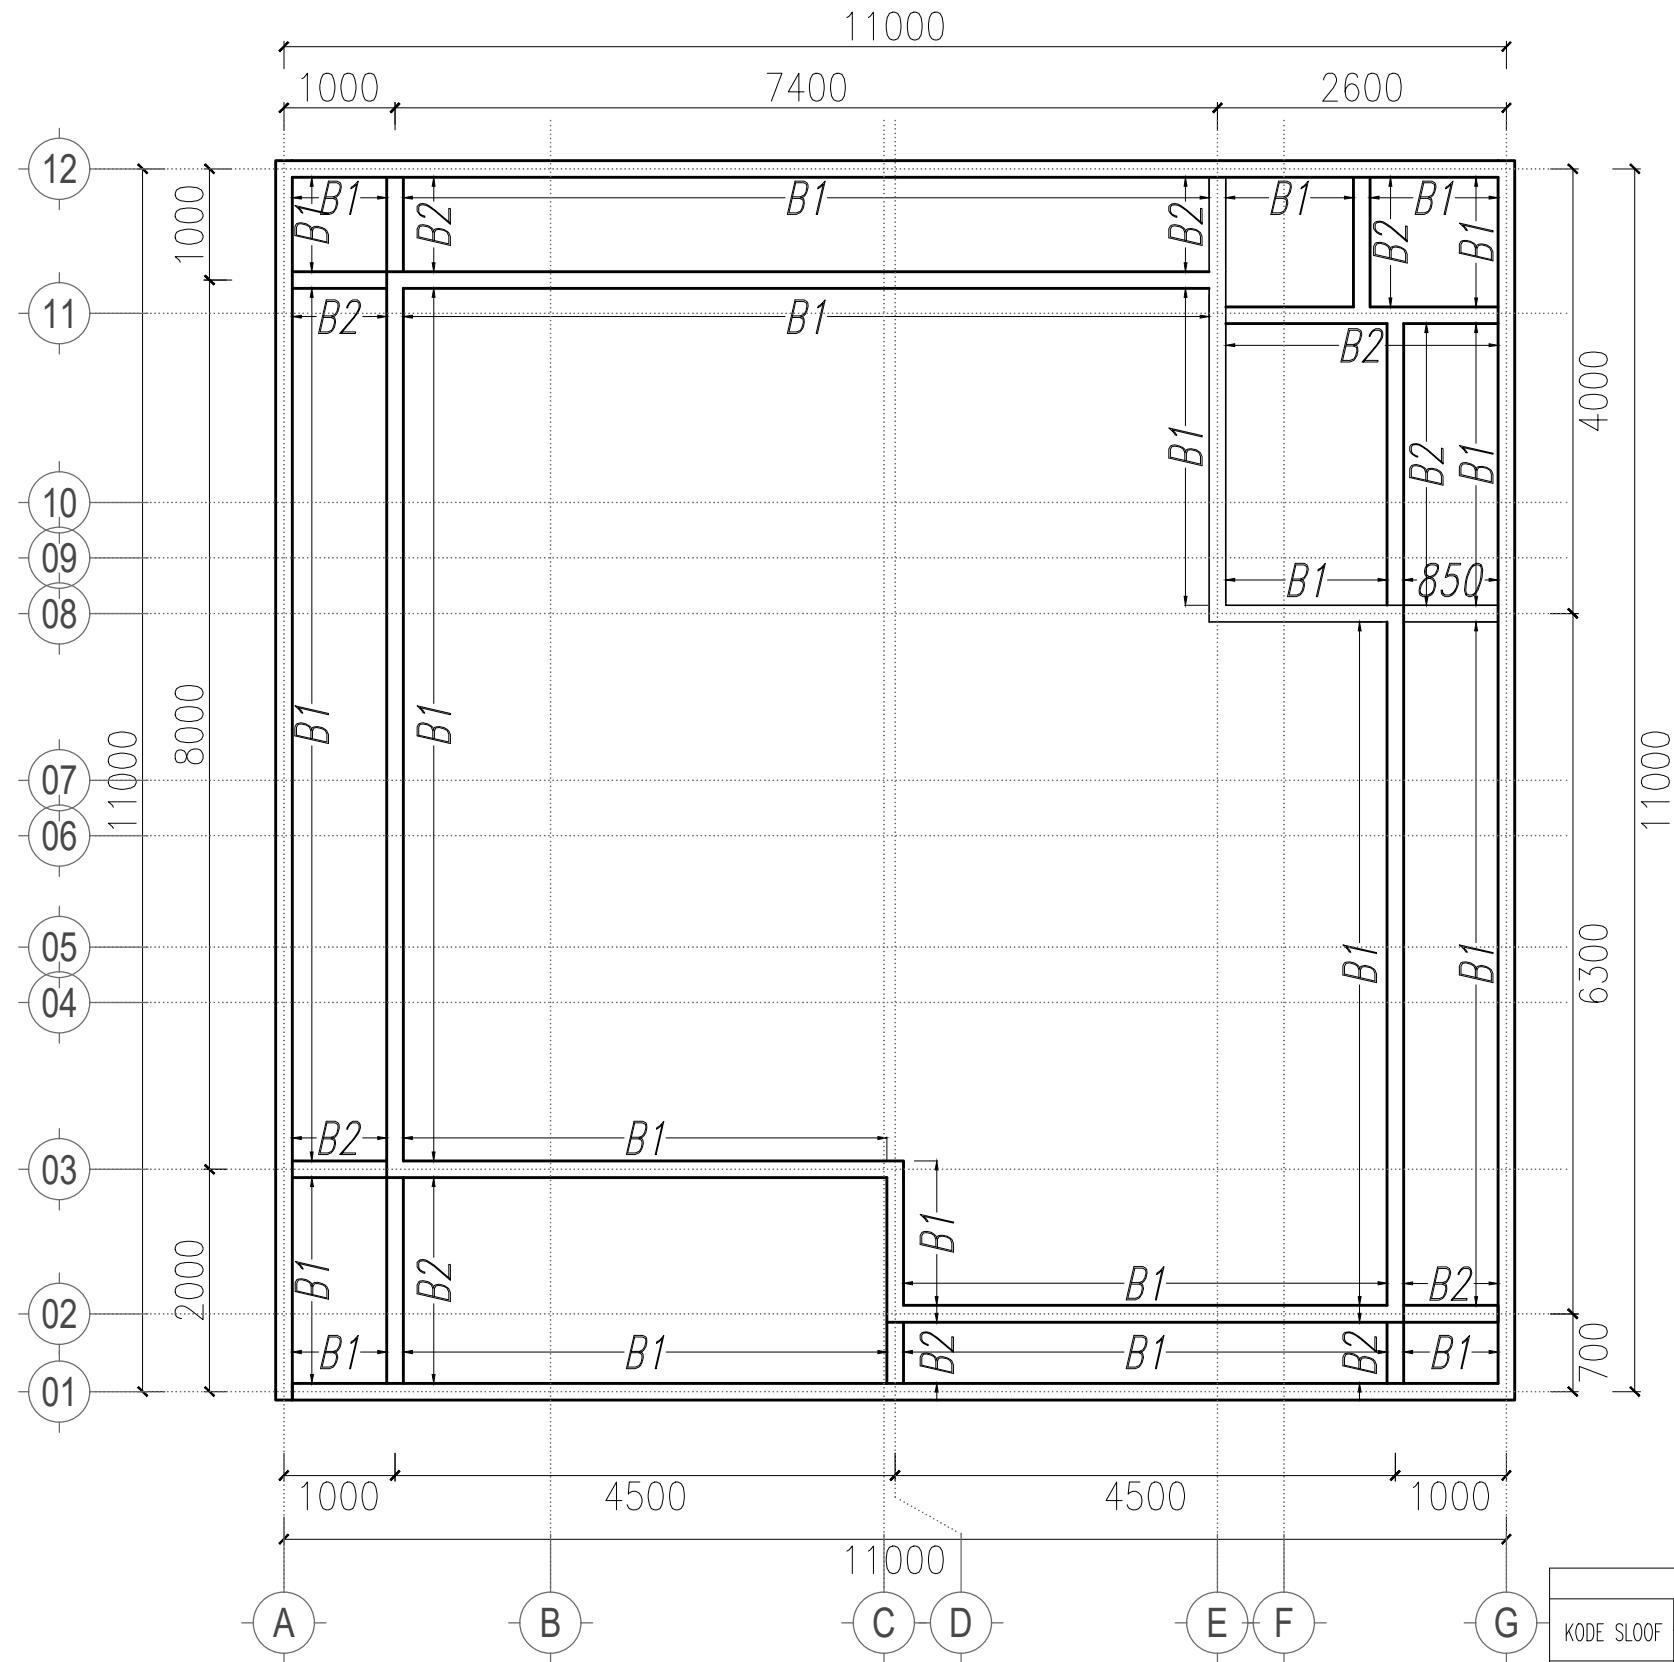

## DENAH BALOK TALANG SFL+8.40


SKALA 1 : 100

KODE SLOOF	B1		B2	
	TUMPUAN	LAPANGAN	TUMPUAN	LAPANGAN
	300	150	300	150
	2013	2013	2010	2010
	-	-	-	-
	2013	2013	2010	2010
	88-150	88-150	88-150	88-150


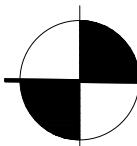


# DENAH PLAT TALANG SFL+8.20

SKALA 1 : 100

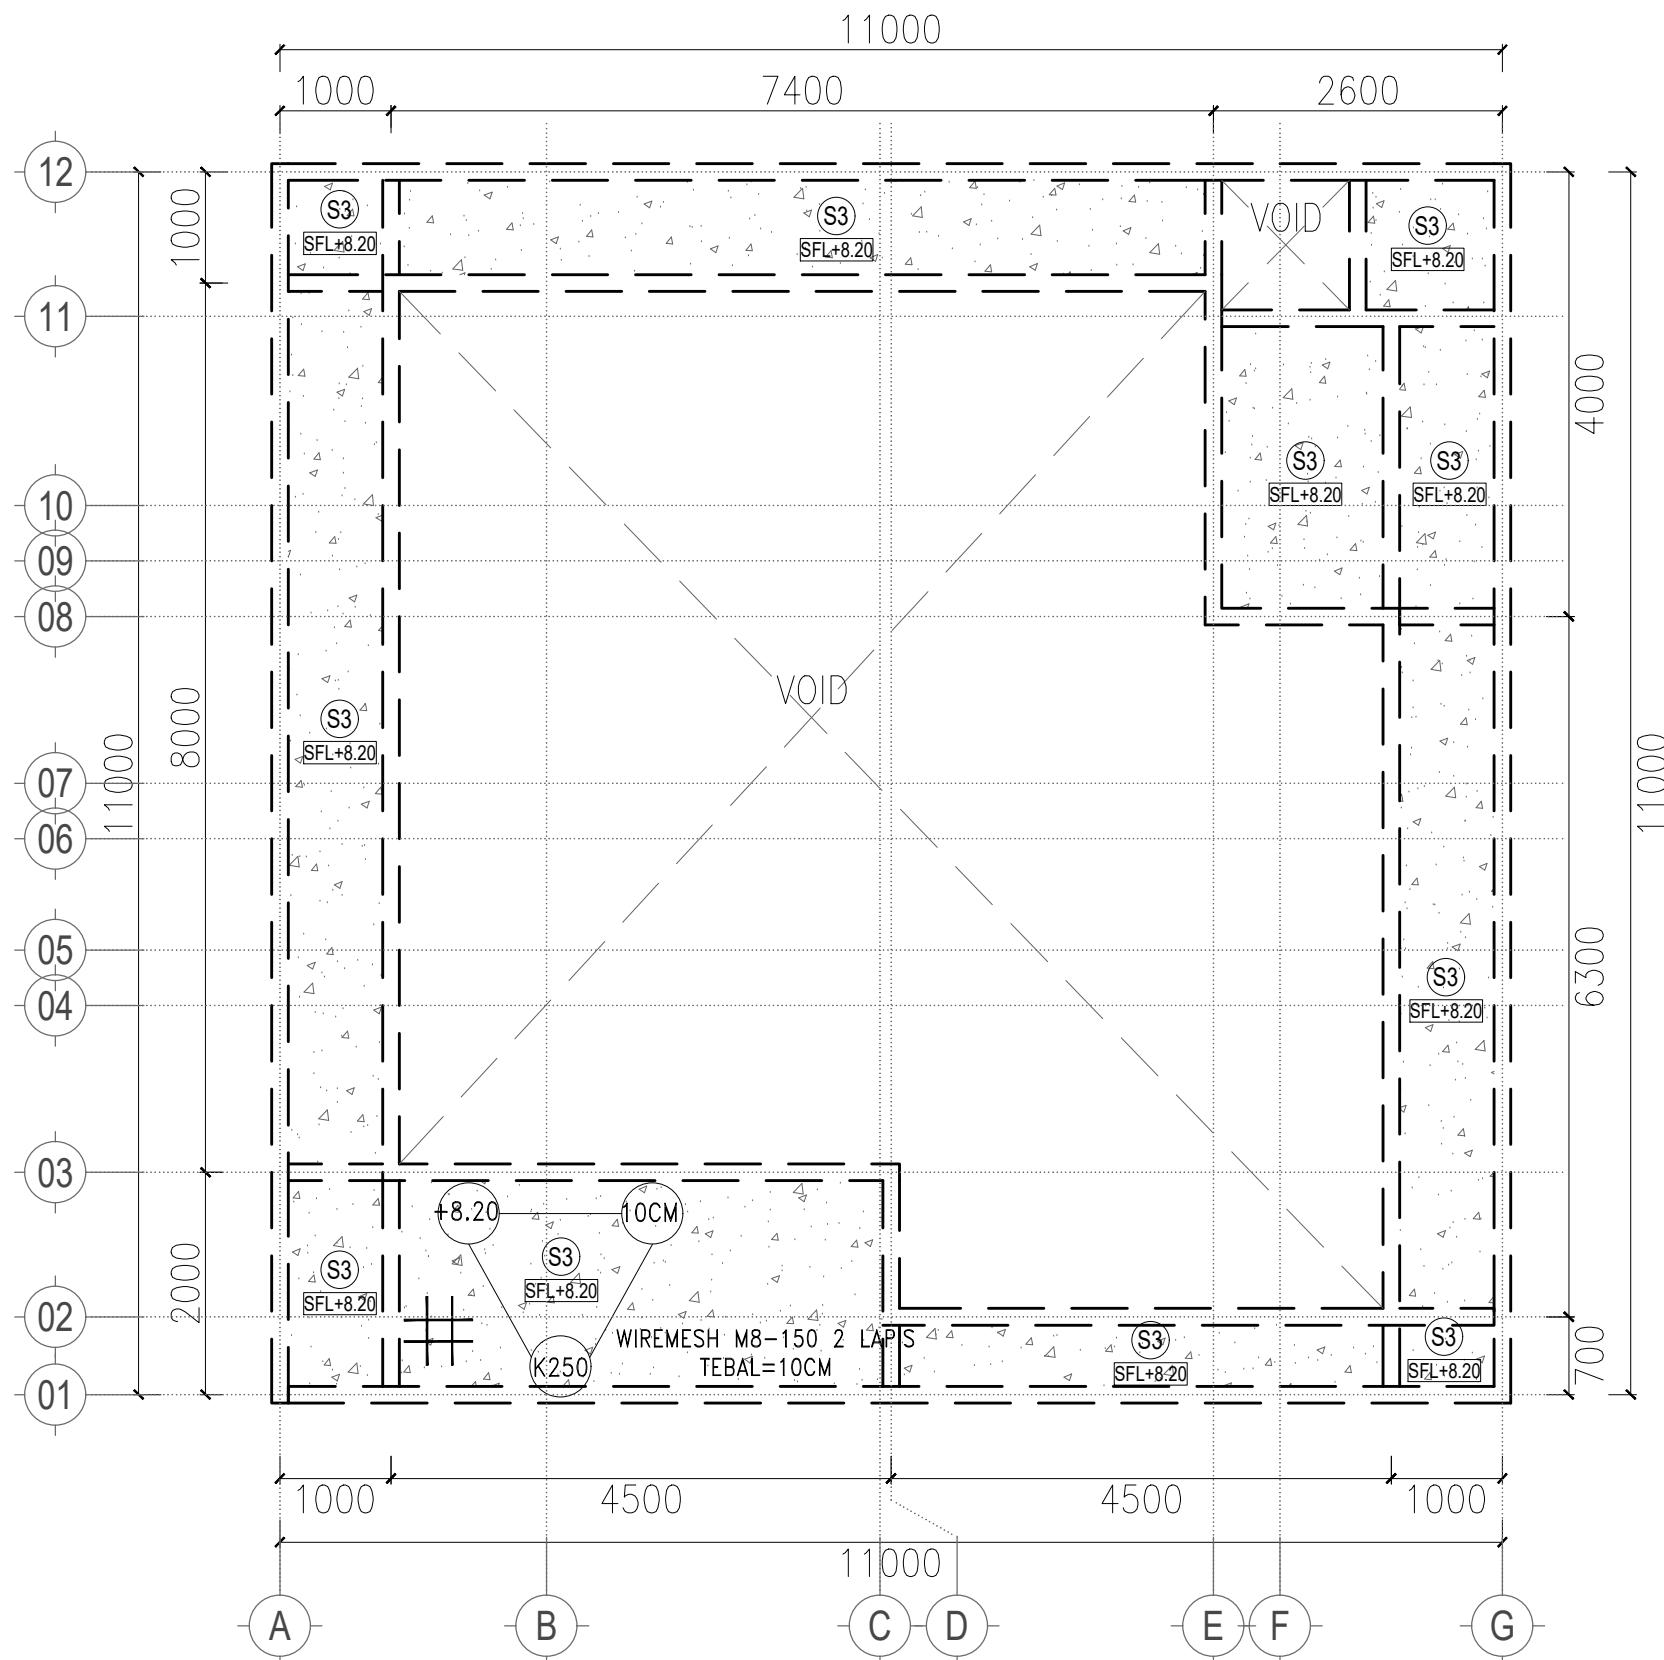

01 DETAIL S3  
STR-00-00 NTS

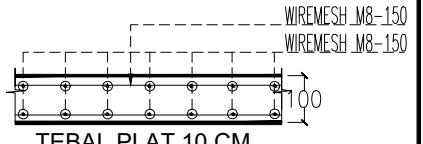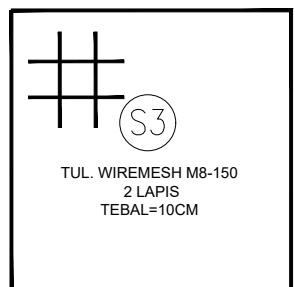

NAMA PROYEK	
<b>RUMAH TINGGAL 2 LANTAI</b>	
LOKASI PROYEK	
-	
-	
PENANGGUNG JAWAB	
DIGAMBAR	PELAKSANA
DISETUJUI	PEMILIK
CATATAN	
1. PELAKSANA ATAU SUBKON WAJIB MEMERIKSA KEMBALI KESESUAIN GAMBAR DENGAN KONDISI LAPANGAN	
JUDUL GAMBAR	SKALA
1. ARS	1 : 100
TANGGAL :	REVISI :
5 AGUSTUS 2024	<b>R1</b>
KODE GAMBAR	
ARS-01-01	
NO. LBR	JUMLAH LBR
00	00

NAMA PROYEK	
<b>RUMAH TINGGAL 2 LANTAI</b>	
LOKASI PROYEK	
-	
PENANGGUNG JAWAB	
DIGAMBAR	PELAKSANA
DISETUJUI	PEMILIK
CATATAN	
1. PELAKSANA ATAU SUBKON WAJIB MEMERIKSA KEMBALI KESESUAIN GAMBAR DENGAN KONDISI LAPANGAN	
JUDUL GAMBAR	SKALA
1.DETAIL SLOOF, BALOK DAN KOLOM	1 : 5
TANGGAL :	REVISI :
5 AGUSTUS 2024	<b>R1</b>
KODE GAMBAR	
STR-03-15	
NO. LBR	JUMLAH LBR
15	00

### DETAIL PENULANGAN KOLOM

KODE KOLOM	K1	K2	KP
DIMENSI	150x400	150x300	150x150
TULANGAN UTAMA	6D13	6D13	4Ø10
SENGKANG	Ø8-150	Ø8-150	Ø8-150

### DETAIL PENULANGAN BALOK

KODE SLOOF	B1		B2	
	TUMPUAN	LAPANGAN	TUMPUAN	LAPANGAN
DIMENSI	150x300	150x300	150x200	150x200
TULANGAN ATAS	2D13	2D13	2Ø10	2Ø10
TULANGAN TENGAH	-	-	-	-
TULANGAN BAWAH	2D13	2D13	2Ø10	2Ø10
SENGKANG	Ø8-150	Ø8-150	Ø8-150	Ø8-150

### DETAIL PENULANGAN SLOOF

KODE SLOOF	BS1	
	TUMPUAN	LAPANGAN
DIMENSI	150x300	150x300
TULANGAN ATAS	2D13	2D13
TULANGAN TENGAH	-	-
TULANGAN BAWAH	2D13	2D13
SENGKANG	Ø8-150	Ø8-150

### DETAIL SLOOF, BALOK, DAN KOLOM

01


AR-00-00

SKALA 1 : 5

STR-03-15


NO. LBR JUMLAH LBR

15 00

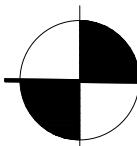

## DENAH INSTALASI AIR BERSIH LT 1


SKALA 1 : 100

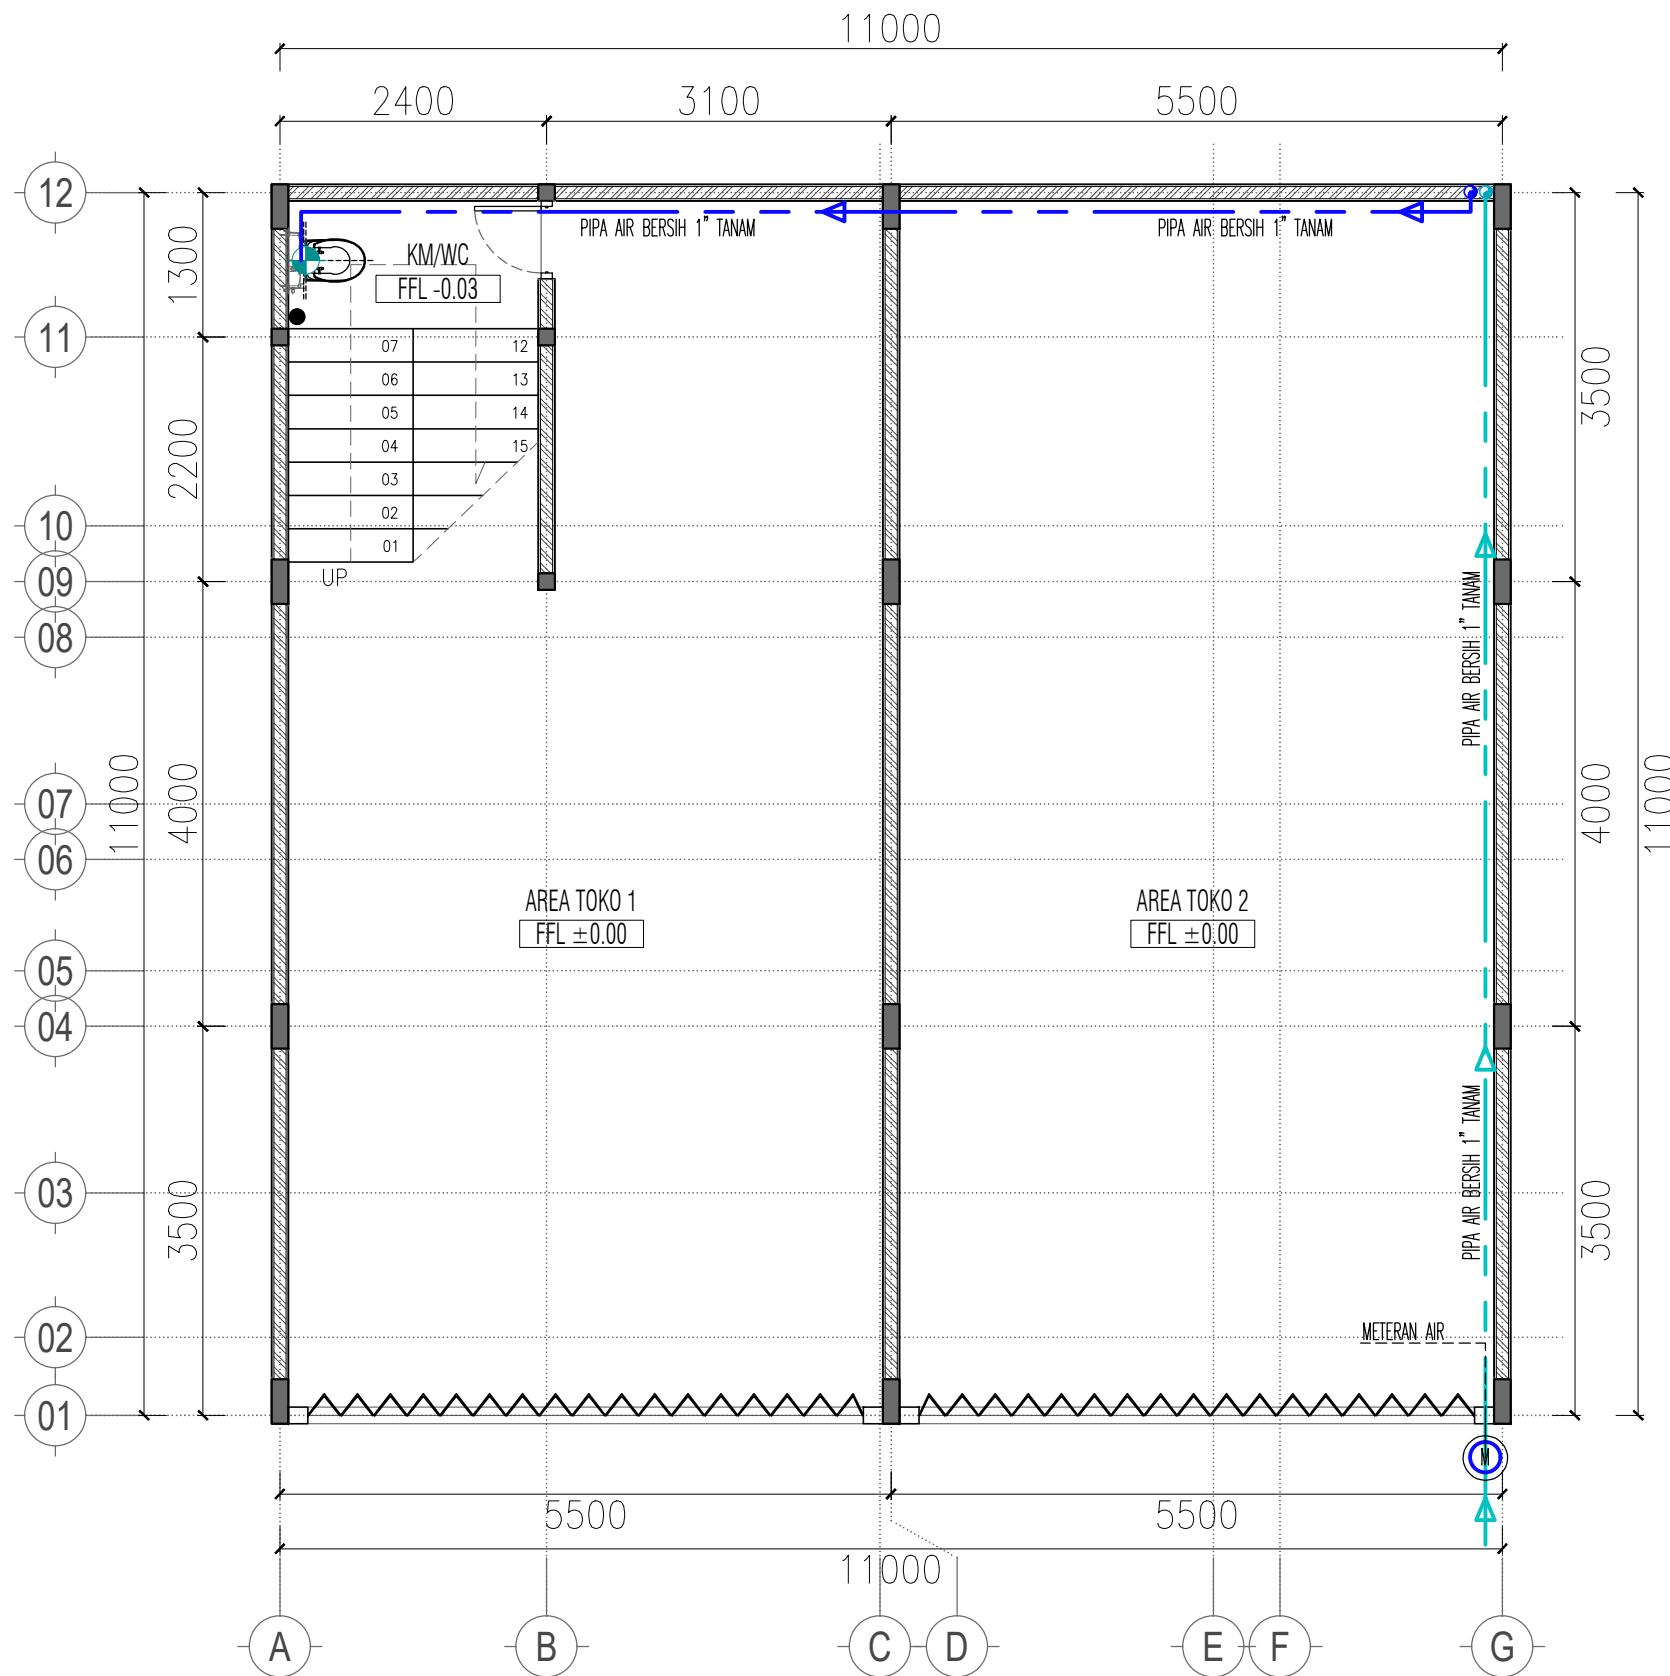

NO	ITEM	KETERANGAN
1.		RISER PIPA AIR BERSIH 1" DARI TANDON
2.		RISER PIPA AIR BERSIH 1" MENUJU TANDON
3.		TITIK AIR BERSIH 1/2"
4.		PIPA AIR BERSIH 1" DARI TANDON
5.		PIPA AIR BERSIH 1" MENUJU TANDON

NAMA PROYEK	
<b>RUMAH TINGGAL 2 LANTAI</b>	
LOKASI PROYEK	
-	
-	
PENANGGUNG JAWAB	
DIGAMBAR	PELAKSANA
DISETUJUI	PEMILIK
CATATAN	
1. PELAKSANA ATAU SUBKON WAJIB MEMERIKSA KEMBALI KESESUAIN GAMBAR DENGAN KONDISI LAPANGAN	
JUDUL GAMBAR	SKALA
1. ARS	1 : 100
TANGGAL :	REVISI :
5 AGUSTUS 2024	<b>R1</b>
KODE GAMBAR	
ARS-01-01	
NO. LBR	JUMLAH LBR
00	00



NAMA PROYEK	RUMAH TINGGAL 2 LANTAI
LOKASI PROYEK	-
PENANGGUNG JAWAB	
DIGAMBAR	PELAKSANA
DISETUJUI	PEMILIK
CATATAN	<p>1. PELAKSANA ATAU SUBKON WAJIB MEMERIKSA KEMBALI KESESUAIN GAMBAR DENGAN KONDISI LAPANGAN</p>
JUDUL GAMBAR	SKALA
1. ARS	1 : 100
TANGGAL :	REVISI :
5 AGUSTUS 2024	R1
KODE GAMBAR	
ARS-01-01	
NO. LBR	JUMLAH LBR
00	00

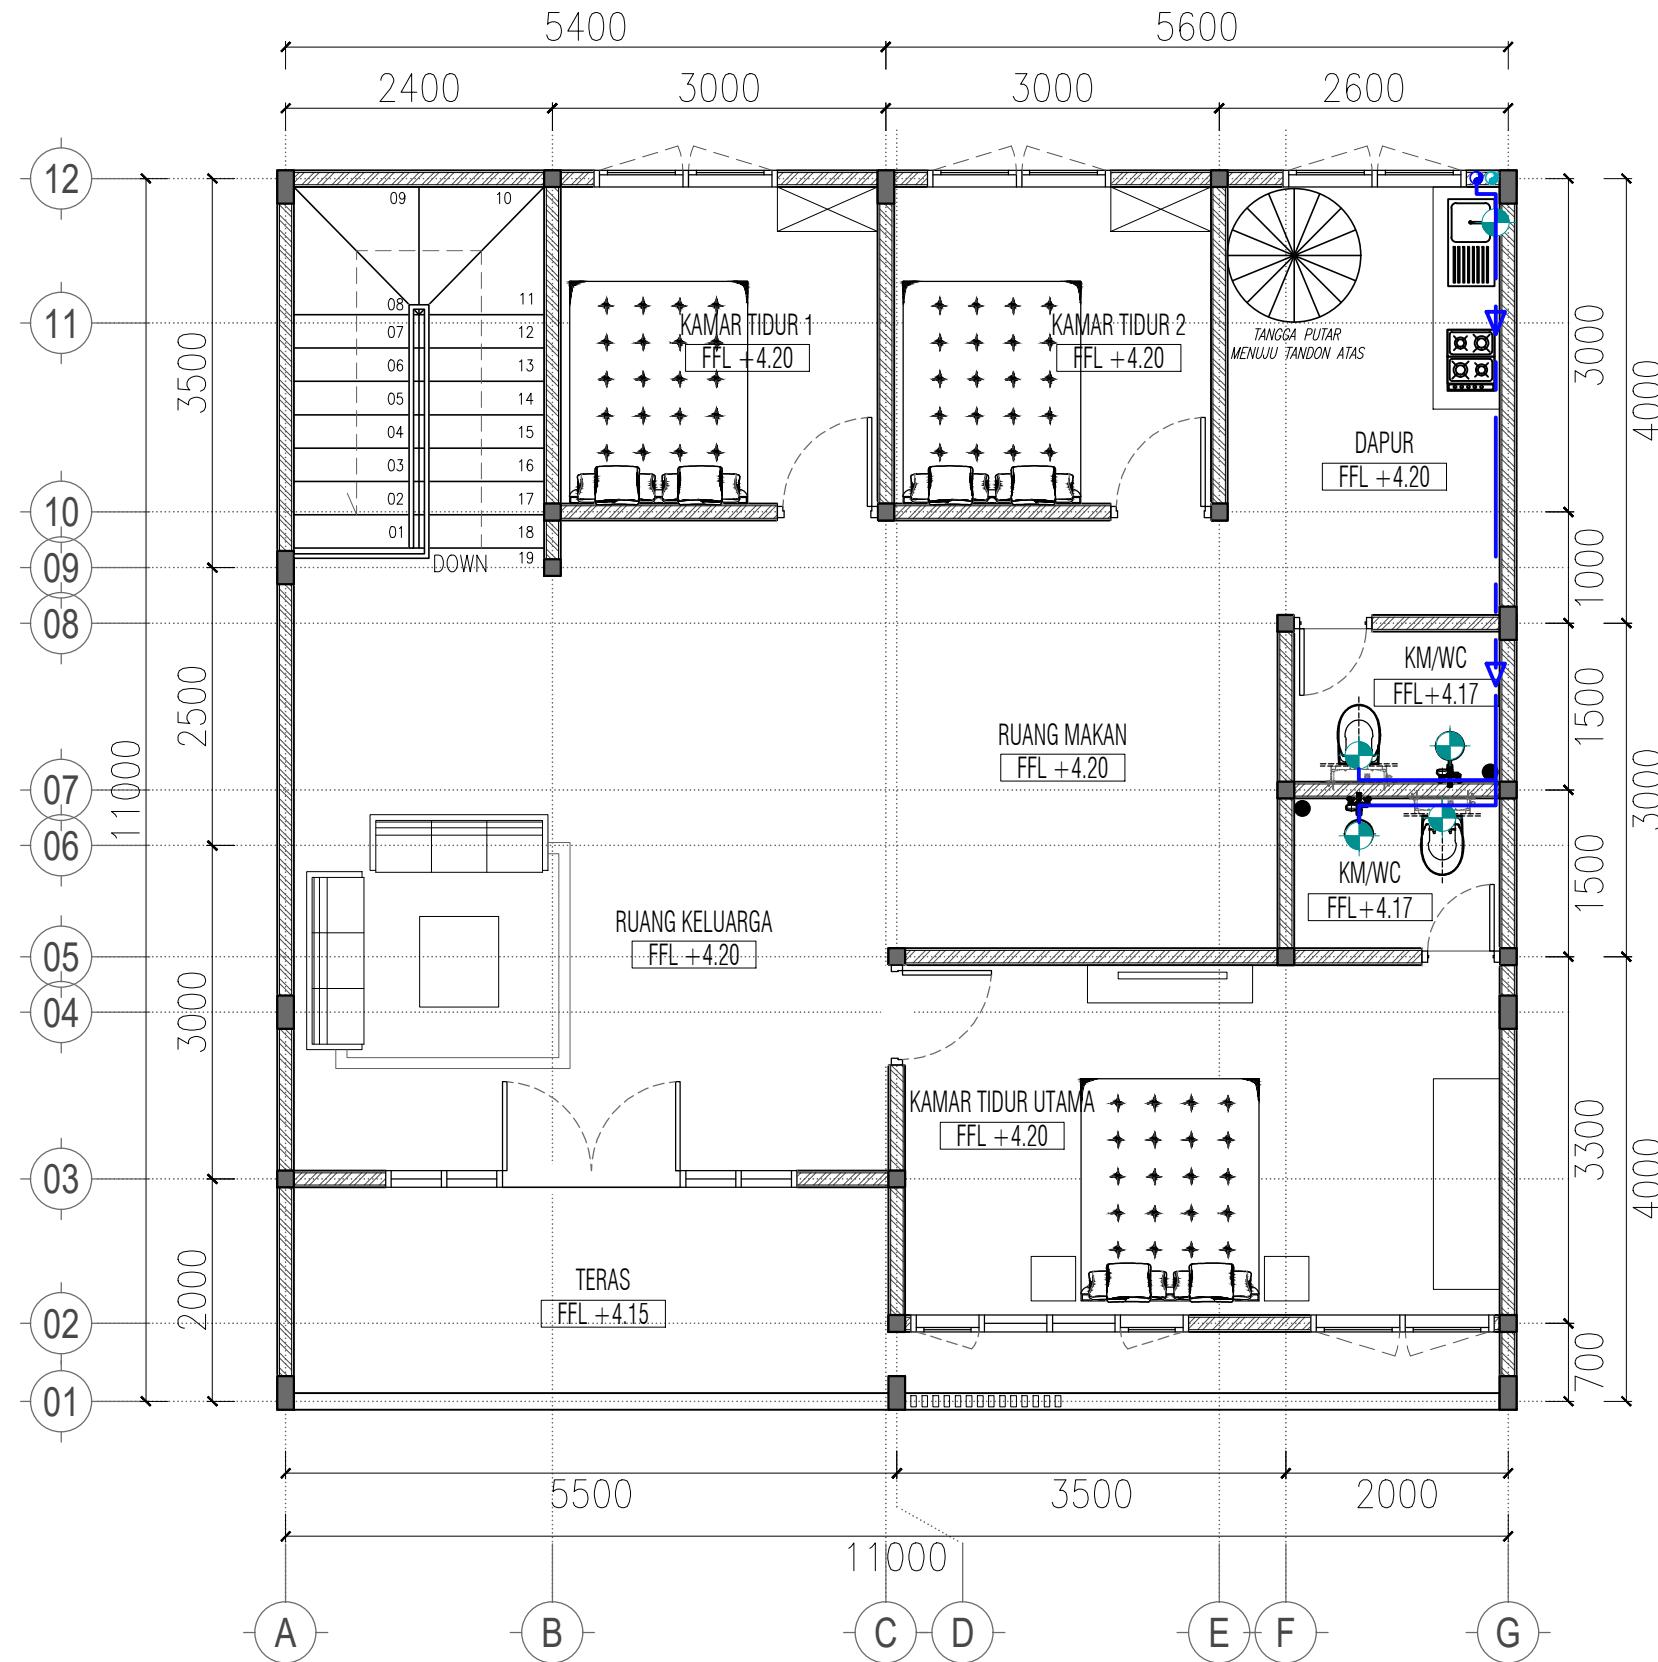

**DENAH INSTALASI AIR BERSIH LT 2**  
SKALA 1 : 100

NO	ITEM	KETERANGAN
1.	●	RISER PIPA AIR BERSIH 1" DARI TANDON
2.	●	RISER PIPA AIR BERSIH 1" MENUJU TANDON
3.	●	TITIK AIR BERSIH 1/2"
4.	—■—	PIPA AIR BERSIH 1" DARI TANDON
5.	—■—	PIPA AIR BERSIH 1" MENUJU TANDON

NAMA PROYEK	RUMAH TINGGAL 2 LANTAI
LOKASI PROYEK	-
PENANGGUNG JAWAB	
DIGAMBAR	PELAKSANA
DISETUJUI	PEMILIK
CATATAN	<p>1. PELAKSANA ATAU SUBKON WAJIB MEMERIKSA KEMBALI KESESUAIN GAMBAR DENGAN KONDISI LAPANGAN</p>
JUDUL GAMBAR	SKALA
1. ARS	1 : 100
TANGGAL :	REVISI :
5 AGUSTUS 2024	R1
KODE GAMBAR	
ARS-01-01	
NO. LBR	JUMLAH LBR
00	00

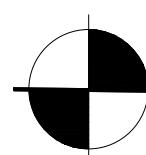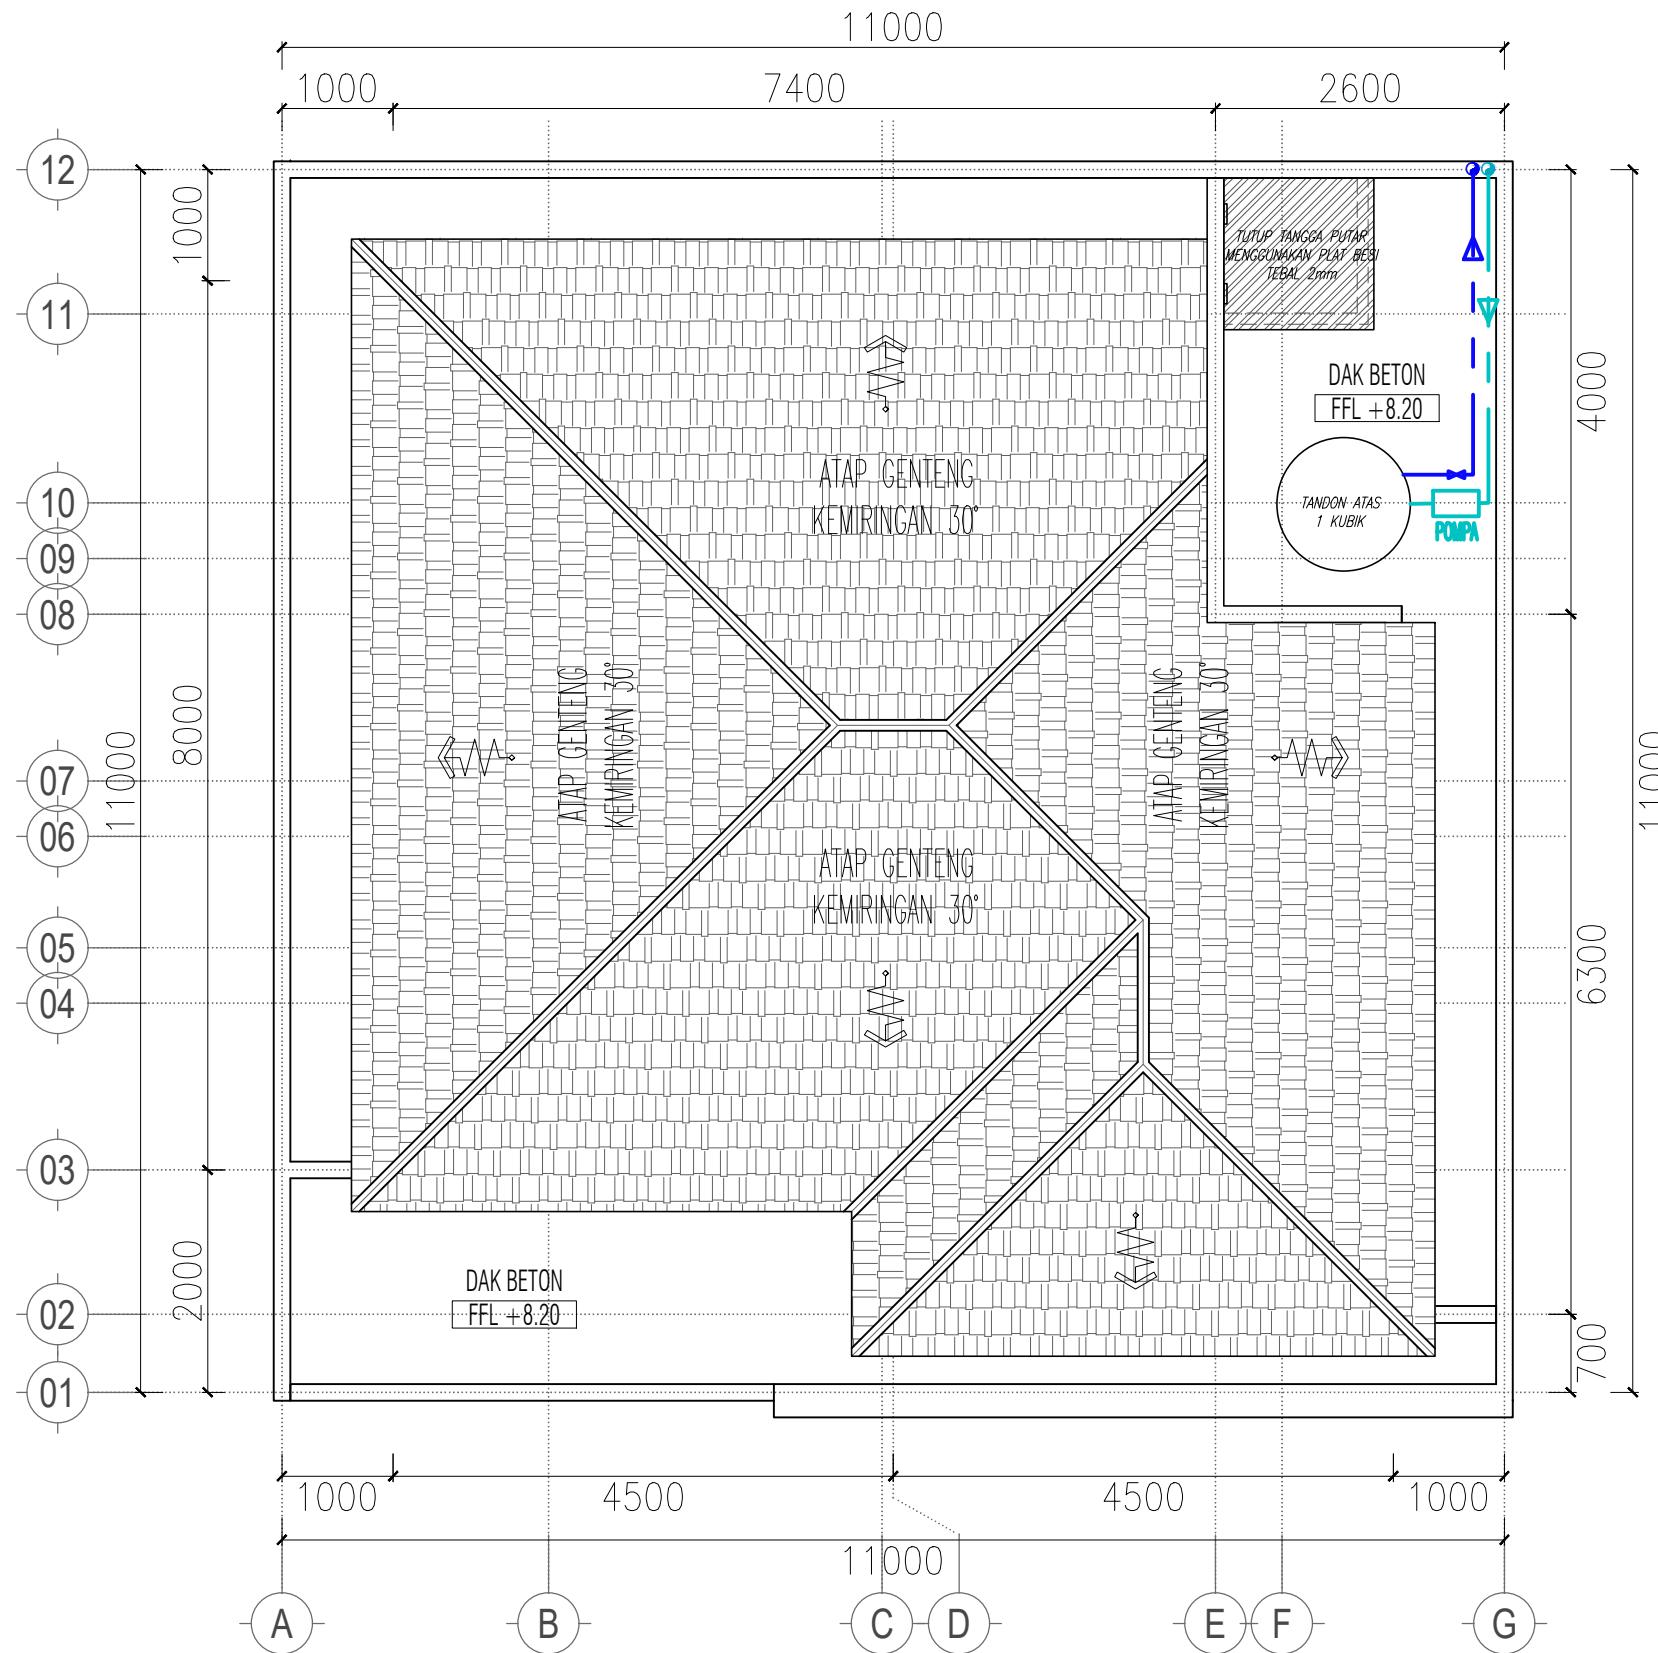


## DENAH INSTALASI AIR BERSIH ATAP

SKALA 1 : 100

NO	ITEM	KETERANGAN
1.	●	RISER PIPA AIR BERSIH 1" DARI TANDON
2.	●	RISER PIPA AIR BERSIH 1" MENUJU TANDON
3.	●	TITIK AIR BERSIH 1/2"
4.	—■—	PIPA AIR BERSIH 1" DARI TANDON
5.	—■—	PIPA AIR BERSIH 1" MENUJU TANDON

NAMA PROYEK	
<b>RUMAH TINGGAL 2 LANTAI</b>	
LOKASI PROYEK	
<p style="text-align: center;">-</p> <p style="text-align: center;">-</p>	
PENANGGUNG JAWAB	
DIGAMBAR	PELAKSANA
DISETUJUI	PEMILIK
CATATAN	
<p>1. PELAKSANA ATAU SUBKON WAJIB MEMERIKSA KEMBALI KESESUAIN GAMBAR DENGAN KONDISI LAPANGAN</p>	
JUDUL GAMBAR	
SKALA	
1. ARS	1 : 100
TANGGAL :	
REVISI :	
5 AGUSTUS 2024 <b>R1</b>	
KODE GAMBAR	
ARS-01-01	
NO. LBR	JUMLAH LBR
00	00

NAMA PROYEK	RUMAH TINGGAL 2 LANTAI
LOKASI PROYEK	-
PENANGGUNG JAWAB	
DIGAMBAR	PELAKSANA
DISETUJUI	PEMILIK
CATATAN	<p>1. PELAKSANA ATAU SUBKON WAJIB MEMERIKSA KEMBALI KESESUAIN GAMBAR DENGAN KONDISI LAPANGAN</p>
JUDUL GAMBAR	SKALA
1. ARS	1 : 100
TANGGAL :	REVISI :
5 AGUSTUS 2024	R1
KODE GAMBAR	
ARS-01-01	
NO. LBR	JUMLAH LBR
00	00


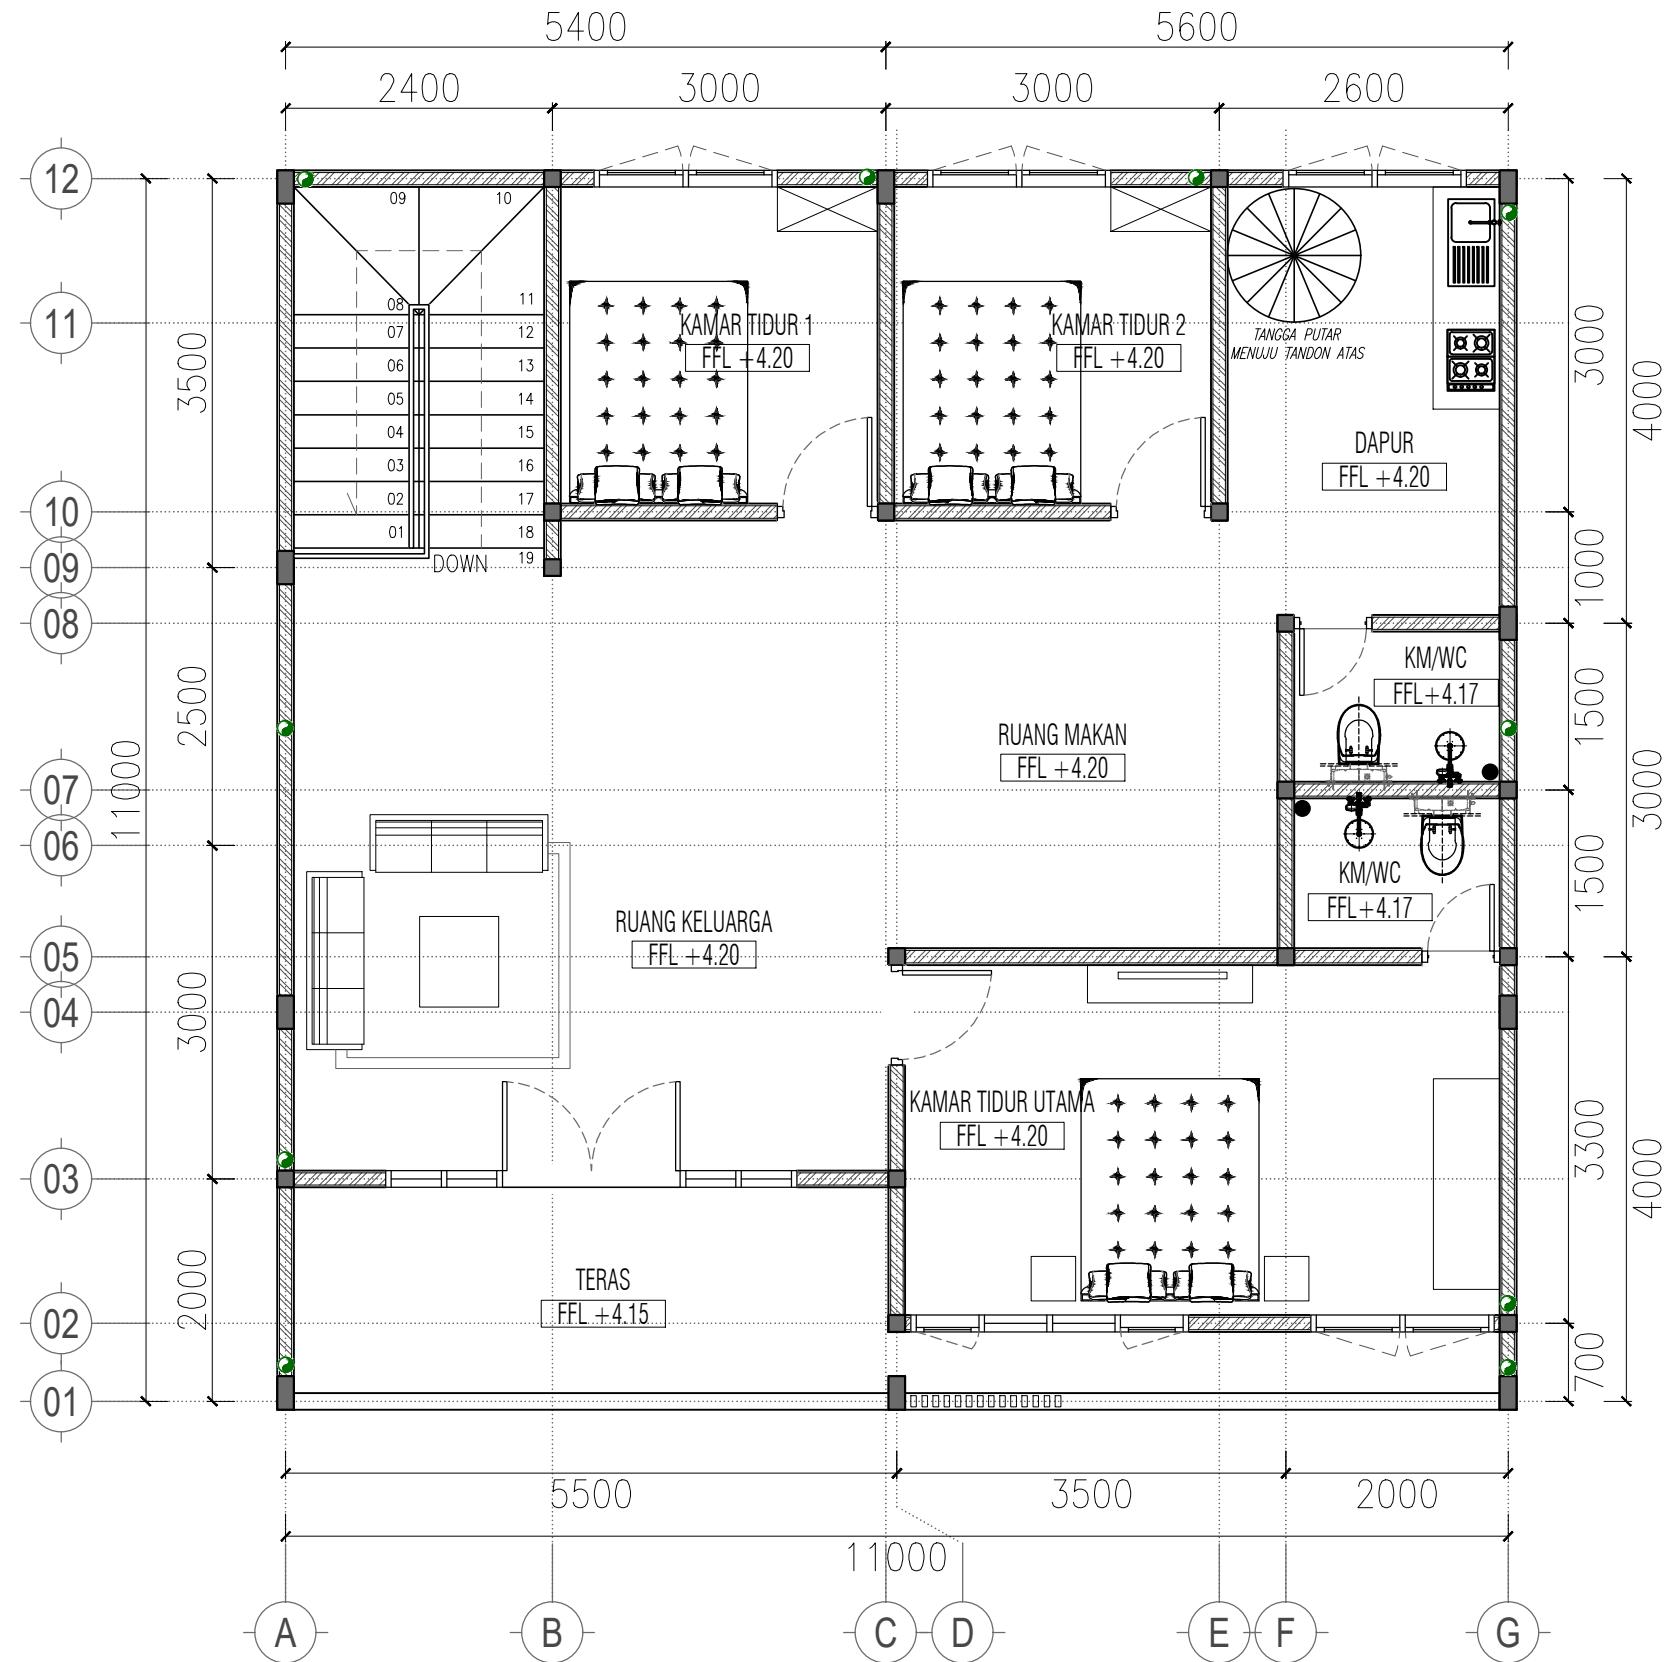


## DENAH INSTALASI AIR HUJAN LT 2

SKALA 1 : 100

NO	ITEM	KETERANGAN
1.		RISER PIPA AIR HUJAN 2,5"
2.		PIPA AIR HUJAN 2,5"
3.		PIPA AIR HUJAN 4"
4.		BAK KONTROL

NAMA PROYEK	RUMAH TINGGAL 2 LANTAI
LOKASI PROYEK	-
PENANGGUNG JAWAB	
DIGAMBAR	PELAKSANA
DISETUJUI	PEMILIK
CATATAN	<p>1. PELAKSANA ATAU SUBKON WAJIB MEMERIKSA KEMBALI KESESUAIN GAMBAR DENGAN KONDISI LAPANGAN</p>
JUDUL GAMBAR	SKALA
1. ARS	1 : 100
TANGGAL :	REVISI :
5 AGUSTUS 2024	R1
KODE GAMBAR	ARS-01-01
NO. LBR	JUMLAH LBR
00	00

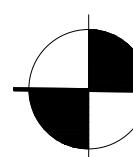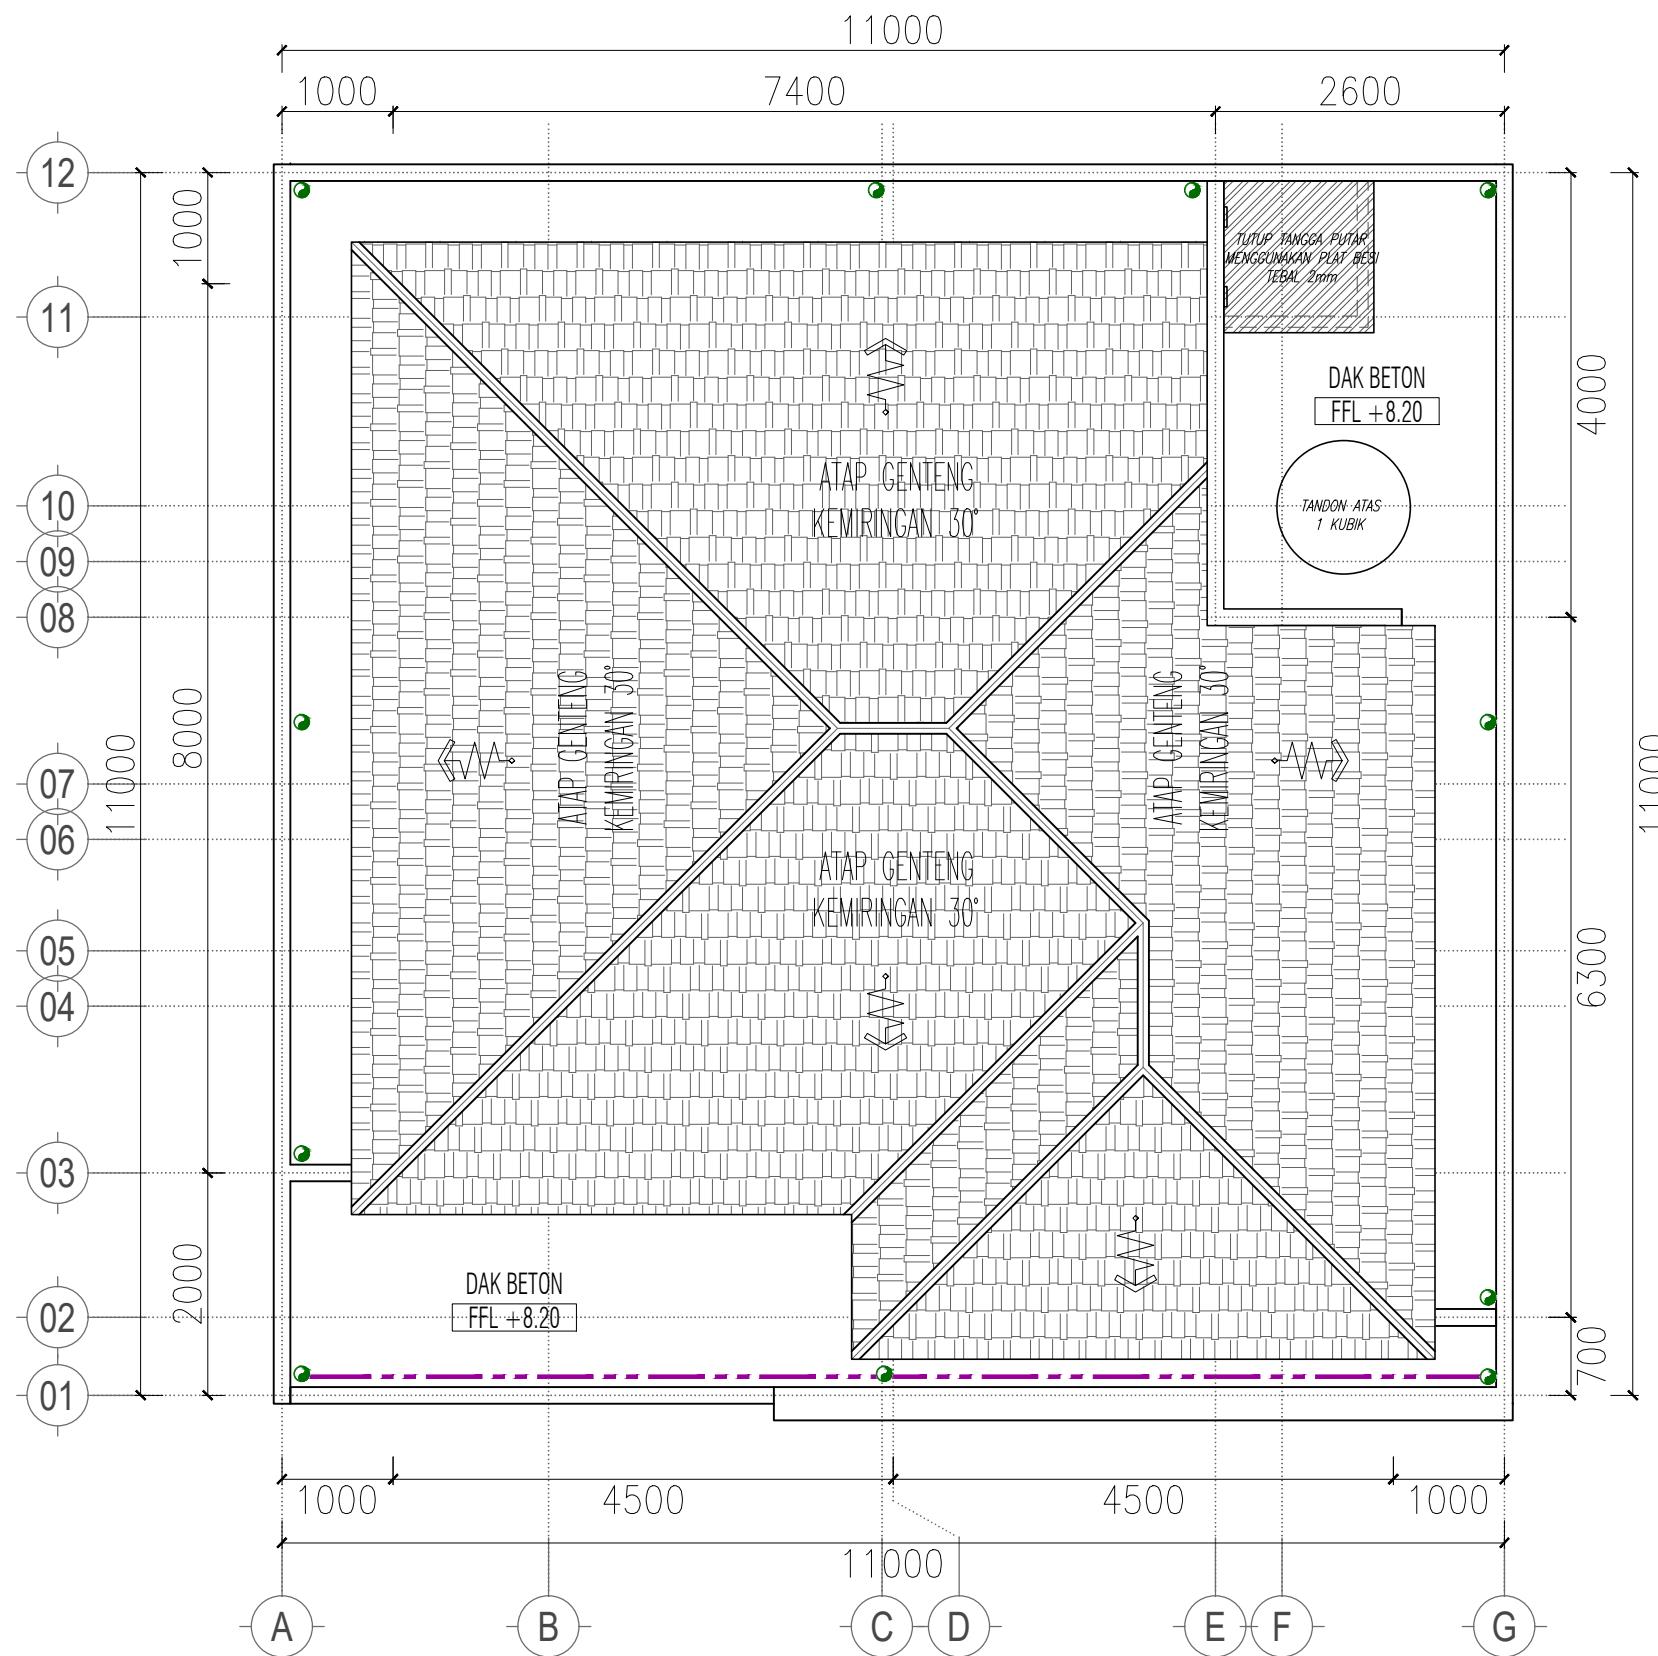


## DENAH INSTALASI AIR HUJAN ATAP

SKALA 1 : 100

NO	ITEM	KETERANGAN
1.		RISER PIPA AIR HUJAN 2,5"
2.		PIPA AIR HUJAN 2,5"
3.		PIPA AIR HUJAN 4"
4.		BAK KONTROL

NAMA PROYEK	RUMAH TINGGAL 2 LANTAI
LOKASI PROYEK	-
PENANGGUNG JAWAB	-
DIGAMBAR	PELAKSANA
DISETUJUI	PEMILIK
CATATAN	<p>1. PELAKSANA ATAU SUBKON WAJIB MEMERIKSA KEMBALI KESESUAIN GAMBAR DENGAN KONDISI LAPANGAN</p>
JUDUL GAMBAR	SKALA
1. ARS	1 : 100
TANGGAL :	REVISI :
5 AGUSTUS 2024	R1
KODE GAMBAR	ARS-01-01
NO. LBR	JUMLAH LBR
00	00

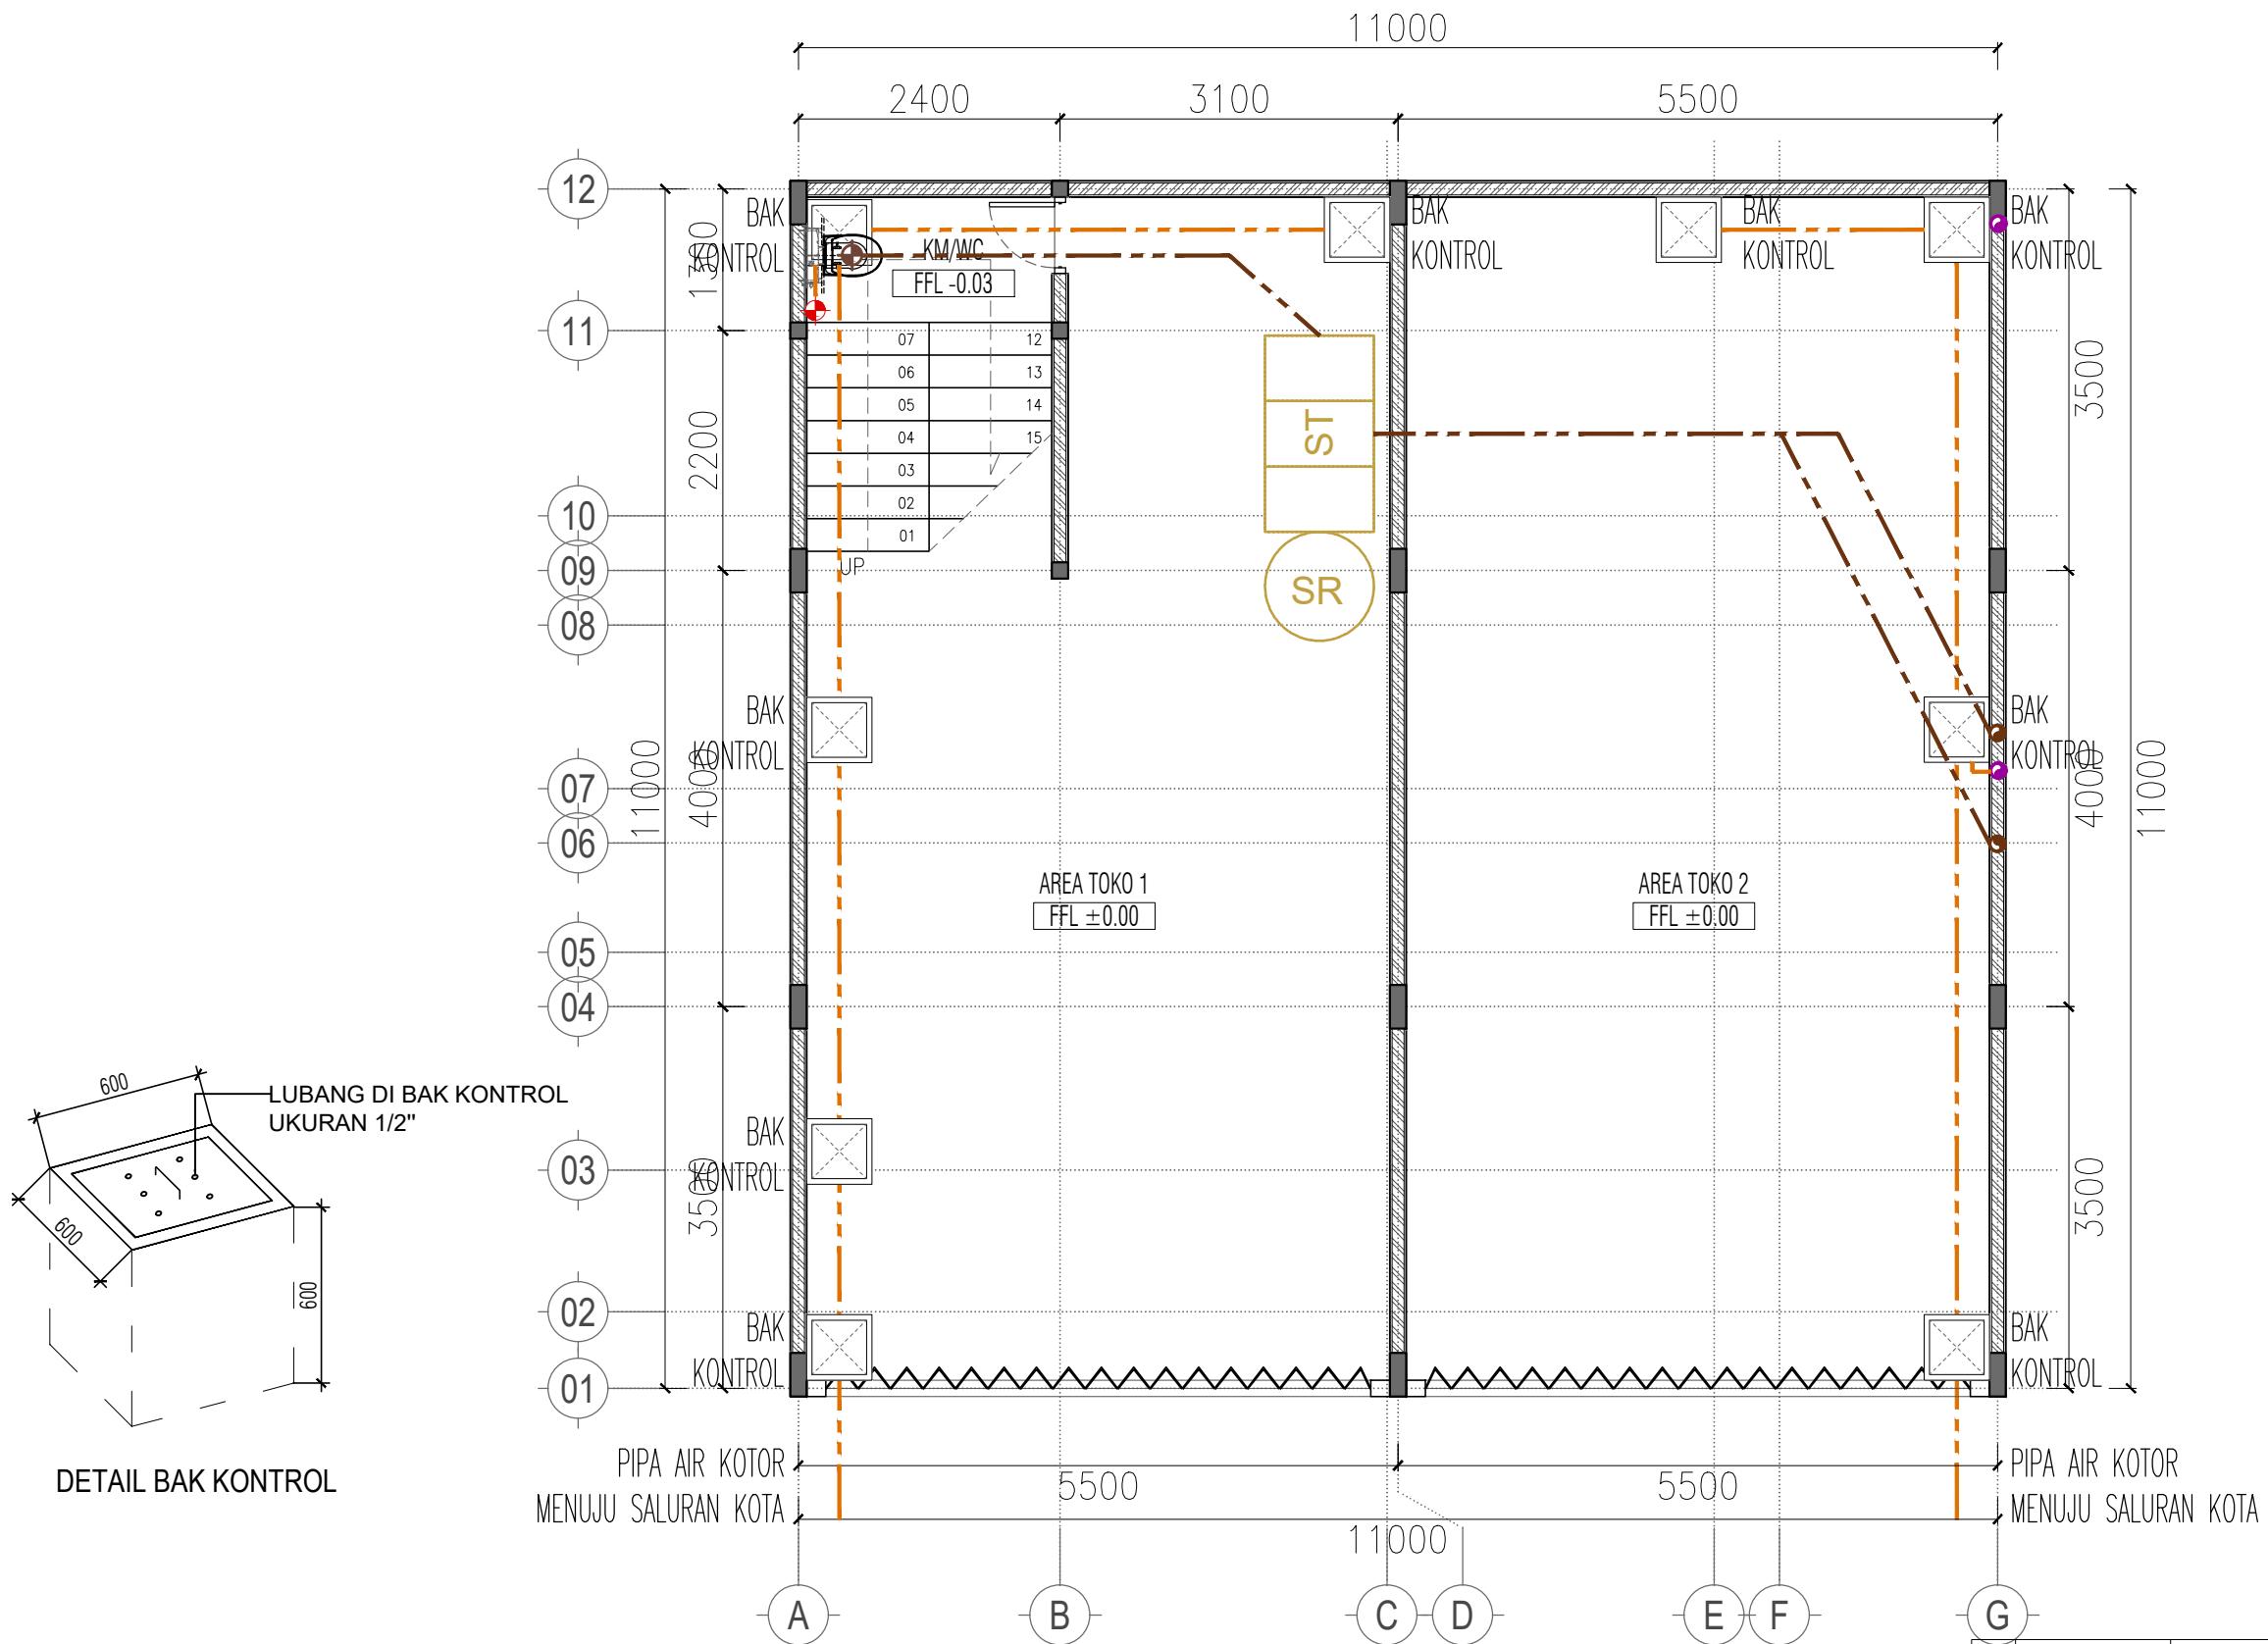


**DENAH INSTALASI AIR KOTOR DAN KOTORAN LT 1**


SKALA 1 : 100

NO	ITEM	KETERANGAN
1.	●	RISER PIPA KOTORAN 2,5"
2.	●	RISER PIPA AIR KOTOR 2,5"
3.	●	TITIK KLOSET
4.	●	AVOUR LANTAI 1,5"
5.	—	PIPA AIR HUJAN 2"
6.	—	PIPA AIR HUJAN 4"
7.	□	BAK KONTROL

NAMA PROYEK	RUMAH TINGGAL 2 LANTAI
LOKASI PROYEK	-
PENANGGUNG JAWAB	
DIGAMBAR	PELAKSANA
DISETUJUI	PEMILIK
CATATAN	<p>1. PELAKSANA ATAU SUBKON WAJIB MEMERIKSA KEMBALI KESESUAIN GAMBAR DENGAN KONDISI LAPANGAN</p>
JUDUL GAMBAR	SKALA
1. ARS	1 : 100
TANGGAL :	REVISI :
5 AGUSTUS 2024	R1
KODE GAMBAR	ARS-01-01
NO. LBR	JUMLAH LBR
00	00

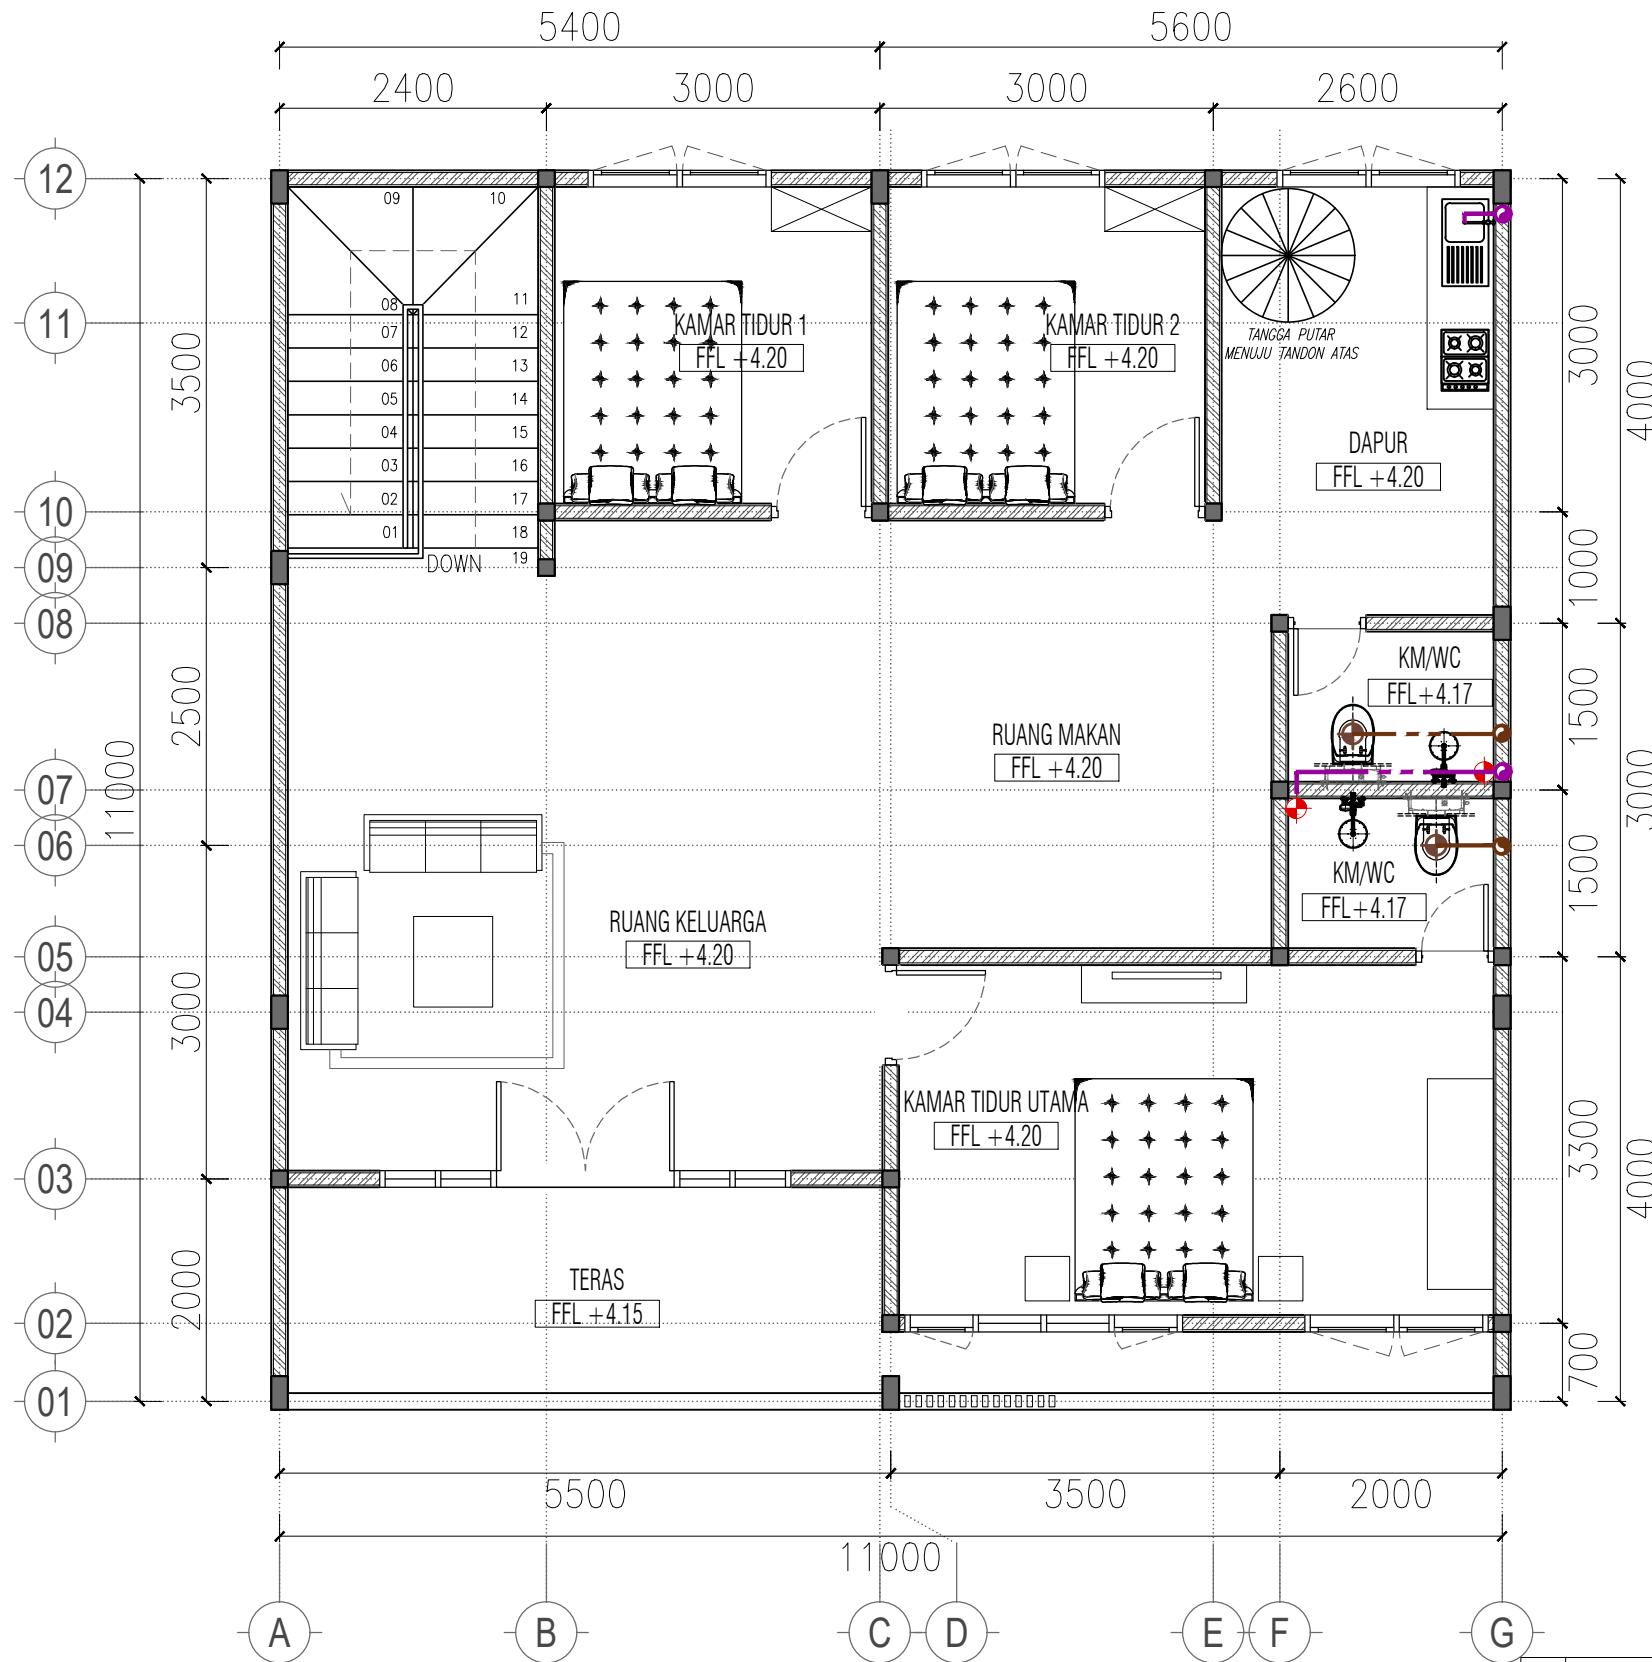



## DENAH INSTALASI AIR KOTOR DAN KOTORAN LT 2

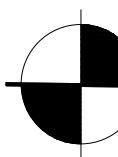



SKALA 1 : 100

NO	ITEM	KETERANGAN
1.	RISER PIPA KOTORAN 2,5"	RISER PIPA KOTORAN 2,5"
2.	RISER PIPA AIR KOTOR 2,5"	RISER PIPA AIR KOTOR 2,5"
3.	TITIK KLOSET	TITIK KLOSET
4.	AVOUR LANTAI 1,5"	AVOUR LANTAI 1,5"
5.	PIPA AIR HUJAN 2"	PIPA AIR HUJAN 2"
6.	PIPA AIR HUJAN 4"	PIPA AIR HUJAN 4"
7.	BAK KONTROL	BAK KONTROL

NAMA PROYEK	
<b>RUMAH TINGGAL 2 LANTAI</b>	
LOKASI PROYEK	
DIGAMBAR	PELAKSANA
DISETUJUI	PEMILIK
CATATAN	
1. PELAKSANA ATAU SUBKON WAJIB MEMERIKSA KEMBALI KESESUAIN GAMBAR DENGAN KONDISI LAPANGAN	
JUDUL GAMBAR	SKALA
1. ARS	1 : 100
TANGGAL :	REVISI :
5 AGUSTUS 2024	<b>R1</b>
KODE GAMBAR	
ARS-01-01	
NO. LBR	JUMLAH LBR
00	00

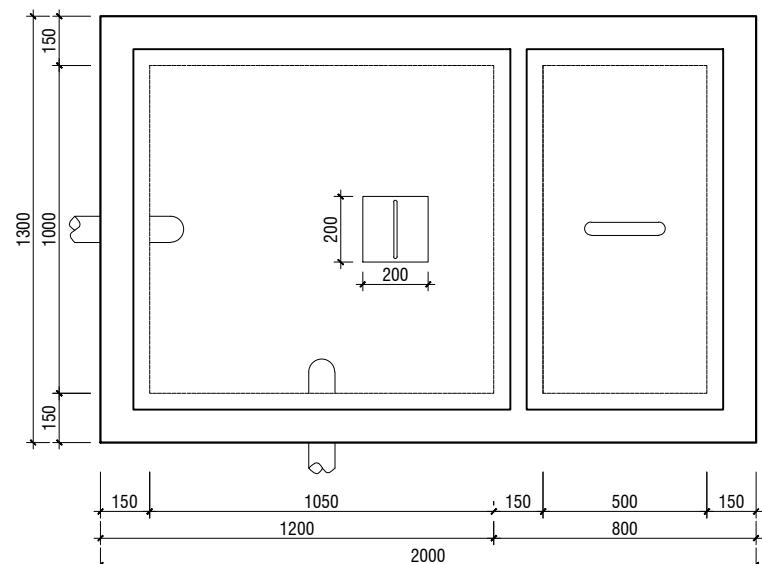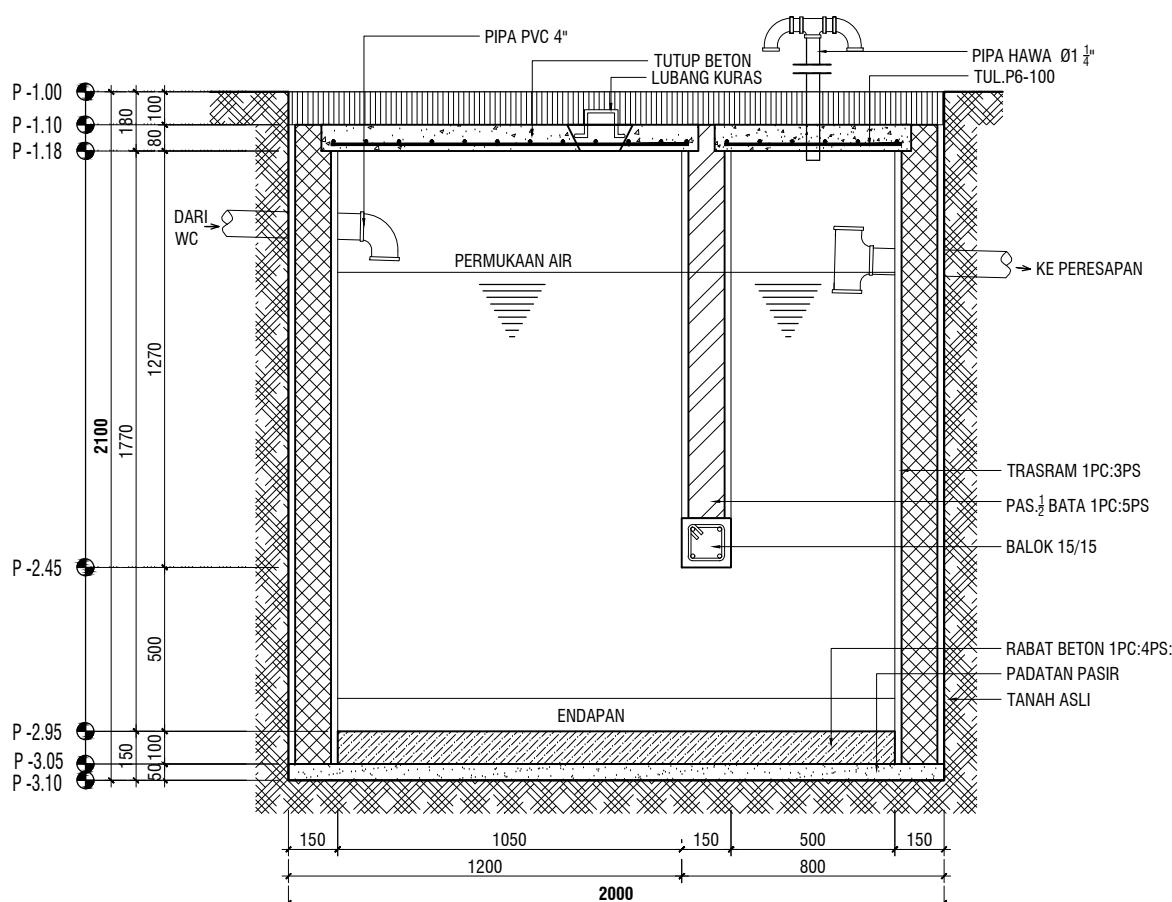


**DETAIL SEPTICTANK**  
SKALA 1 : 25

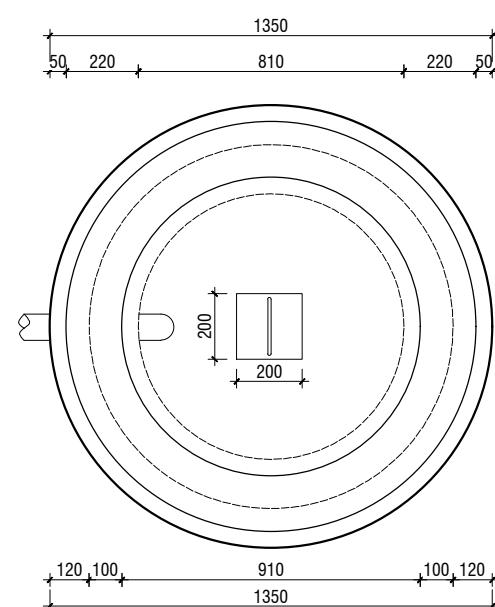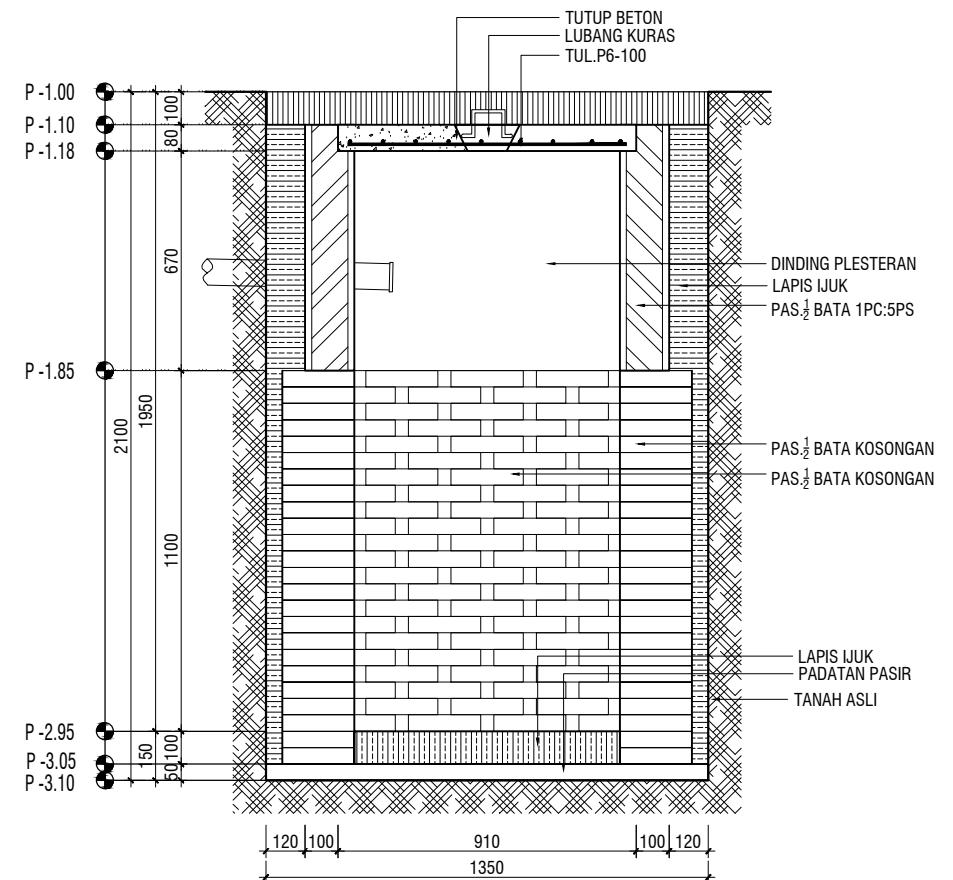

**DETAIL RESAPAN**  
SKALA 1 : 25

NAMA PROYEK	RUMAH TINGGAL 2 LANTAI
LOKASI PROYEK	-
PENANGGUNG JAWAB	-
DIGAMBAR	PELAKSANA
DISETUJUI	PEMILIK
CATATAN	<p>1. PELAKSANA ATAU SUBKON WAJIB MEMERIKSA KEMBALI KESESUAIN GAMBAR DENGAN KONDISI LAPANGAN</p>
JUDUL GAMBAR	SKALA
1. ARS	1 : 100
TANGGAL :	REVISI :
5 AGUSTUS 2024	R1
KODE GAMBAR	ARS-01-01
NO. LBR	JUMLAH LBR
00	00

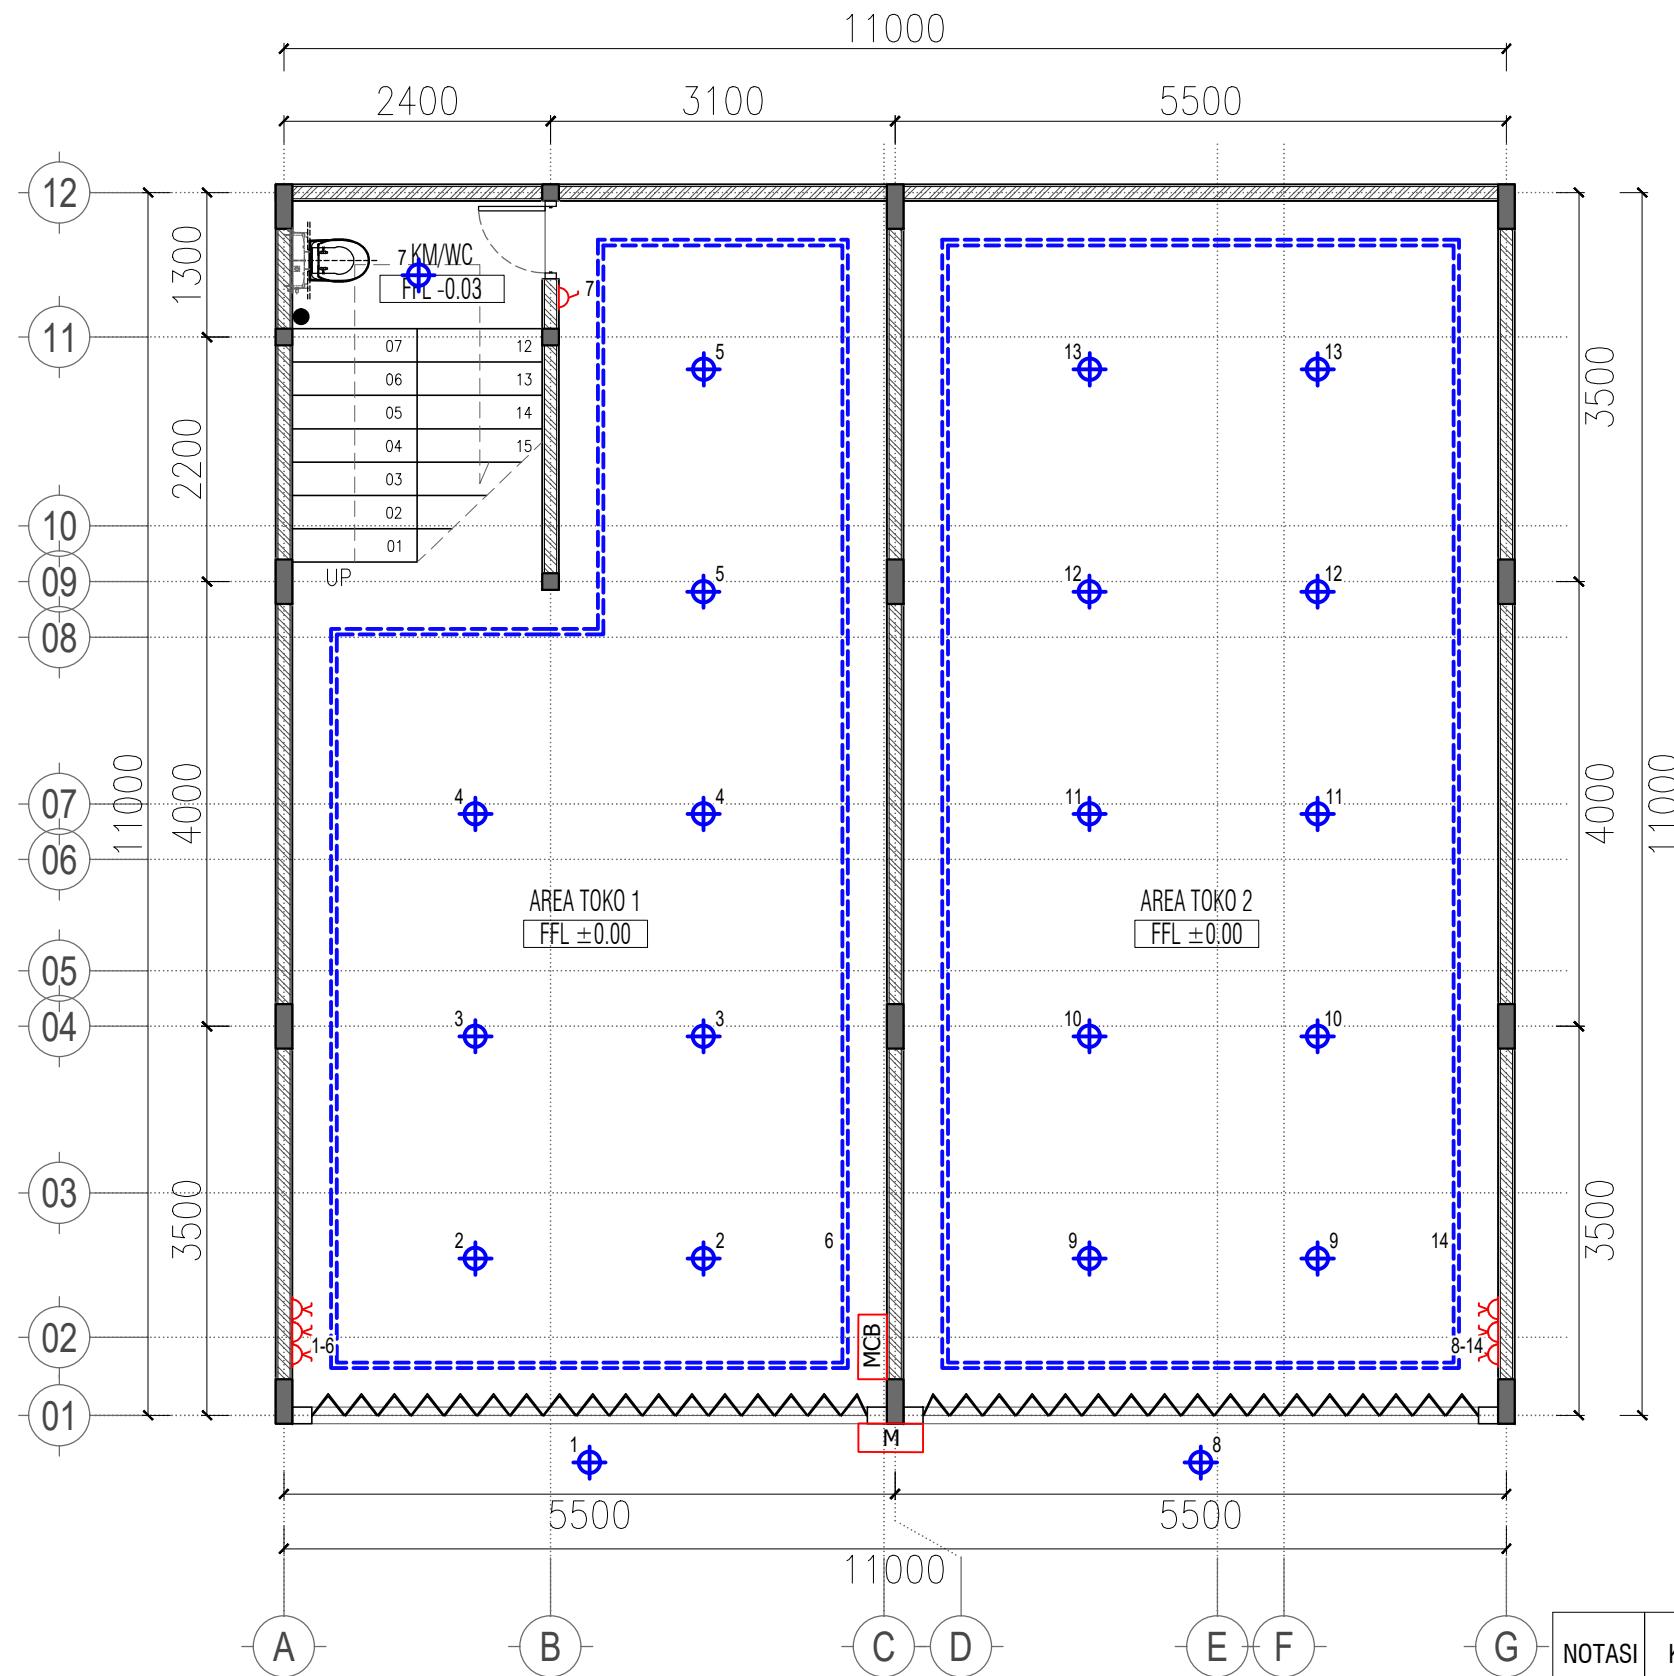


## DENAH INSTALASI TITIK LAMPU LT 1

SKALA 1 : 100

NAMA PROYEK	
<b>RUMAH TINGGAL 2 LANTAI</b>	
LOKASI PROYEK	
-	
-	
PENANGGUNG JAWAB	
<u>DIGAMBAR</u>	<u>PELAKSANA</u>
<u>DISETUJUI</u>	<u>PEMILIK</u>
CATATAN	
1. PELAKSANA ATAU SUBKON WAJIB MEMERIKSA KEMBALI KESESUAIN GAMBAR DENGAN KONDISI LAPANGAN	
JUDUL GAMBAR	
1. ARS	
SKALA	
1 : 100	
TANGGAL :	
5 AGUSTUS 2024	
REVISI :	
<b>R1</b>	
KODE GAMBAR	
ARS-01-01	
NO. LBR	JUMLAH LBR
00	00

NAMA PROYEK	
<b>RUMAH TINGGAL 2 LANTAI</b>	
LOKASI PROYEK	
-	-
PENANGGUNG JAWAB	
DIGAMBAR	PELAKSANA
DISETUJUI	PEMILIK
CATATAN	
1. PELAKSANA ATAU SUBKON WAJIB MEMERIKSA KEMBALI KESESUAIN GAMBAR DENGAN KONDISI LAPANGAN	
JUDUL GAMBAR	SKALA
1. ARS	1 : 100
TANGGAL :	REVISI :
5 AGUSTUS 2024	R1
KODE GAMBAR	
ARS-01-01	
NO. LBR	JUMLAH LBR
00	00

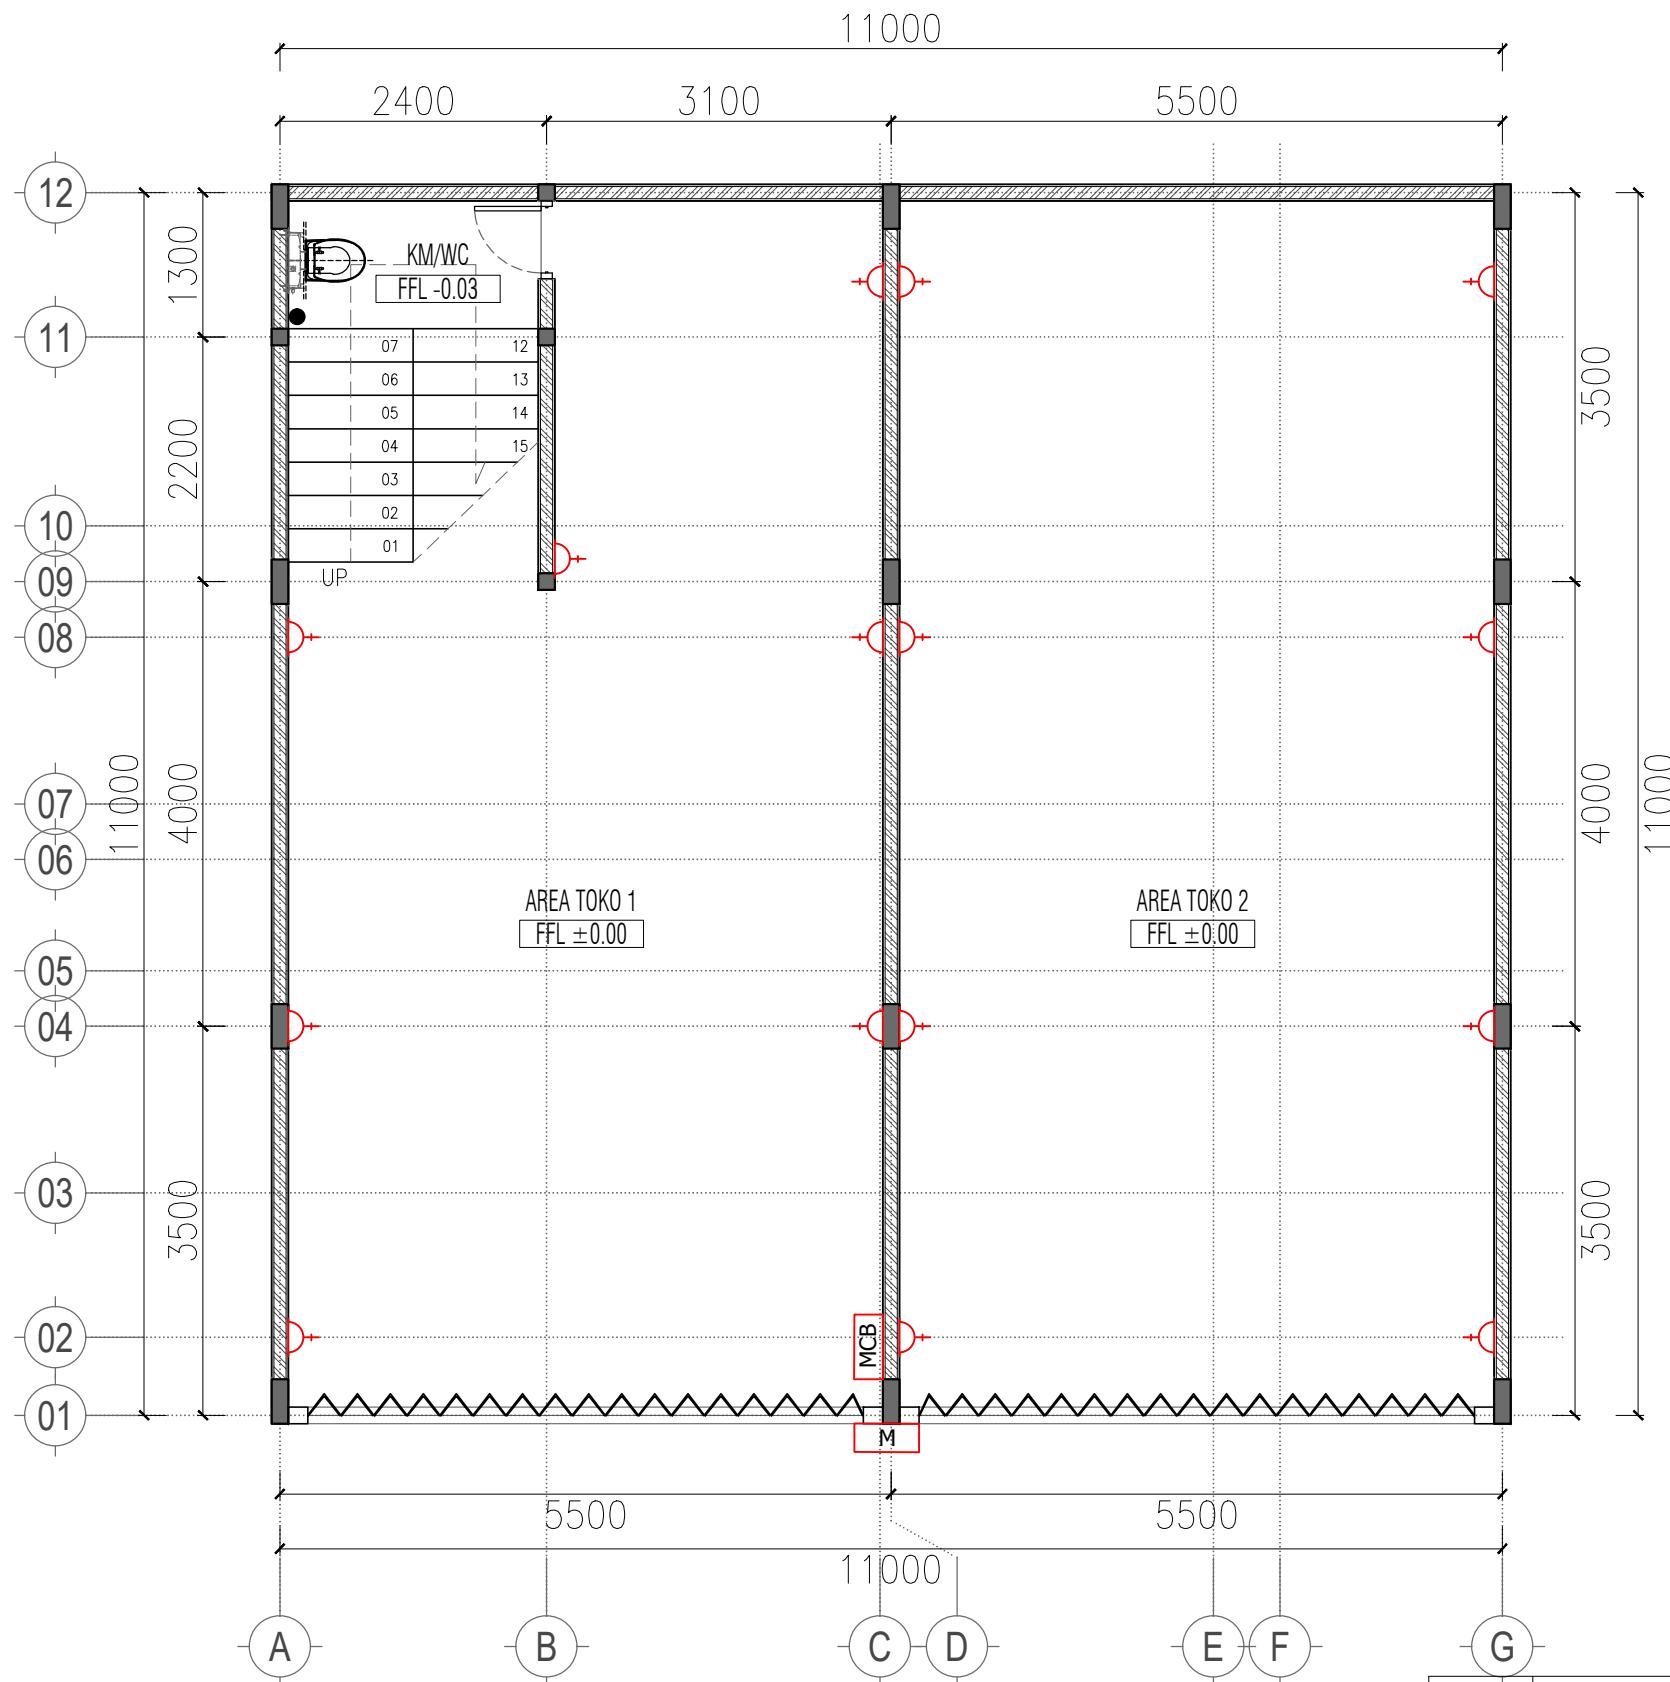


## DENAH INSTALASI STOP KONTAK LT 1



SKALA 1 : 100

NOTASI	KETERANGAN	JUMLAH	TINGGI DARI LANTAI
STOP KONTAK DINDING	15	30 CM	
STOP KONTAK AC	-	300 CM	
METERAN LISTRIK	1	200 CM	
MCB	1	200 CM	

NAMA PROYEK	RUMAH TINGGAL 2 LANTAI
LOKASI PROYEK	-
PENANGGUNG JAWAB	-
DIGAMBAR	PELAKSANA
DISETUJUI	PEMILIK
CATATAN	<p>1. PELAKSANA ATAU SUBKON WAJIB MEMERIKSA KEMBALI KESESUAIN GAMBAR DENGAN KONDISI LAPANGAN</p>
JUDUL GAMBAR	SKALA
1. ARS	1 : 100
TANGGAL :	REVISI :
5 AGUSTUS 2024	R1
KODE GAMBAR	
ARS-01-01	
NO. LBR	JUMLAH LBR
00	00

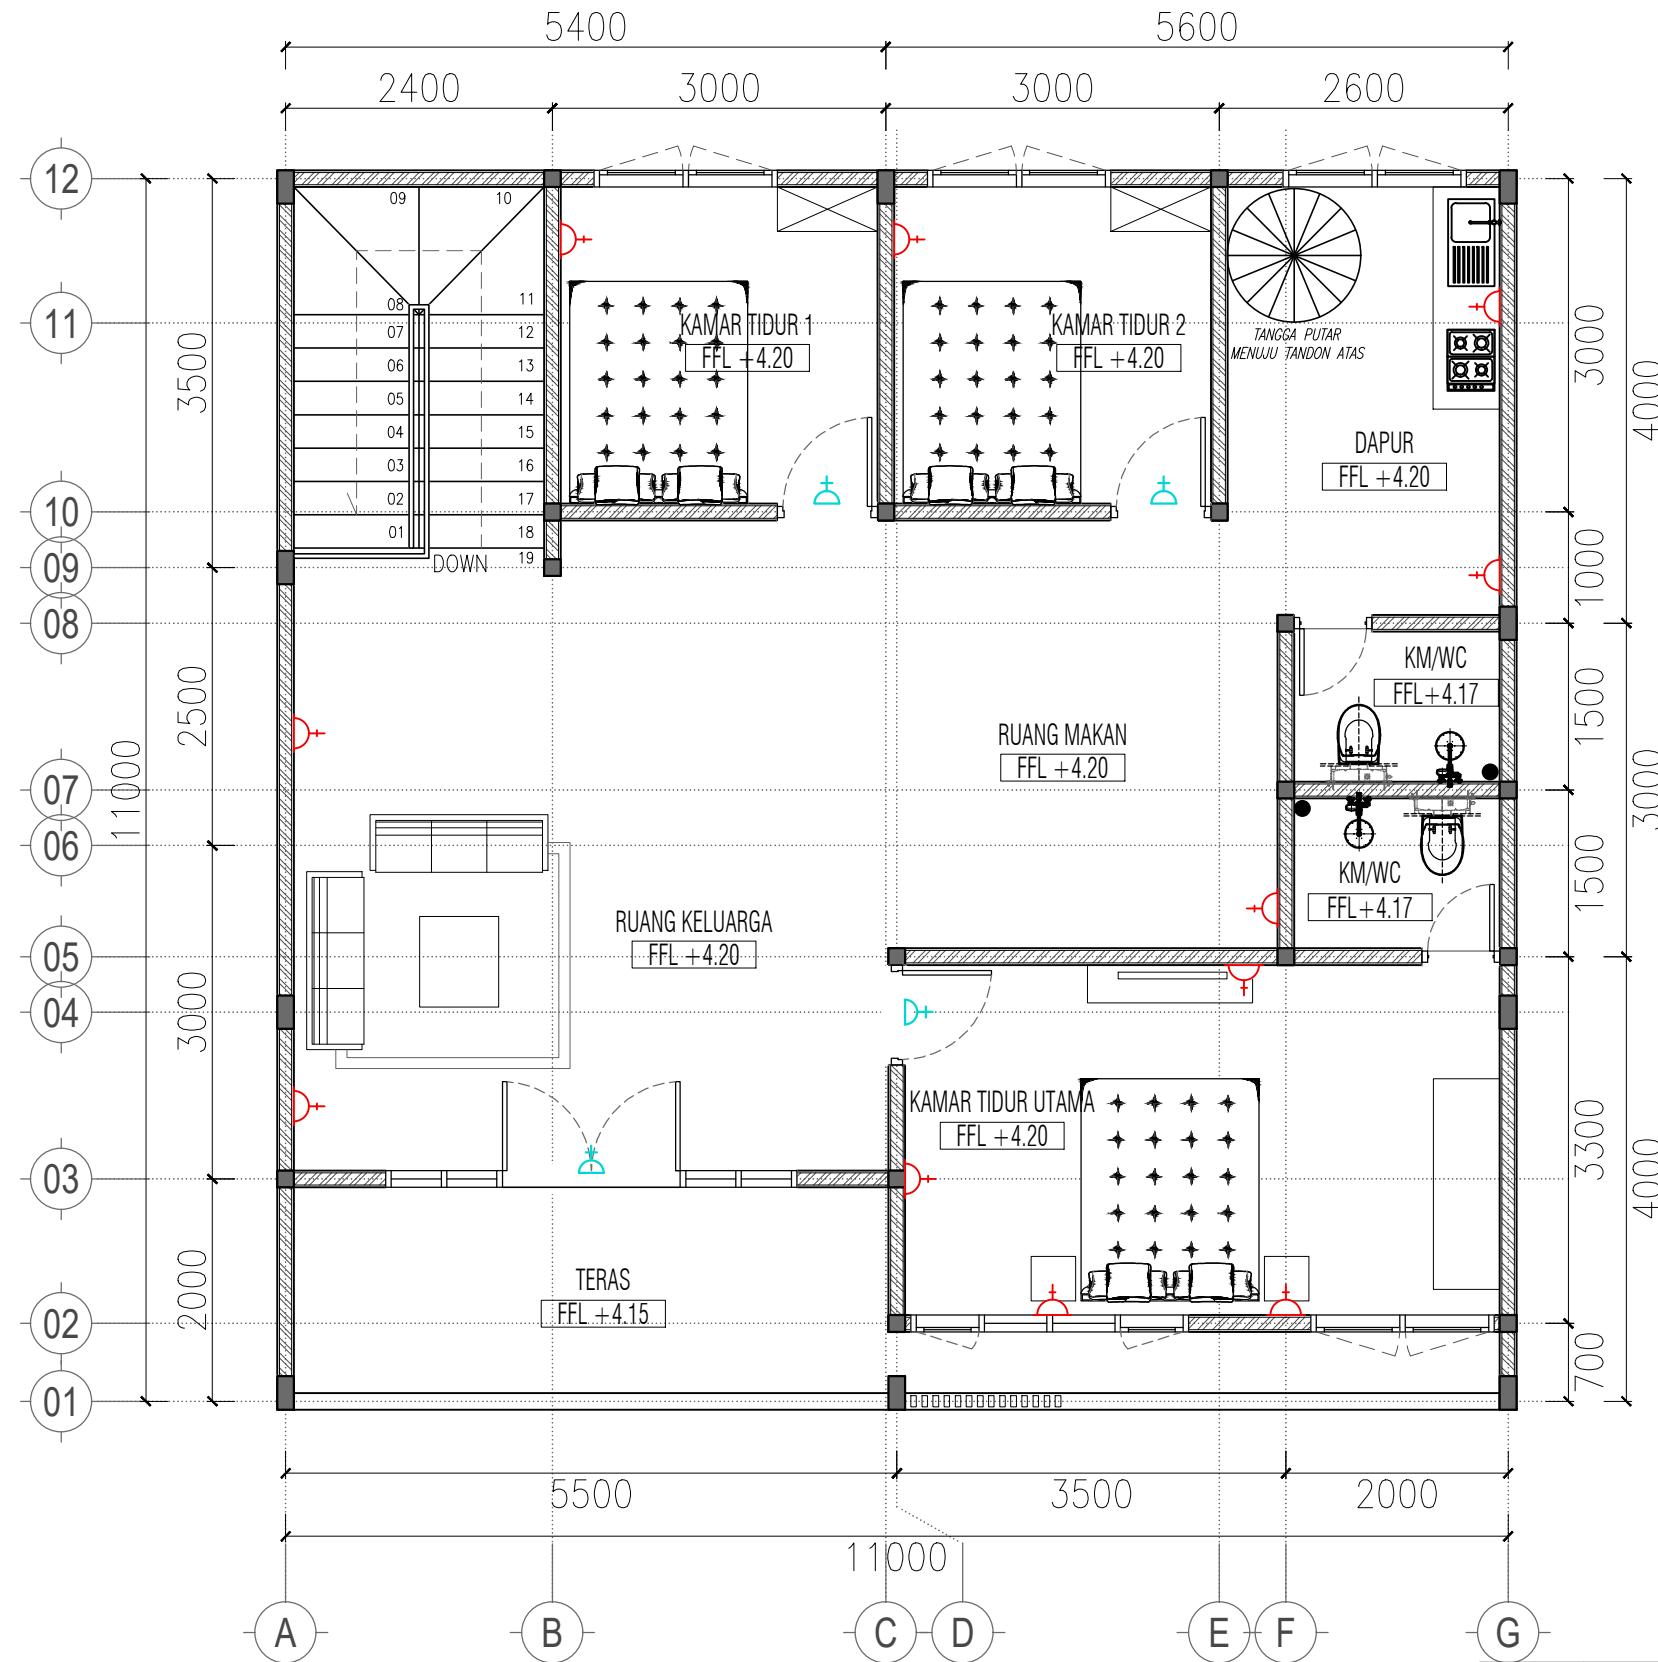


## DENAH INSTALASI STOP KONTAK LT 2

SKALA 1 : 100

NOTASI	KETERANGAN	JUMLAH	TINGGI DARI LANTAI
STOP KONTAK DINDING	STOP KONTAK DINDING	11	30 CM
STOP KONTAK AC	STOP KONTAK AC	4	300 CM
M	METERAN LISTRIK	-	200 CM
MCB	MCB	-	200 CM


NAMA PROYEK	RUMAH TINGGAL 2 LANTAI	
LOKASI PROYEK	-	
PENANGGUNG JAWAB	-	
DIGAMBAR	PELAKSANA	
DISETUJUI	PEMILIK	
CATATAN	<p>1. PELAKSANA ATAU SUBKON WAJIB MEMERIKSA KEMBALI KESESUAIN GAMBAR DENGAN KONDISI LAPANGAN</p>	
JUDUL GAMBAR	SKALA	
1. ARS	1 : 100	
TANGGAL :	REVISI :	
5 AGUSTUS 2024	R1	
KODE GAMBAR	ARS-01-01	
NO. LBR	JUMLAH LBR	
00	00	

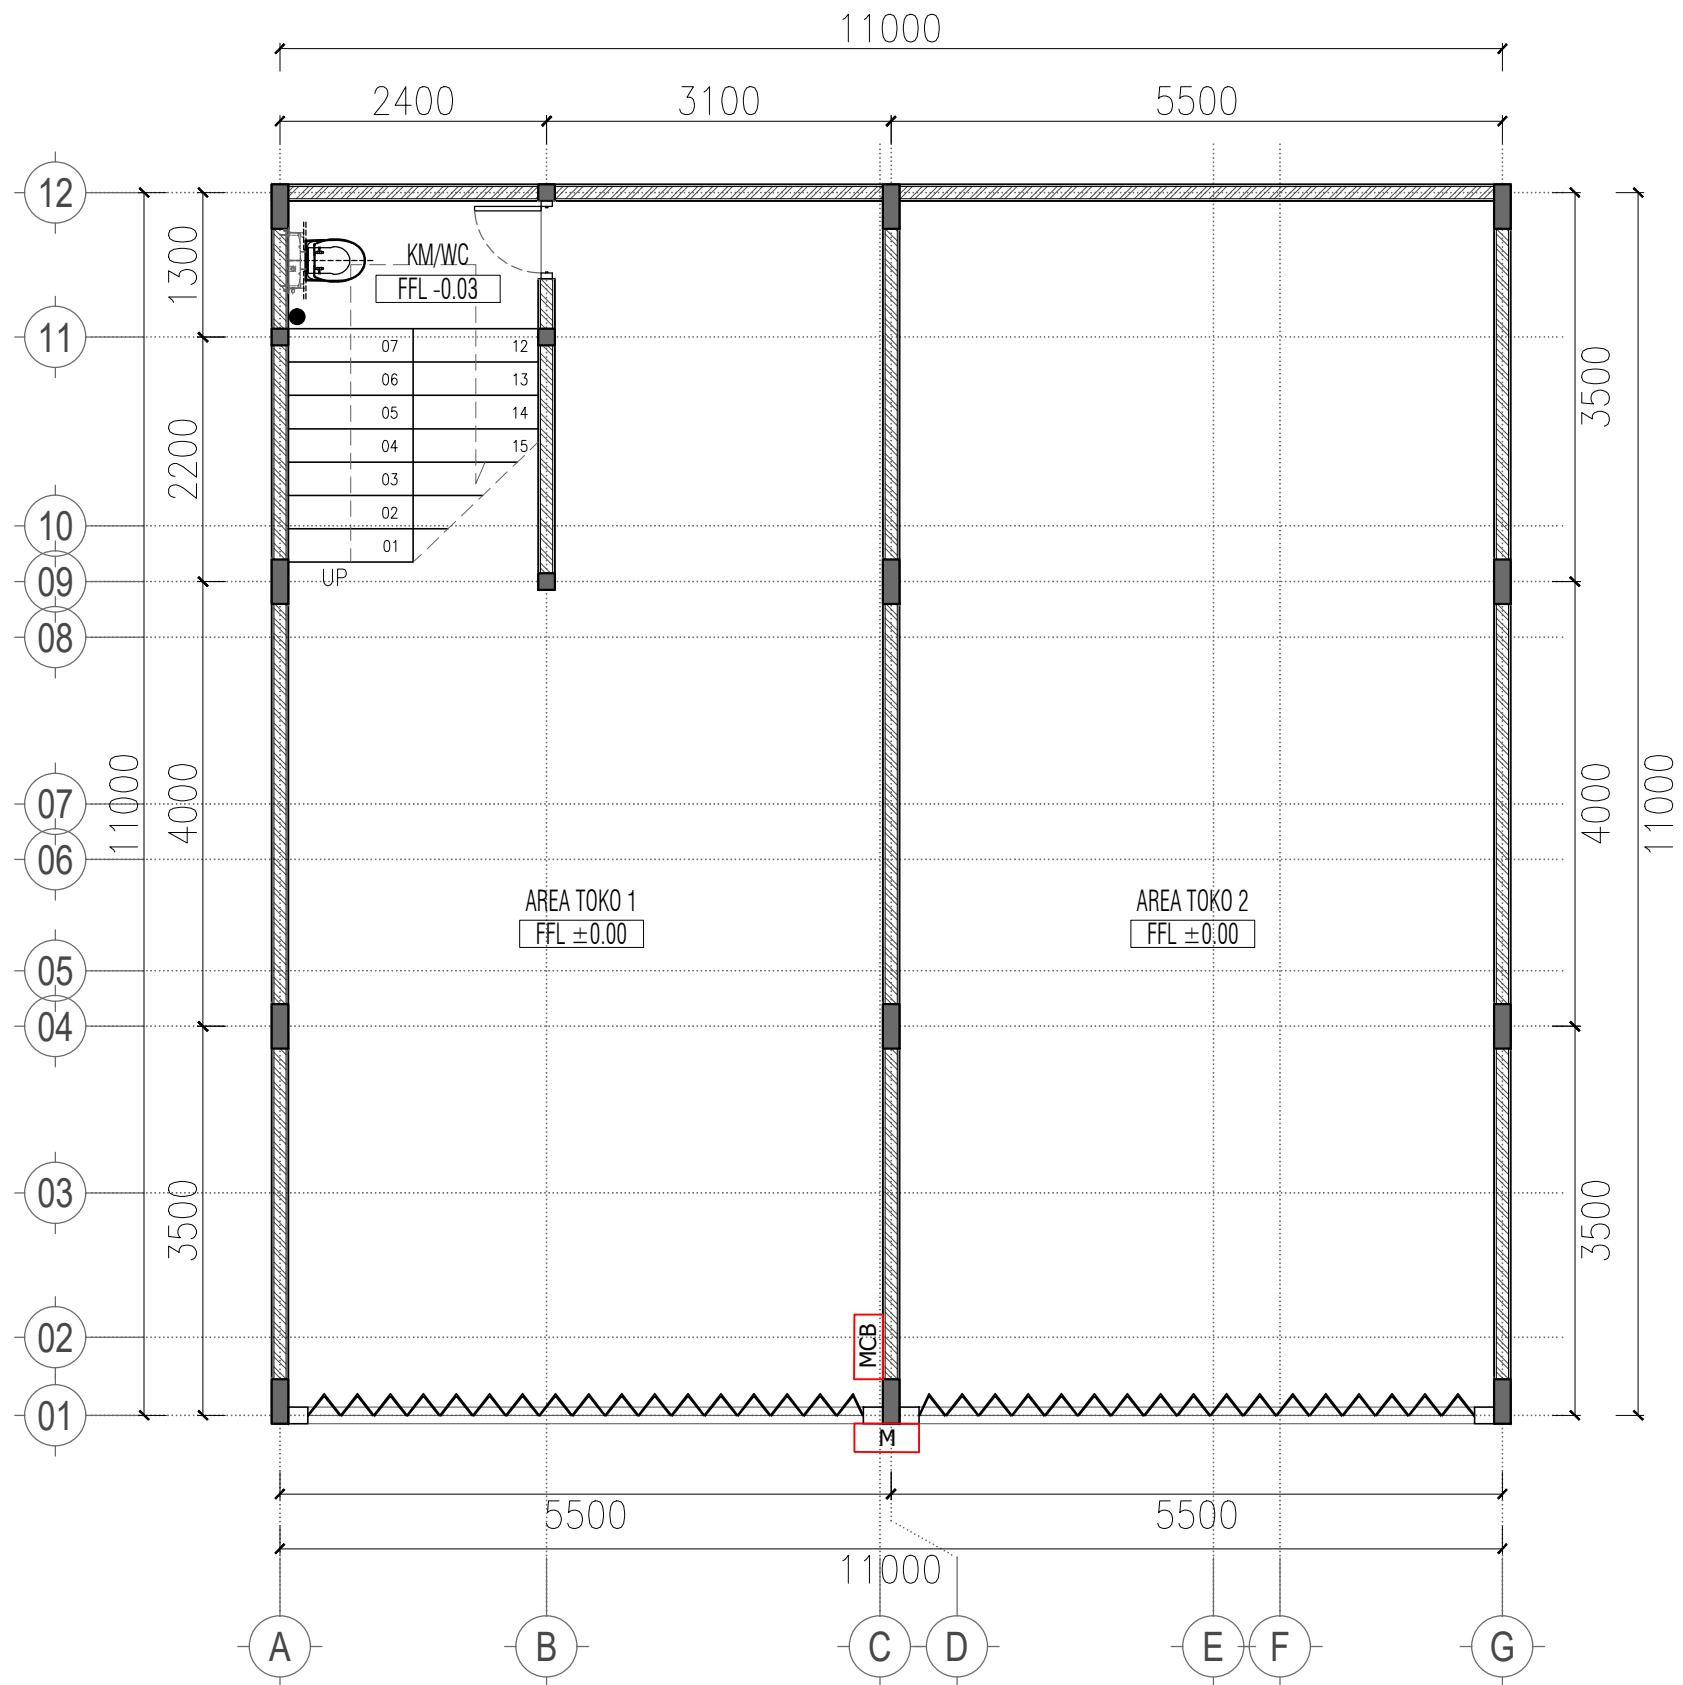

## DENAH INSTALASI AC LT 1


SKALA 1 : 100

NAMA PROYEK	RUMAH TINGGAL 2 LANTAI	
LOKASI PROYEK	-	
PENANGGUNG JAWAB	-	
DIGAMBAR	PELAKSANA	
DISETUJUI	PEMILIK	
CATATAN	<p>1. PELAKSANA ATAU SUBKON WAJIB MEMERIKSA KEMBALI KESESUAIN GAMBAR DENGAN KONDISI LAPANGAN</p>	
JUDUL GAMBAR	SKALA	
1. ARS	1 : 100	
TANGGAL :	REVISI :	
5 AGUSTUS 2024	R1	
KODE GAMBAR	ARS-01-01	
NO. LBR	JUMLAH LBR	
00	00	

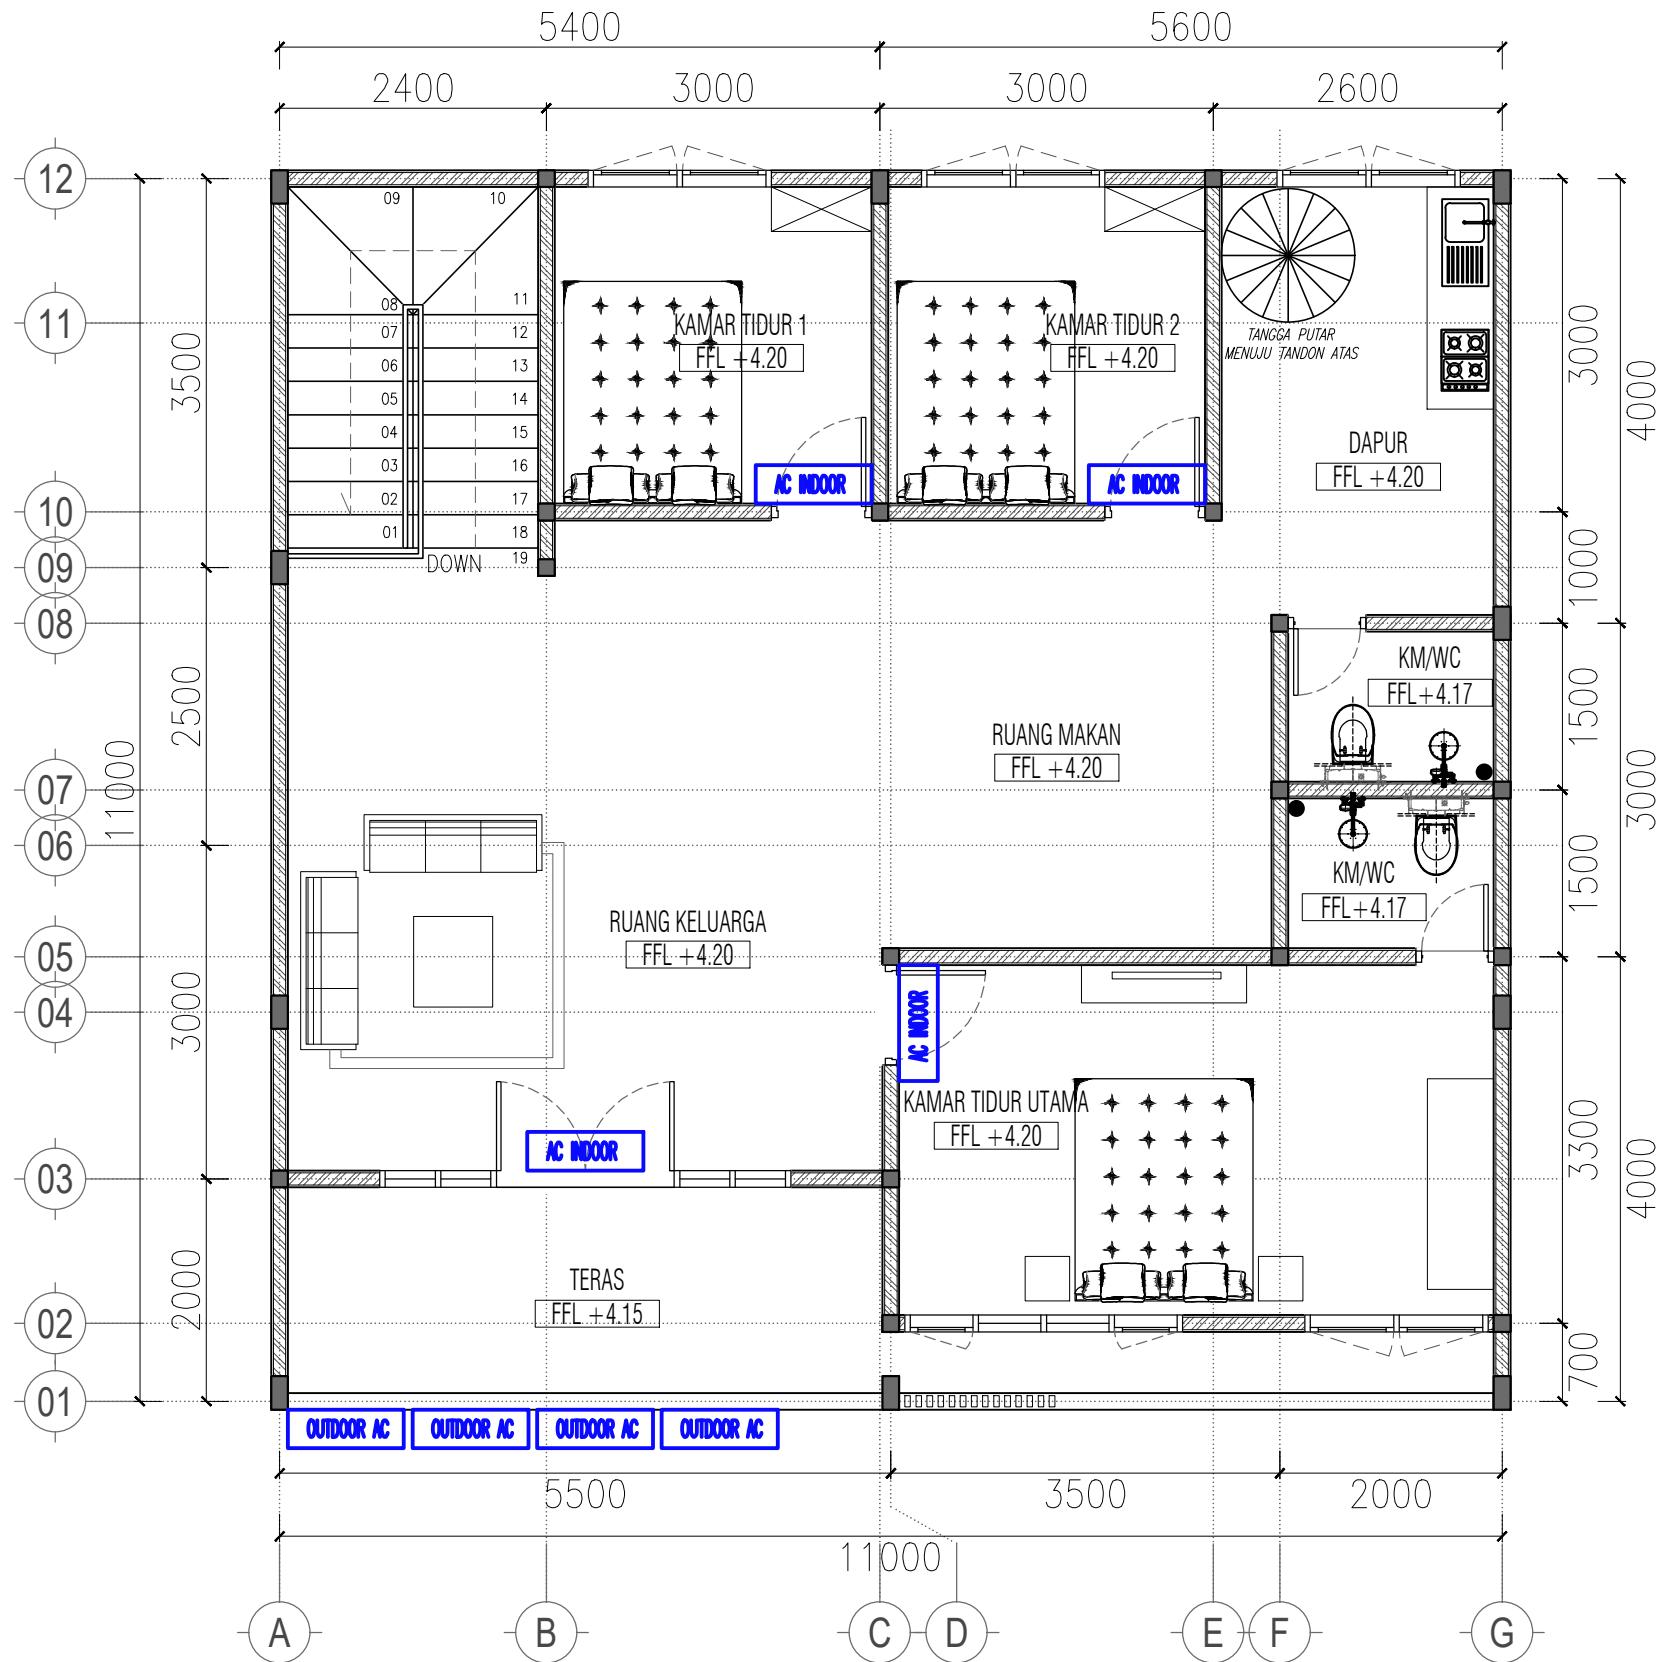

**DENAH INSTALASI AC LT 2**  
SKALA 1 : 100

NAMA PROYEK	
<b>RUMAH TINGGAL 2 LANTAI</b>	
LOKASI PROYEK	
-	-
PENANGGUNG JAWAB	
DIGAMBAR	PELAKSANA
DISETUJUI	PEMILIK
CATATAN	
1. PELAKSANA ATAU SUBKON WAJIB MEMERIKSA KEMBALI KESESUAIN GAMBAR DENGAN KONDISI LAPANGAN	
JUDUL GAMBAR	SKALA
1. ARS	1 : 100
TANGGAL :	REVISI :
5 AGUSTUS 2024	<b>R1</b>
KODE GAMBAR	
ARS-01-01	
NO. LBR	JUMLAH LBR
00	00

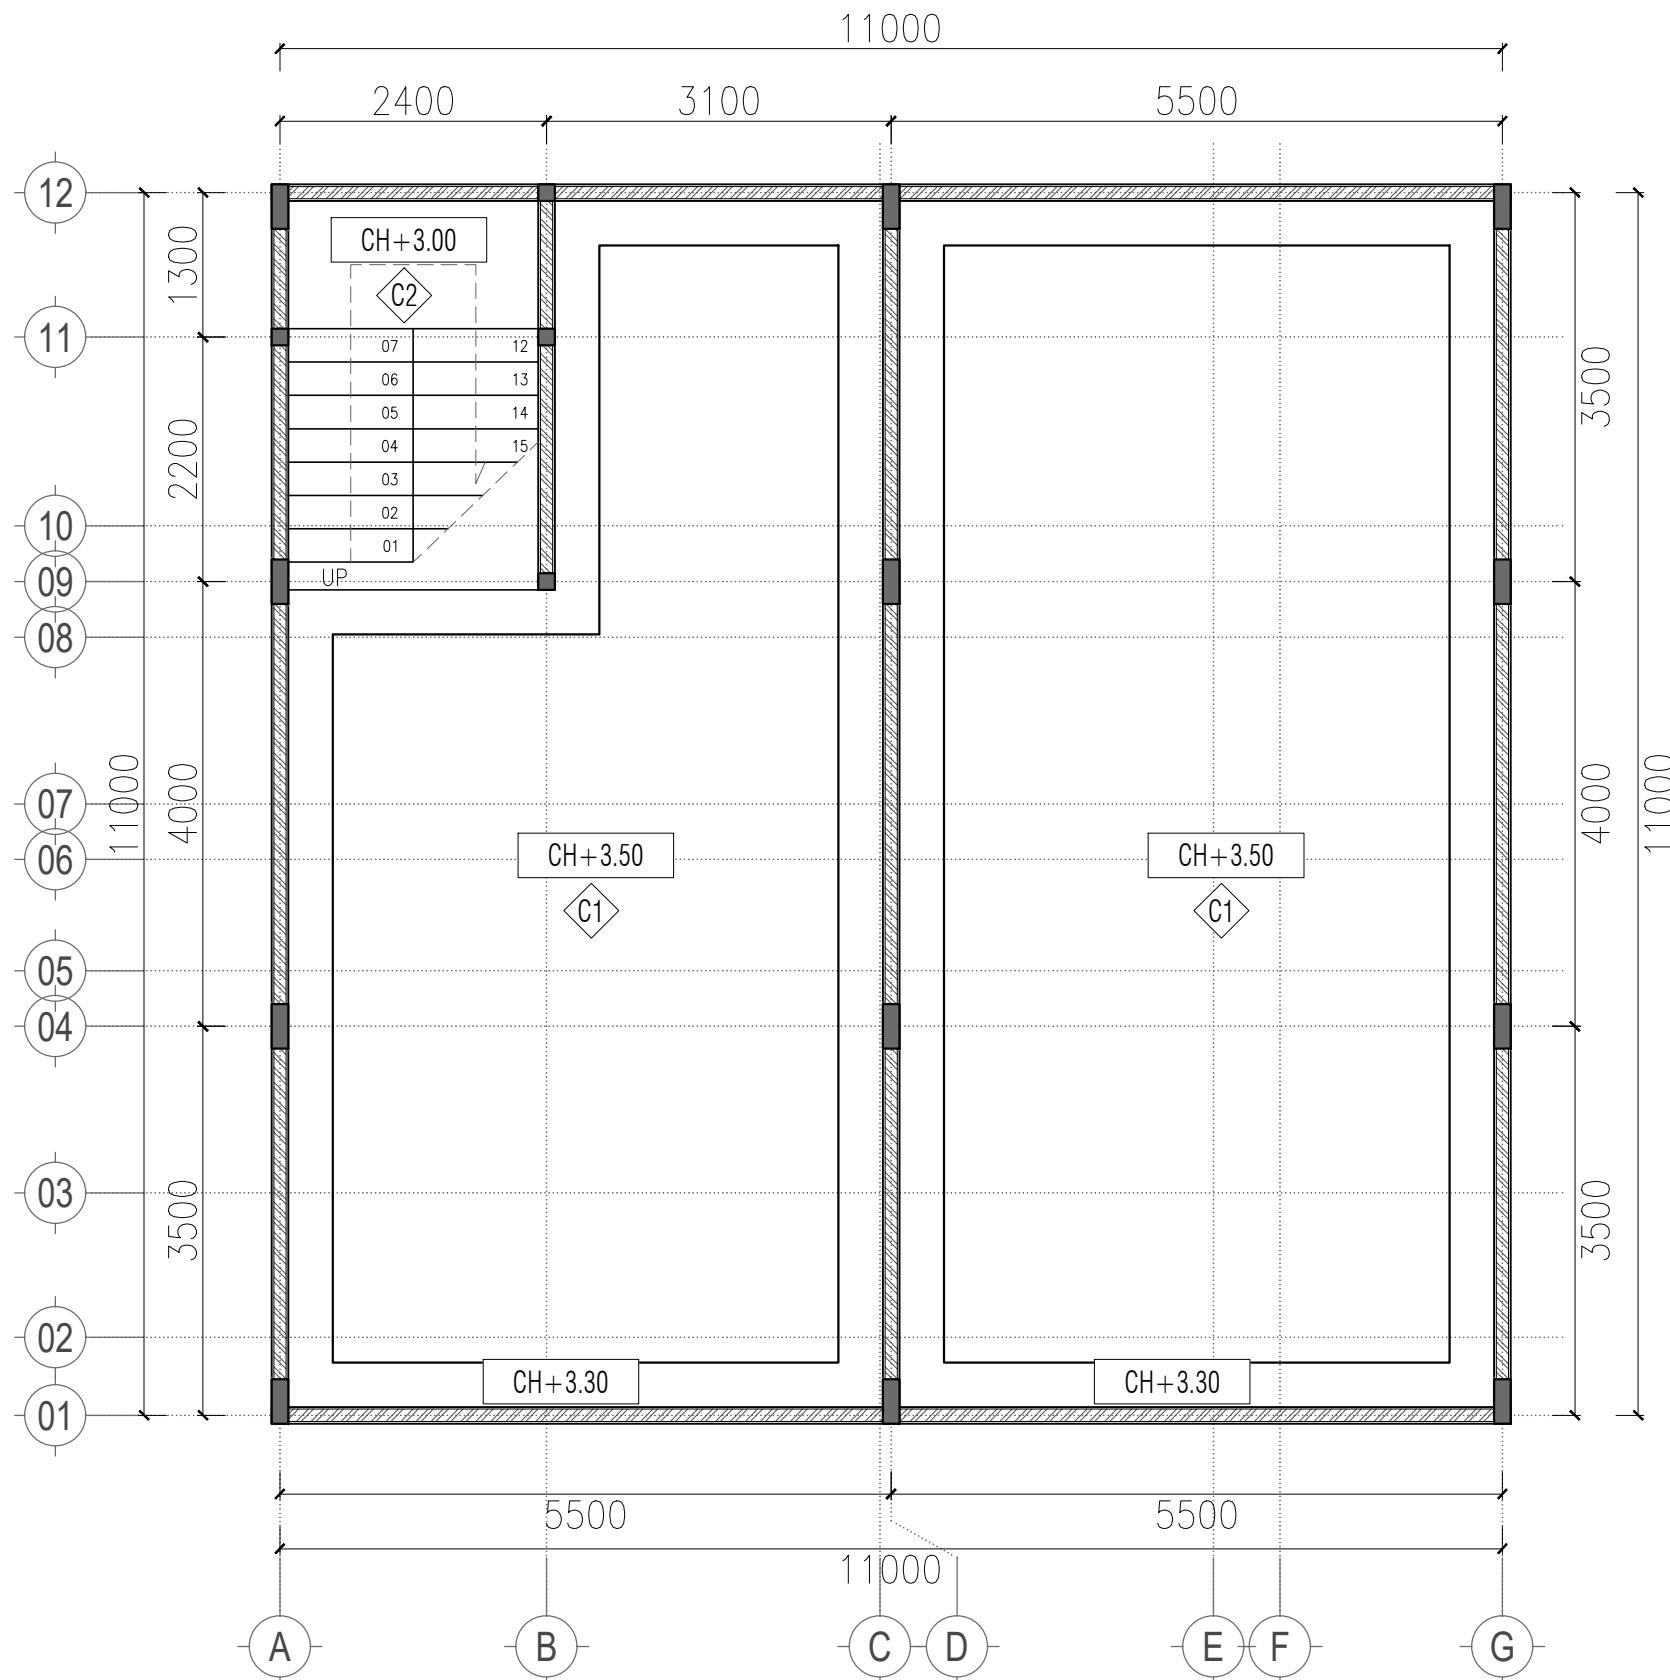


## DENAH RENCANA PLAFOND LT 1

SKALA 1 : 100

SYMBOL	SPECIFICATION
	PLAFOND GYPSUM 9MM, RANGKA HOLLOW 4x4, 2x4
	PLAFOND GYPSUM WR 9MM, RANGKA HOLLOW 4x4, 2x4

NAMA PROYEK	
<b>RUMAH TINGGAL 2 LANTAI</b>	
LOKASI PROYEK	
-	-
PENANGGUNG JAWAB	
DIGAMBAR	PELAKSANA
DISETUJUI	PEMILIK
CATATAN	
1. PELAKSANA ATAU SUBKON WAJIB MEMERIKSA KEMBALI KESESUAIN GAMBAR DENGAN KONDISI LAPANGAN	
JUDUL GAMBAR	SKALA
1. ARS	1 : 100
TANGGAL :	REVISI :
5 AGUSTUS 2024	<b>R1</b>
KODE GAMBAR	
ARS-01-01	
NO. LBR	JUMLAH LBR
00	00

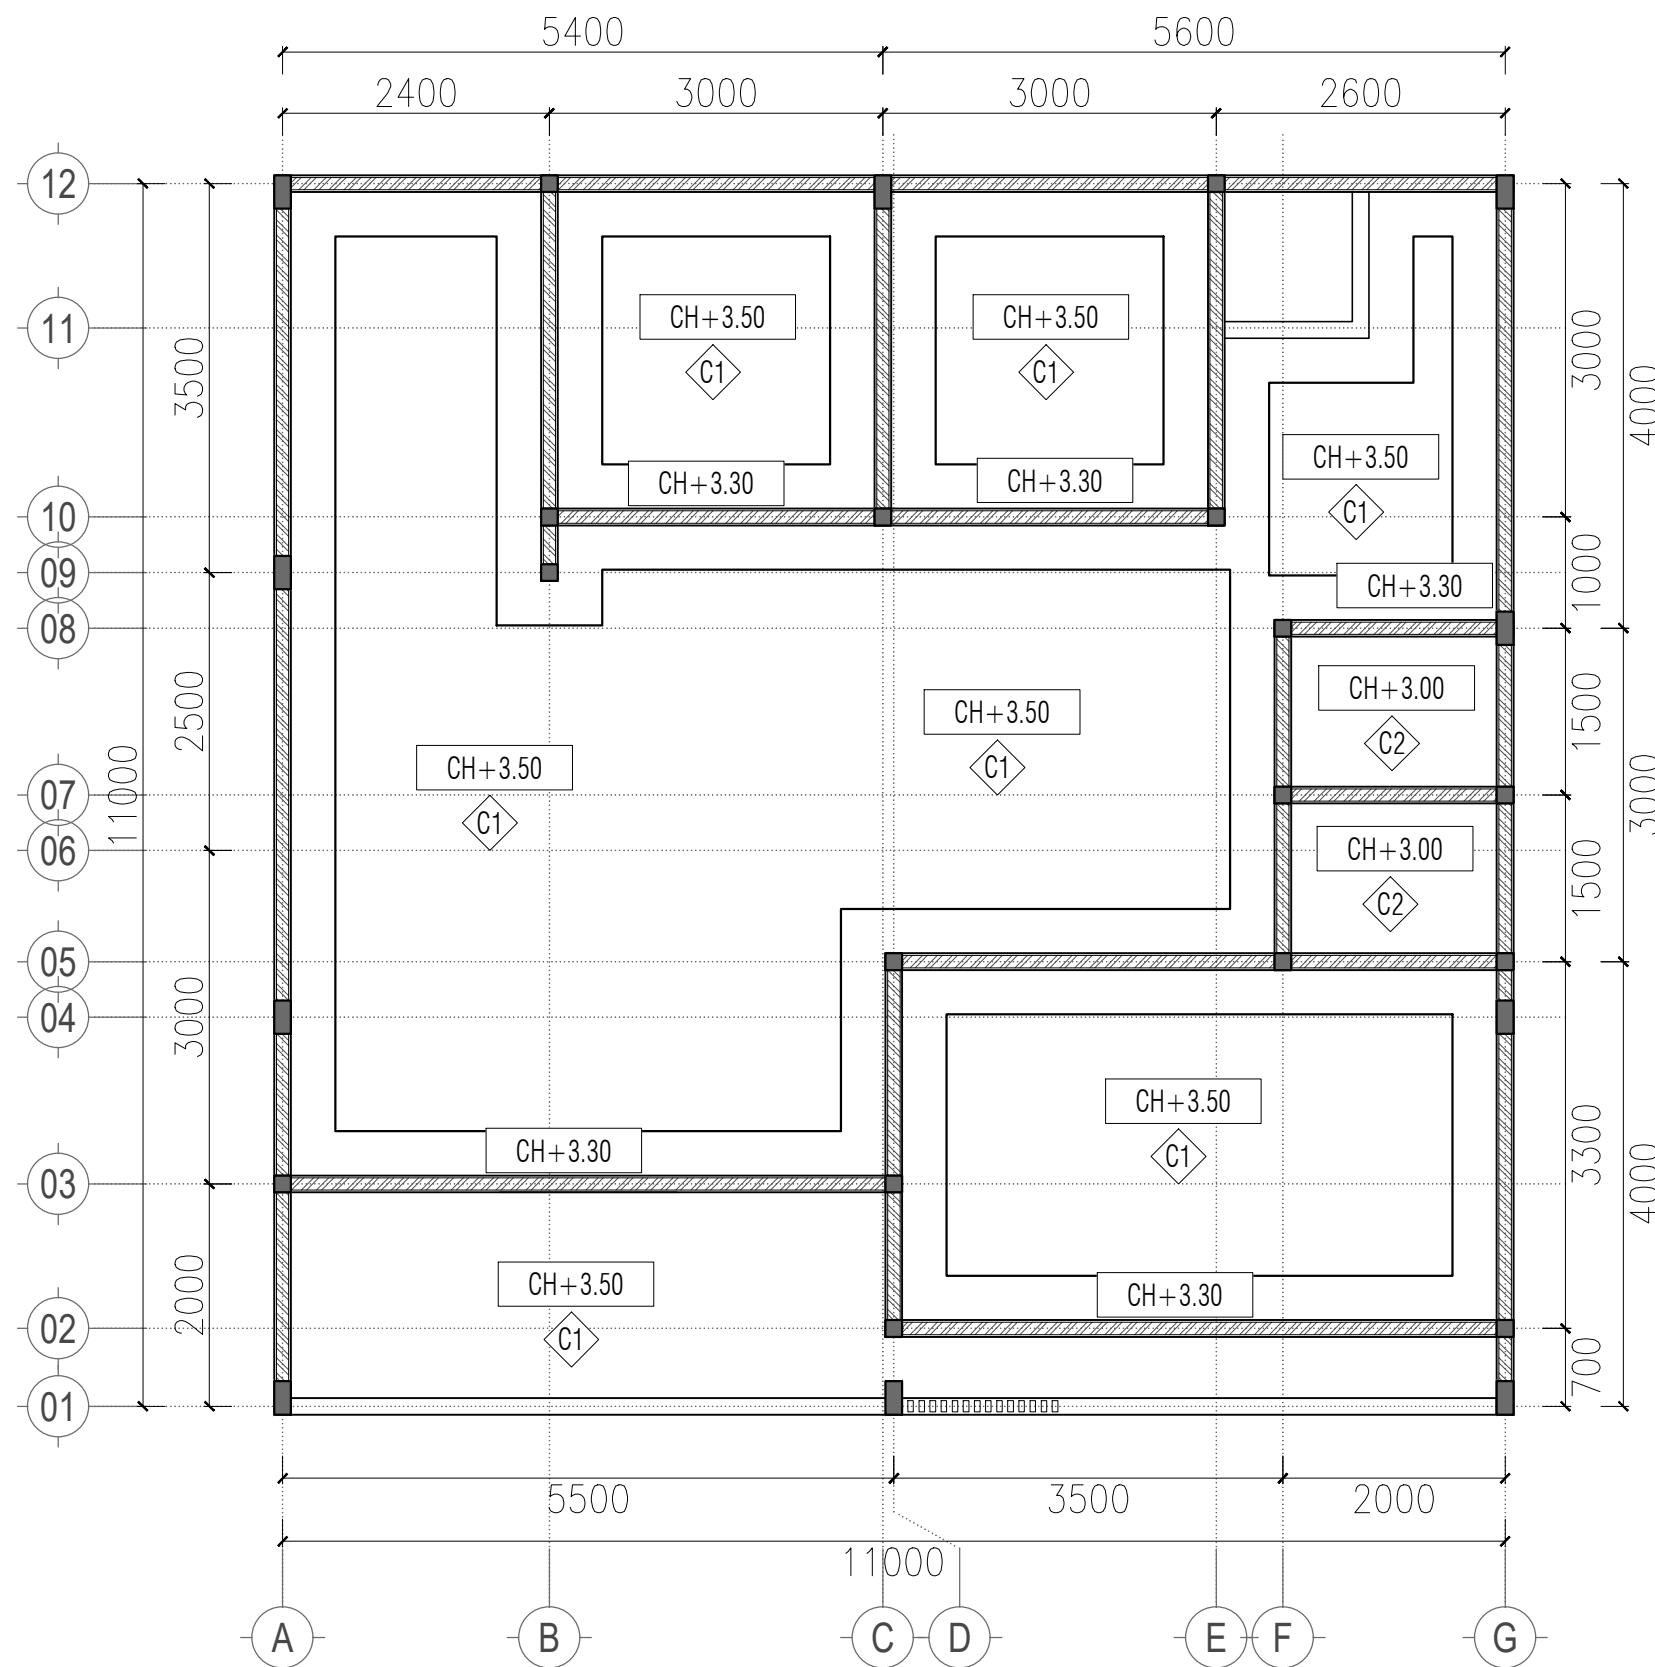


## DENAH RENCANA PLAFOND LT 2


SKALA 1 : 100

SYMBOL	SPECIFICATION
	PLAFOND GYPSUM 9MM, RANGKA HOLLOW 4x4, 2x4
	PLAFOND GYPSUM WR 9MM, RANGKA HOLLOW 4x4, 2x4

NAMA PROYEK	
<b>RUMAH TINGGAL 2 LANTAI</b>	
LOKASI PROYEK	
-	-
PENANGGUNG JAWAB	
DIGAMBAR	PELAKSANA
DISETUJU	PEMILIK
CATATAN	
1. PELAKSANA ATAU SUBKON WAJIB MEMERIKSA KEMBALI KESESUAIN GAMBAR DENGAN KONDISI LAPANGAN	
JUDUL GAMBAR	SKALA
1.DETAIL 3D RANGKA PLAFOND	NTS
TANGGAL :	REVISI :
5 AGUSTUS 2024	<b>R1</b>
KODE GAMBAR	
ARS-01-01	
NO. LBR	JUMLAH LBR
00	00

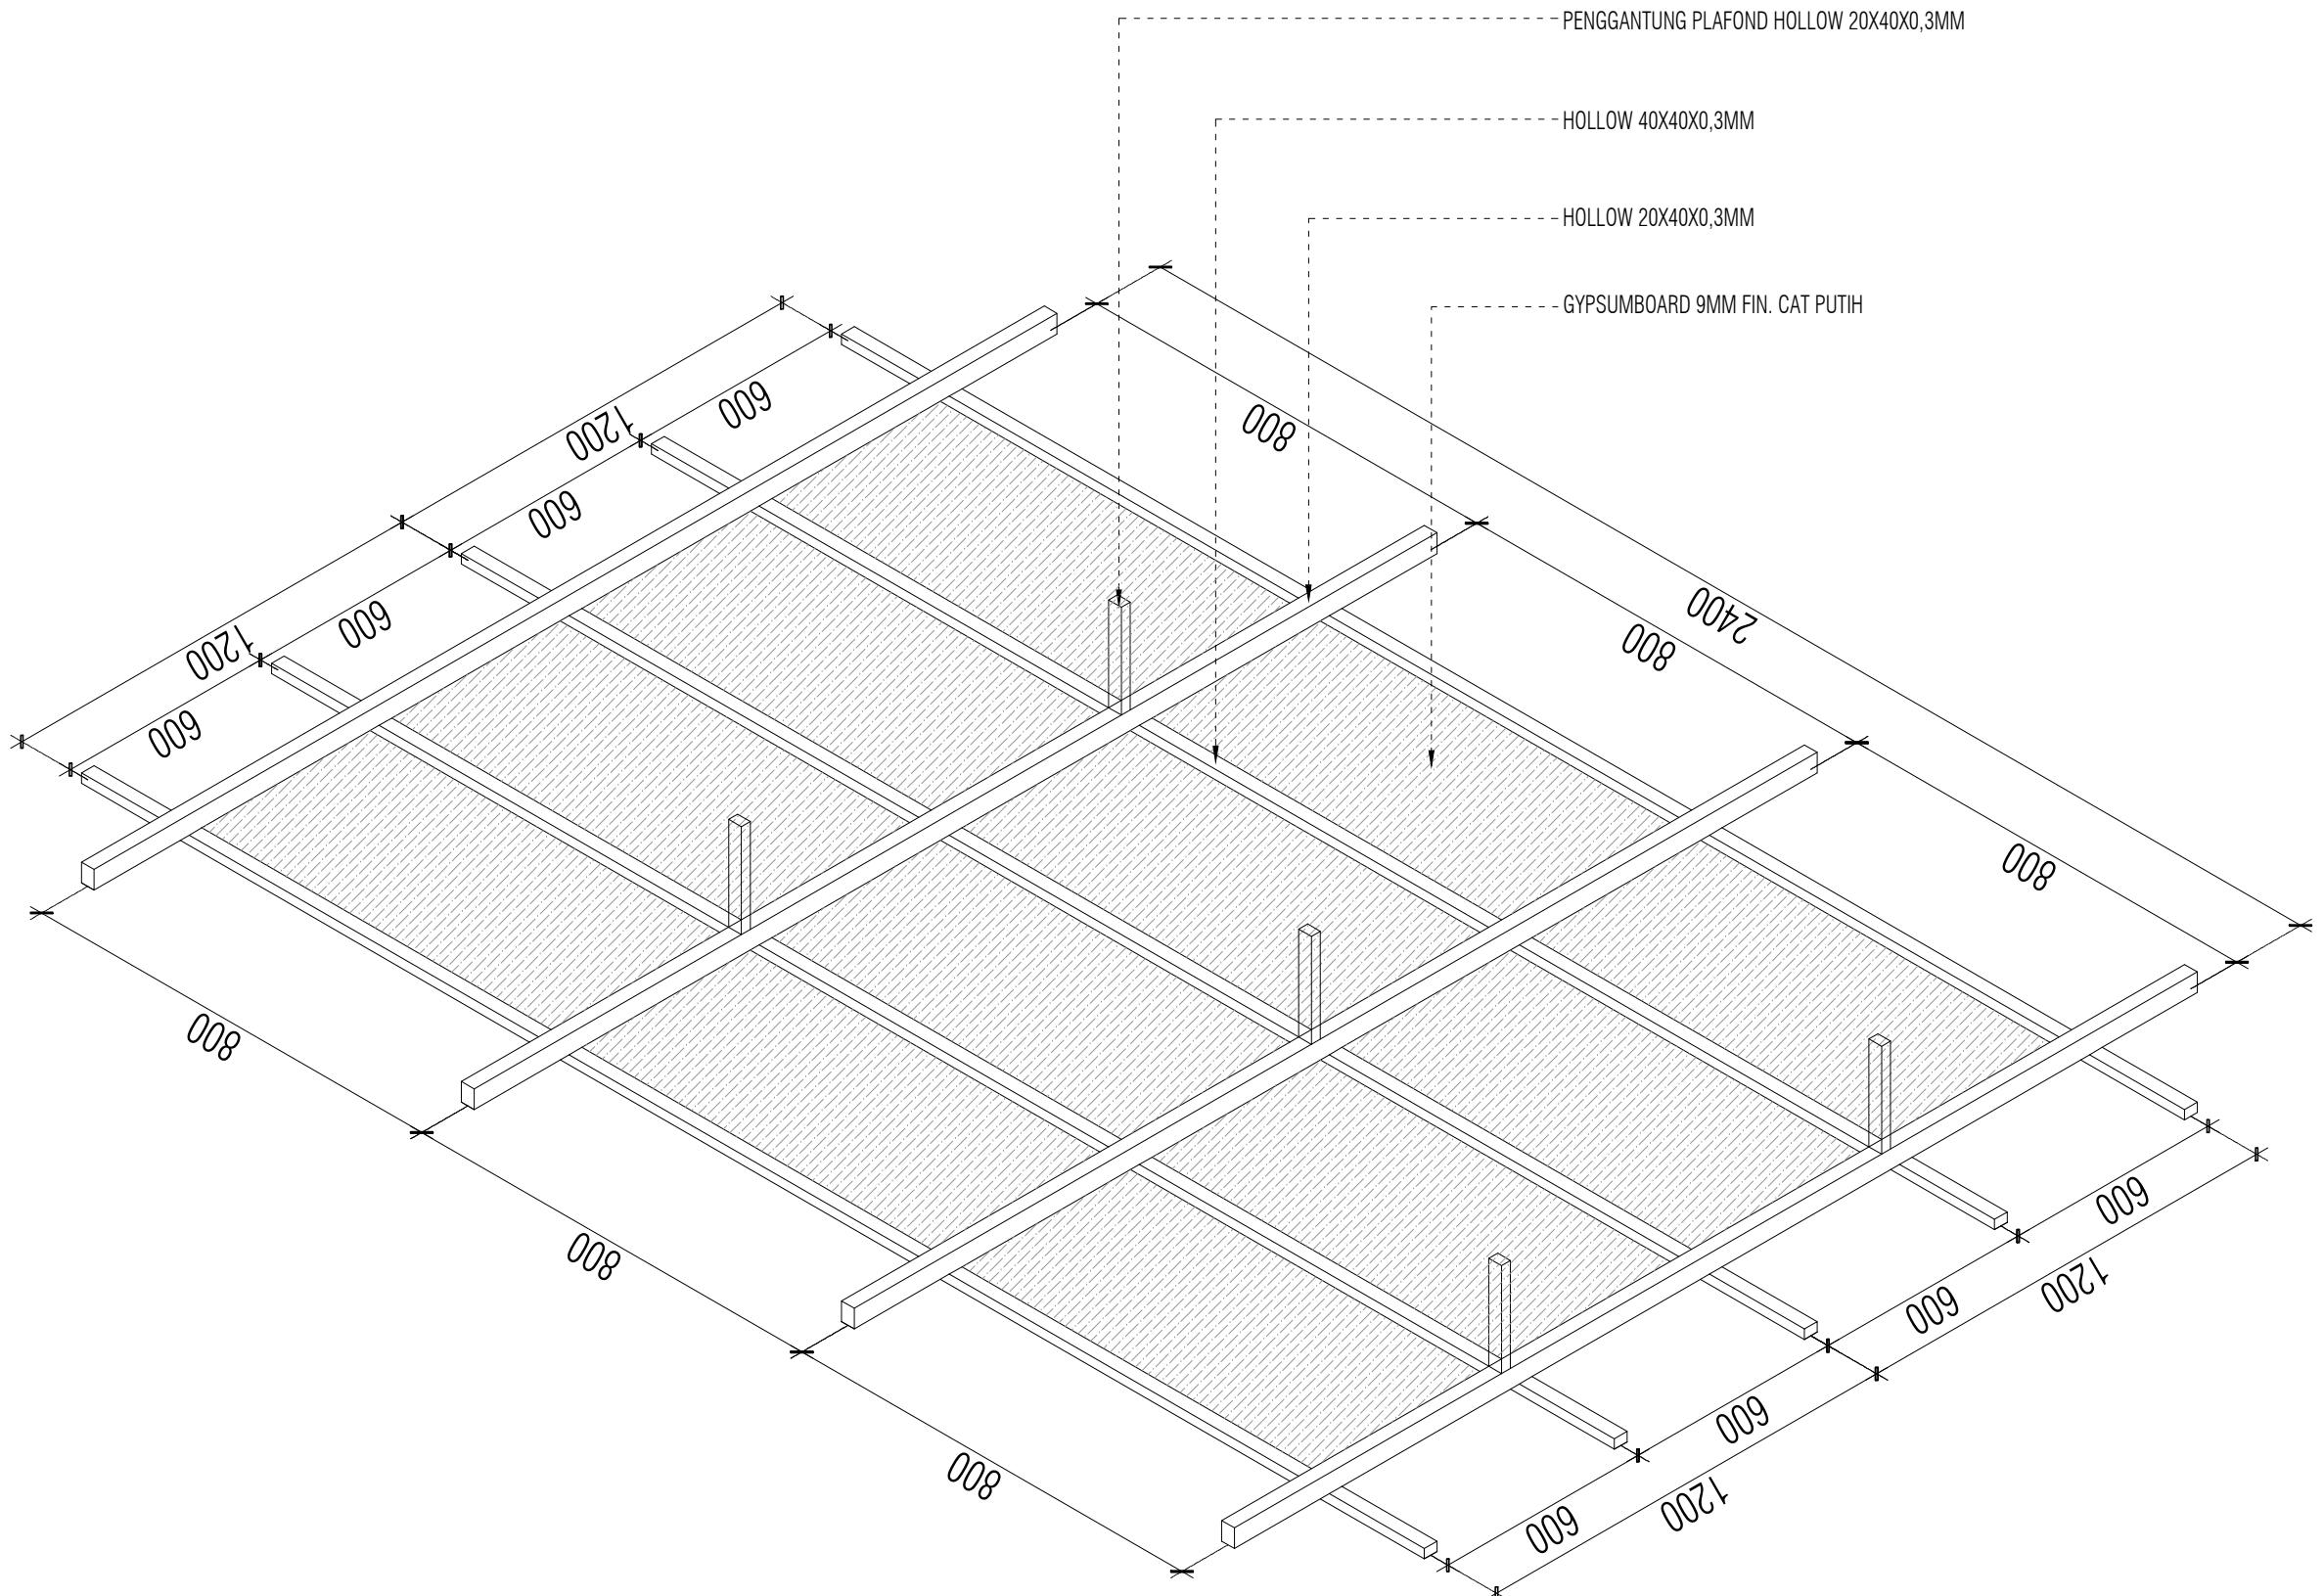


NAMA PROYEK	RUMAH TINGGAL 2 LANTAI	
LOKASI PROYEK	-	
PENANGGUNG JAWAB	-	
DIGAMBAR	PELAKSANA	
DISETUJUI	PEMILIK	
CATATAN	<p>1. PELAKSANA ATAU SUBKON WAJIB MEMERIKSA KEMBALI KESESUAIN GAMBAR DENGAN KONDISI LAPANGAN</p>	
JUDUL GAMBAR	SKALA	
1. ARS	1 : 100	
TANGGAL :	REVISI :	
5 AGUSTUS 2024	R1	
KODE GAMBAR	ARS-01-01	
NO. LBR	JUMLAH LBR	
00	00	

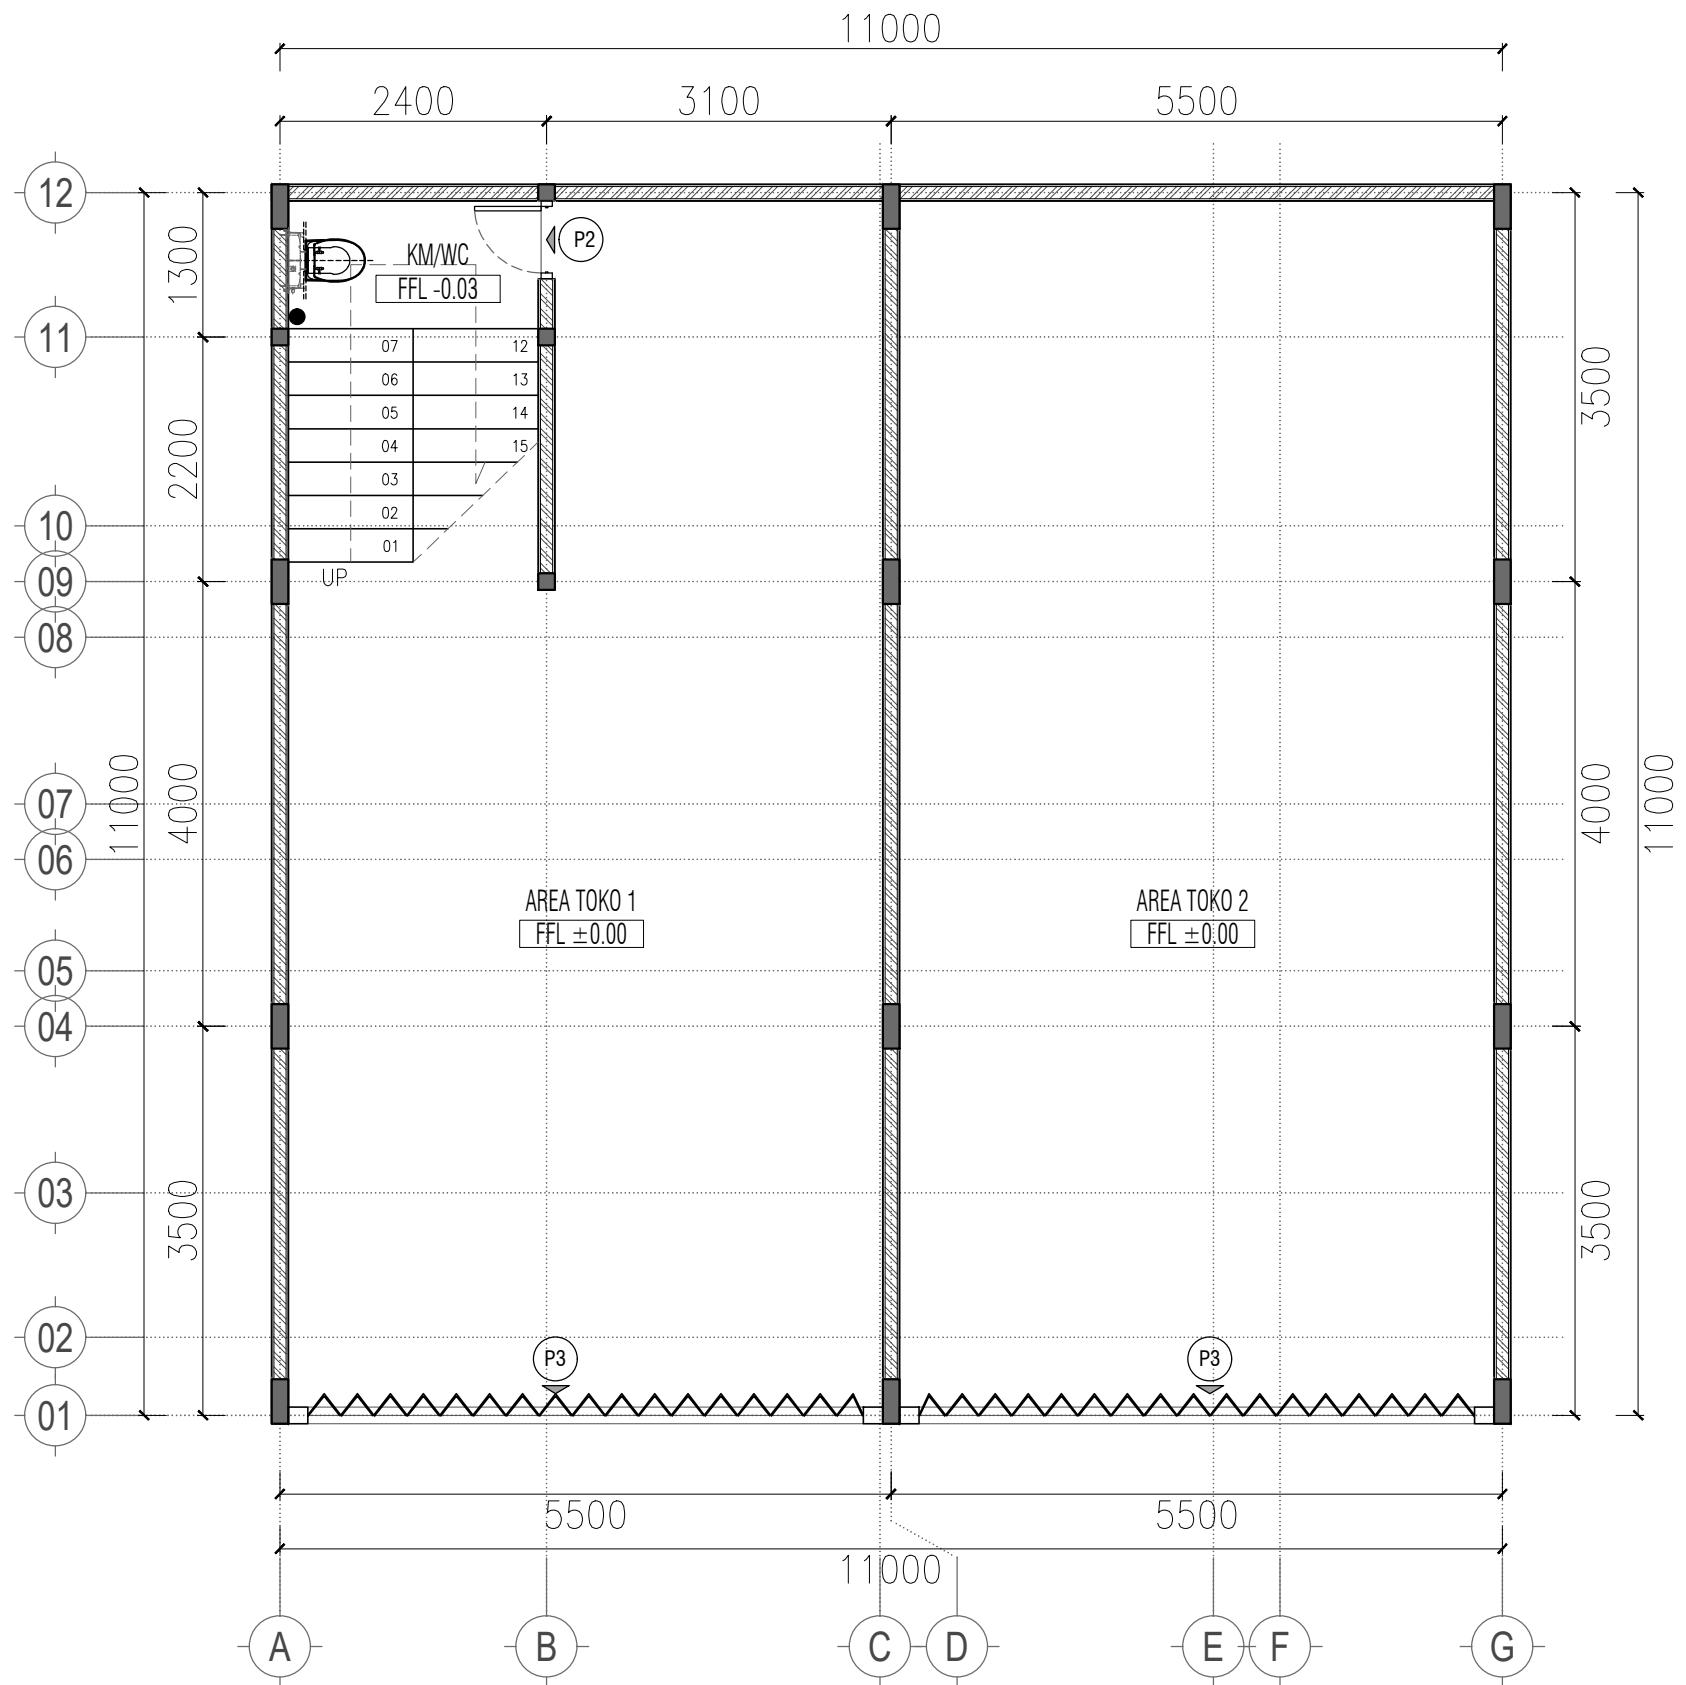

**DENAH PINTU DAN JENDELA LANTAI 1**

SKALA 1 : 100



NAMA PROYEK	RUMAH TINGGAL 2 LANTAI	
LOKASI PROYEK	-	
PENANGGUNG JAWAB	-	
DIGAMBAR	PELAKSANA	
DISETUJUI	PEMILIK	
CATATAN	<p>1. PELAKSANA ATAU SUBKON WAJIB MEMERIKSA KEMBALI KESESUAIN GAMBAR DENGAN KONDISI LAPANGAN</p>	
JUDUL GAMBAR	SKALA	
1. ARS	1 : 100	
TANGGAL :	REVISI :	
5 AGUSTUS 2024	R1	
KODE GAMBAR	ARS-01-01	
NO. LBR	JUMLAH LBR	
00	00	

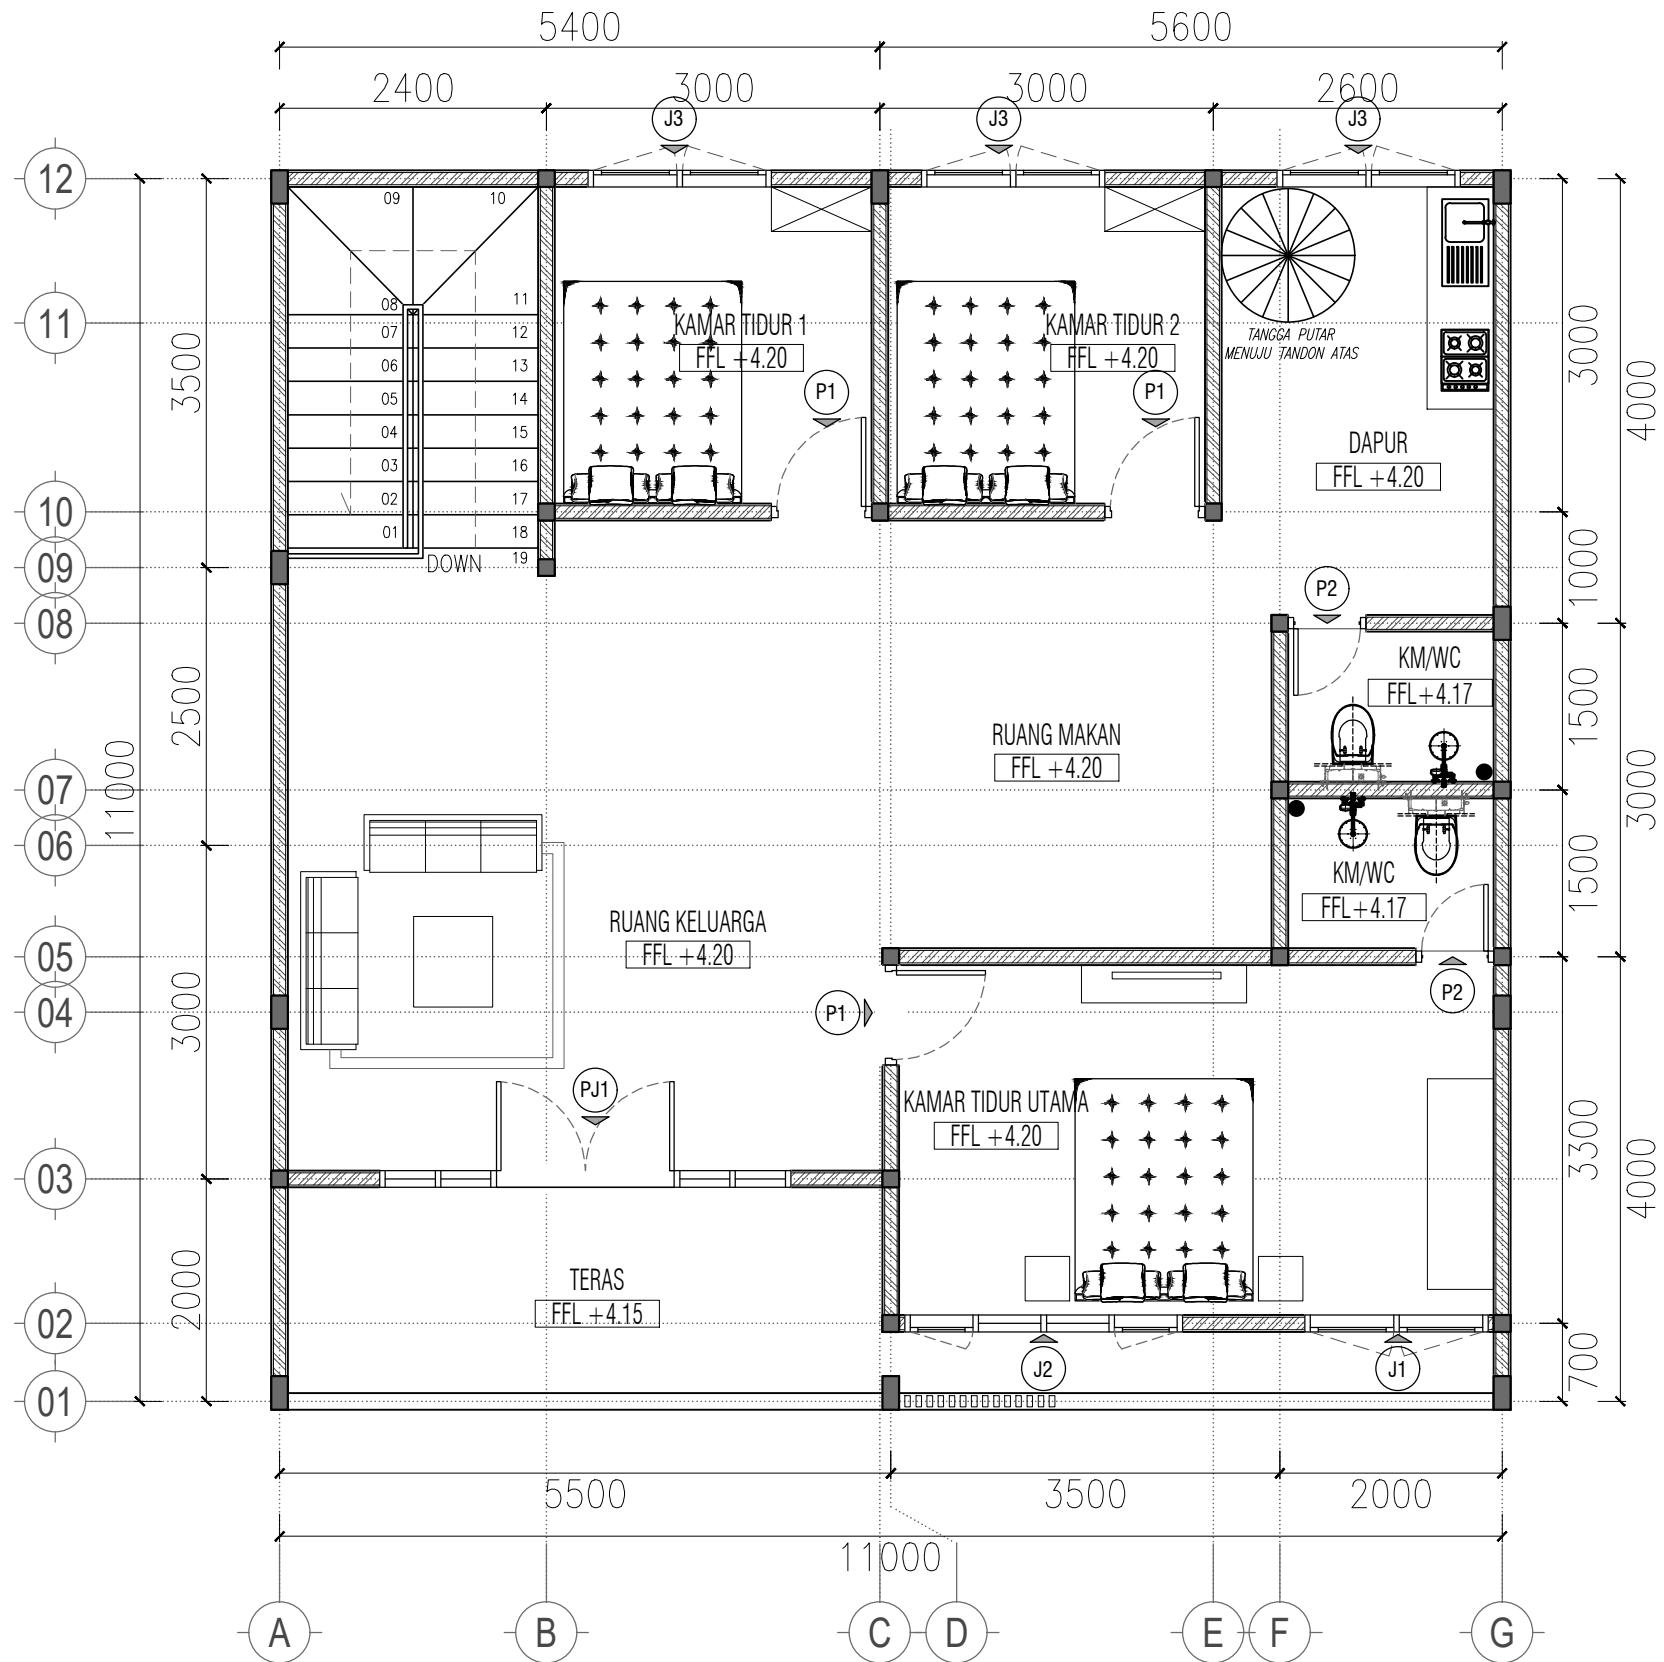

**DENAH PINTU DAN JENDELA LANTAI 2**

SKALA 1 : 100




NAMA PROYEK	
<b>RUMAH TINGGAL 2 LANTAI</b>	
LOKASI PROYEK	
DIGAMBAR	PELAKSANA
DISETUJUI	PEMILIK
CATATAN	
1. PELAKSANA ATAU SUBKON WAJIB MEMERIKSA KEMBALI KESESUAIN GAMBAR DENGAN KONDISI LAPANGAN	
JUDUL GAMBAR	SKALA
1.DETAIL P1	1 : 25
TANGGAL :	REVISI :
5 AGUSTUS 2024	<b>R1</b>
KODE GAMBAR	
ARS-06-33	
NO. LBR	JUMLAH LBR
33	00

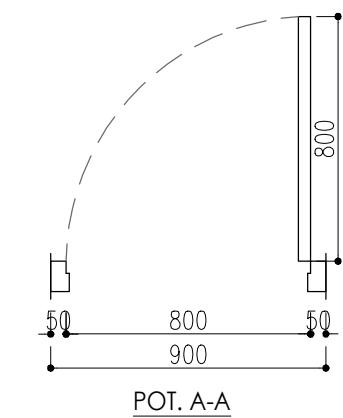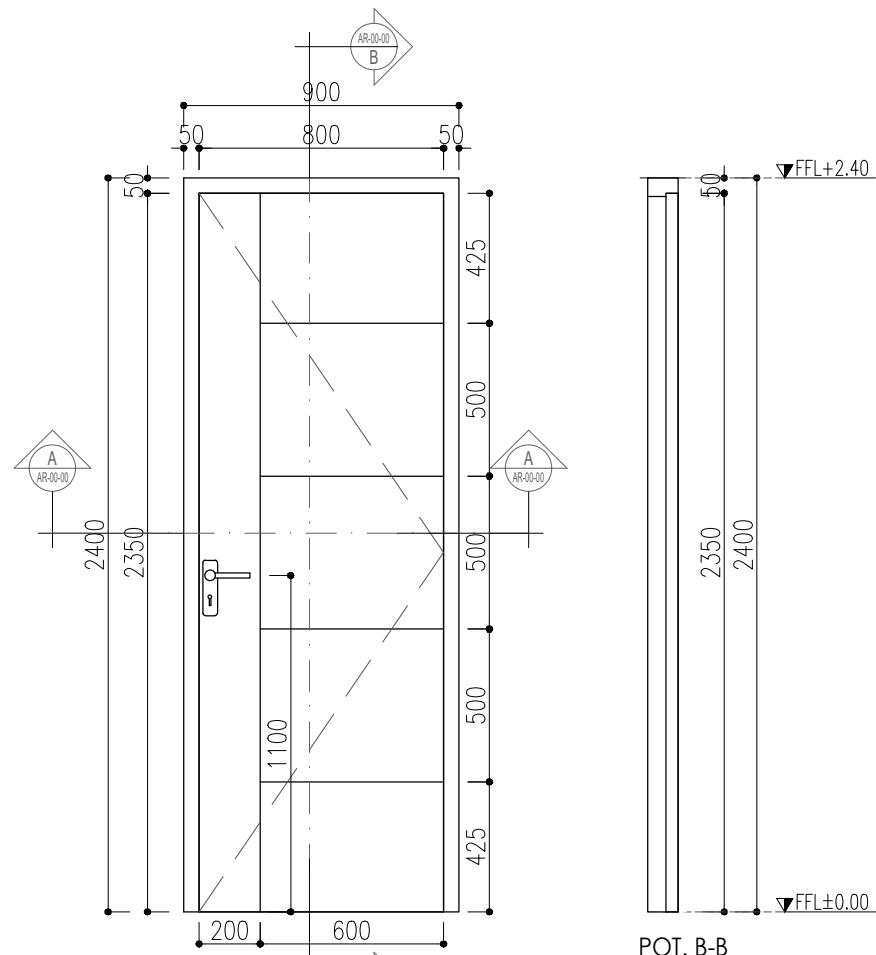

LOKASI	KAMAR TIDUR
JUMLAH	3 BUAH
KUSEN	ALUMUNIUM
DAUN PINTU	KAYU SOLID
FINISHING	WARNA HITAM
JENIS PINTU	PINTU SINGLE SWING

LOKASI	KAMAR MANDI
JUMLAH	3 BUAH
KUSEN	ALUMUNIUM
DAUN PINTU	ALUMUNIUM SPANDREL
FINISHING	WARNA HITAM
JENIS PINTU	ALUMINIUM SINGLE SWING



NAMA PROYEK	
<b>RUMAH TINGGAL 2 LANTAI</b>	
LOKASI PROYEK	
-	
PENANGGUNG JAWAB	
DIGAMBAR	PELAKSANA
DISETUJUI	PEMILIK
CATATAN	
1. PELAKSANA ATAU SUBKON WAJIB MEMERIKSA KEMBALI KESESUAIN GAMBAR DENGAN KONDISI LAPANGAN	
JUDUL GAMBAR	SKALA
1.DETAIL P1	1 : 25
TANGGAL :	REVISI :
5 AGUSTUS 2024	<b>R1</b>
KODE GAMBAR	ARS-06-33
NO. LBR	JUMLAH LBR
33	00

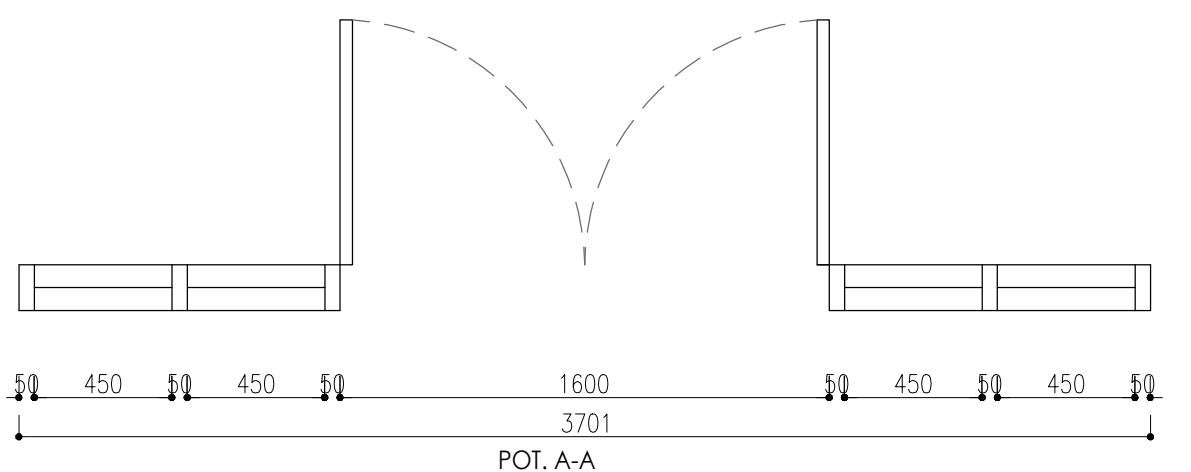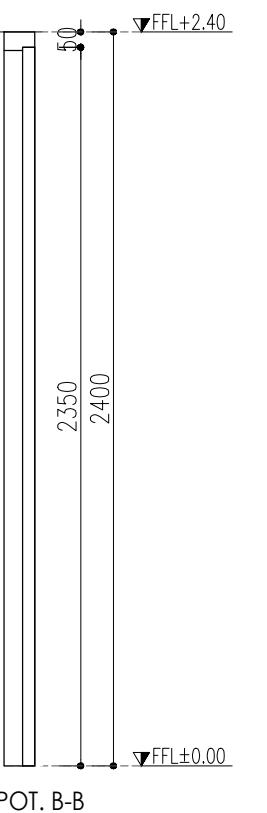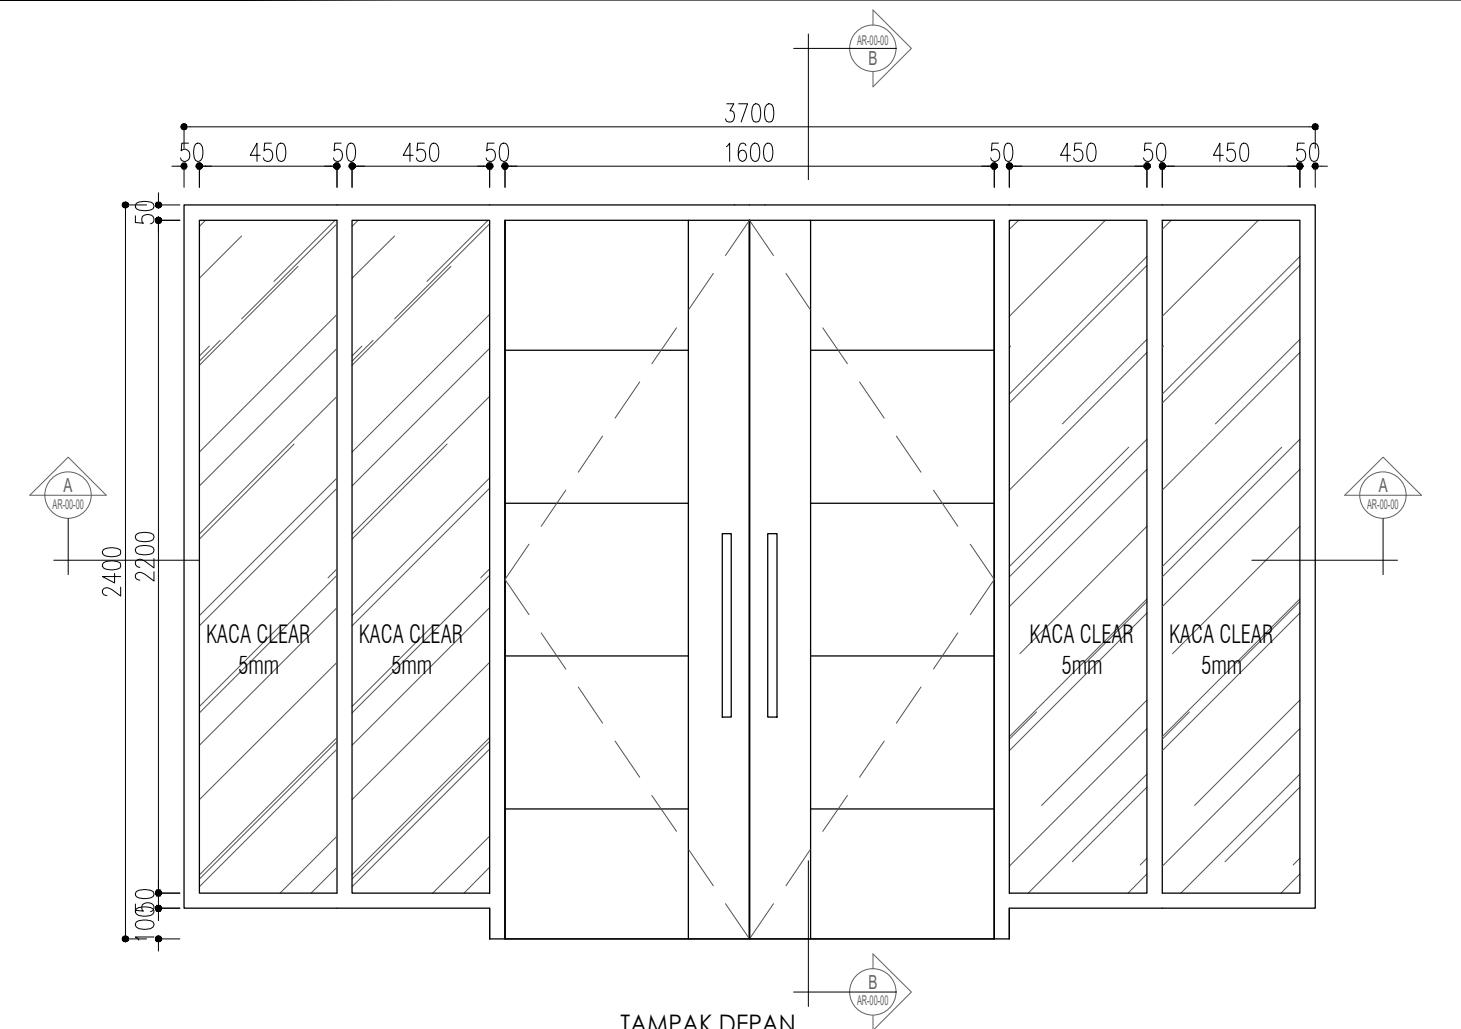

**DETAIL PJ1 = 1 PCS**  
SKALA 1 : 25

LOKASI	RUANG KELUARGA
JUMLAH	1 BUAH
KUSEN	ALUMUNIUM
DAUN PINTU	ALUMUNIUM + KACA CLEAR 5mm
FINISHING	WARNA HITAM
JENIS PINTU	PINTU DOUBLE SWING + JENDELA KACA 4 DAUN



NAMA PROYEK	
<b>RUMAH TINGGAL 2 LANTAI</b>	
LOKASI PROYEK	
-	
PENANGGUNG JAWAB	
DIGAMBAR	PELAKSANA
DISETUJUI	PEMILIK
CATATAN	
1. PELAKSANA ATAU SUBKON WAJIB MEMERIKSA KEMBALI KESESUAIN GAMBAR DENGAN KONDISI LAPANGAN	
JUDUL GAMBAR	SKALA
1.DETAIL P1	1 : 25
TANGGAL :	REVISI :
5 AGUSTUS 2024	<b>R1</b>
KODE GAMBAR	ARS-06-33
NO. LBR	JUMLAH LBR
33	00

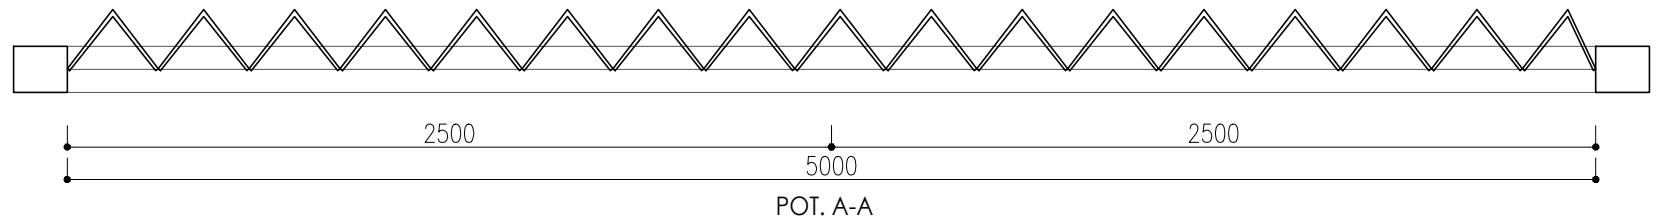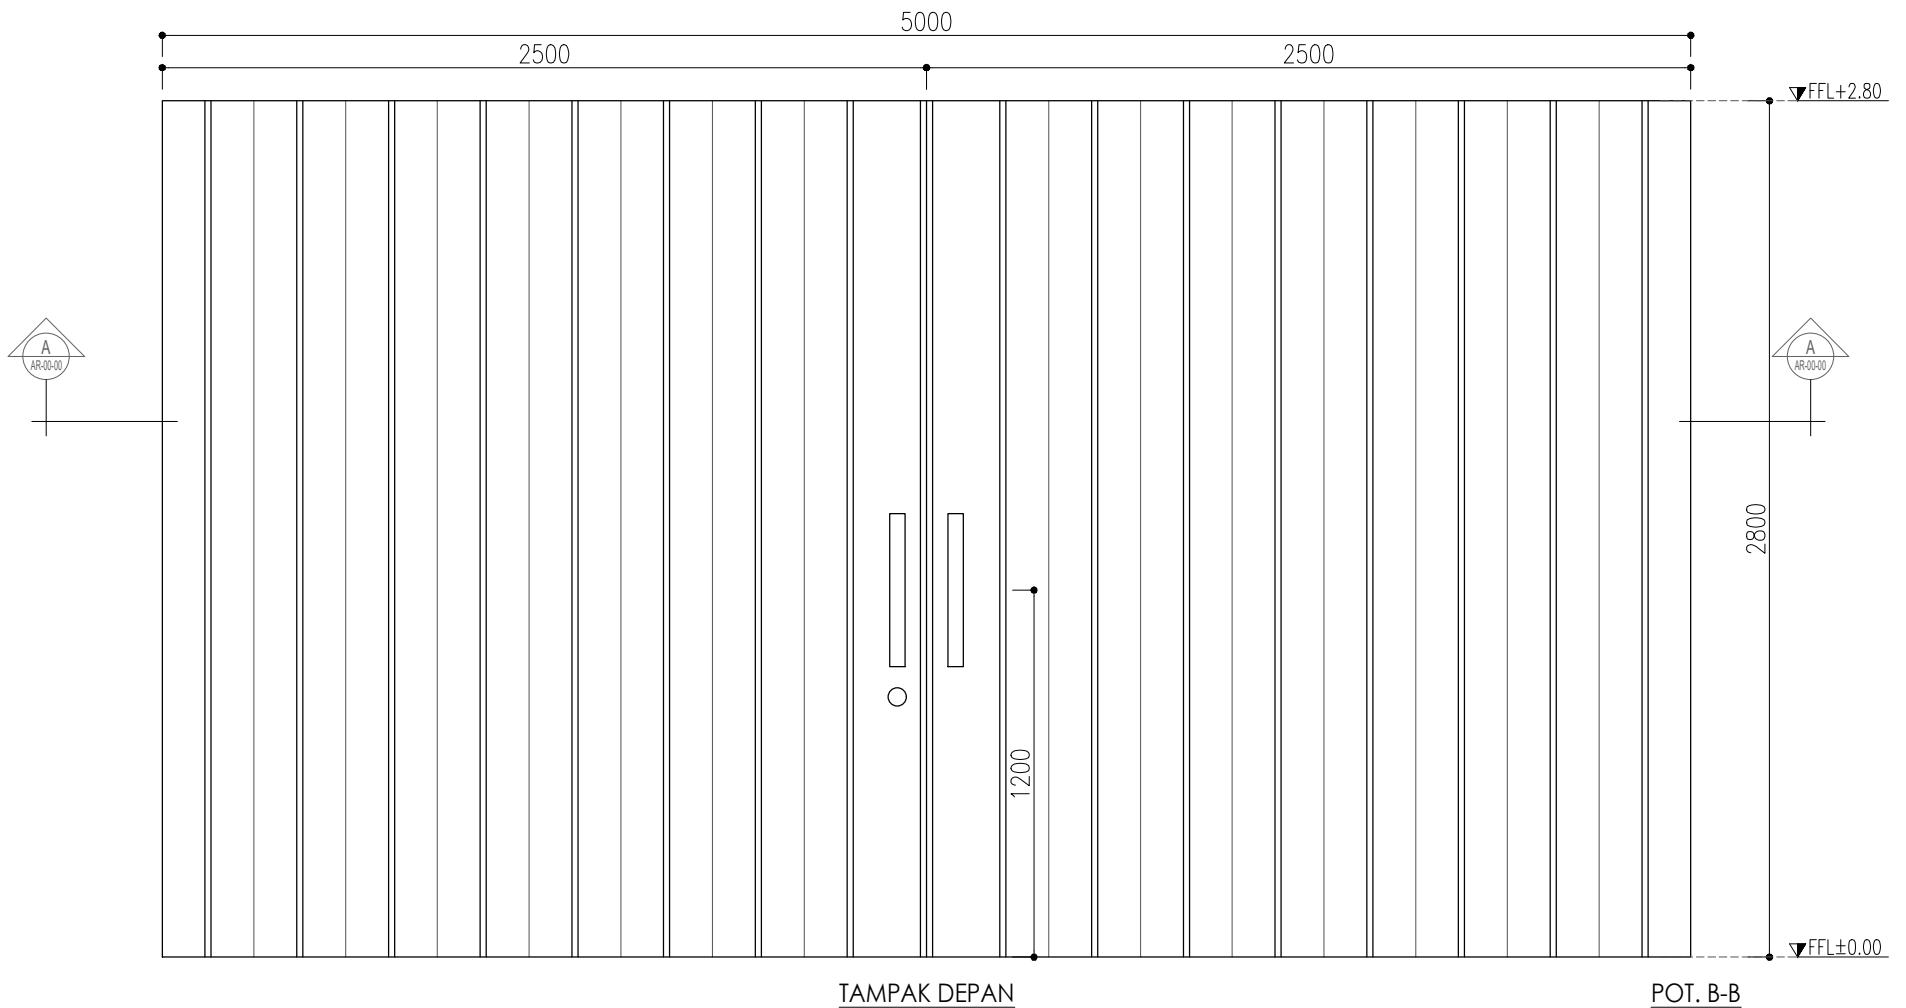



**DETAIL P3 = 2 PCS**  
SKALA 1 : 25

LOKASI	AREA TOKO
JUMLAH	2 BUAH
KUSEN	BESI
DAUN PINTU	BESI
FINISHING	WARNA HITAM
JENIS PINTU	PINTU HARMONIKA

NAMA PROYEK	
<b>RUMAH TINGGAL 2 LANTAI</b>	
LOKASI PROYEK	
DIGAMBAR	PELAKSANA
DISETUJUI	PEMILIK
CATATAN	
1. PELAKSANA ATAU SUBKON WAJIB MEMERIKSA KEMBALI KESESUAIN GAMBAR DENGAN KONDISI LAPANGAN	
JUDUL GAMBAR	SKALA
1.DETAIL P1	1 : 25
TANGGAL :	REVISI :
5 AGUSTUS 2024	<b>R1</b>
KODE GAMBAR	
ARS-06-33	
NO. LBR	JUMLAH LBR
33	00

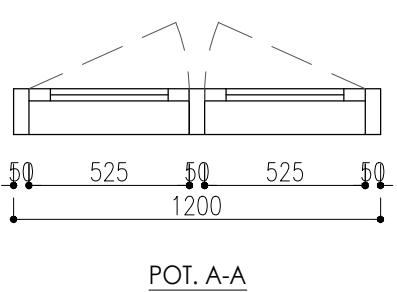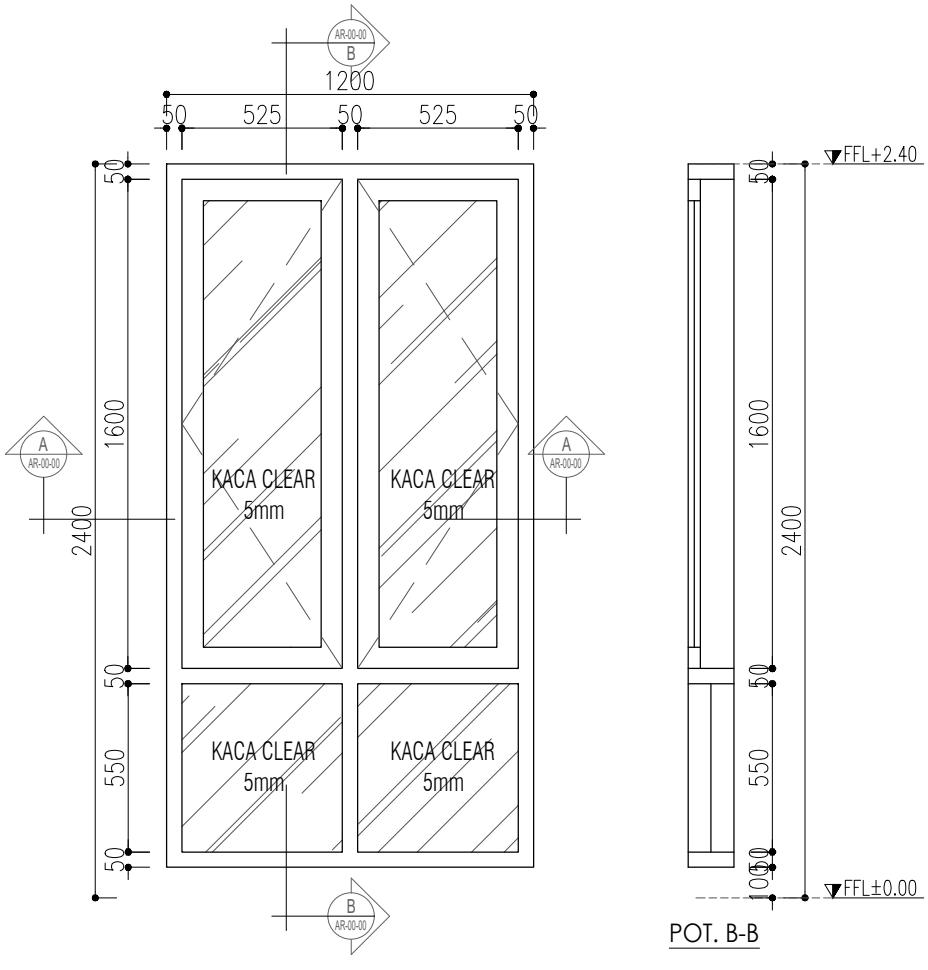

**DETAIL J1 = 1 PCS**  
SKALA 1 : 25

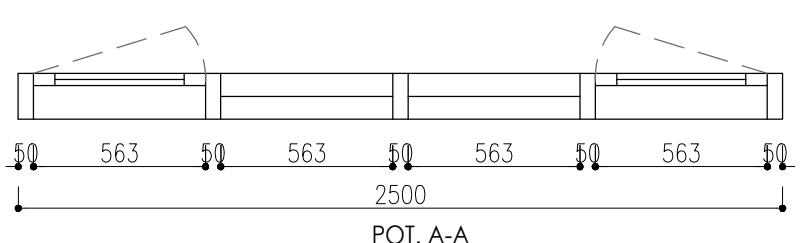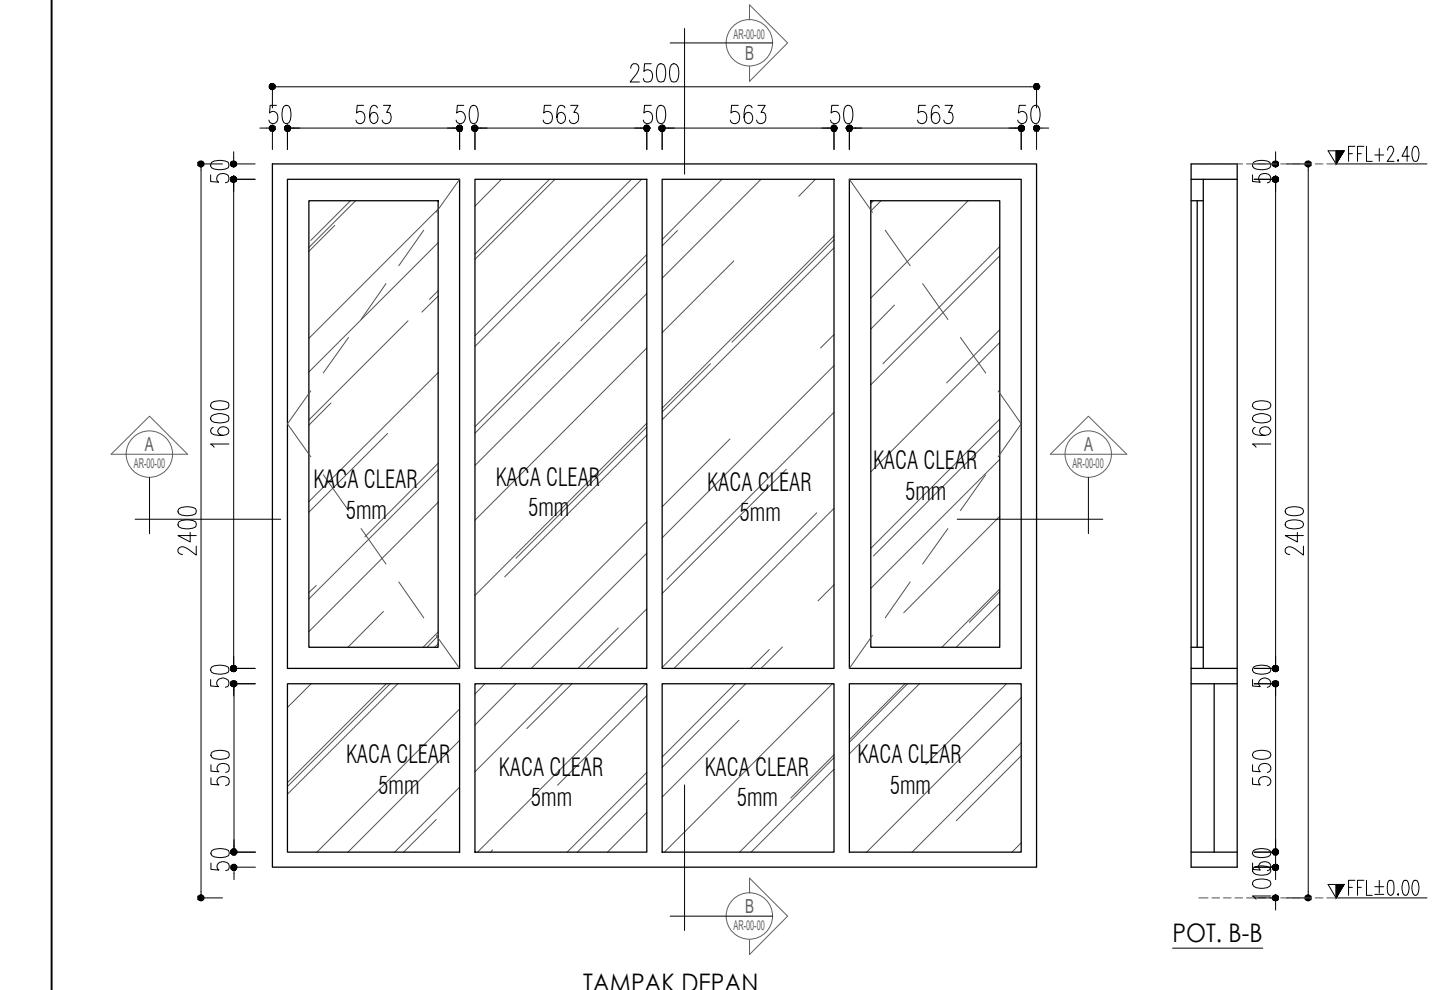


**DETAIL J2 = 1 PCS**  
SKALA 1 : 25

LOKASI	TAMPAK DEPAN
JUMLAH	1 BUAH
KUSEN	ALUMUNIUM
DAUN JENDELA	ALUMUNIUM + KACA CLEAR 5mm
FINISHING	WARNA HITAM
JENIS JENDELA	JENDELA 2 DAUN


LOKASI	TAMPAK DEPAN
JUMLAH	1 BUAH
KUSEN	ALUMUNIUM
DAUN JENDELA	ALUMUNIUM + KACA CLEAR 5mm
FINISHING	WARNA HITAM
JENIS JENDELA	JENDELA 4 DAUN

NAMA PROYEK	
<b>RUMAH TINGGAL 2 LANTAI</b>	
LOKASI PROYEK	
-	-
PENANGGUNG JAWAB	
DIGAMBAR	PELAKSANA
DISETUJUI	PEMILIK
CATATAN	
1. PELAKSANA ATAU SUBKON WAJIB MEMERIKSA KEMBALI KESESUAIN GAMBAR DENGAN KONDISI LAPANGAN	
JUDUL GAMBAR	SKALA
1.DETAIL P1	1 : 25
TANGGAL :	REVISI :
5 AGUSTUS 2024	<b>R1</b>
KODE GAMBAR	
ARS-06-33	
NO. LBR	JUMLAH LBR
33	00

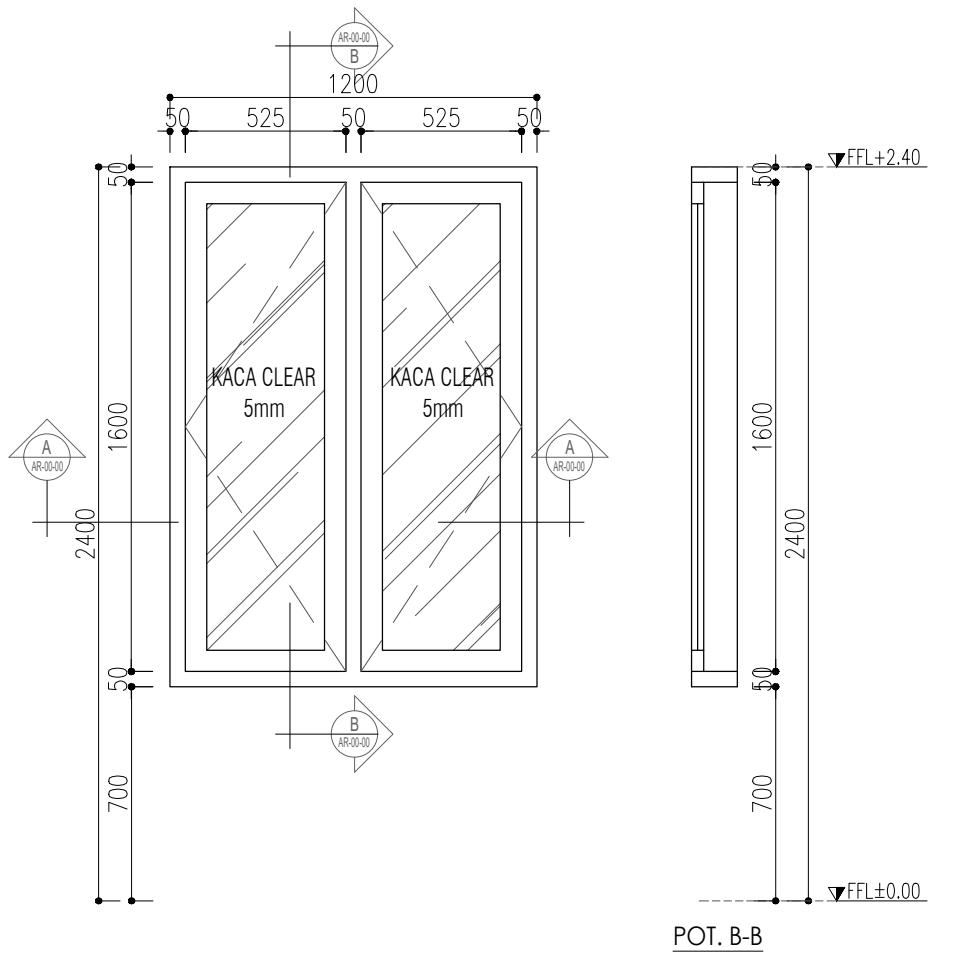

TAMPAK DEPAN

POT. B-B

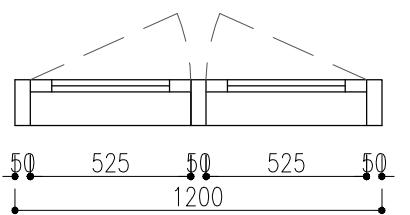

POT. A-A





**DETAIL J3 = 3 PCS**


SKALA 1 : 25

LOKASI	TAMPAK BELAKANG
JUMLAH	3 BUAH
KUSEN	ALUMUNIUM
DAUN JENDELA	ALUMUNIUM + KACA CLEAR 5mm
FINISHING	WARNA HITAM
JENIS JENDELA	JENDELA 2 DAUN


NAMA PROYEK	
<b>RUMAH TINGGAL 2 LANTAI</b>	
LOKASI PROYEK	
-	-
PENANGGUNG JAWAB	
DIGAMBAR	PELAKSANA
DISETUJUI	PEMILIK
CATATAN	
1. PELAKSANA ATAU SUBKON WAJIB MEMERIKSA KEMBALI KESESUAIN GAMBAR DENGAN KONDISI LAPANGAN	
JUDUL GAMBAR	SKALA
1. ARS	1 : 100
TANGGAL :	REVISI :
5 AGUSTUS 2024	<b>R1</b>
KODE GAMBAR	
ARS-01-01	
NO. LBR	JUMLAH LBR
00	00

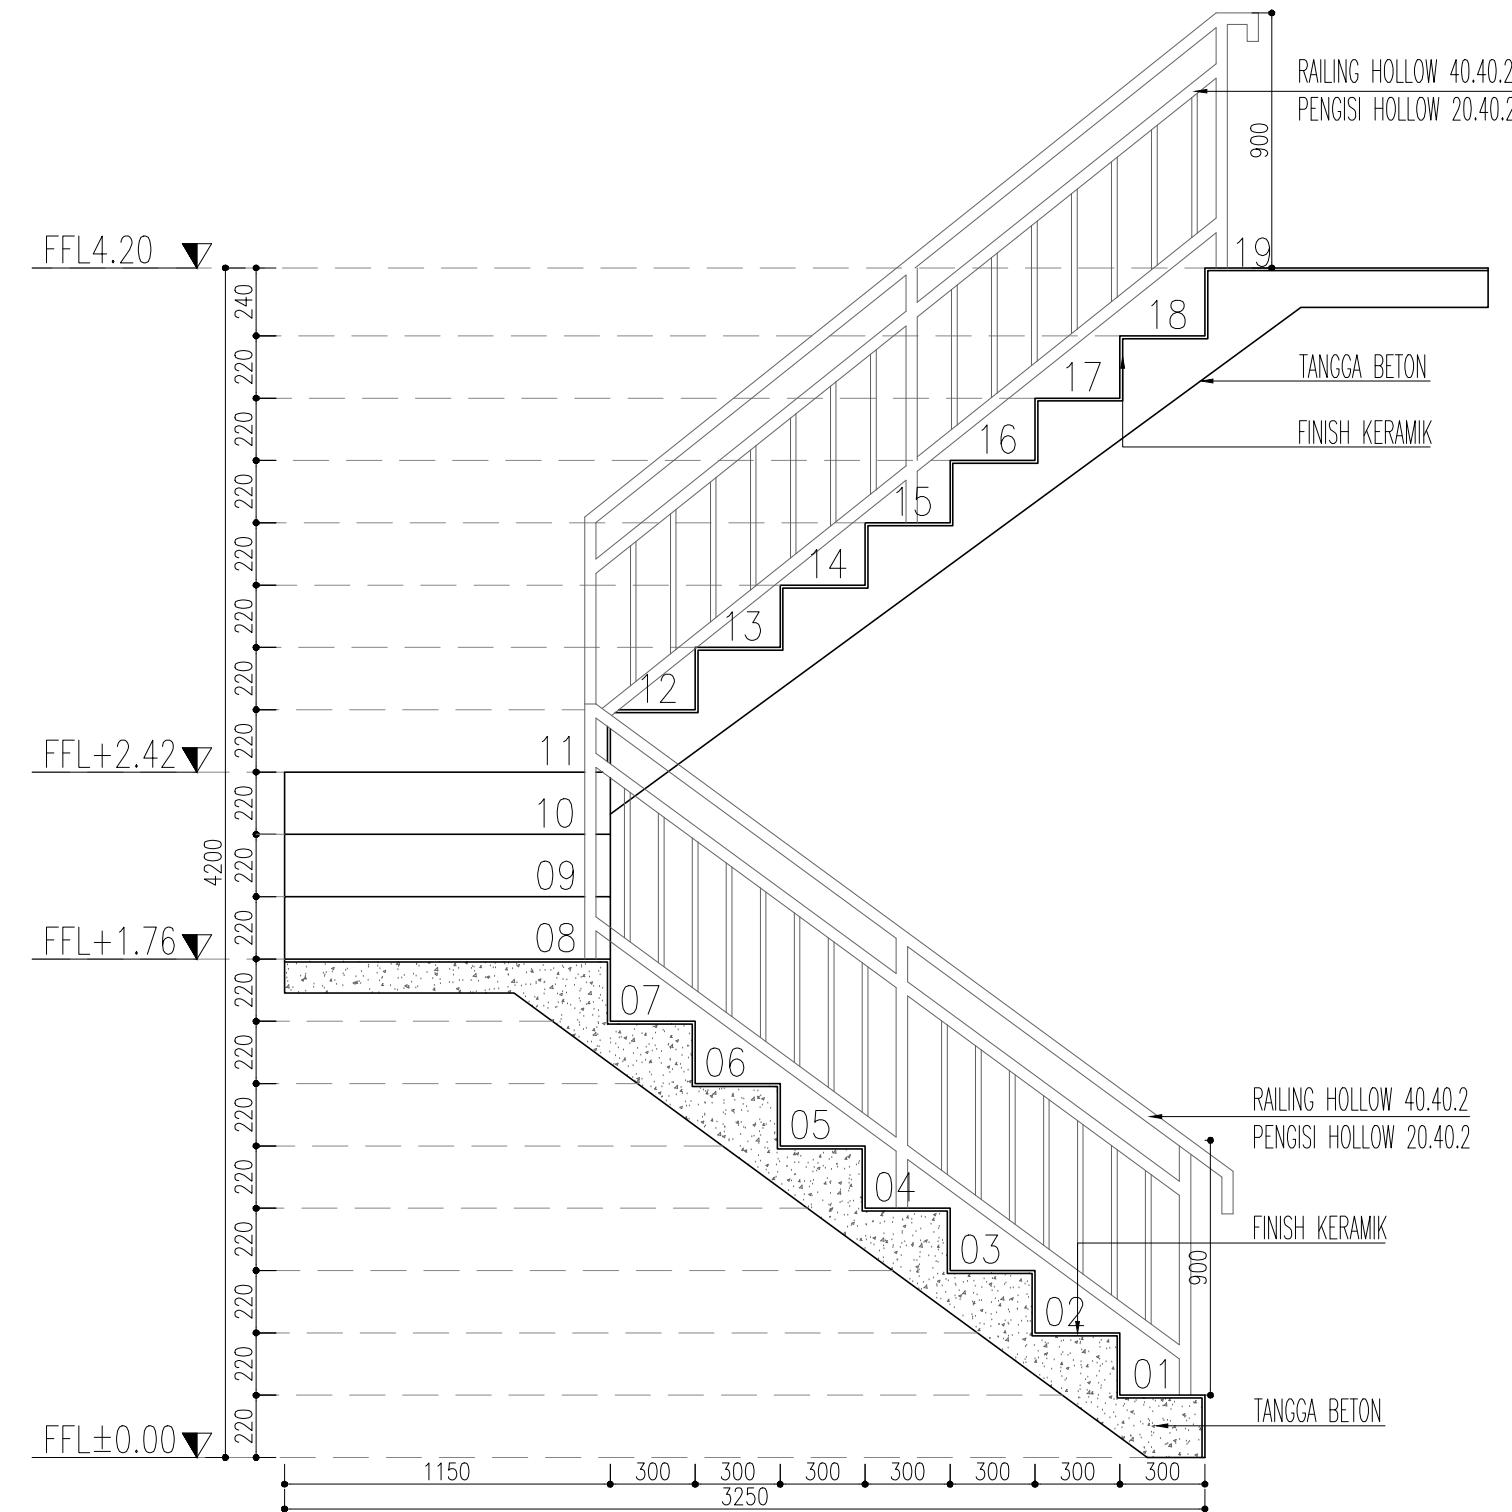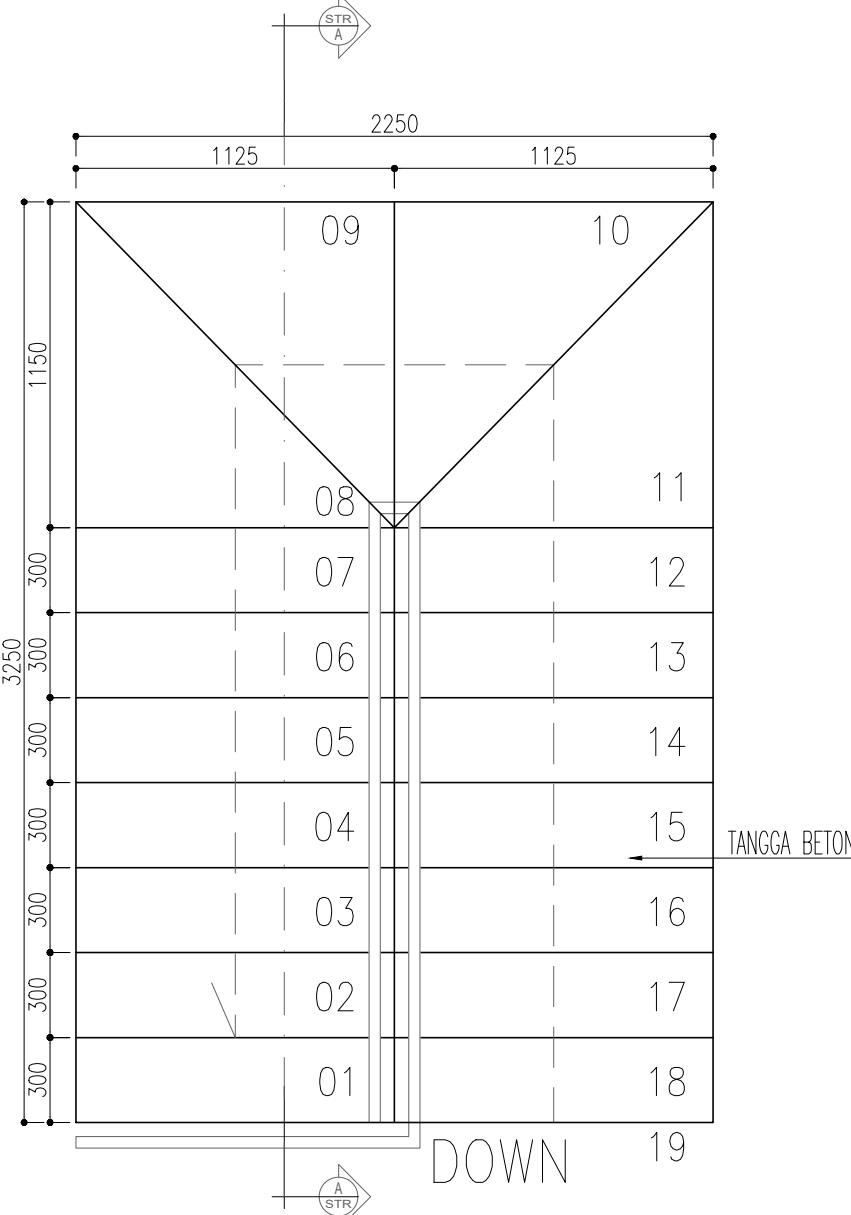

NAMA PROYEK	
<b>RUMAH TINGGAL 2 LANTAI</b>	
LOKASI PROYEK	
-	-
PENANGGUNG JAWAB	
DIGAMBAR	PELAKSANA
DISETUJUI	PEMILIK
CATATAN	
1. PELAKSANA ATAU SUBKON WAJIB MEMERIKSA KEMBALI KESESUAIN GAMBAR DENGAN KONDISI LAPANGAN	
JUDUL GAMBAR	SKALA
1. ARS	1 : 100
TANGGAL :	REVISI :
5 AGUSTUS 2024	<b>R1</b>
KODE GAMBAR	
ARS-01-01	
NO. LBR	JUMLAH LBR
00	00

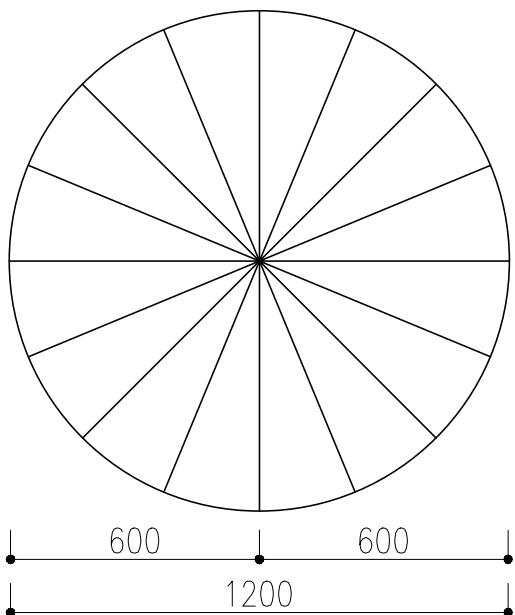

**DENAH TANGGA PUTAR**  
SKALA 1 : 25

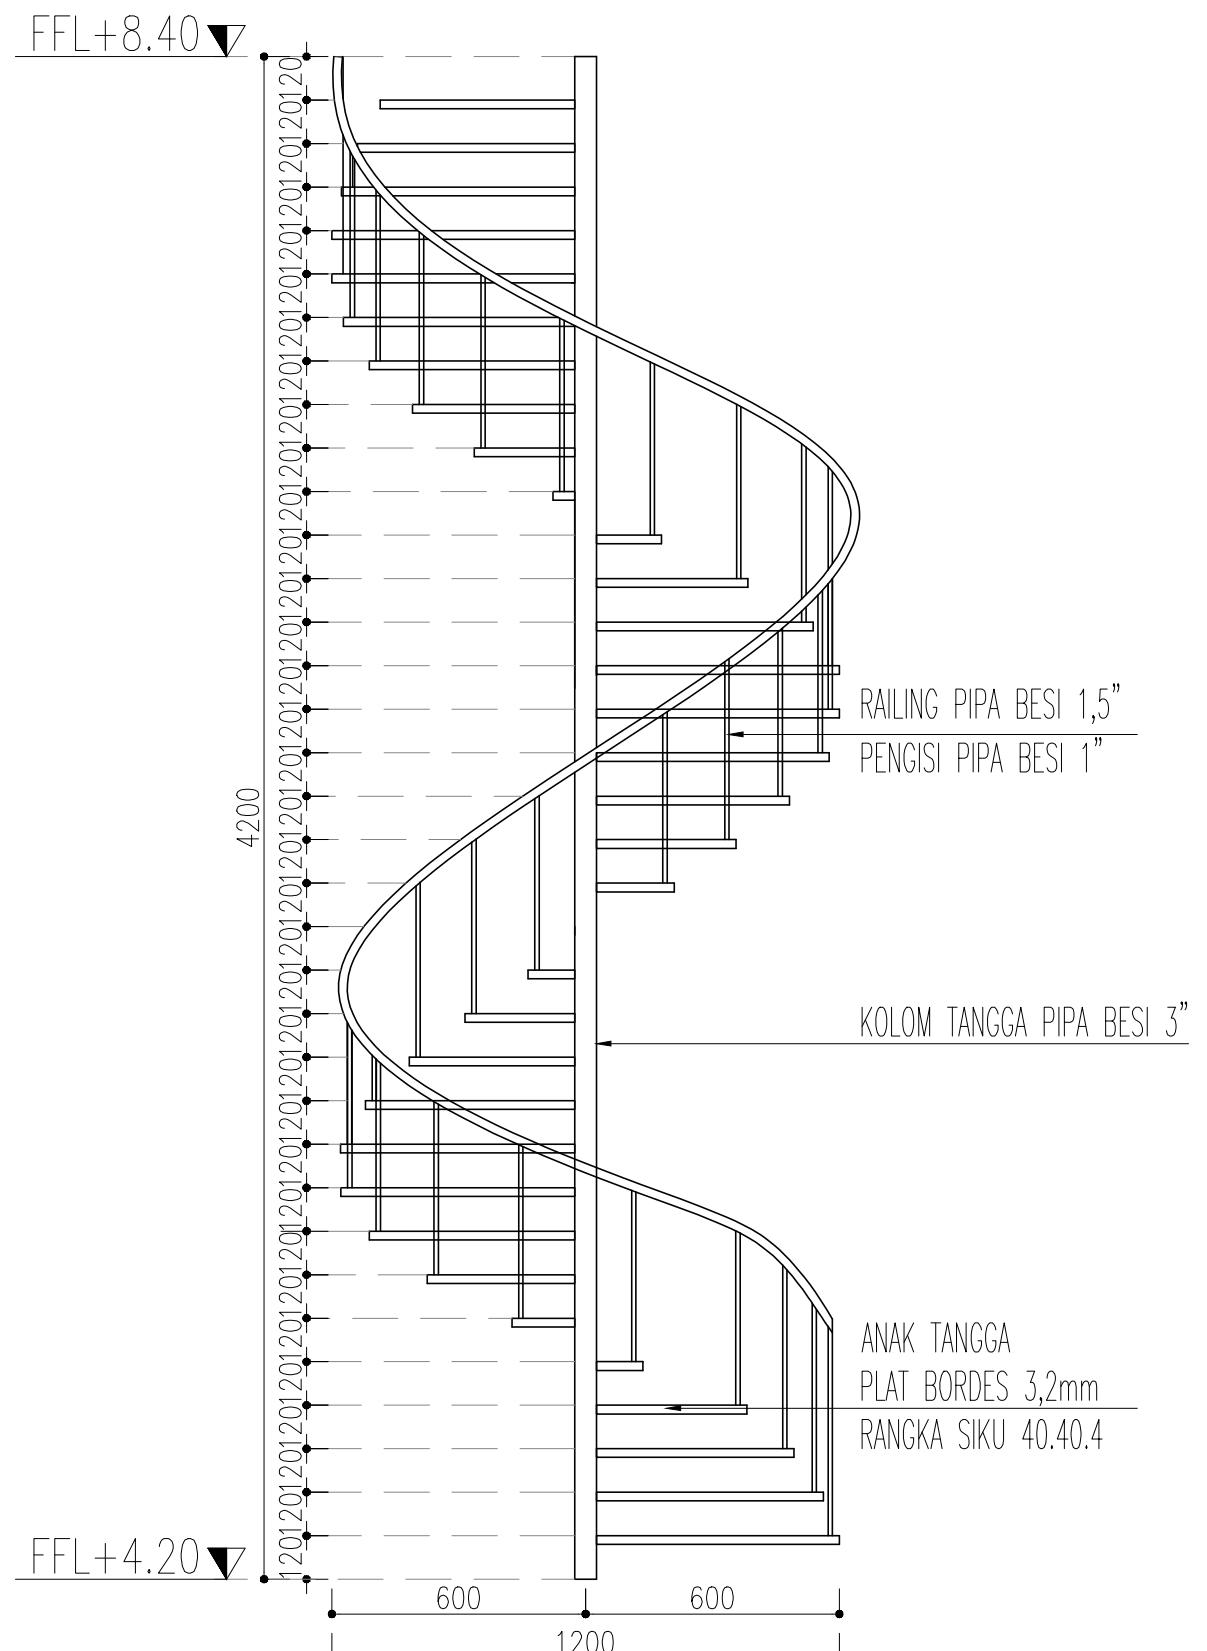

**TAMPAK TANGGA PUTAR**  
SKALA 1 : 25