


## DAFTAR GAMBAR

NOMER	NAMA GAMBAR	SKALA	KODE
<b>BAB.01</b>	<b>DAFTAR GAMBAR</b>		
1	DAFTAR GAMBAR	NTS	ARS-01-01
<b>BAB.02</b>	<b>SITE PLAN</b>		
2	SITE PLAN	1:100	ARS-02-02
<b>BAB.03</b>	<b>ARSITEKTUR</b>		
3	DENAH RENCANA GUDANG	1:100	ARS-03-03
4	DENAH RENCANA ATAP	1:100	ARS-03-04
5	TAMPAK DEPAN	1:50	ARS-03-05
6	TAMPAK BELAKANG	1:50	ARS-03-06
7	TAMPAK SAMPING KIRI	1:50	ARS-03-07
8	TAMPAK SAMPING KANAN	1:50	ARS-03-08
9	POTONGAN A-A	1:50	ARS-03-09
10	POTONGAN B-B	1:50	ARS-03-10
11	POTONGAN C-C	1:50	ARS-03-11
12	POTONGAN D-D	1:50	ARS-03-12
<b>BAB.04</b>	<b>STRUKTUR</b>		
13	DENAH PILECAP SFL-1.00 (ELEVASI BOTTOM)	1:100	STR-04-13
14	DETAIL PONDASI PC 1 DAN PC 2	1:25	STR-04-14
15	DENAH SLOOF SFL±0.00	1:100	STR-04-15
16	DENAH PLAT DAN KOLOM SFL±0.00	1:100	STR-04-16
17	DETAIL SLOOF, BALOK, DAN KOLOM	1:25	STR-04-17
18	DENAH KOLOM BAJA SFL+1.00	1:100	STR-04-18
19	DENAH BALOK RELL PINTU SFL+3.80	1:100	STR-04-19
20	DENAH REGEL SFL+7.00	1:100	STR-04-20
21	DENAH RAFTER/KUDA-KUDA	1:100	STR-04-21
22	DENAH RANGKA ATAP	1:100	STR-04-22


## DAFTAR GAMBAR

NAMA PROYEK	
<p style="text-align: center;"><b>PROJECT GUDANG</b></p> <p style="text-align: center;">PT. JOJOPLAST GEMILANG</p>	
LOKASI PROYEK	
<p style="text-align: center;">jl. Raya Sawocangkring no.102</p> <p style="text-align: center;"><b>Wonoayu, Sidoarjo - JATIM</b></p>	
PENANGGUNG JAWAB	
DIGAMBAR	PELAKSANA
DISETUJUI	PEMILIK
CATATAN	
<p>1. PELAKSANA ATAU SUBKON WAJIB MEMERIKSA KEMBALI KESESUAIN GAMBAR DENGAN KONDISI LAPANGAN</p>	
JUDUL GAMBAR	
1. DAFTAR GAMBAR	
NTS	
TANGGAL :	REVISI :
15 NOVEMBER 2024	
<b>R1</b>	
KODE GAMBAR	
ARS-01-01	
NO. LBR	JUMLAH LBR
01	33

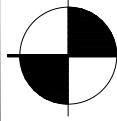

## SITE PLAN


SKALA 1 : 500

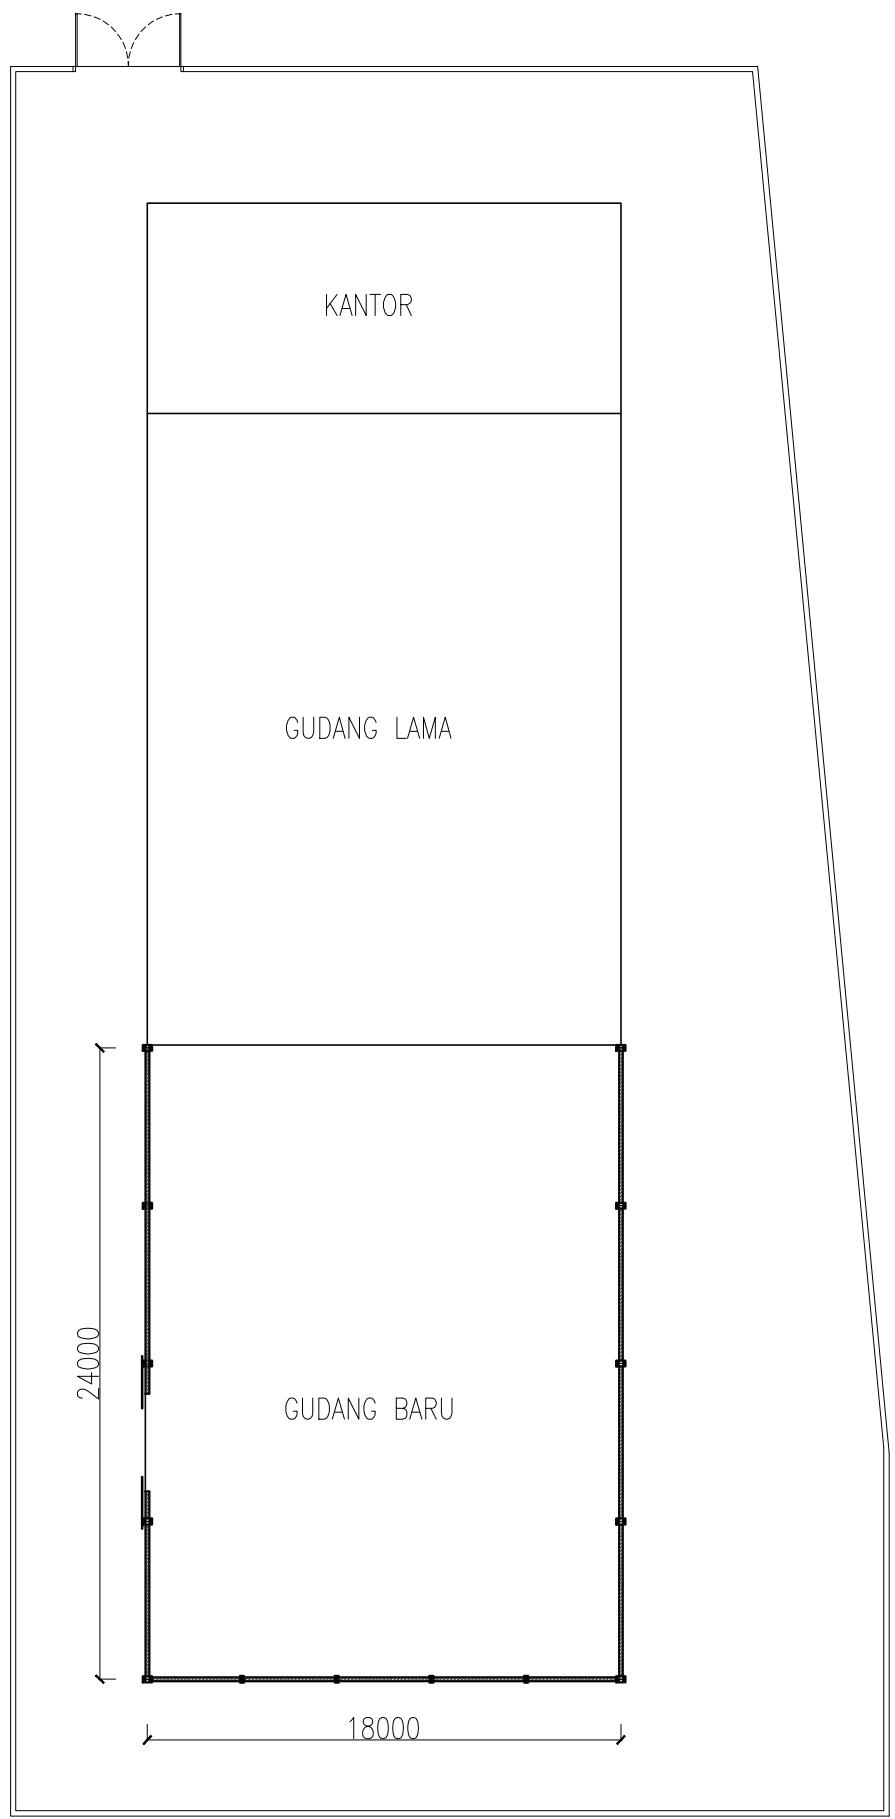


1. PELAKSANA ATAU SUBKON WAJIB MEMERIKSA KEMBALI KESESUAIN GAMBAR DENGAN KONDISI LAPANGAN


PROJECT GUDANG	
PT. JOJOPLAST GEMILANG	
LOKASI PROYEK	
jl. Raya Sawocangkring no.102	
Wonoaju, Sidoarjo - JATIM	
PENANGGUNG JAWAB	
DIGAMBAR	PELAKSANA
DISETUJU	PENULIR
CATATAN	
JUDUL GAMBAR	SKALA
TANGGAL :	REVISI :
15 NOVEMBER 2024	R1
KODE GAMBAR	
ARS-02-02	
NO. LBR	JUMLAH LBR
02	33

NAMA PROYEK	
<b>PROJECT GUDANG</b> PT. JOJOPLAST GEMILANG	
LOKASI PROYEK	
jl. Raya Sawocangkring no.102 <b>Wonoayu, Sidoarjo - JATIM</b>	
PENANGGUNG JAWAB	
DIGAMBAR	PELAKSANA
DISETUJU	PEMILIK
CATATAN	
1. PELAKSANA ATAU SUBKON WAJIB MEMERIKSA KEMBALI KESESUAIN GAMBAR DENGAN KONDISI LAPANGAN	
JUDUL GAMBAR	SKALA
TANGGAL :	REVISI :
15 NOVEMBER 2024	<b>R1</b>
KODE GAMBAR	
<b>STR-03-03</b>	
NO. LBR	JUMLAH LBR
03	33

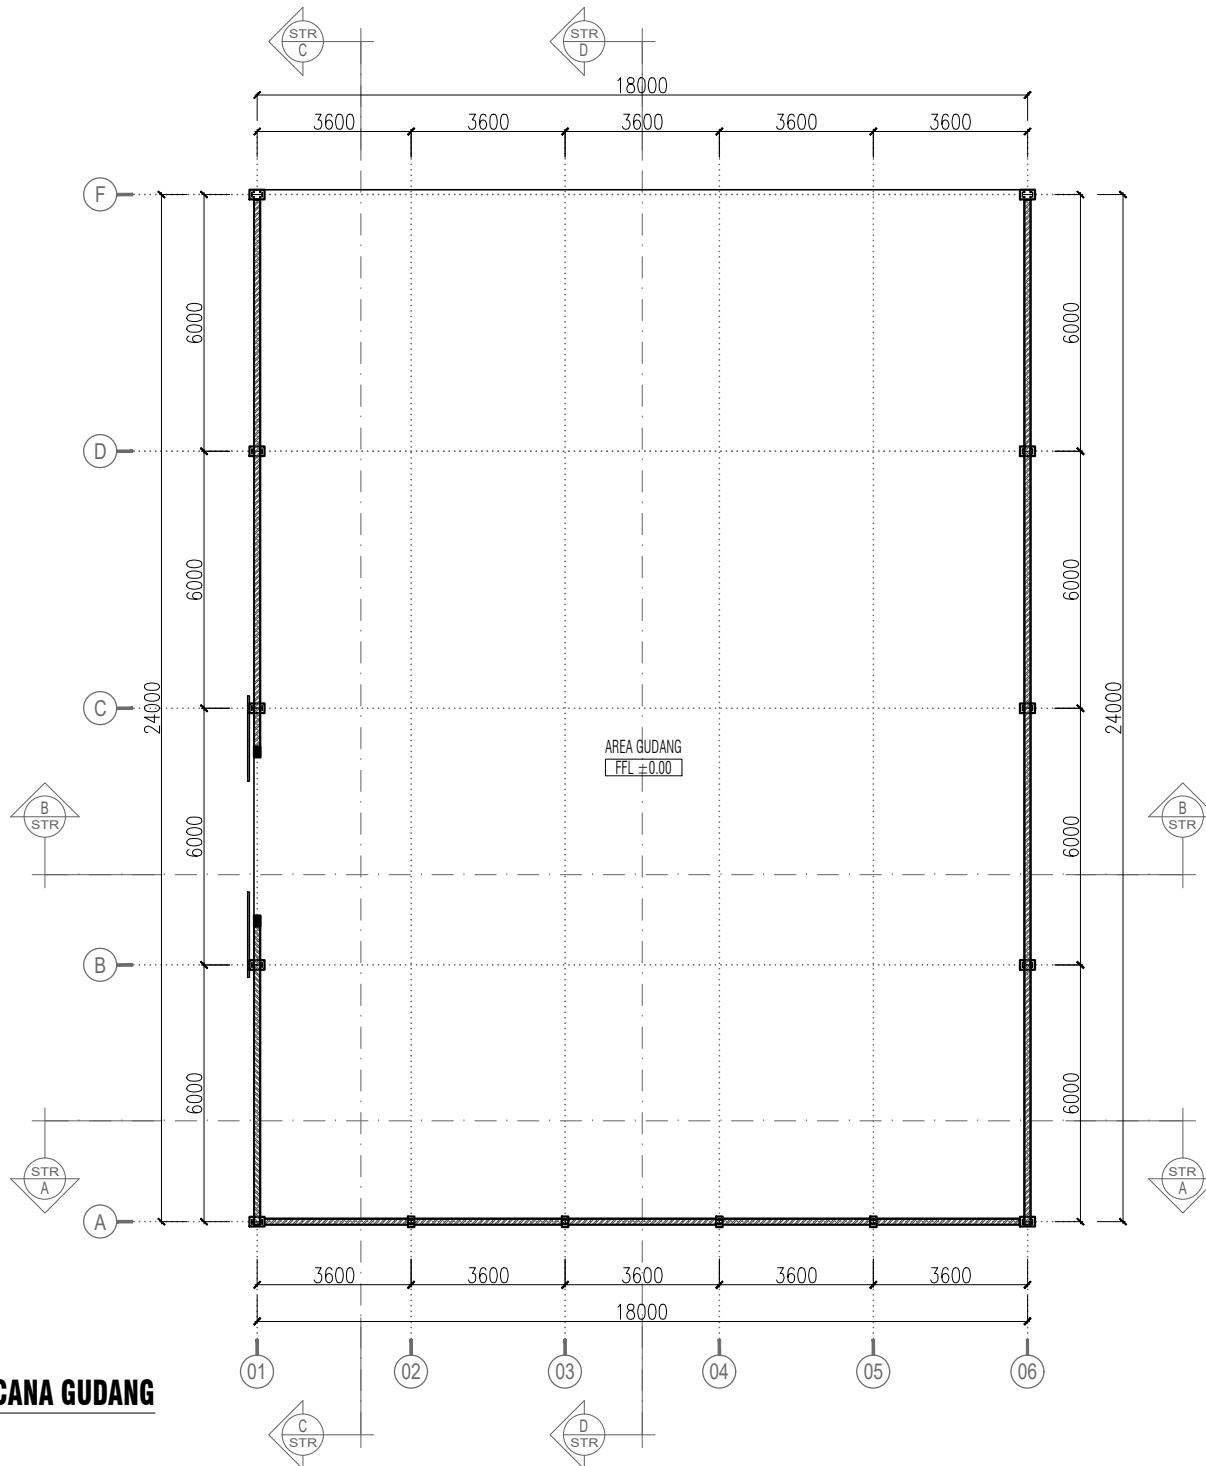


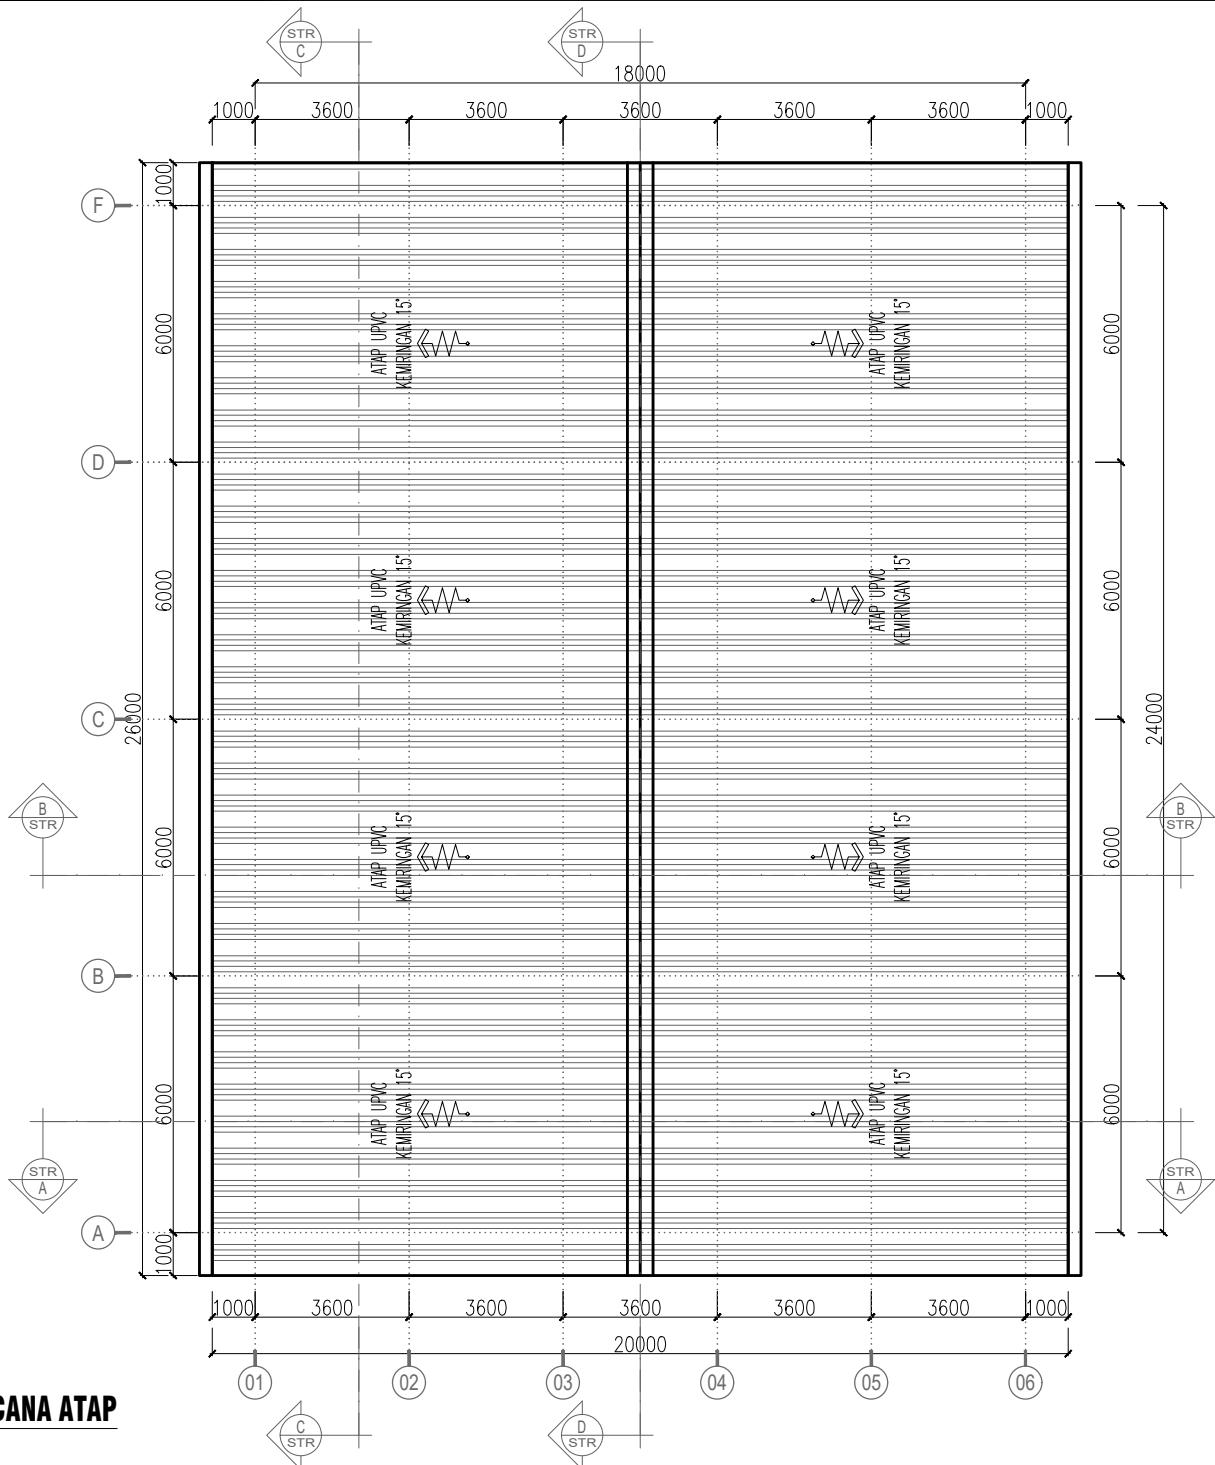


NAMA PROYEK	
<b>PROJECT GUDANG</b> PT. JOJOPLAST GEMILANG	
LOKASI PROYEK	
jl. Raya Sawocangkring no.102 <b>Wonoayu, Sidoarjo - JATIM</b>	
PENANGGUNG JAWAB	
DIGAMBAR	PELAKSANA
DISETUJU	PEMILIK
CATATAN	
1. PELAKSANA ATAU SUBKON WAJIB MEMERIKSA KEMBALI KESESUAIN GAMBAR DENGAN KONDISI LAPANGAN	
JUDUL GAMBAR	SKALA
SKALA 1 : 50	
TANGGAL :	REVISI :
15 NOVEMBER 2024	<b>R1</b>
KODE GAMBAR	
<b>STR-03-05</b>	
NO. LBR	JUMLAH LBR
05	33

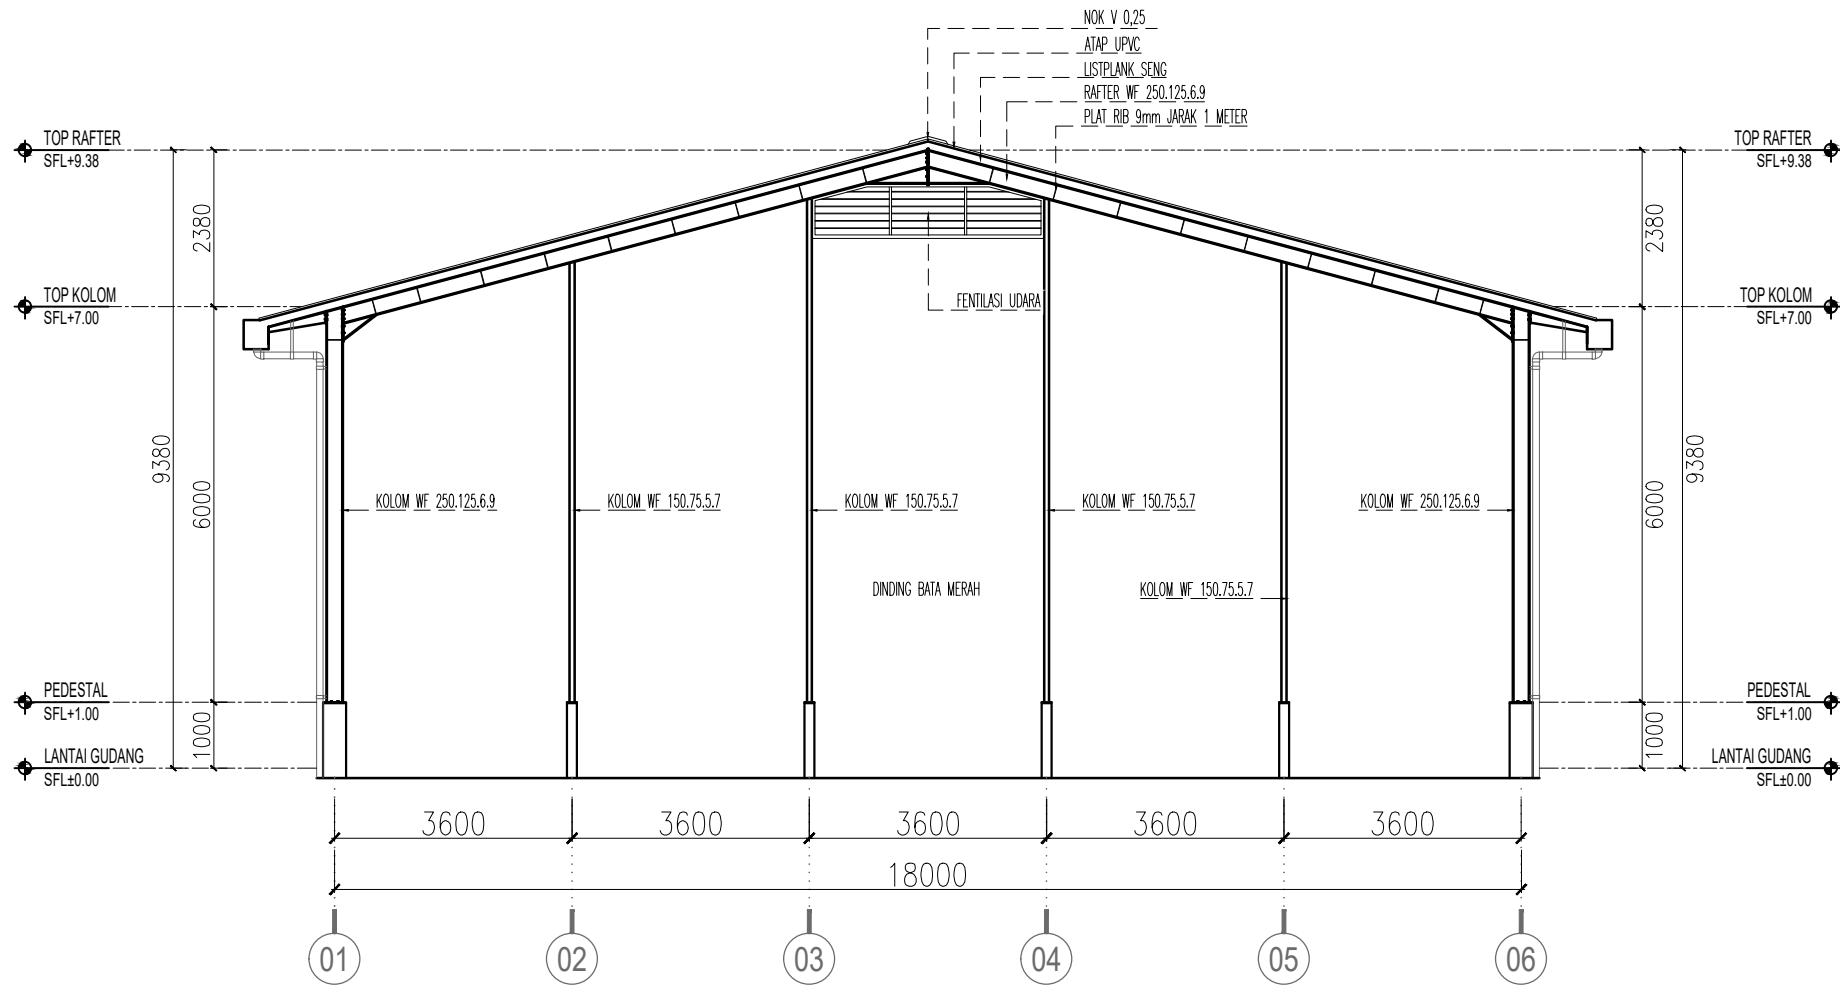

NAMA PROYEK	
<b>PROJECT GUDANG</b> PT. JOJOPLAST GEMILANG	
LOKASI PROYEK	
jl. Raya Sawocangkring no.102 <b>Wonoayu, Sidoarjo - JATIM</b>	
PENANGGUNG JAWAB	
DIGAMBAR	PELAKSANA
DISETUJU	PEMILIK
CATATAN	
1. PELAKSANA ATAU SUBKON WAJIB MEMERIKSA KEMBALI KESESUAIN GAMBAR DENGAN KONDISI LAPANGAN	
JUDUL GAMBAR	SKALA
TANGGAL :	REVISI :
15 NOVEMBER 2024	<b>R1</b>
KODE GAMBAR	
<b>STR-03-06</b>	
NO. LBR	JUMLAH LBR
06	33

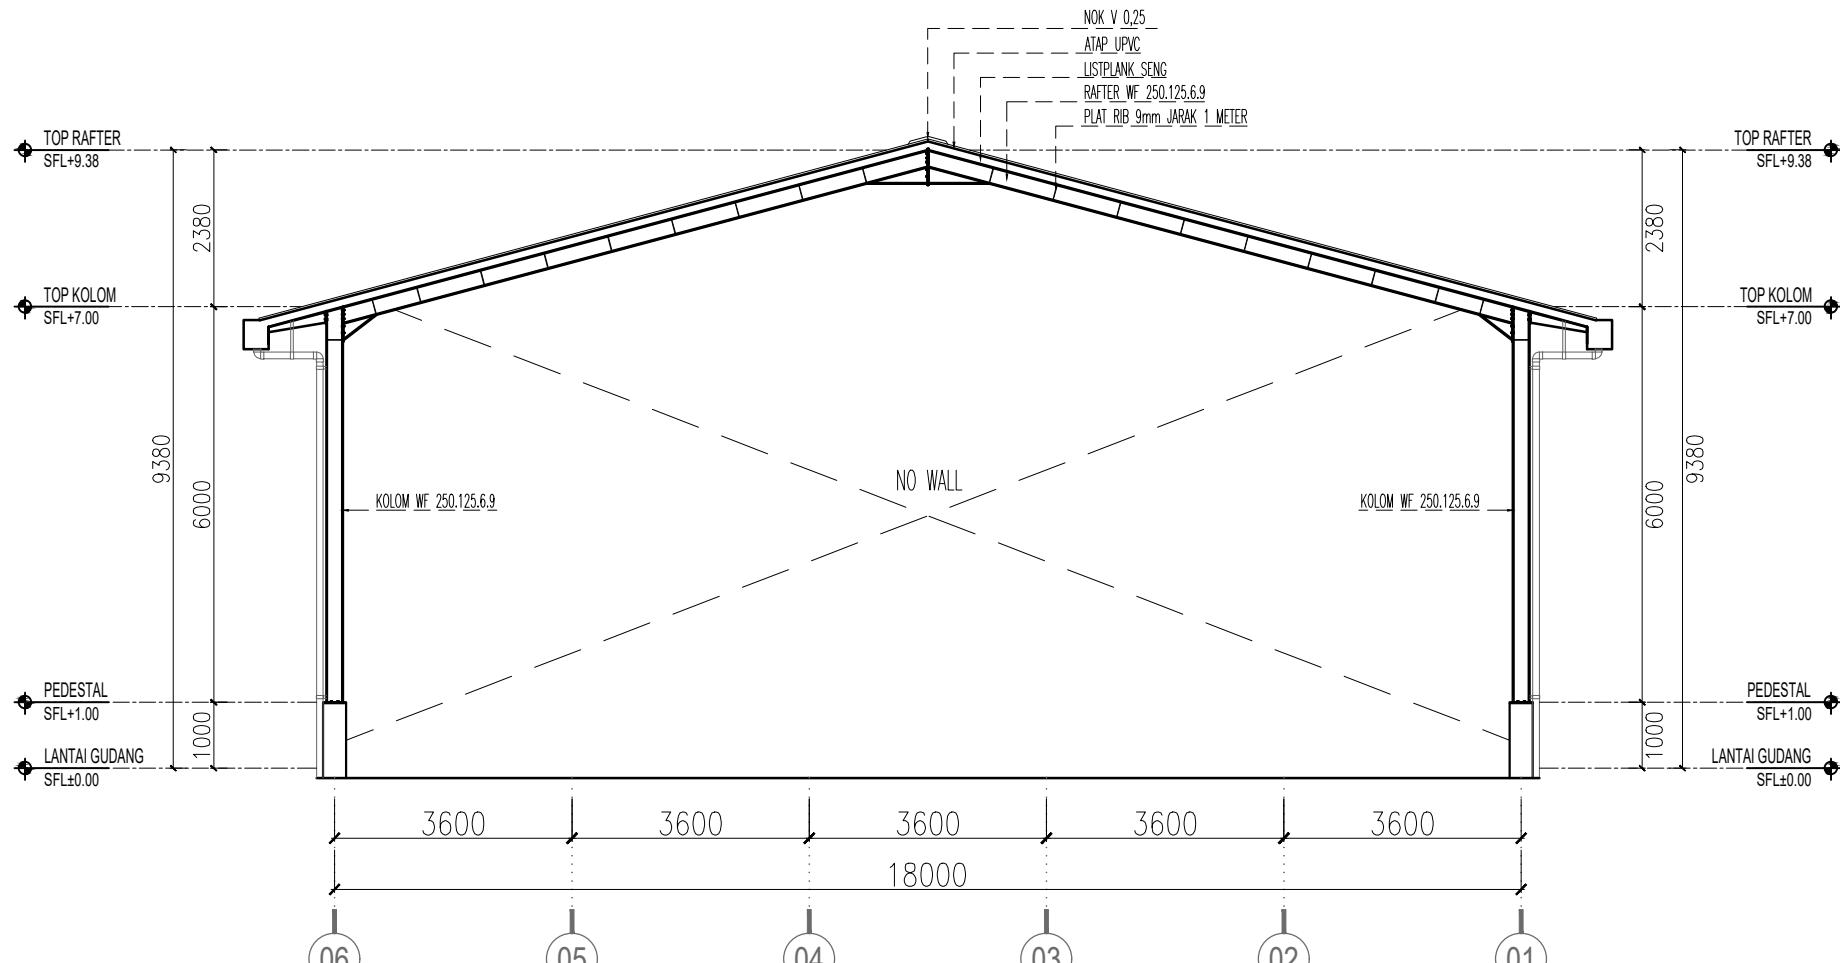


NAMA PROYEK	
<b>PROJECT GUDANG</b> PT. JOJOPLAST GEMILANG	
LOKASI PROYEK	
jl. Raya Sawocangkring no.102 <b>Wonoayu, Sidoarjo - JATIM</b>	
PENANGGUNG JAWAB	
DIGAMBAR	PELAKSANA
DISETUJU	PEMILIK
CATATAN	
1. PELAKSANA ATAU SUBKON WAJIB MEMERIKSA KEMBALI KESESUAIN GAMBAR DENGAN KONDISI LAPANGAN	
JUDUL GAMBAR	SKALA
TANGGAL :	REVISI :
15 NOVEMBER 2024	<b>R1</b>
KODE GAMBAR	
<b>STR-03-07</b>	
NO. LBR	JUMLAH LBR
07	33

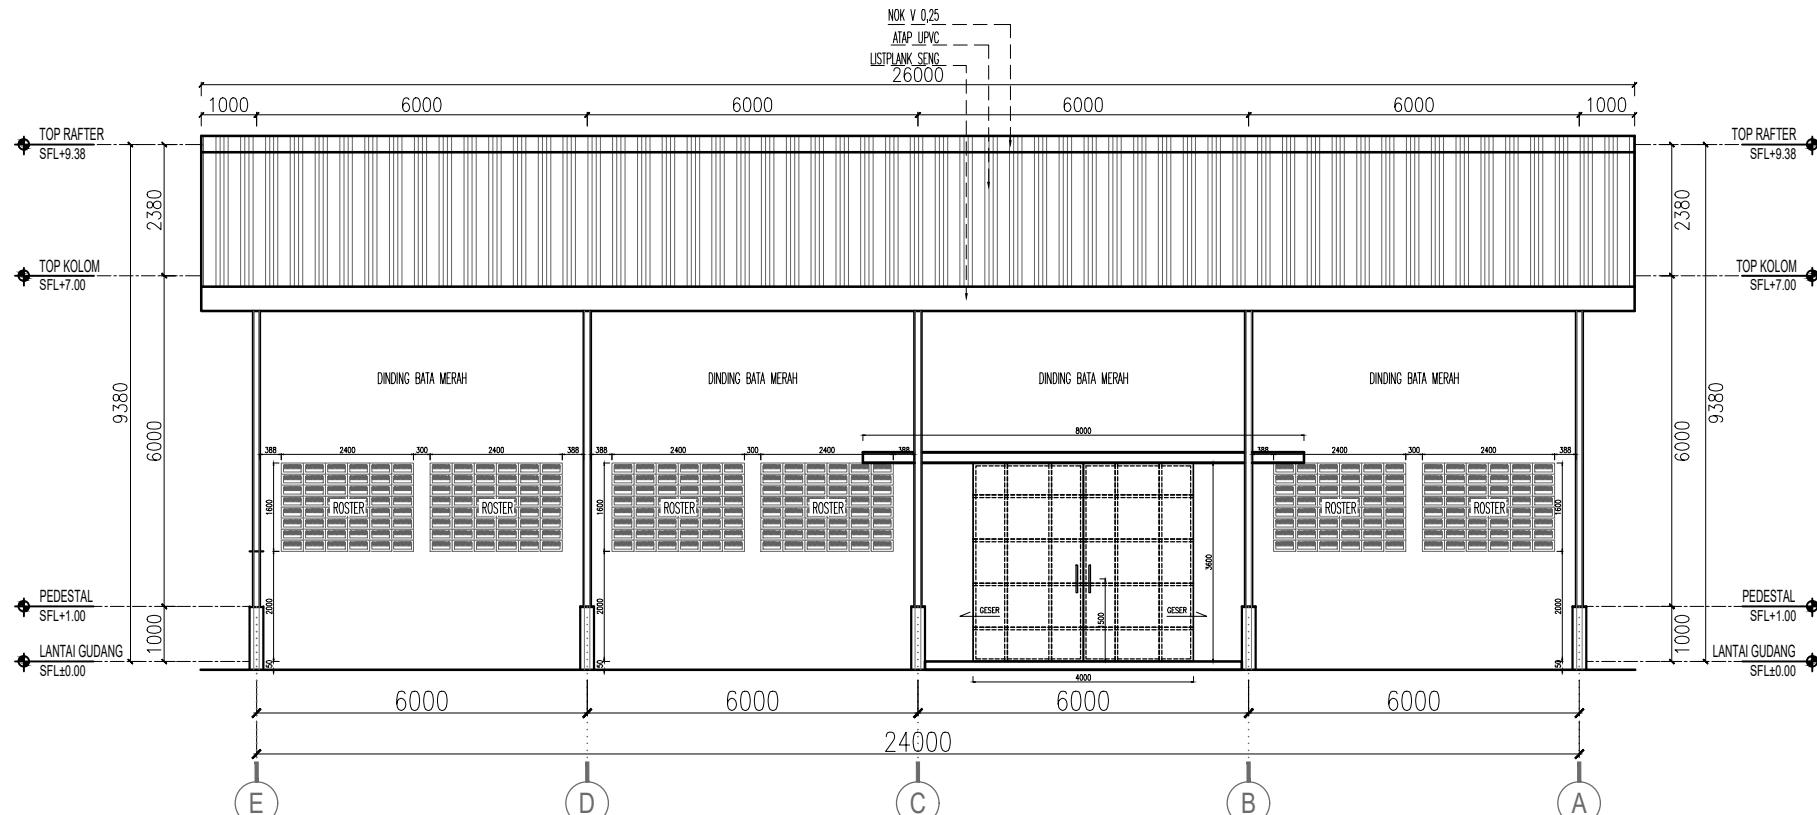


**TAMPAK SAMPING KIRI**  
SKALA 1 : 50

NAMA PROYEK	
<b>PROJECT GUDANG</b> PT. JOPLAST GEMILANG	
LOKASI PROYEK	
jl. Raya Sawocangkring no.102 <b>Wonoayu, Sidoarjo - JATIM</b>	
PENANGGUNG JAWAB	
DIGAMBAR	PELAKSANA
DISETUJU	PEMILIK
CATATAN	
1. PELAKSANA ATAU SUBKON WAJIB MEMERIKSA KEMBALI KESESUAIN GAMBAR DENGAN KONDISI LAPANGAN	
JUDUL GAMBAR	SKALA
TANGGAL :	REVISI :
15 NOVEMBER 2024	<b>R1</b>
KODE GAMBAR	
<b>STR-03-08</b>	
NO. LBR	JUMLAH LBR
08	33

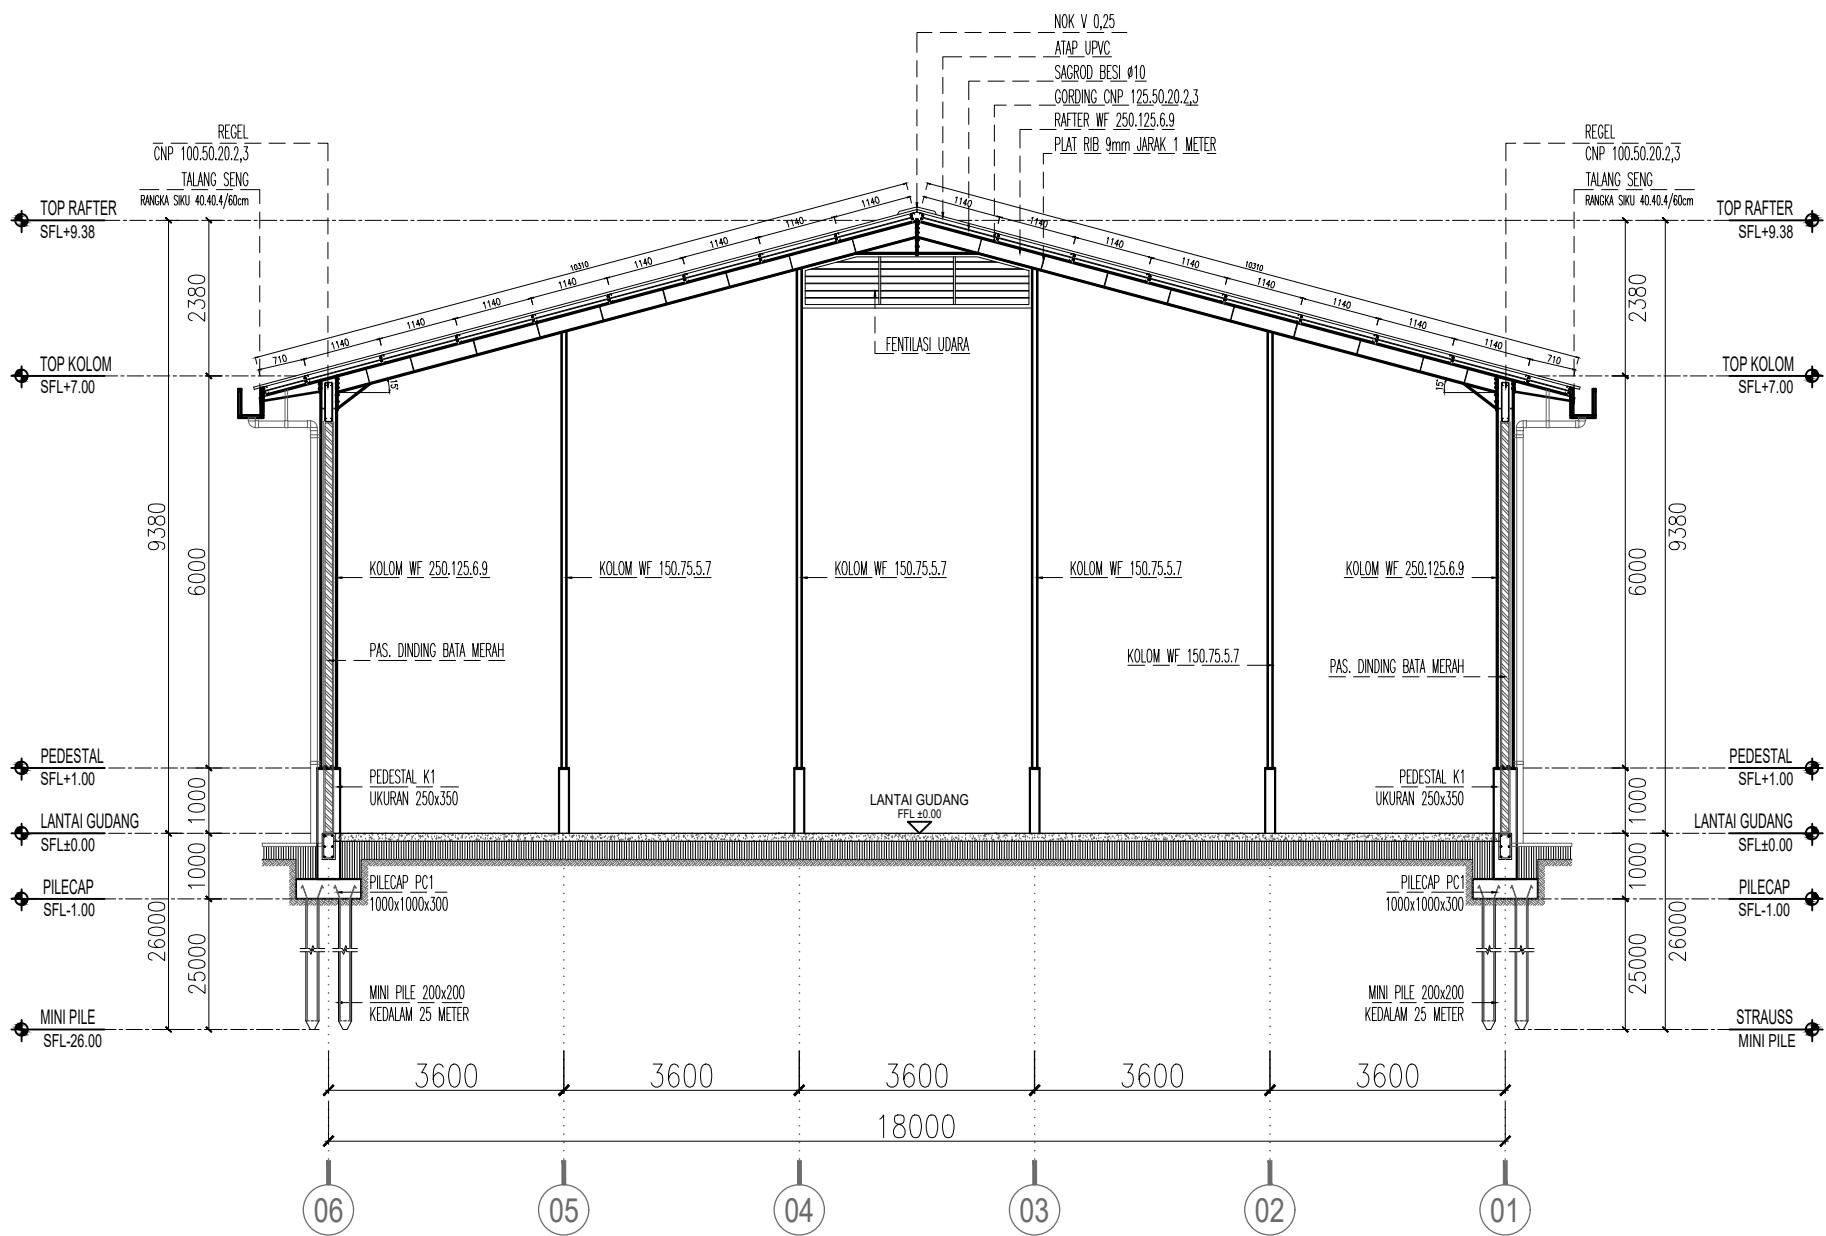



NAMA PROYEK	
<b>PROJECT GUDANG</b> PT. JOJOPLAST GEMILANG	
LOKASI PROYEK	
jl. Raya Sawangkring no.102 <b>Wonoayu, Sidoarjo - JATIM</b>	
PENANGGUNG JAWAB	
DIGAMBAR	PELAKSANA
DISETUJU	PEMILIK
CATATAN	
1. PELAKSANA ATAU SUBKON WAJIB MEMERIKSA KEMBALI KESESUAIN GAMBAR DENGAN KONDISI LAPANGAN	
JUDUL GAMBAR	SKALA
TANGGAL :	REVISI :
15 NOVEMBER 2024	R1
KODE GAMBAR	
STR-03-09	
NO. LBR	JUMLAH LBR
09	33

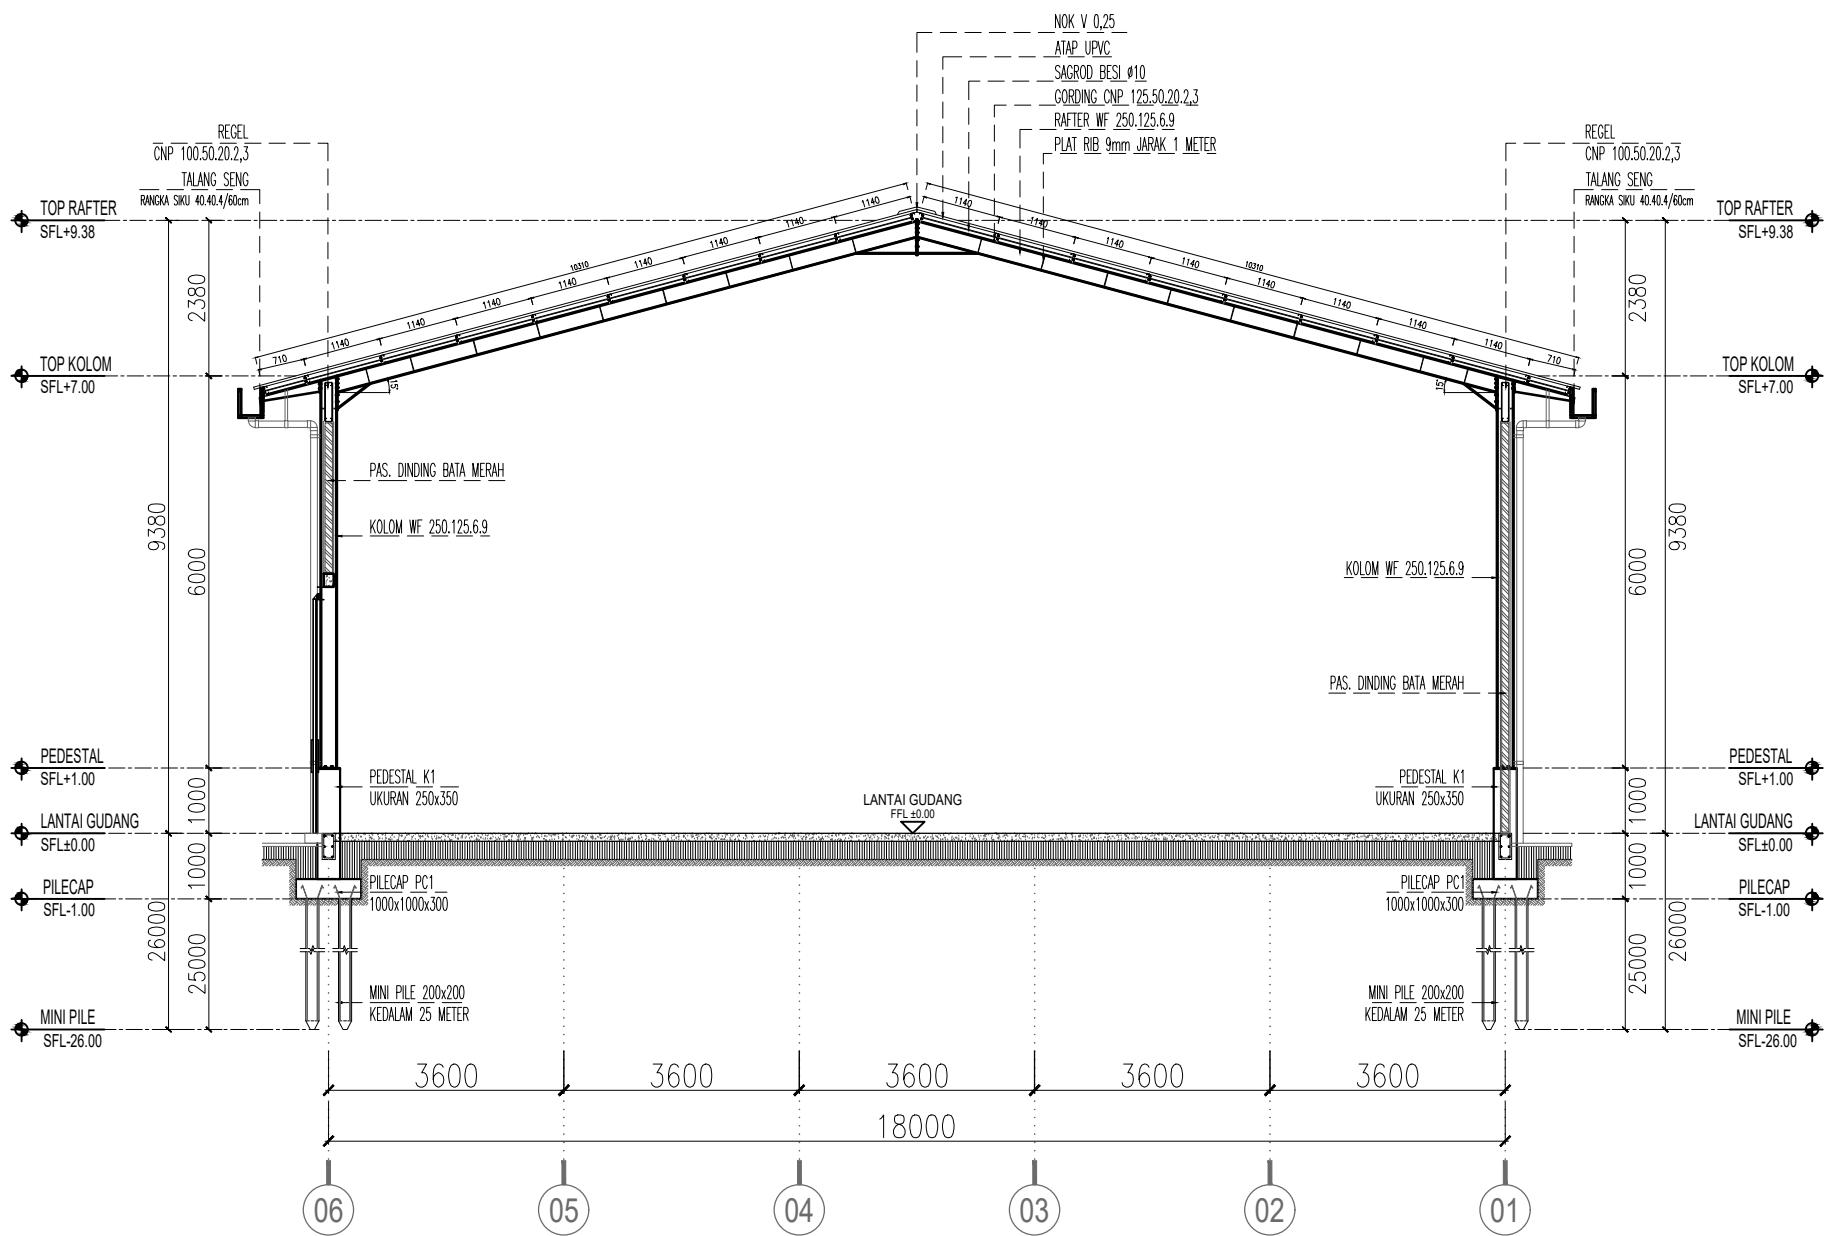

NAMA PROYEK	
<b>PROJECT GUDANG</b> PT. JOJOPLAST GEMILANG	
LOKASI PROYEK	
jl. Raya Sawangkring no.102 <b>Wonoayu, Sidoarjo - JATIM</b>	
PENANGGUNG JAWAB	
DIGAMBAR	PELAKSANA
DISETUJU	PEMILIK
CATATAN	
1. PELAKSANA ATAU SUBKON WAJIB MEMERIKSA KEMBALI KESESUAIN GAMBAR DENGAN KONDISI LAPANGAN	
JUDUL GAMBAR	SKALA
TANGGAL :	REVISI :
15 NOVEMBER 2024	<b>R1</b>
KODE GAMBAR	
STR-03-10	
NO. LBR	JUMLAH LBR
10	33

NAMA PROYEK	
<b>PROJECT GUDANG</b> PT. JOJOPLAST GEMILANG	
LOKASI PROYEK	
jl. Raya Sawocangkring no.102 <b>Wonoayu, Sidoarjo - JATIM</b>	
PENANGGUNG JAWAB	
DIGAMBAR	PELAKSANA
DISETUJU	PEMILIK
CATATAN	
1. PELAKSANA ATAU SUBKON WAJIB MEMERIKSA KEMBALI KESESUAIN GAMBAR DENGAN KONDISI LAPANGAN	
JUDUL GAMBAR	SKALA
TANGGAL :	REVISI :
15 NOVEMBER 2024	R1
KODE GAMBAR	
STR-03-11	
NO. LBR	JUMLAH LBR
11	33

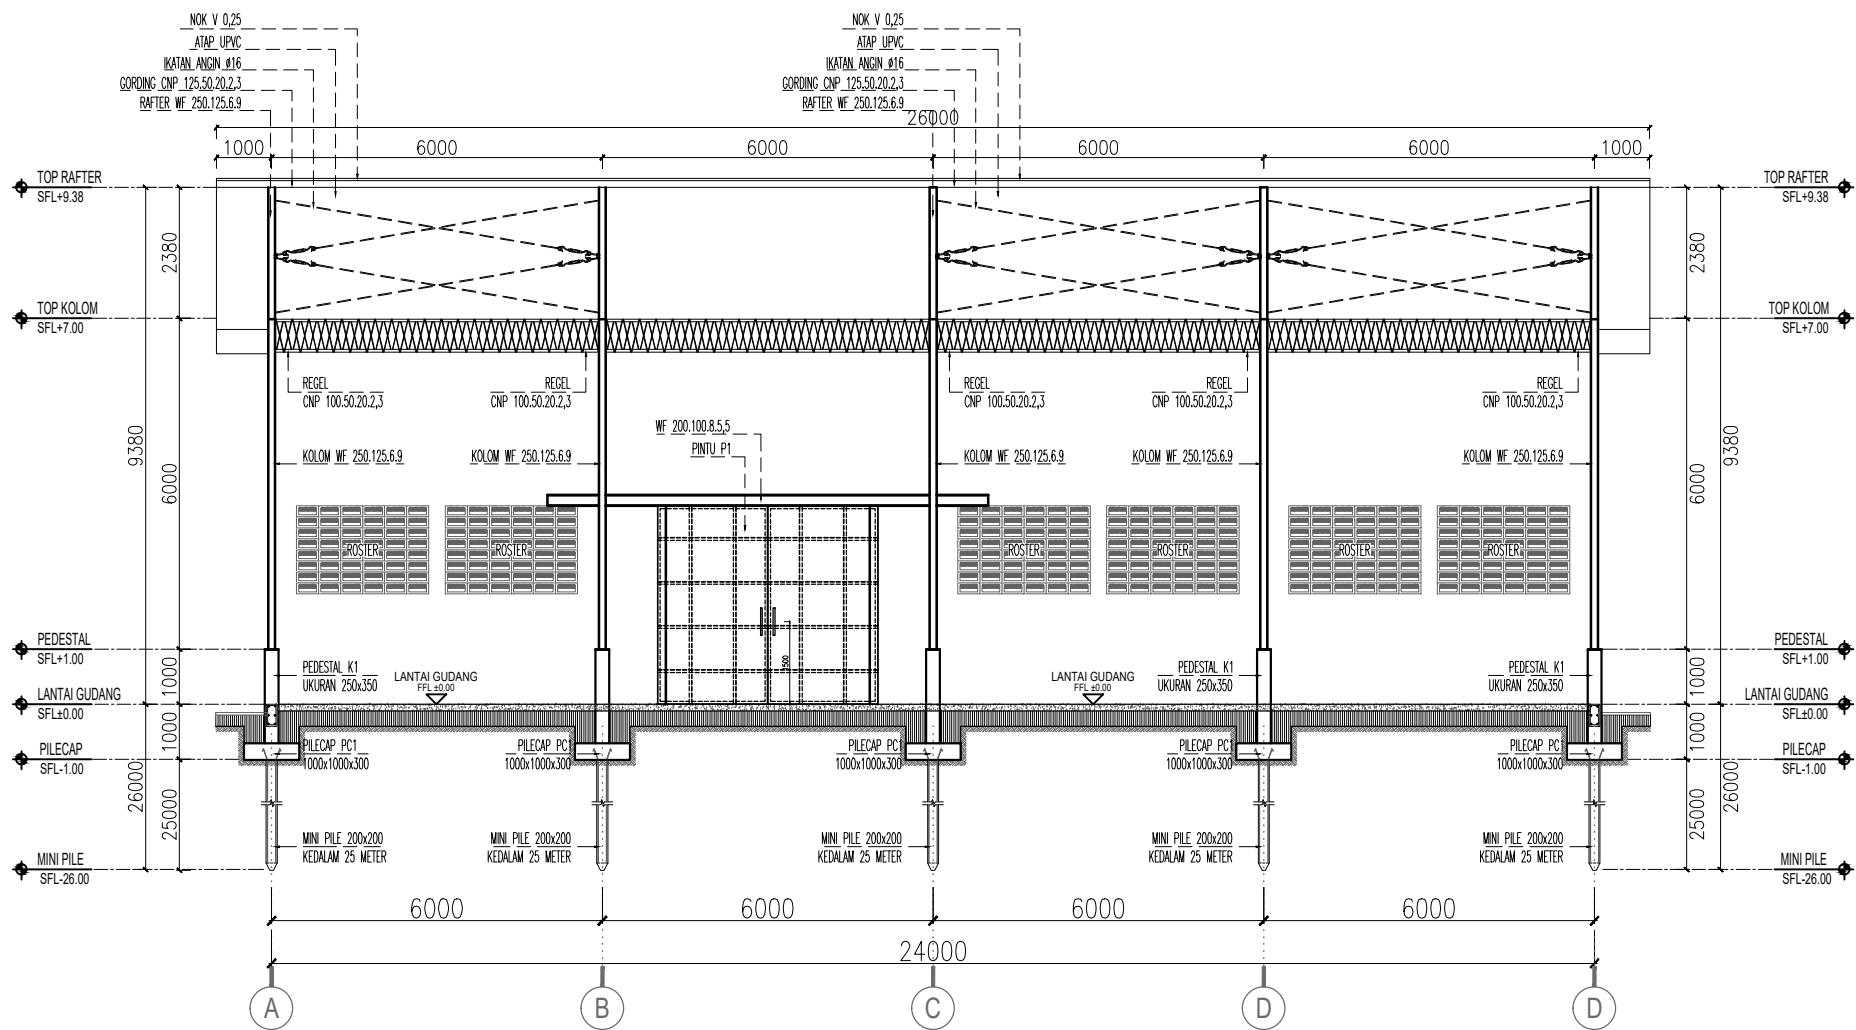

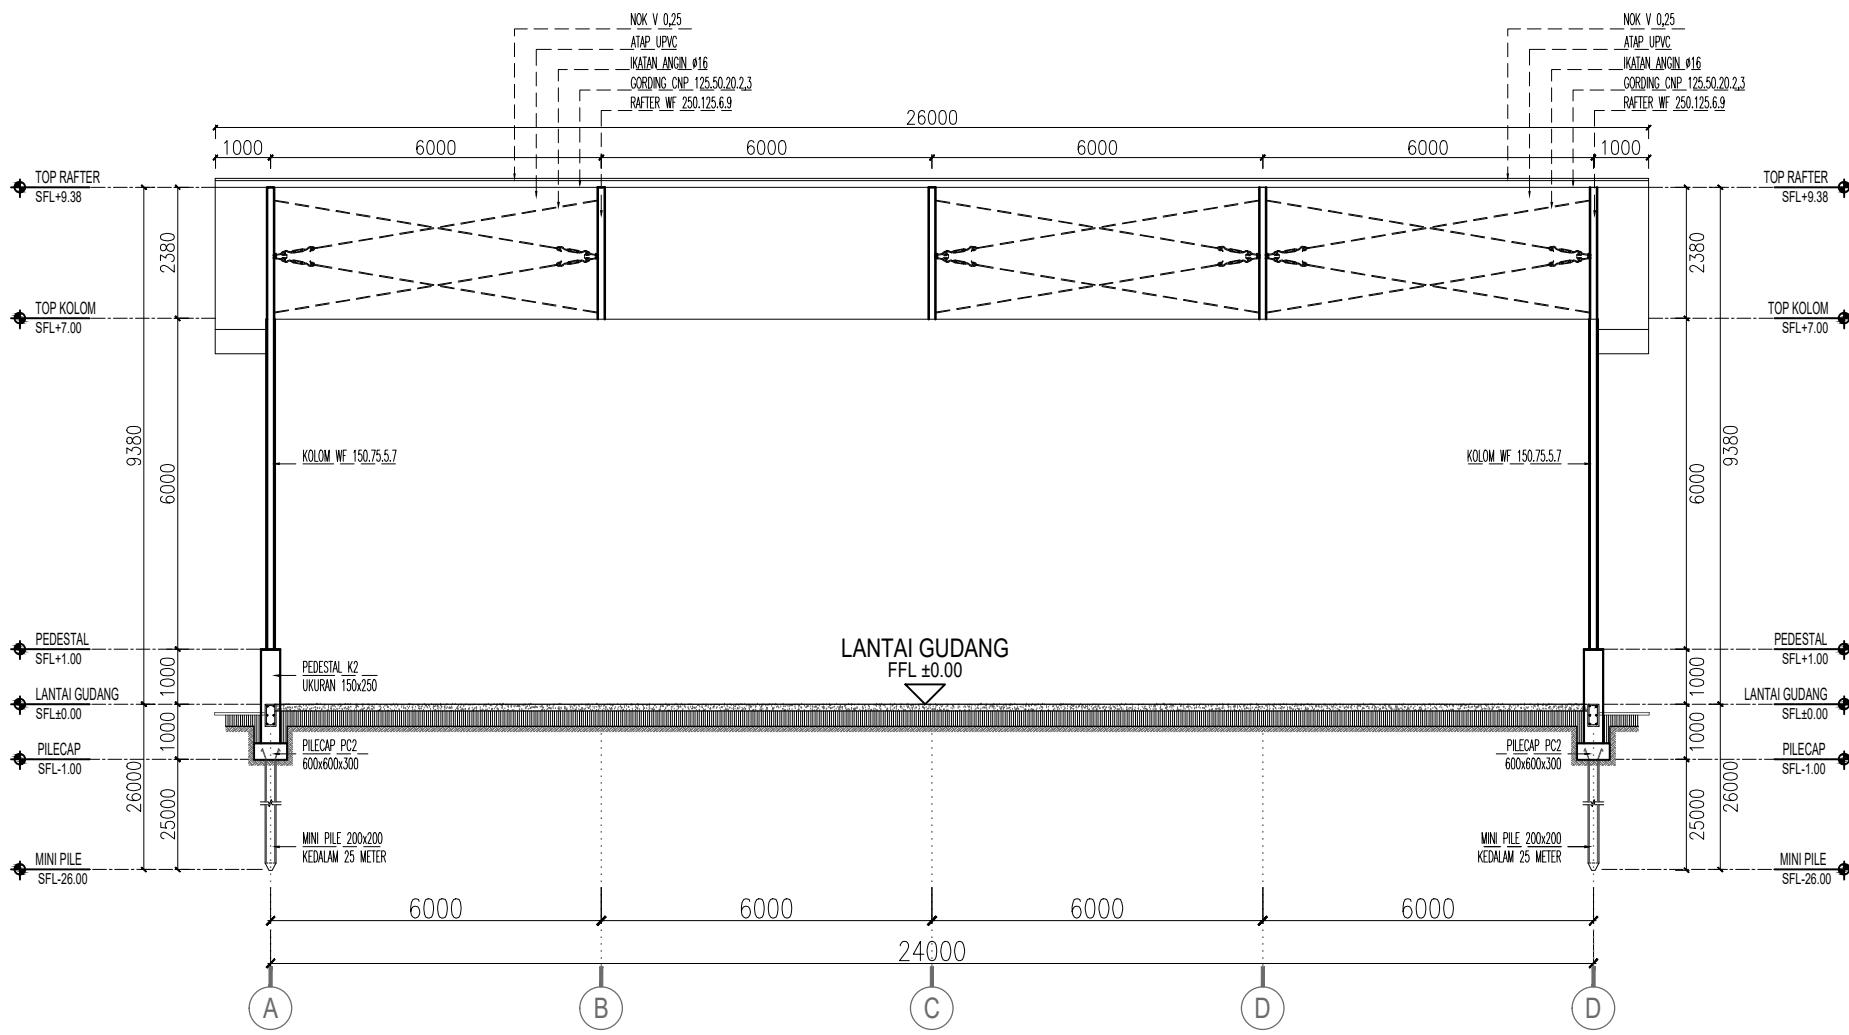


## POTONGAN D-D

SKALA 1 : 50

NAMA PROYEK	
<p style="text-align: center;"><b>PROJECT GUDANG</b></p> <p style="text-align: center;">PT. JOOPLAST GEMILANG</p>	
LOKASI PROYEK	
<p style="text-align: center;">jl. Raya Sawocangkring no.102</p> <p style="text-align: center;"><b>Wonoayu, Sidoarjo - JATIM</b></p>	
PENANGGUNG JAWAB	
<u>DIGAMBAR</u>	<u>PELAKSANA</u>
<u>DISETUJUI</u>	<u>PEMILIK</u>
CATATAN	
<p>1. PELAKSANA ATAU SUBKON WAJIB MEMERIKSA KEMBALI KESESUAIN GAMBAR DENGAN KONDISI LAPANGAN</p>	
JUDUL GAMBAR	SKALA
TANGGAL :	REVISI :
15 NOVEMBER 2024	<b>R1</b>
KODE GAMBAR	
STR-03-12	
NO. LBR	JUMLAH LBR
12	33


NAMA PROYEK	
<b>PROJECT GUDANG</b> PT. JOJOPLAST GEMILANG	
LOKASI PROYEK	
jl. Raya Sawocangkring no.102 <b>Wonoayu, Sidoarjo - JATIM</b>	
PENANGGUNG JAWAB	
DIGAMBAR	PELAKSANA
DISETUJU	PEMILIK
CATATAN	
1. PELAKSANA ATAU SUBKON WAJIB MEMERIKSA KEMBALI KESESUAIN GAMBAR DENGAN KONDISI LAPANGAN	
JUDUL GAMBAR	SKALA
TANGGAL :	REVISI :
15 NOVEMBER 2024	<b>R1</b>
KODE GAMBAR	
<b>STR-04-13</b>	
NO. LBR	JUMLAH LBR
13	33

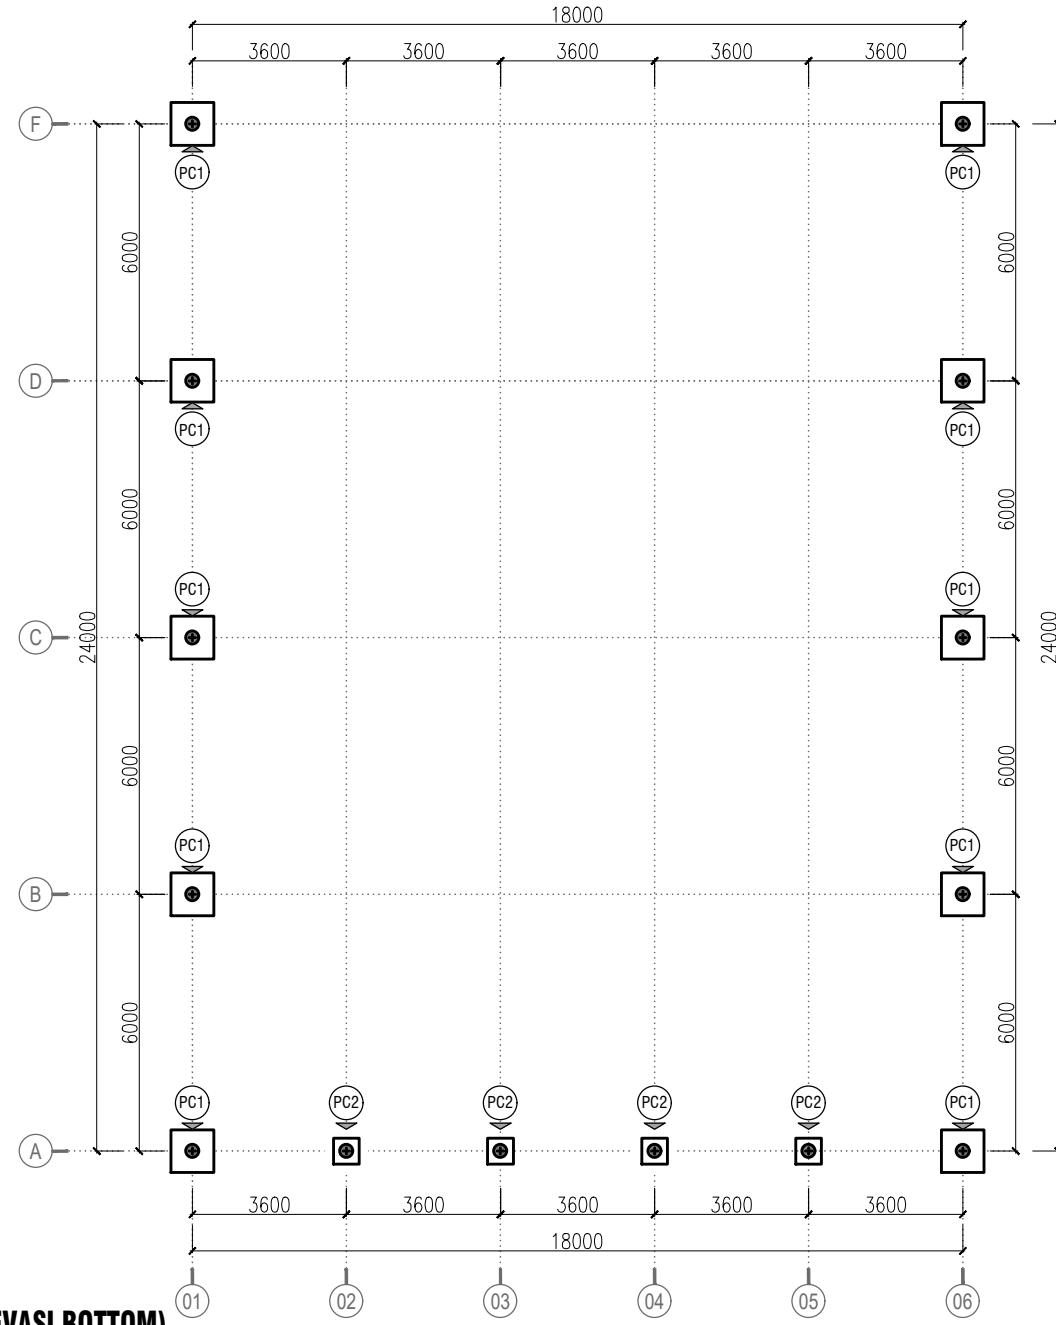

**DENAH PILECAP SFL-1.00 (ELEVASI BOTTOM)**

SKALA 1 : 100


NAMA PROYEK	
<b>PROJECT GUDANG</b> PT. JOJOPLAST GEMILANG	
LOKASI PROYEK	
jl. Raya Sawocangkring no.102 <b>Wonoayu, Sidoarjo - JATIM</b>	
PENANGGUNG JAWAB	
DIGAMBAR	PELAKSANA
DISETUJU	PEMILIK
CATATAN	
1. PELAKSANA ATAU SUBKON WAJIB MEMERIKSA KEMBALI KESESUAIN GAMBAR DENGAN KONDISI LAPANGAN	
JUDUL GAMBAR	SKALA
TANGGAL :	REVISI :
15 NOVEMBER 2024	<b>R1</b>
KODE GAMBAR	
<b>STR-04-14</b>	
NO. LBR	JUMLAH LBR
14	33

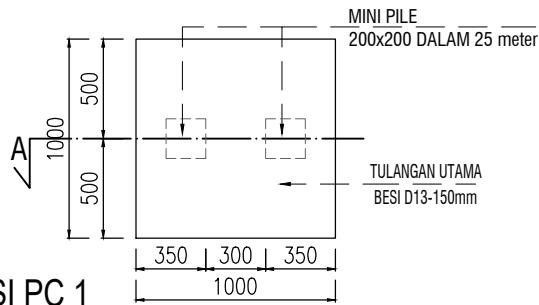

**DENAH PONDASI PC 1**

01  
AR-00-00

SKALA 1 : 25

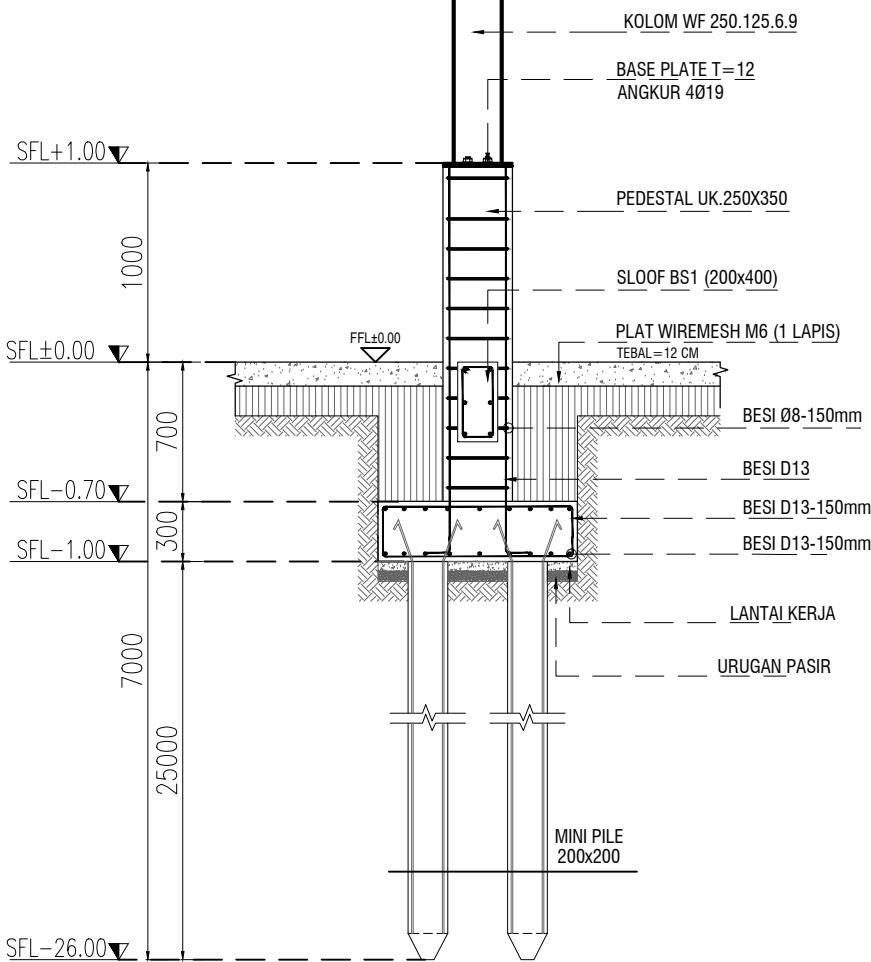


**POTONGAN A-A**

01  
AR-00-00


SKALA 1 : 25

250 500 250  
1000

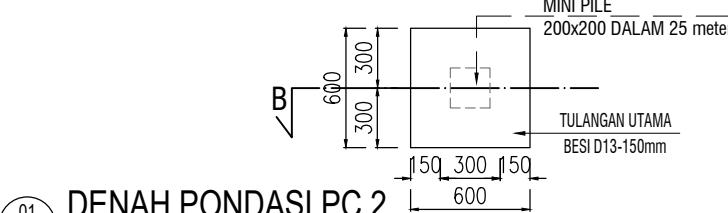

**DENAH PONDASI PC 2**

01  
AR-00-00 SKALA 1 : 25

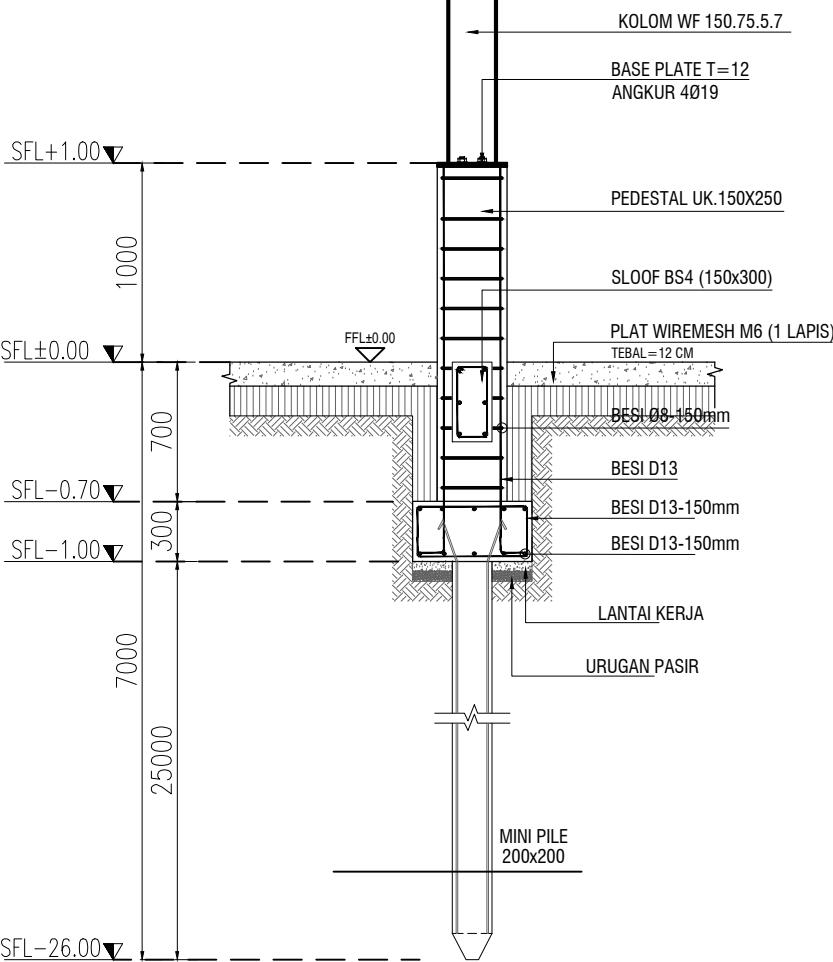


**POTONGAN B-B**

01  
AR-00-00 SKALA 1 : 25


14 33

NAMA PROYEK	
<b>PROJECT GUDANG</b> PT. JOJOPLAST GEMILANG	
LOKASI PROYEK	
jl. Raya Sawocangkring no.102 <b>Wonoayu, Sidoarjo - JATIM</b>	
PENANGGUNG JAWAB	
DIGAMBAR	PELAKSANA
DISETUJU	PEMILIK
CATATAN	
1. PELAKSANA ATAU SUBKON WAJIB MEMERIKSA KEMBALI KESESUAIN GAMBAR DENGAN KONDISI LAPANGAN	
JUDUL GAMBAR	SKALA
TANGGAL :	REVISI :
15 NOVEMBER 2024	<b>R1</b>
KODE GAMBAR	
<b>STR-04-15</b>	
NO. LBR	JUMLAH LBR
15	33

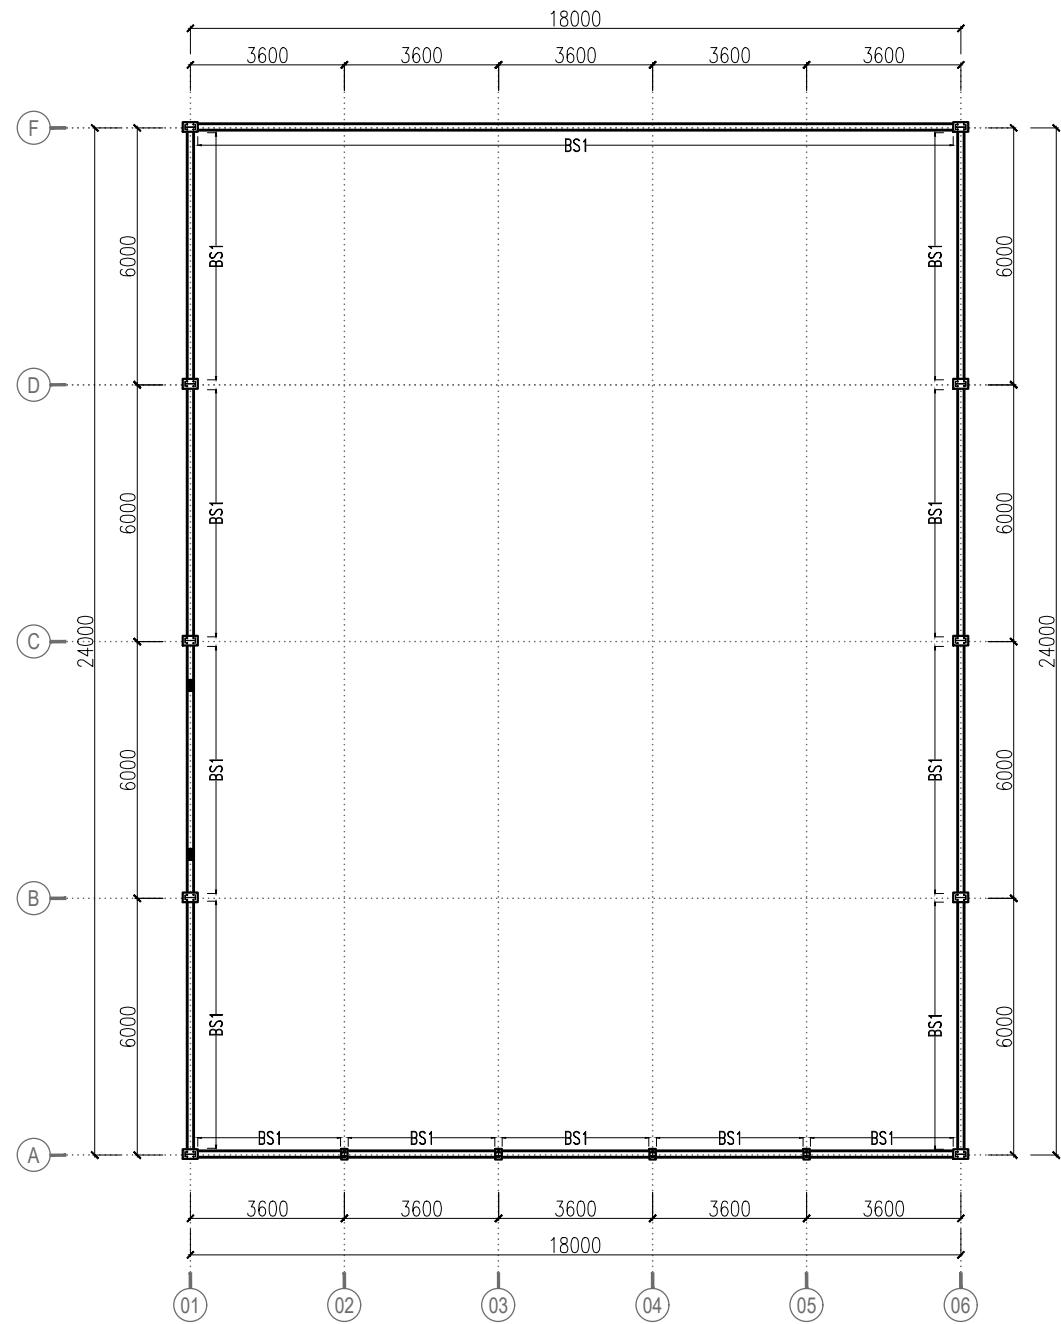

DETAIL PENULANGAN SLOOR		
KODE SLOOR	BS1	
	TUMPAN	LAPANGAN
	400	400
	200	200
DIMENSI	200x400	200x400
TULANGAN ATAS	2013	2013
TULANGAN TENGAH	2013	2013
TULANGAN BAWAH	2013	2013
SENGKANG	Ø8-150	Ø8-150




NAMA PROYEK	
<b>PROJECT GUDANG</b> PT. JOJOPLAST GEMILANG	
LOKASI PROYEK	
jl. Raya Sawangkring no.102 <b>Wonoayu, Sidoarjo - JATIM</b>	
PENANGGUNG JAWAB	
DIGAMBAR	PELAKSANA
DISETUJUJ	PEMILIK
CATATAN	
1. PELAKSANA ATAU SUBKON WAJIB MEMERIKSA KEMBALI KESESUAIN GAMBAR DENGAN KONDISI LAPANGAN	
JUDUL GAMBAR	SKALA
STR-04-16	
TANGGAL :	REVISI :
15 NOVEMBER 2024	<b>R1</b>
KODE GAMBAR	
<b>STR-04-16</b>	
NO. LBR	JUMLAH LBR
16	33

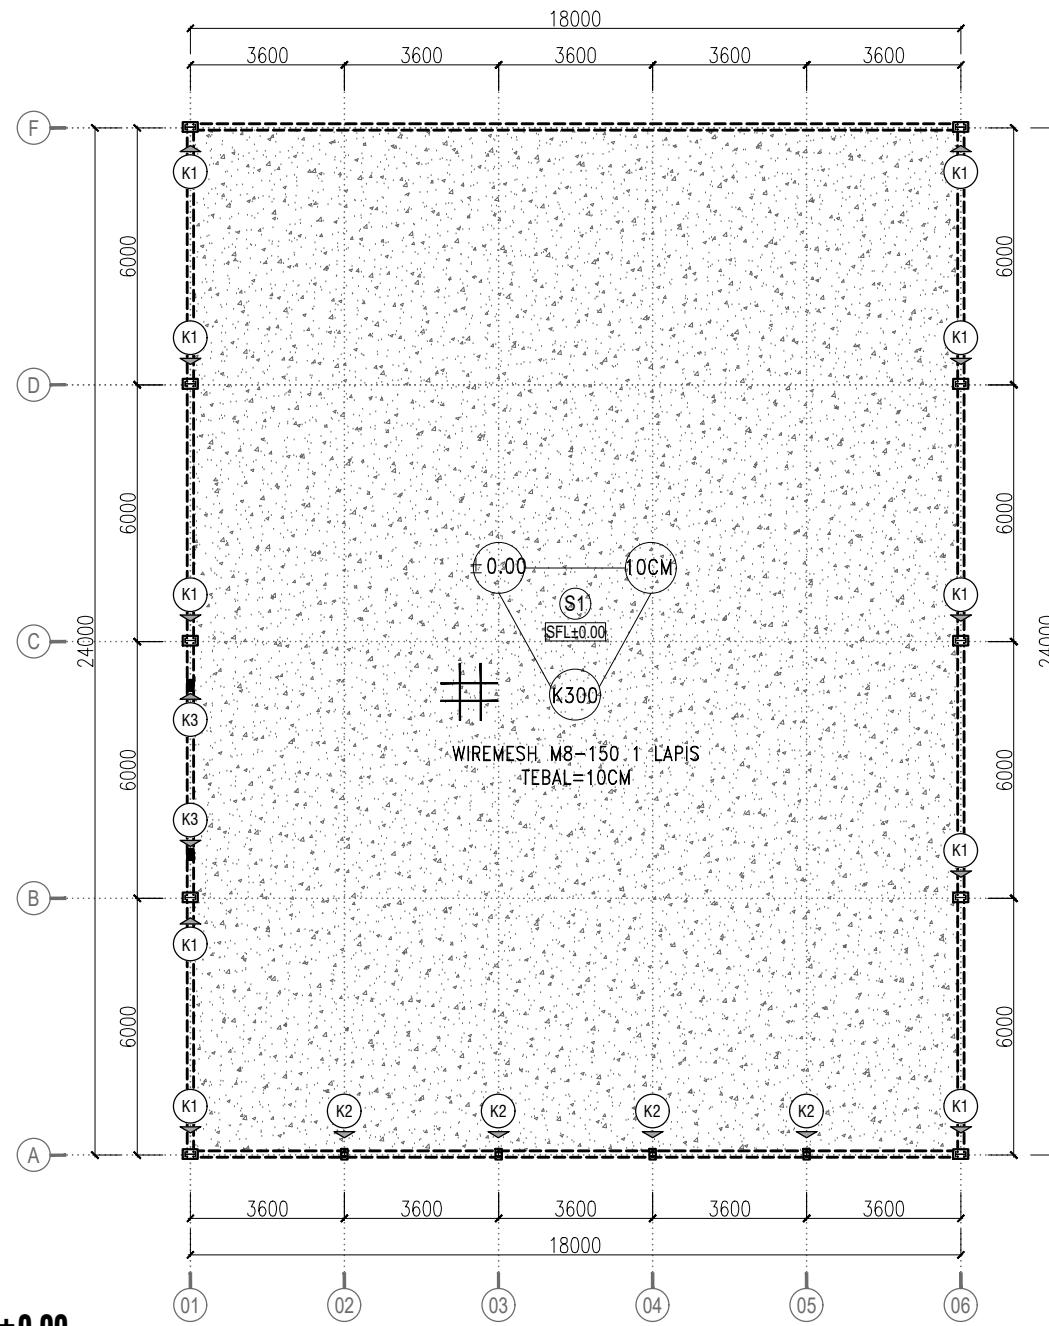


NAMA PROYEK	
<b>PROJECT GUDANG</b> PT. JOJOPLAST GEMILANG	
LOKASI PROYEK	
jl. Raya Sawocangkring no.102 <b>Wonoayu, Sidoarjo - JATIM</b>	
PENANGGUNG JAWAB	
DIGAMBAR	PELAKSANA
DISETUJUJ	PEMILIK
CATATAN	
1. PELAKSANA ATAU SUBKON WAJIB MEMERIKSA KEMBALI KESESUAIN GAMBAR DENGAN KONDISI LAPANGAN	
JUDUL GAMBAR	SKALA
TANGGAL :	REVISI :
15 NOVEMBER 2024	<b>R1</b>
KODE GAMBAR	
<b>STR-04-17</b>	
NO. LBR	JUMLAH LBR
17	33

## DETAIL PENULANGAN SLOOF

## DETAIL PENULANGAN KOLOM

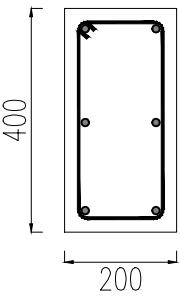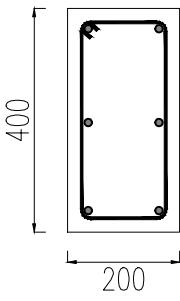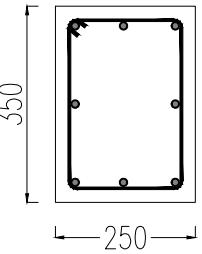
KODE SLOOF	BS1		KODE KOLOM	PEDESTAL K1	PEDESTAL K2	K3
	TUMPUAN	LAPANGAN				
						
DIMENSI	200x400	200x400		250x350	150x250	150x250
TULANGAN ATAS	2D13	2D13				
TULANGAN TENGAH	2D13	2D13	DIMENSI			
TULANGAN BAWAH	2D13	2D13	TULANGAN UTAMA	8D13	6D13	4D13
SENGKANG	Ø8-150	Ø8-150	SENGKANG	Ø8-150	Ø8-150	Ø8-150

## DETAIL KOLOM DAN BALOK SLOOF

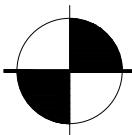

SKALA 1 : 5


NAMA PROYEK		
<b>PROJECT GUDANG</b> PT. JOJOPLAST GEMILANG		
LOKASI PROYEK		
jl. Raya Sawangkring no.102 <b>Wonoayu, Sidoarjo - JATIM</b>		
PENANGGUNG JAWAB		
DIGAMBAR	PELAKSANA	
DISETUJU	PEMILIK	
CATATAN		
1. PELAKSANA ATAU SUBKON WAJIB MEMERIKSA KEMBALI KESESUAIN GAMBAR DENGAN KONDISI LAPANGAN		
JUDUL GAMBAR	SKALA	
TANGGAL :	REVISI :	
15 NOVEMBER 2024	<b>R1</b>	
KODE GAMBAR		
<b>STR-04-18</b>		
NO	ITEM KOLOM	KETERANGAN
1.		KOLOM WF 250.125.6.9
2.		KOLOM WF 150.75.5.7
NO. LBR	JUMLAH LBR	
18	33	

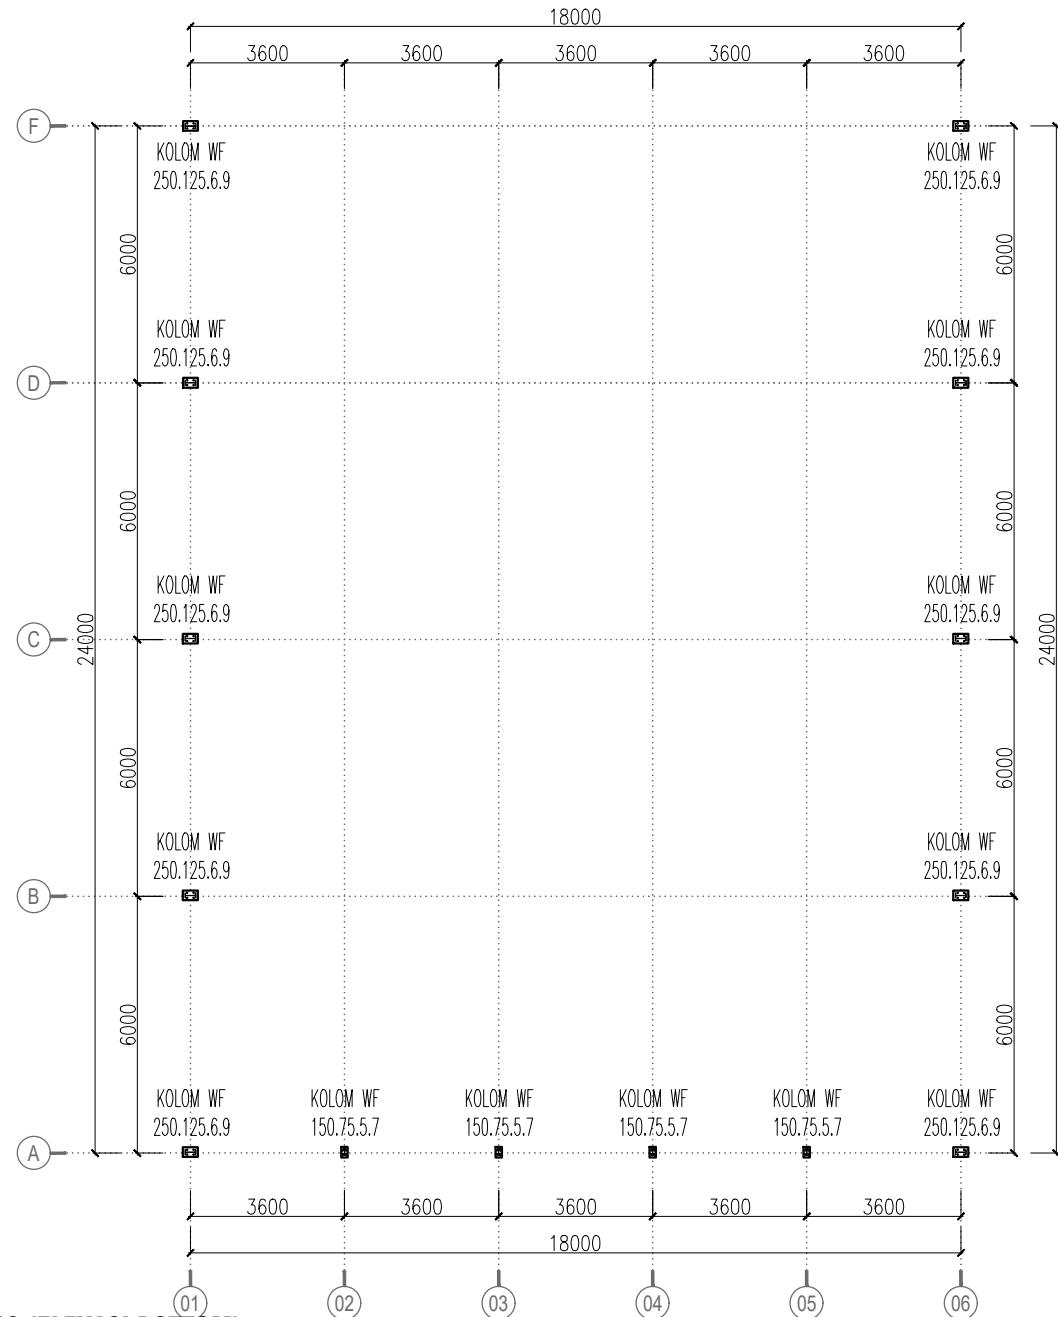

**DENAH KOLOM BAJA SFL+1.00 (ELEVASI BOTTOM)**



SKALA 1 : 100

NAMA PROYEK	
<b>PROJECT GUDANG</b> PT. JOJOPLAST GEMILANG	
LOKASI PROYEK	
jl. Raya Sawocangkring no.102 <b>Wonoayu, Sidoarjo - JATIM</b>	
PENANGGUNG JAWAB	
DIGAMBAR	PELAKSANA
DISETUJU	PEMILIK
CATATAN	
1. PELAKSANA ATAU SUBKON WAJIB MEMERIKSA KEMBALI KESESUAIN GAMBAR DENGAN KONDISI LAPANGAN	
JUDUL GAMBAR	SKALA
TANGGAL :	REVISI :
15 NOVEMBER 2024	<b>R1</b>
KODE GAMBAR	
<b>STR-04-19</b>	
NO. LBR	JUMLAH LBR
19	33

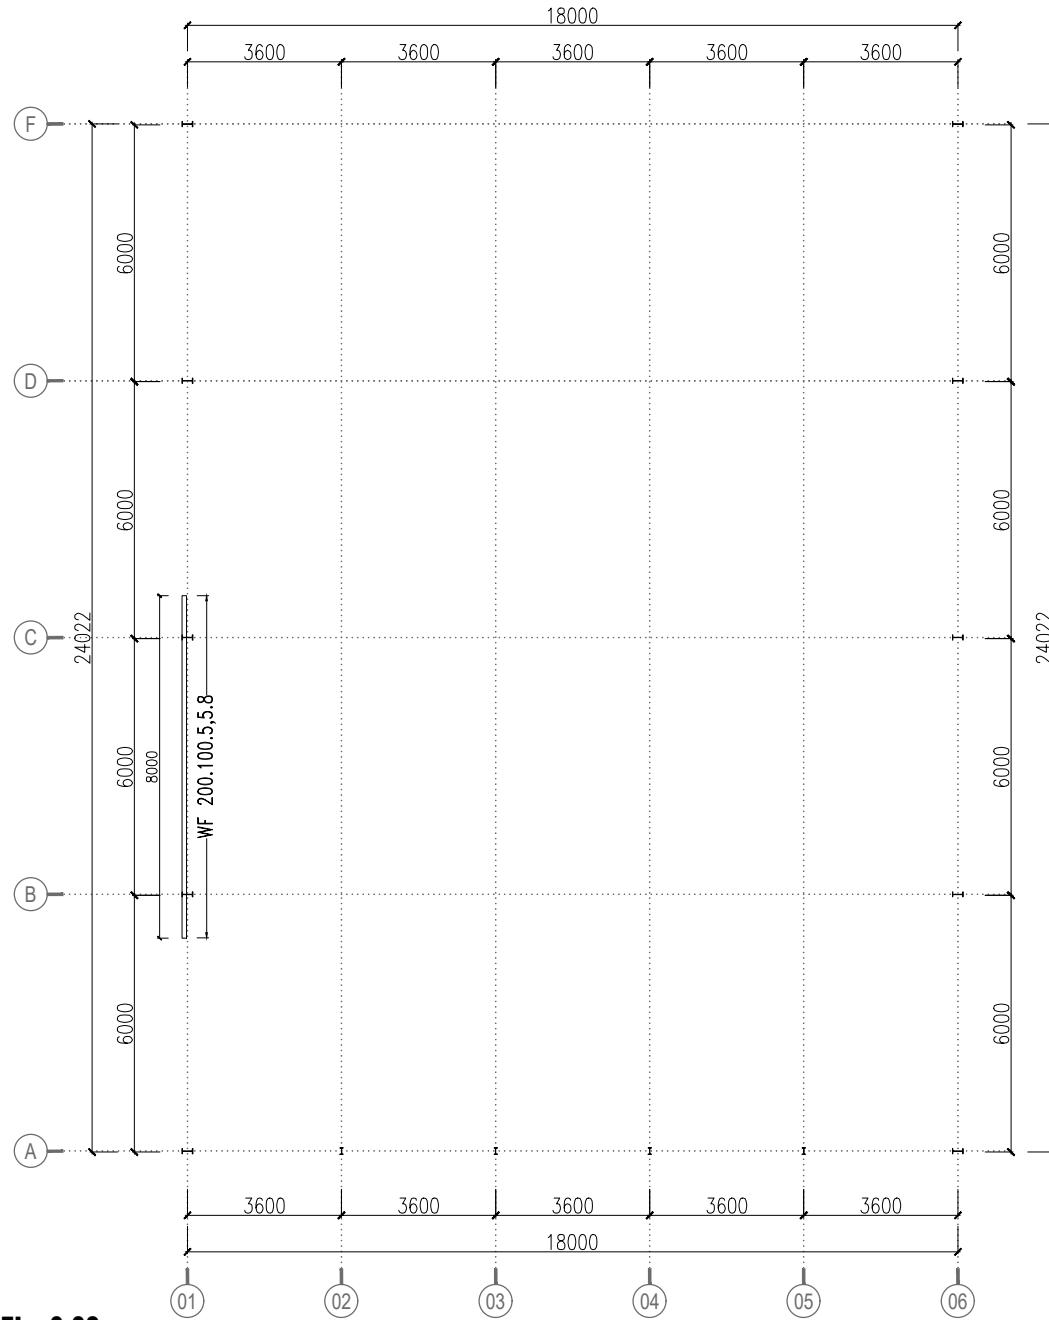


NO	ITEM BALOK	KETERANGAN
1.	I	BALOK WF 200.100.5,5.8

NAMA PROYEK	
<b>PROJECT GUDANG</b> PT. JOJOPLAST GEMILANG	
LOKASI PROYEK	
jl. Raya Sawocangkring no.102 <b>Wonoayu, Sidoarjo - JATIM</b>	
PENANGGUNG JAWAB	
DIGAMBAR	PELAKSANA
DISETUJU	PEMILIK
CATATAN	
1. PELAKSANA ATAU SUBKON WAJIB MEMERIKSA KEMBALI KESESUAIN GAMBAR DENGAN KONDISI LAPANGAN	
JUDUL GAMBAR	SKALA
TANGGAL :	REVISI :
15 NOVEMBER 2024	R1
KODE GAMBAR	
STR-04-20	
NO. LBR	JUMLAH LBR
20	33

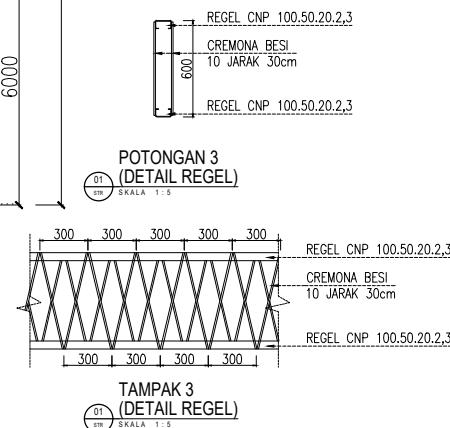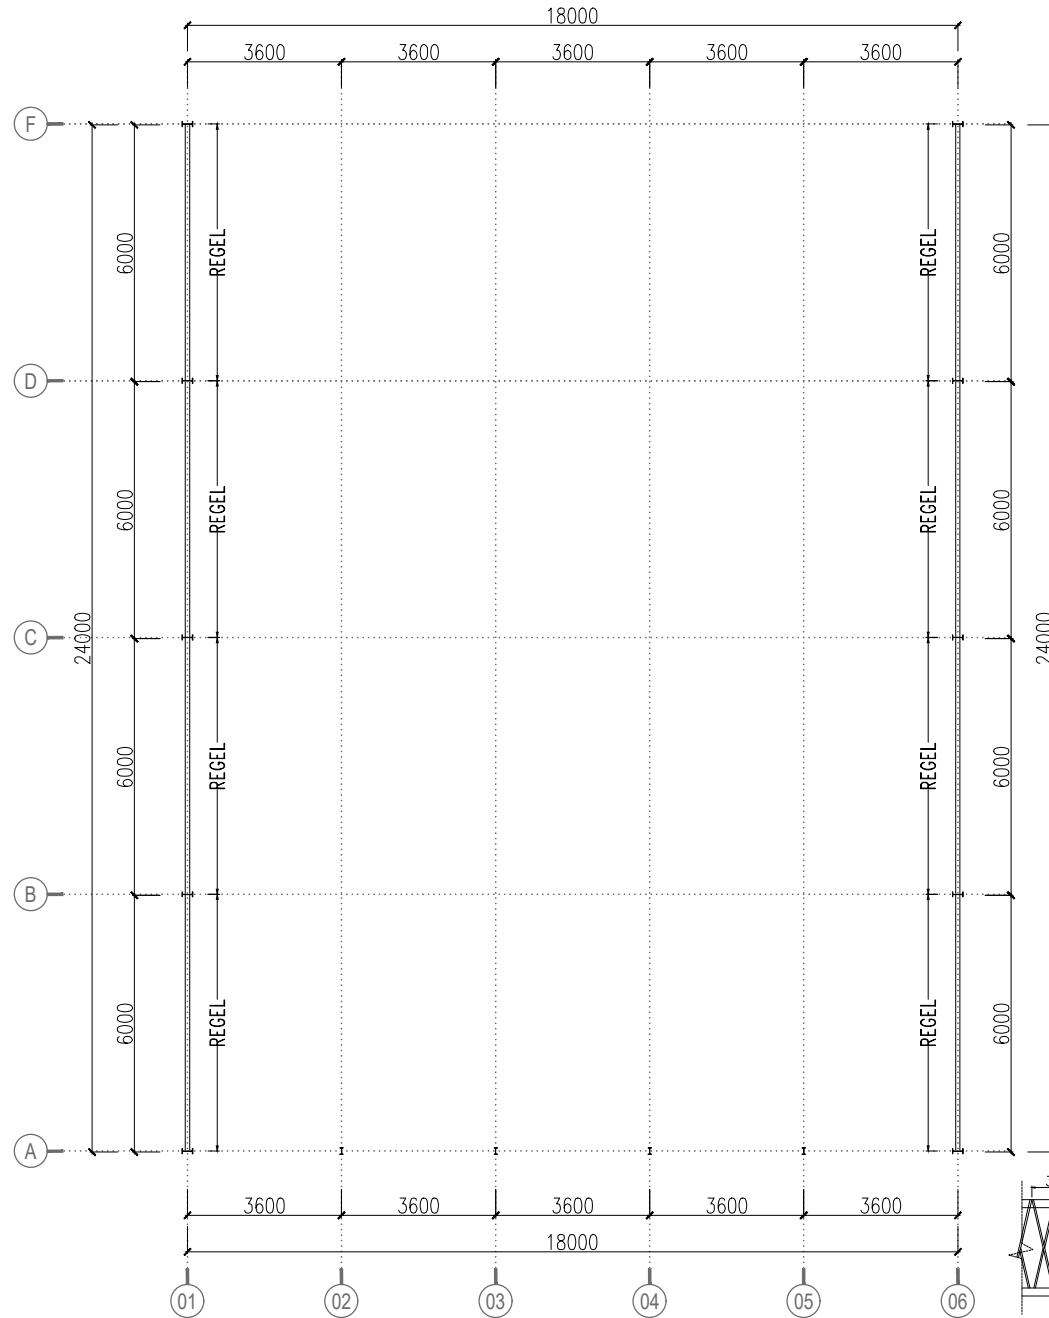


NAMA PROYEK		
<b>PROJECT GUDANG</b> PT. JOJOPLAST GEMILANG		
LOKASI PROYEK		
jl. Raya Sawangkring no.102 <b>Wonoayu, Sidoarjo - JATIM</b>		
PENANGGUNG JAWAB		
DIGAMBAR	PELAKSANA	
DISETUJU	PEMILIK	
CATATAN		
1. PELAKSANA ATAU SUBKON WAJIB MEMERIKSA KEMBALI KESESUAIN GAMBAR DENGAN KONDISI LAPANGAN		
JUDUL GAMBAR	SKALA	
TANGGAL :	REVISI :	
15 NOVEMBER 2024	R1	
KODE GAMBAR		
<b>STR-04-21</b>		
NO.	ITEM RAFTER	KETERANGAN
1.		KOLOM WF 250.125.6.9
NO. LBR	JUMLAH LBR	
21	33	

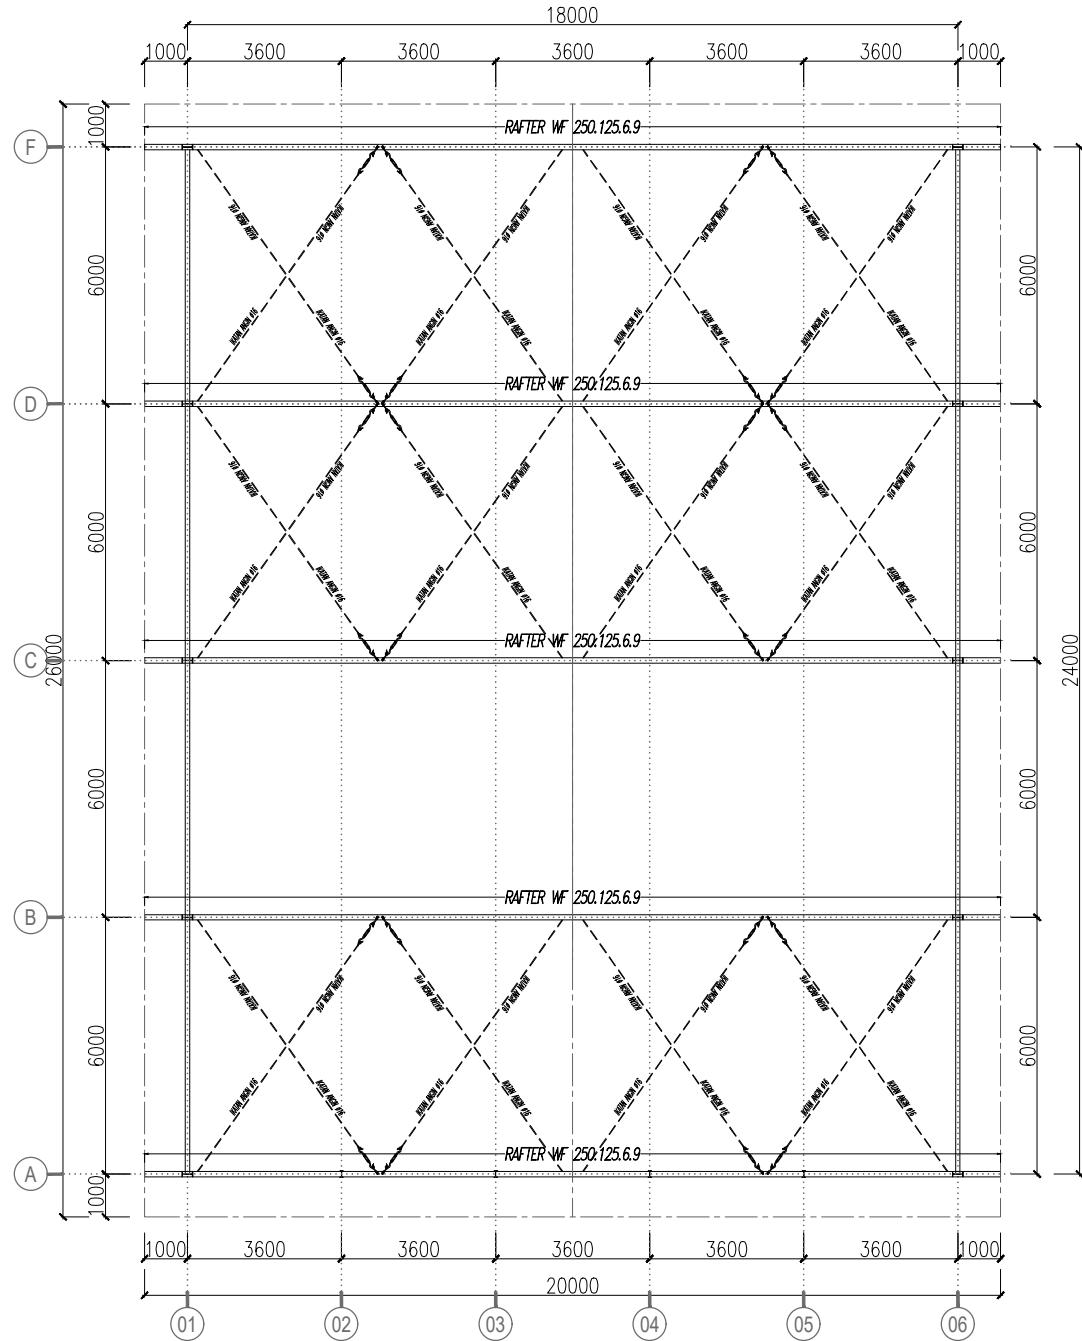




## DENAH RANGKA ATAP

SKALA 1 : 100

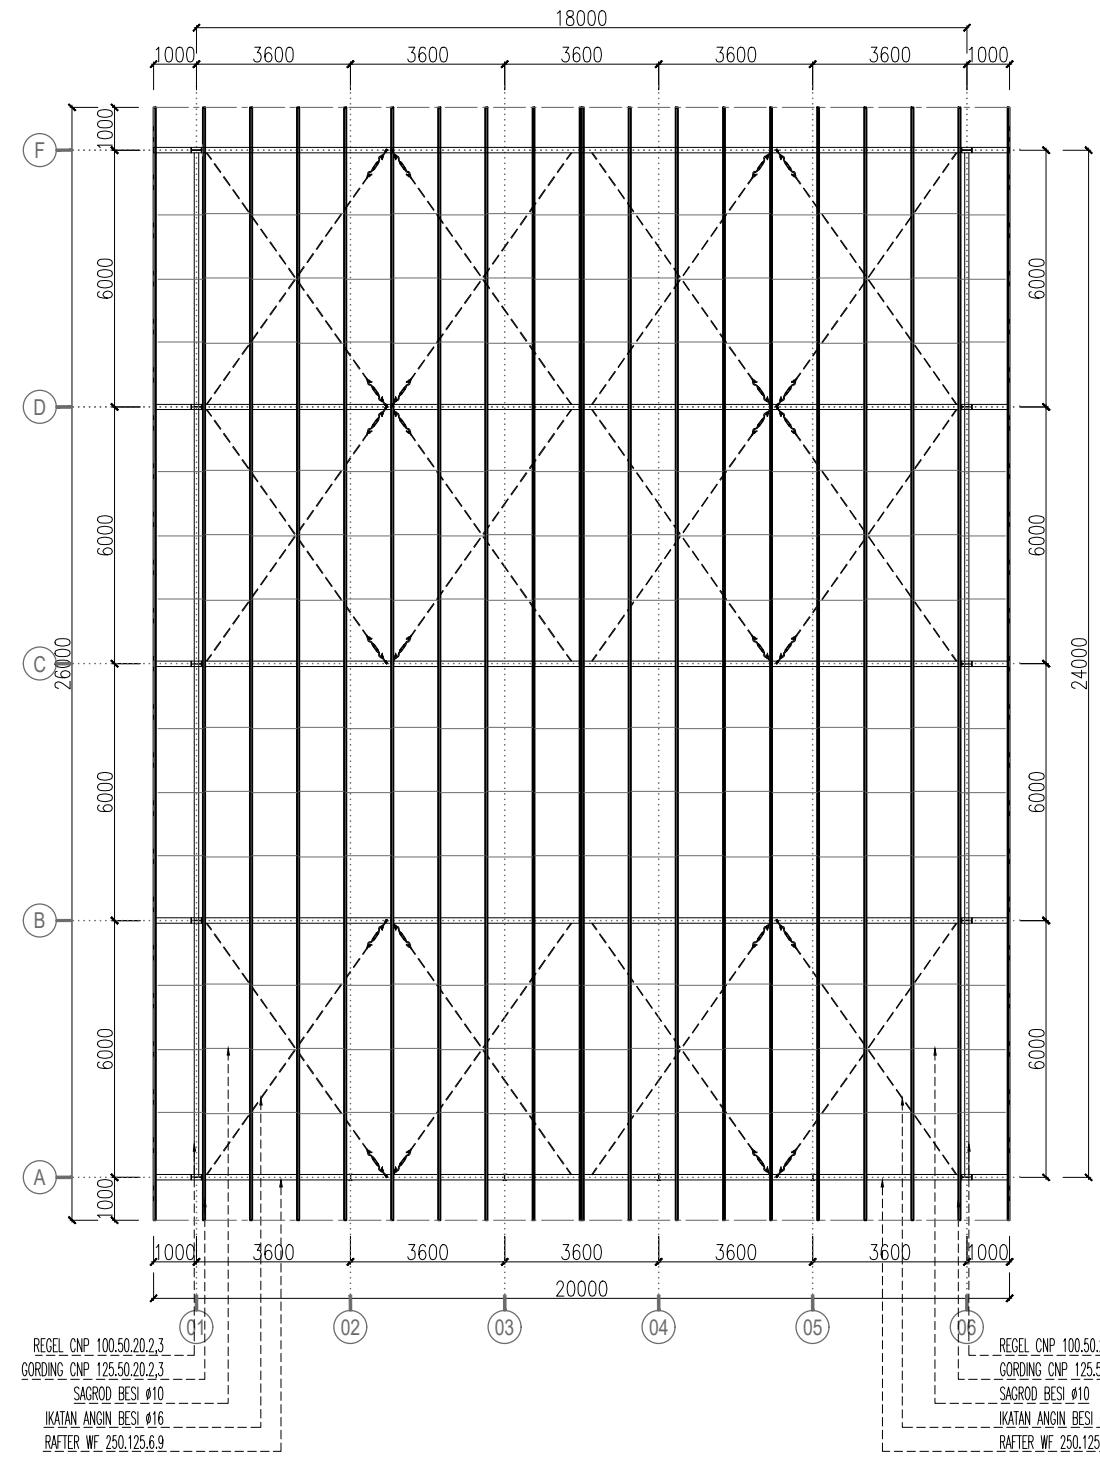


NAMA PROYEK	
<p style="text-align: center;"><b>PROJECT GUDANG</b></p> <p style="text-align: center;">PT. JOPLAST GEMILANG</p>	
LOKASI PROYEK	
<p style="text-align: center;">jl. Raya Sawocangkring no.102 <b>Wonoayu, Sidoarjo - JATIM</b></p>	
PENANGGUNG JAWAB	
<u>DIGAMBAR</u>	<u>PELAKSANA</u>
<u>DISETUJUI</u>	<u>PEMILIK</u>
CATATAN	
<p>1. PELAKSANA ATAU SUBKON WAJIB MEMERIKSA KEMBALI KESESUAIN GAMBAR DENGAN KONDISI LAPANGAN</p>	
JUDUL GAMBAR	SKALA
TANGGAL :	REVISI :
15 NOVEMBER 2024	<b>R1</b>
KODE GAMBAR	
STR-04-22	
NO. LBR	JUMLAH LBR
22	33

NAMA PROYEK	
<b>PROJECT GUDANG</b> PT. JOJOPLAST GEMILANG	
LOKASI PROYEK	
jl. Raya Sawocangkring no.102 <b>Wonoayu, Sidoarjo - JATIM</b>	
PENANGGUNG JAWAB	
DIGAMBAR	PELAKSANA
DISETUJU	PEMILIK
CATATAN	
1. PELAKSANA ATAU SUBKON WAJIB MEMERIKSA KEMBALI KESESUAIN GAMBAR DENGAN KONDISI LAPANGAN	
JUDUL GAMBAR	SKALA
TANGGAL :	REVISI :
15 NOVEMBER 2024	<b>R1</b>
KODE GAMBAR	
<b>STR-05-23</b>	
NO. LBR	JUMLAH LBR
23	33

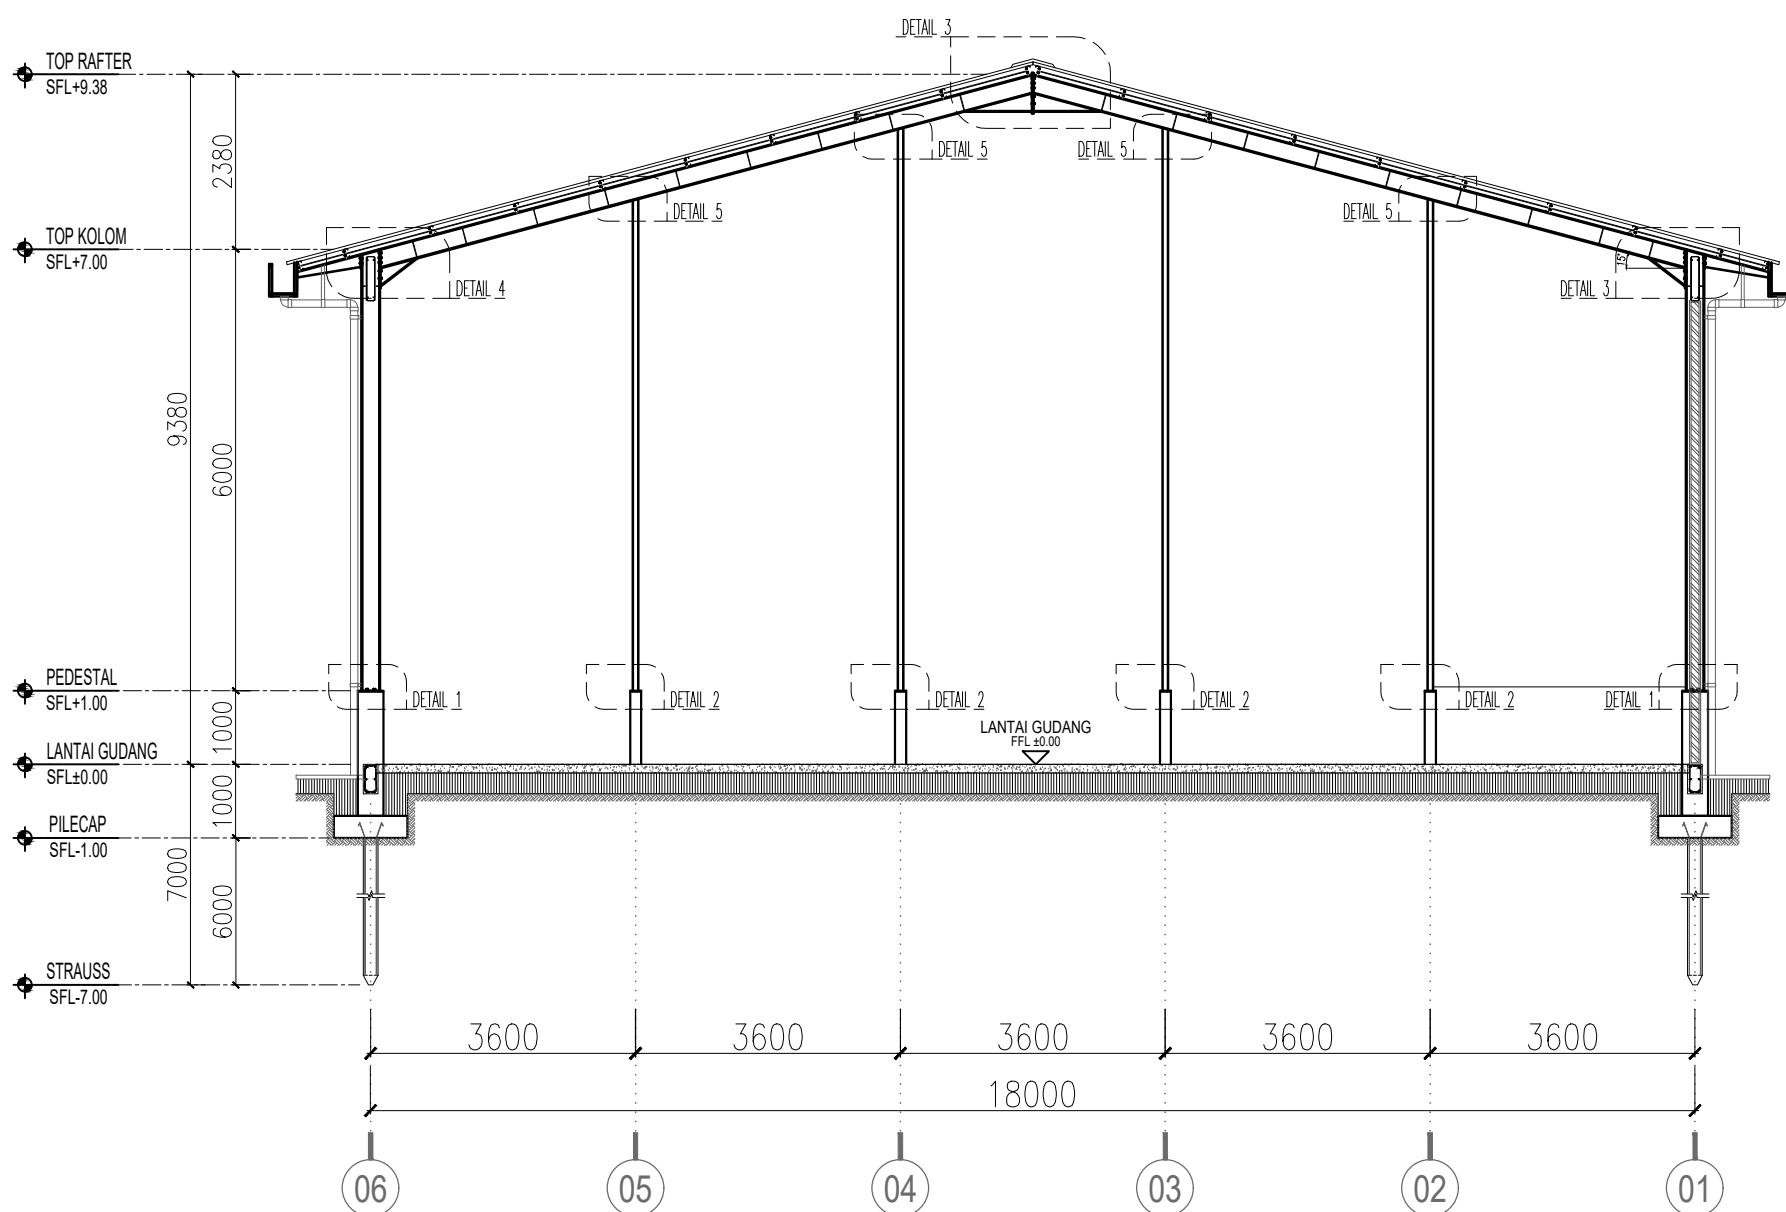


NAMA PROYEK	
<b>PROJECT GUDANG</b> PT. JOJOPLAST GEMILANG	
LOKASI PROYEK	
jl. Raya Sawangkring no.102 <b>Wonoayu, Sidoarjo - JATIM</b>	
PENANGGUNG JAWAB	
DIGAMBAR	PELAKSANA
DISETUJU	PEMILIK
CATATAN	
1. PELAKSANA ATAU SUBKON WAJIB MEMERIKSA KEMBALI KESESUAIN GAMBAR DENGAN KONDISI LAPANGAN	
JUDUL GAMBAR	SKALA
TANGGAL :	REVISI :
15 NOVEMBER 2024	<b>R1</b>
KODE GAMBAR	
<b>STR-05-24</b>	
NO. LBR	JUMLAH LBR
24	33

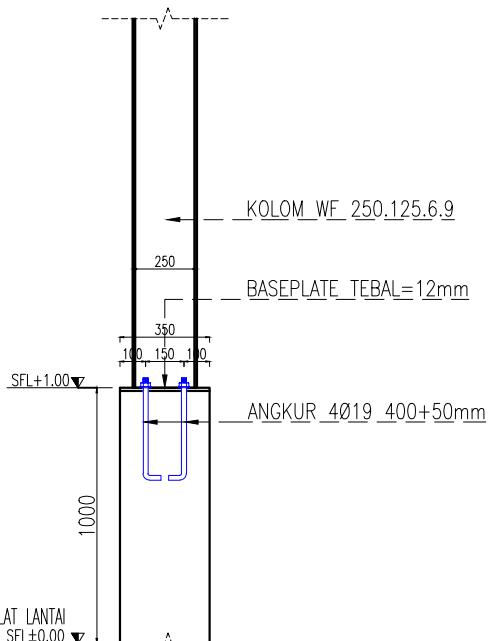


01  
STR SKALA 1 : 25

**POTONGAN A-A**

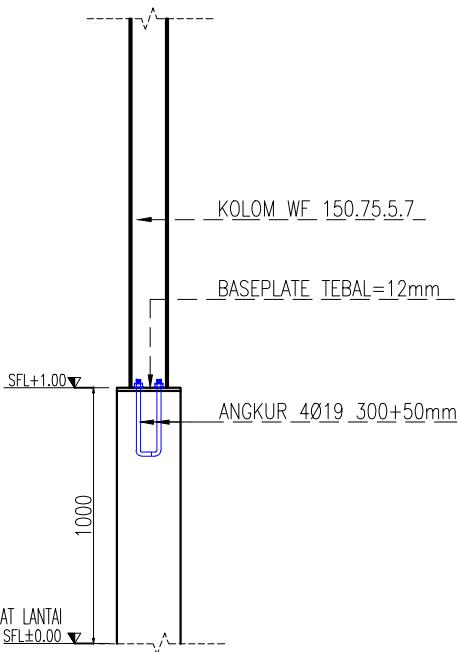


01  
STR SKALA 1 : 25

**POTONGAN B-B**

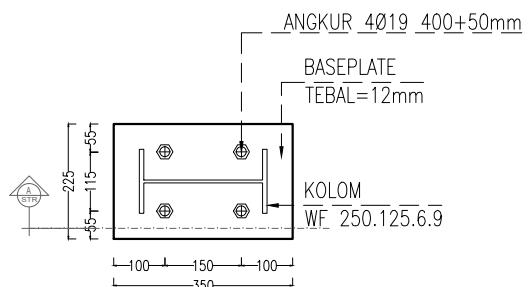

01  
STR SKALA 1 : 25




**DENAH BASEPLATE  
KOLOM WF 250.125.6.9**

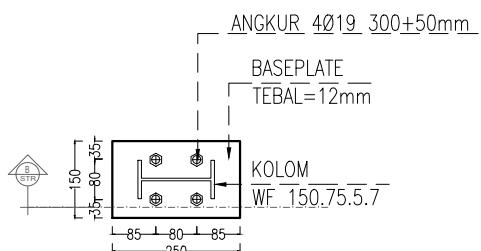






01  
STR SKALA 1 : 25

**DENAH BASEPLATE  
KOLOM WF 150.75.5.7**


NAMA PROYEK	
<b>PROJECT GUDANG</b> PT. JOJOPLAST GEMILANG	
LOKASI PROYEK	
jl. Raya Sawangkring no.102 <b>Wonoayu, Sidoarjo - JATIM</b>	
PENANGGUNG JAWAB	
DIGAMBAR	PELAKSANA
DISETUJU	PEMILIK
CATATAN	
1. PELAKSANA ATAU SUBKON WAJIB MEMERIKSA KEMBALI KESESUAIN GAMBAR DENGAN KONDISI LAPANGAN	
JUDUL GAMBAR	SKALA
TANGGAL :	REVISI :
15 NOVEMBER 2024	R1
KODE GAMBAR	
STR-05-25	
NO. LBR	JUMLAH LBR
25	33

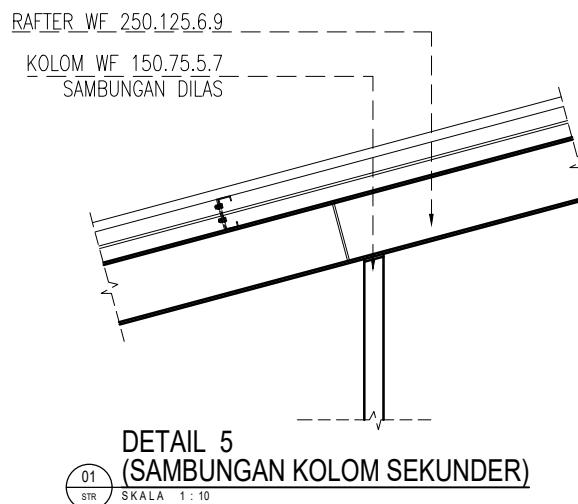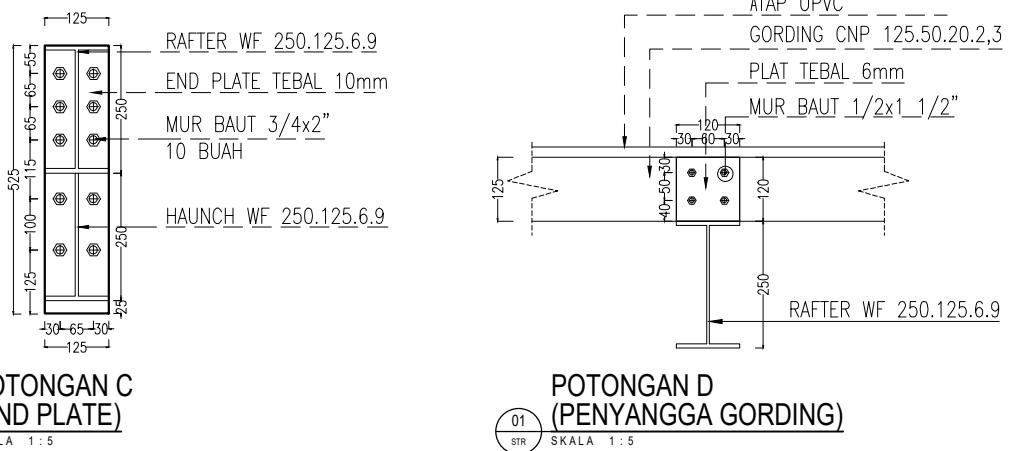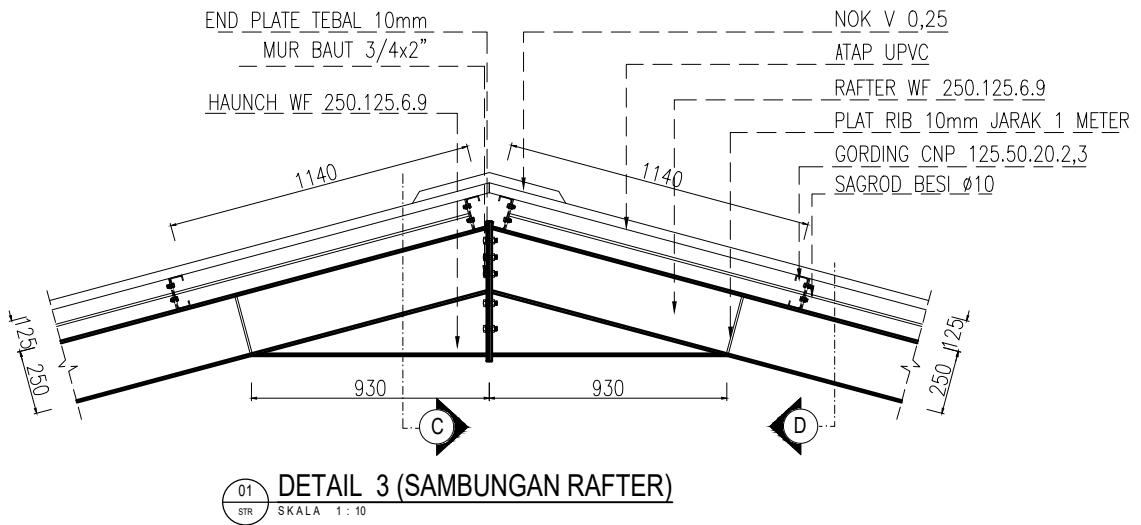

NAMA PROYEK	
PROJECT GUDANG	PT. JOJOPLAST GEMILANG
LOKASI PROYEK	
jl. Raya Sawocangkring no.102 Wonoayu, Sidoarjo - JATIM	
PENANGGUNG JAWAB	
DIGAMBAR	PELAKSANA
DISETUJU	PEMILIK
CATATAN	
1. PELAKSANA ATAU SUBKON WAJIB MEMERIKSA KEMBALI KESESUAIN GAMBAR DENGAN KONDISI LAPANGAN	
JUDUL GAMBAR	SKALA
TANGGAL :	REVISI :
15 NOVEMBER 2024	R1
KODE GAMBAR	
STR-05-26	
NO. LBR	JUMLAH LBR
26	33

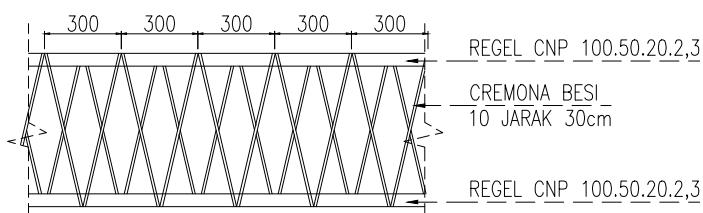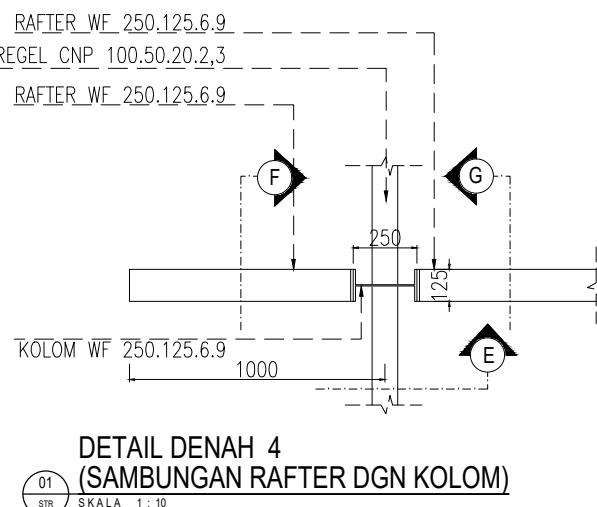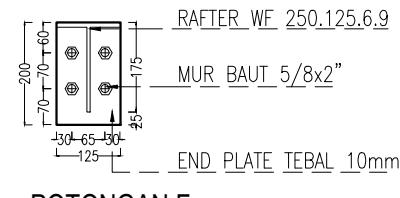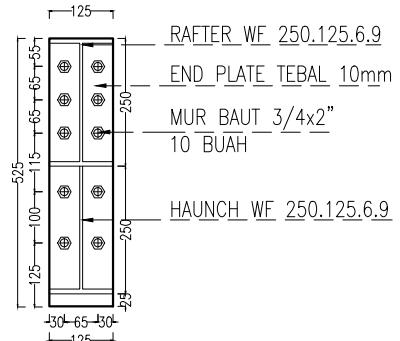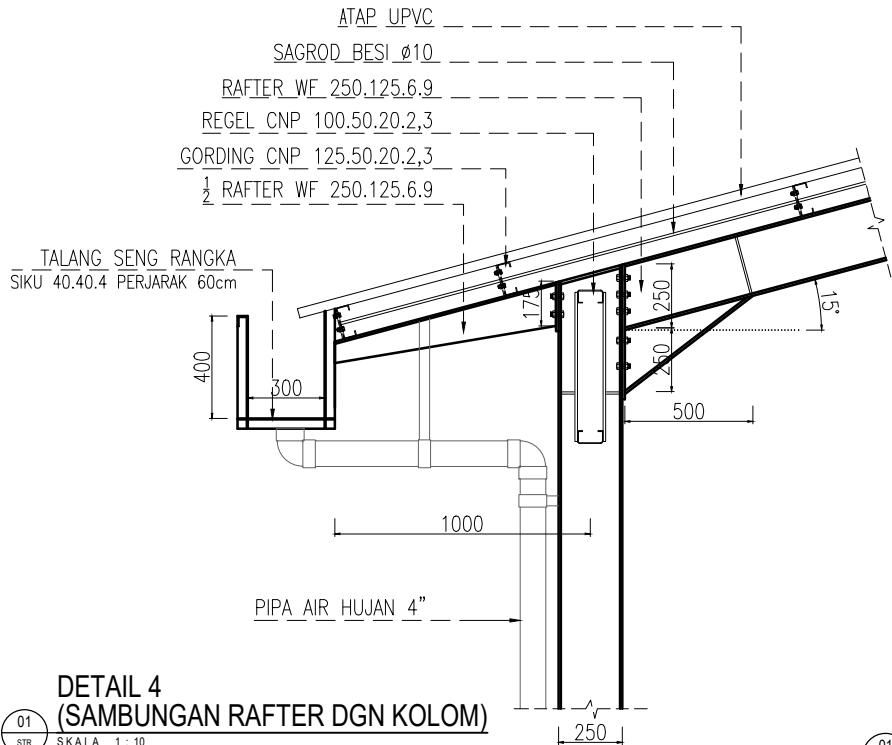


NAMA PROYEK	
<b>PROJECT GUDANG</b> PT. JOJOPLAST GEMILANG	
LOKASI PROYEK	
jl. Raya Sawangkring no.102 <b>Wonoayu, Sidoarjo - JATIM</b>	
PENANGGUNG JAWAB	
DIGAMBAR	PELAKSANA
DISETUJU	PEMILIK
CATATAN	
1. PELAKSANA ATAU SUBKON WAJIB MEMERIKSA KEMBALI KESESUAIN GAMBAR DENGAN KONDISI LAPANGAN	
JUDUL GAMBAR	SKALA
TANGGAL :	REVISI :
15 NOVEMBER 2024	<b>R1</b>
KODE GAMBAR	
<b>STR-05-27</b>	
NO. LBR	JUMLAH LBR
27	33

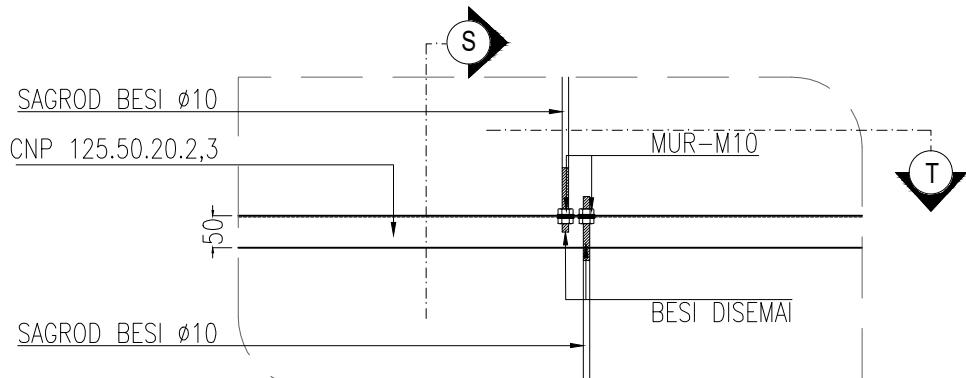


**DETAIL DENAH  
(PEMASANGAN SAGROD GORDING)**

01  
STR  
NTS

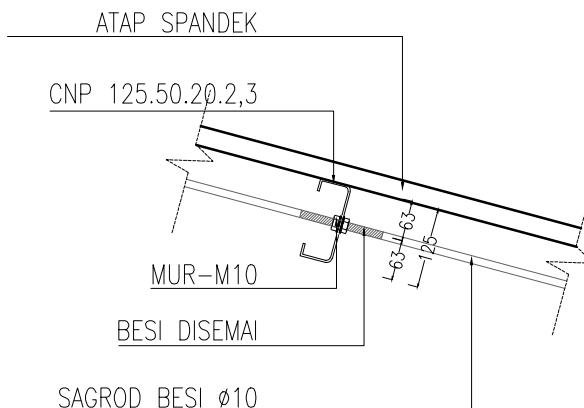


**POTONGAN S**

01  
STR  
SKALA 1 : 5

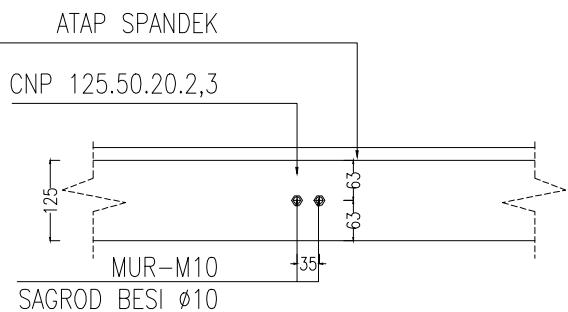


**POTONGAN T**

01  
STR  
SKALA 1 : 5

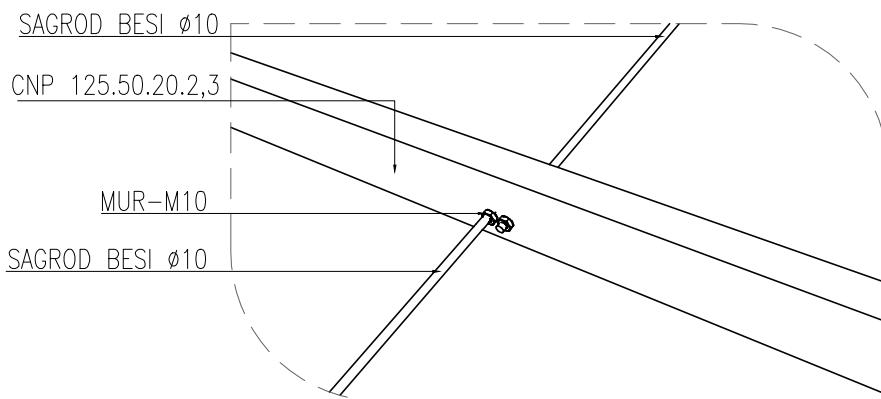

**3D AKSONOMETRI  
(PEMASANGAN SAGROD GORDING)**

01  
STR  
NTS

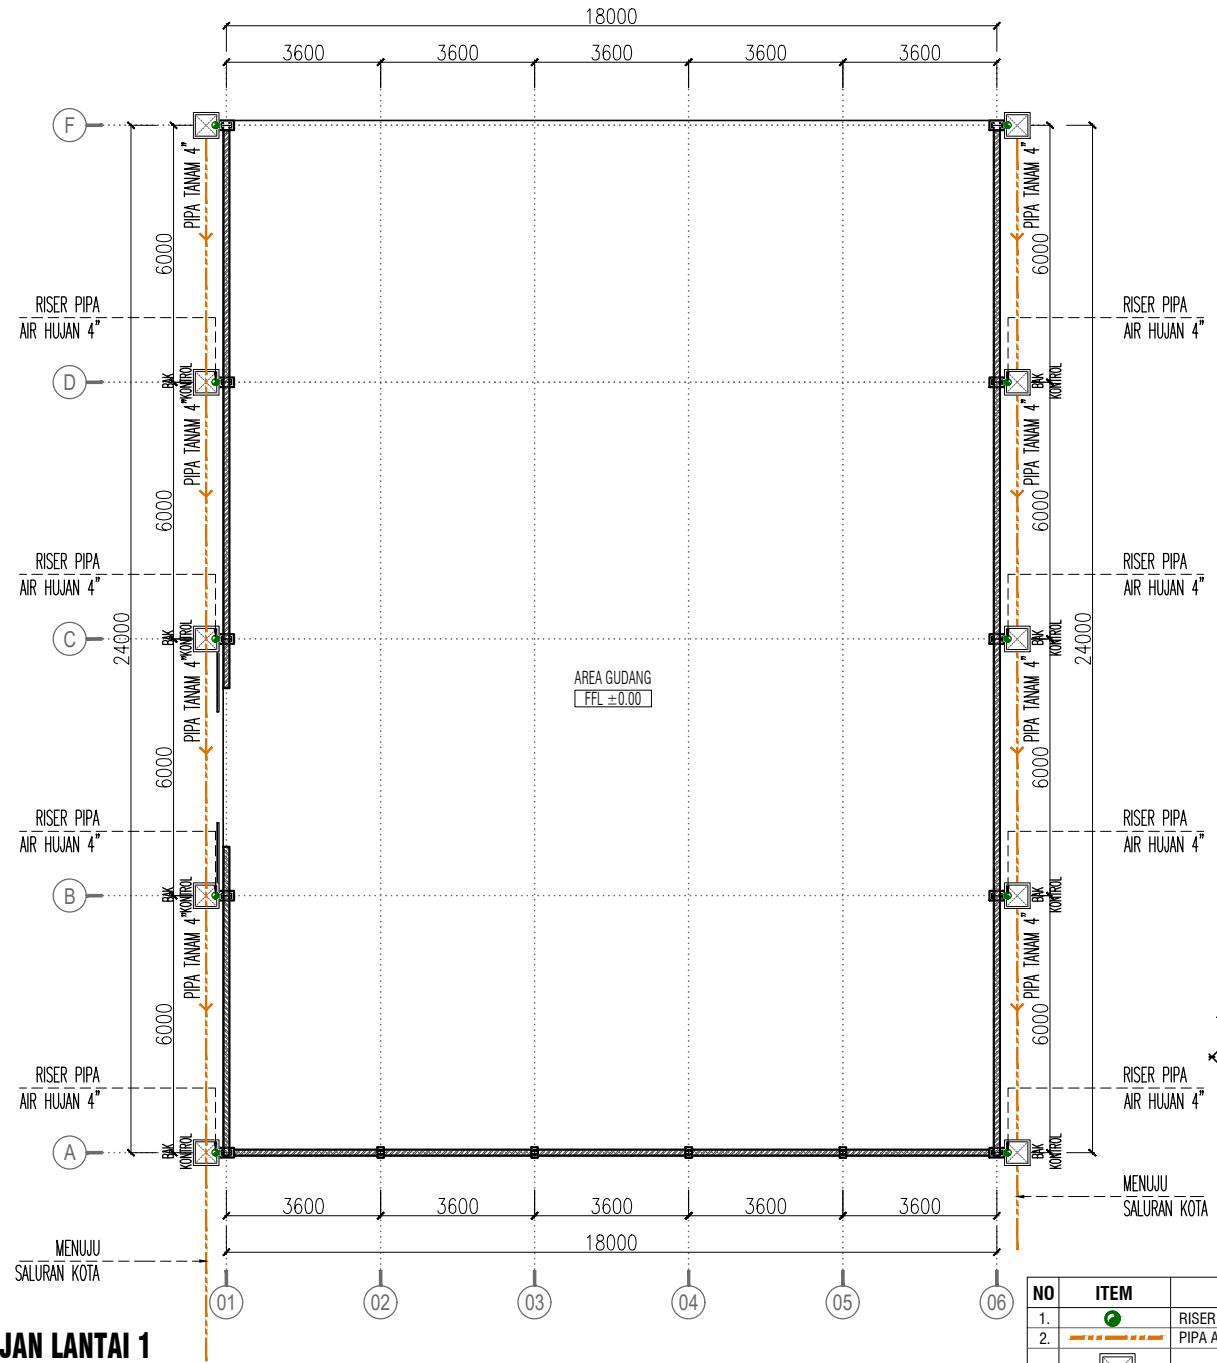


## DENAH KOTOR DAN AIR HUJAN LANTAI 1

SKALA 1 : 100

NO	ITEM	KETERANGAN
1.		RISER PIPA AIR AIR HUJAN 4"
2.		PIPA AIR HUJAN 4"
3.		BAK KONTROL

NAMA PROYEK	
<b>PROJECT GUDANG</b> <b>PT. JOOPLAST GEMILANG</b>	
LOKASI PROYEK	
<b>jl. Raya Sawocangkring no.102 Wonoayu, Sidoarjo - JATIM</b>	
PENANGGUNG JAWAB	
DIGAMBAR	PELAKSANA
DISETUJUI	PEMILIK
CATATAN	
<p>1. PELAKSANA ATAU SUBKON WAJIB MEMERIKSA KEMBALI KESESUAIN GAMBAR DENGAN KONDISI LAPANGAN</p>	
JUDUL GAMBAR	SKALA
TANGGAL :	REVISI :
15 NOVEMBER 2024	<b>R1</b>
KODE GAMBAR	
<b>STR-06-28</b>	
NO. LBR	JUMLAH LBR
28	33


NAMA PROYEK	
<b>PROJECT GUDANG</b> PT. JOJOPLAST GEMILANG	
LOKASI PROYEK	
jl. Raya Sawocangkring no.102 <b>Wonoayu, Sidoarjo - JATIM</b>	
PENANGGUNG JAWAB	
DIGAMBAR	PELAKSANA
DISETUJU	PEMILIK
CATATAN	
1. PELAKSANA ATAU SUBKON WAJIB MEMERIKSA KEMBALI KESESUAIN GAMBAR DENGAN KONDISI LAPANGAN	
JUDUL GAMBAR	SKALA
TANGGAL :	REVISI :
15 NOVEMBER 2024	R1
KODE GAMBAR	
STR-06-29	
NO. LBR	JUMLAH LBR
29	33

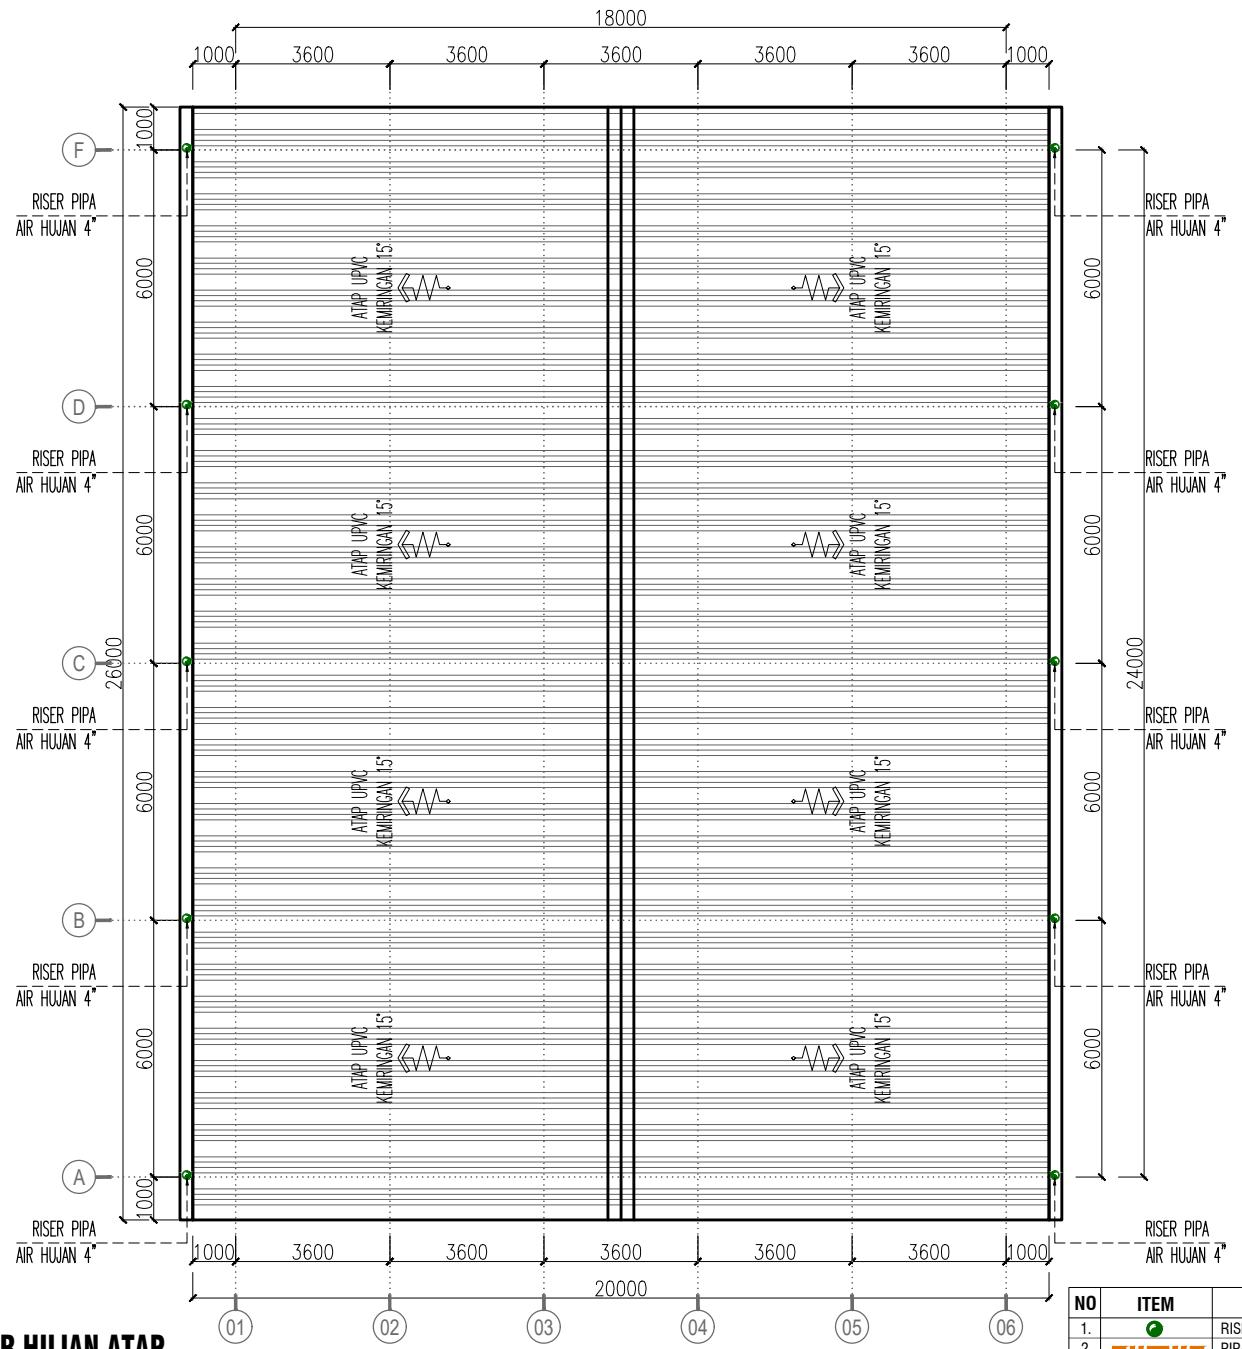

**DENAH KOTOR DAN AIR HUJAN ATAP**

SKALA 1 : 100

NO	ITEM	KETERANGAN
1.		RISER PIPA AIR AIR HUJAN 4"
2.		PIPA AIR HUJAN 4"
3.		BAK KONTROL

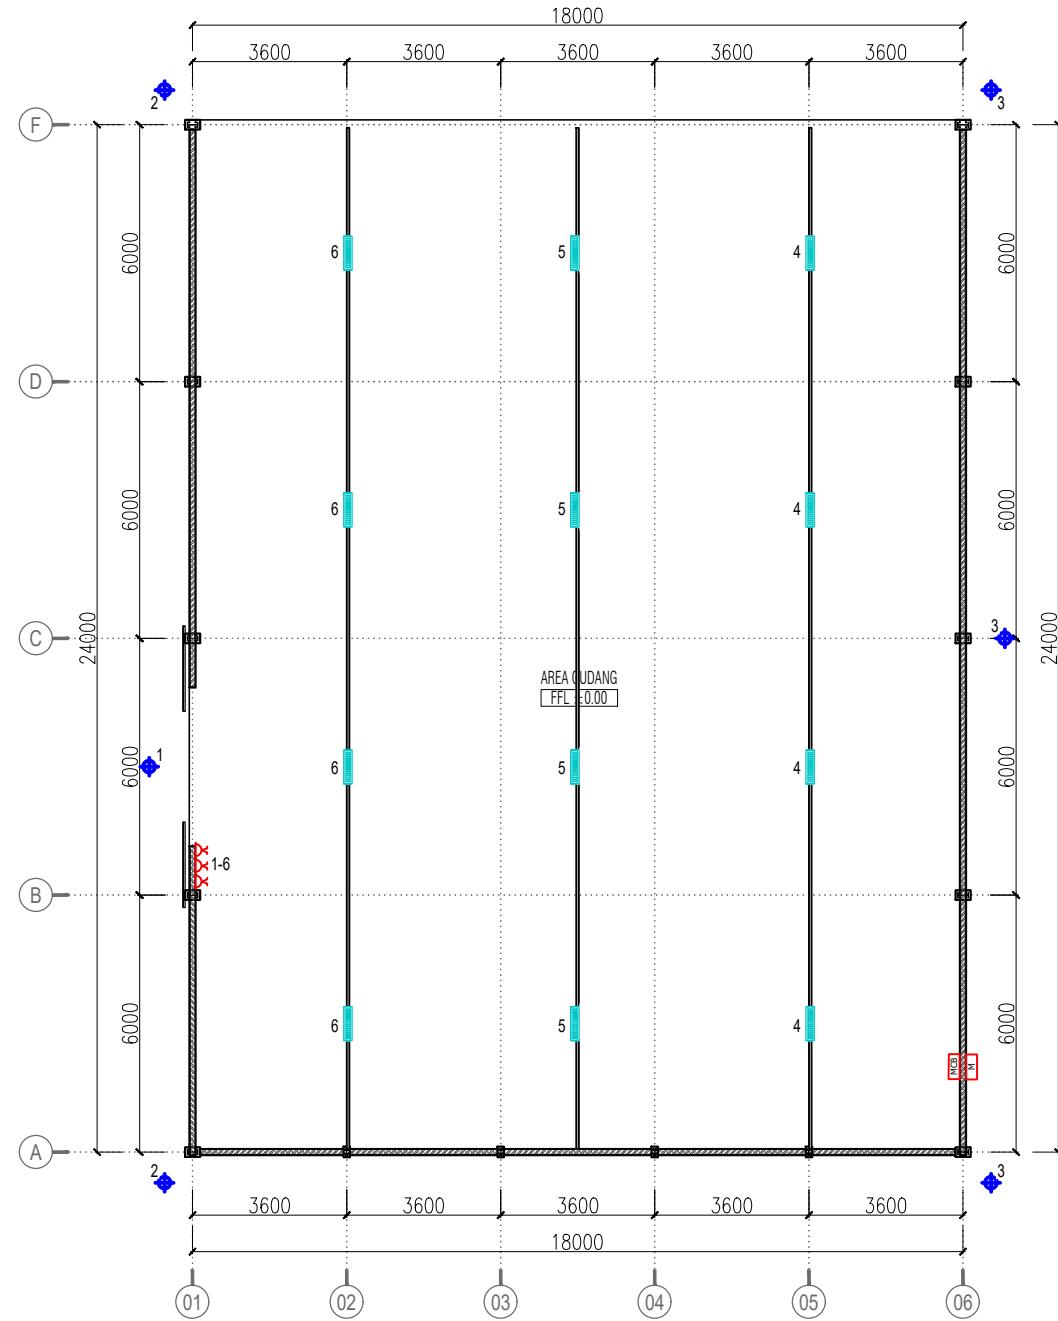


NOTASI	KETERANGAN	JUMLAH	TINGGI DARI LANTAI
☒	SAKLAR GANDA	3	130 CM
△	SAKLAR TUNGGAL	0	130 CM
◆	DLIGHT	6	-
■	LAMPU SOROT	12	-
■	METERAN LISTRIK	1	200 CM
■	MCB	1	200 CM

## DENAH TITIK LAMPU

SKALA 1 : 100

NAMA PROYEK	
<p style="text-align: center;"><b>PROJECT GUDANG</b></p> <p style="text-align: center;">PT. JOOPLAST GEMILANG</p>	
LOKASI PROYEK	
<p style="text-align: center;">jl. Raya Sawocangkring no.102</p> <p style="text-align: center;"><b>Wonoayu, Sidoarjo - JATIM</b></p>	
PENANGGUNG JAWAB	
<u>DIGAMBAR</u>	<u>PELAKSANA</u>
<u>DISETJUUI</u>	<u>PEMILIK</u>
CATATAN	
<p>1. PELAKSANA ATAU SUBKON WAJIB MEMERIKSA KEMBALI KESESUAIN GAMBAR DENGAN KONDISI LAPANGAN</p>	
JUDUL GAMBAR	SKALA
TANGGAL :	REVISI :
15 NOVEMBER 2024	<b>R1</b>
KODE GAMBAR	
STR-07-30	
NO. LBR	JUMLAH LBR
30	33

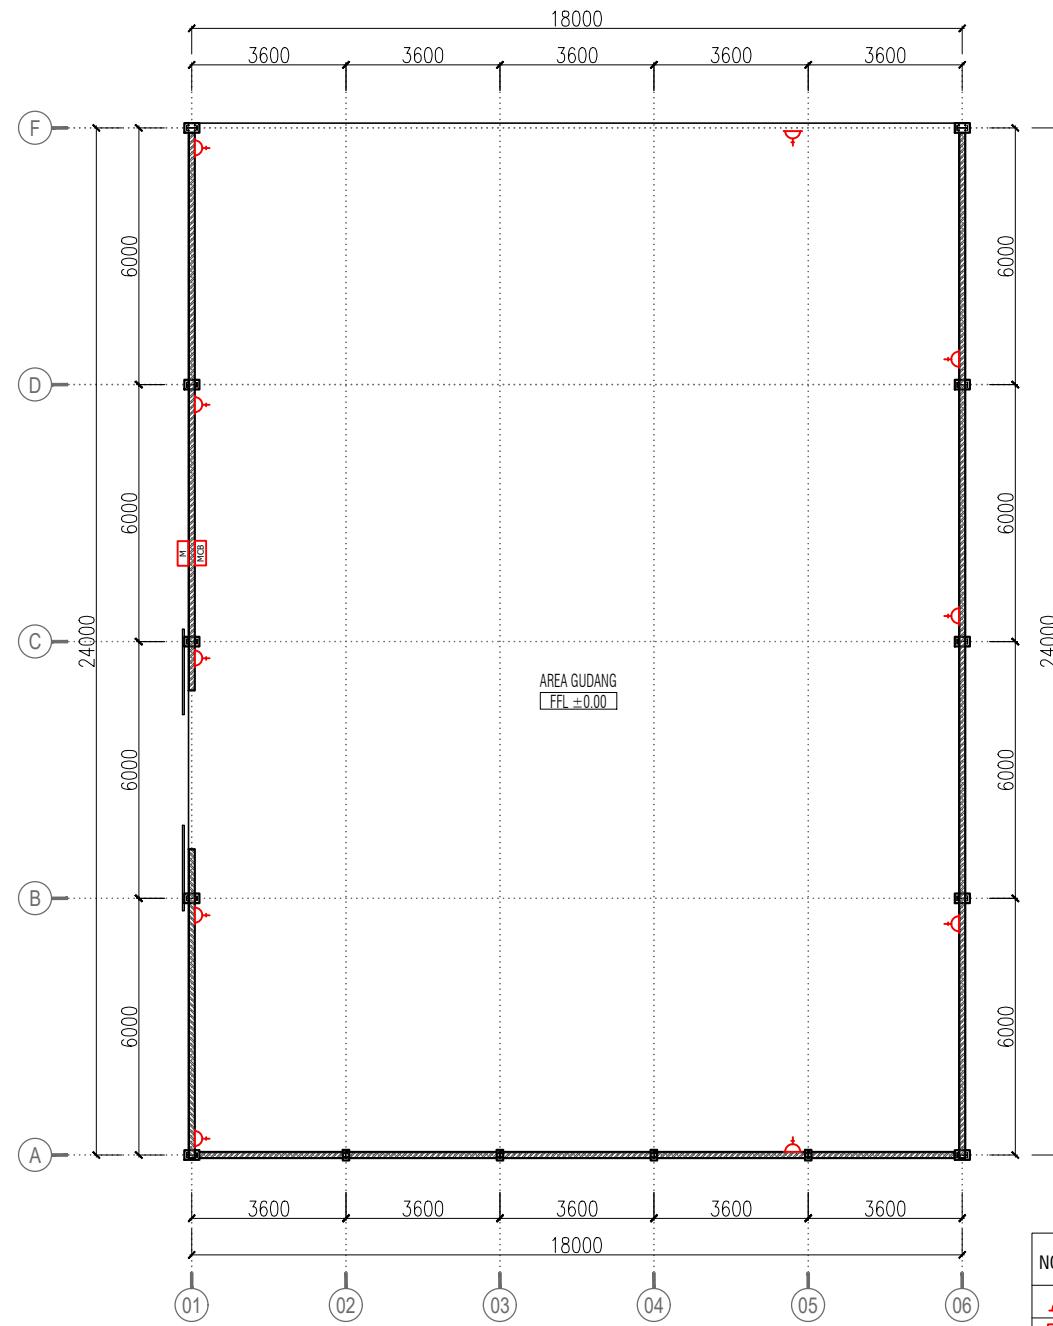


NOTASI	KETERANGAN	JUMLAH	TINGGI DARI LANTAI
	STOP KONTAK DINDING	10	30 CM
	METERAN LISTRIK	1	200 CM
	MCB	1	200 CM

## DENAH STOP KONTAK



SKALA 1 : 100

NAMA PROYEK	
<p style="text-align: center;"><b>PROJECT GUDANG</b></p> <p style="text-align: center;">PT. JOOPLAST GEMILANG</p>	
LOKASI PROYEK	
<p style="text-align: center;">jl. Raya Sawocangkring no.102</p> <p style="text-align: center;"><b>Wonoayu, Sidoarjo - JATIM</b></p>	
PENANGGUNG JAWAB	
<u>DIGAMBAR</u>	<u>PELAKSANA</u>
<u>DISETYUJU</u>	<u>PEMILIK</u>
CATATAN	
<p>1. PELAKSANA ATAU SUBKON WAJIB MEMERIKSA KEMBALI KESESUAIN GAMBAR DENGAN KONDISI LAPANGAN</p>	
JUDUL GAMBAR	SKALA
TANGGAL :	REVISI :
15 NOVEMBER 2024	<b>R1</b>
KODE GAMBAR	
STR-07-31	
NO. LBR	JUMLAH LBR
31	33

NAMA PROYEK	
<b>PROJECT GUDANG</b> PT. JOJOPLAST GEMILANG	
LOKASI PROYEK	
jl. Raya Sawocangkring no.102 <b>Wonoayu, Sidoarjo - JATIM</b>	
PENANGGUNG JAWAB	
DIGAMBAR	PELAKSANA
DISETUJU	PEMILIK
CATATAN	
1. PELAKSANA ATAU SUBKON WAJIB MEMERIKSA KEMBALI KESESUAIN GAMBAR DENGAN KONDISI LAPANGAN	
JUDUL GAMBAR	SKALA
TANGGAL :	REVISI :
15 NOVEMBER 2024	<b>R1</b>
KODE GAMBAR	
<b>STR-08-32</b>	
NO. LBR	JUMLAH LBR
32	33

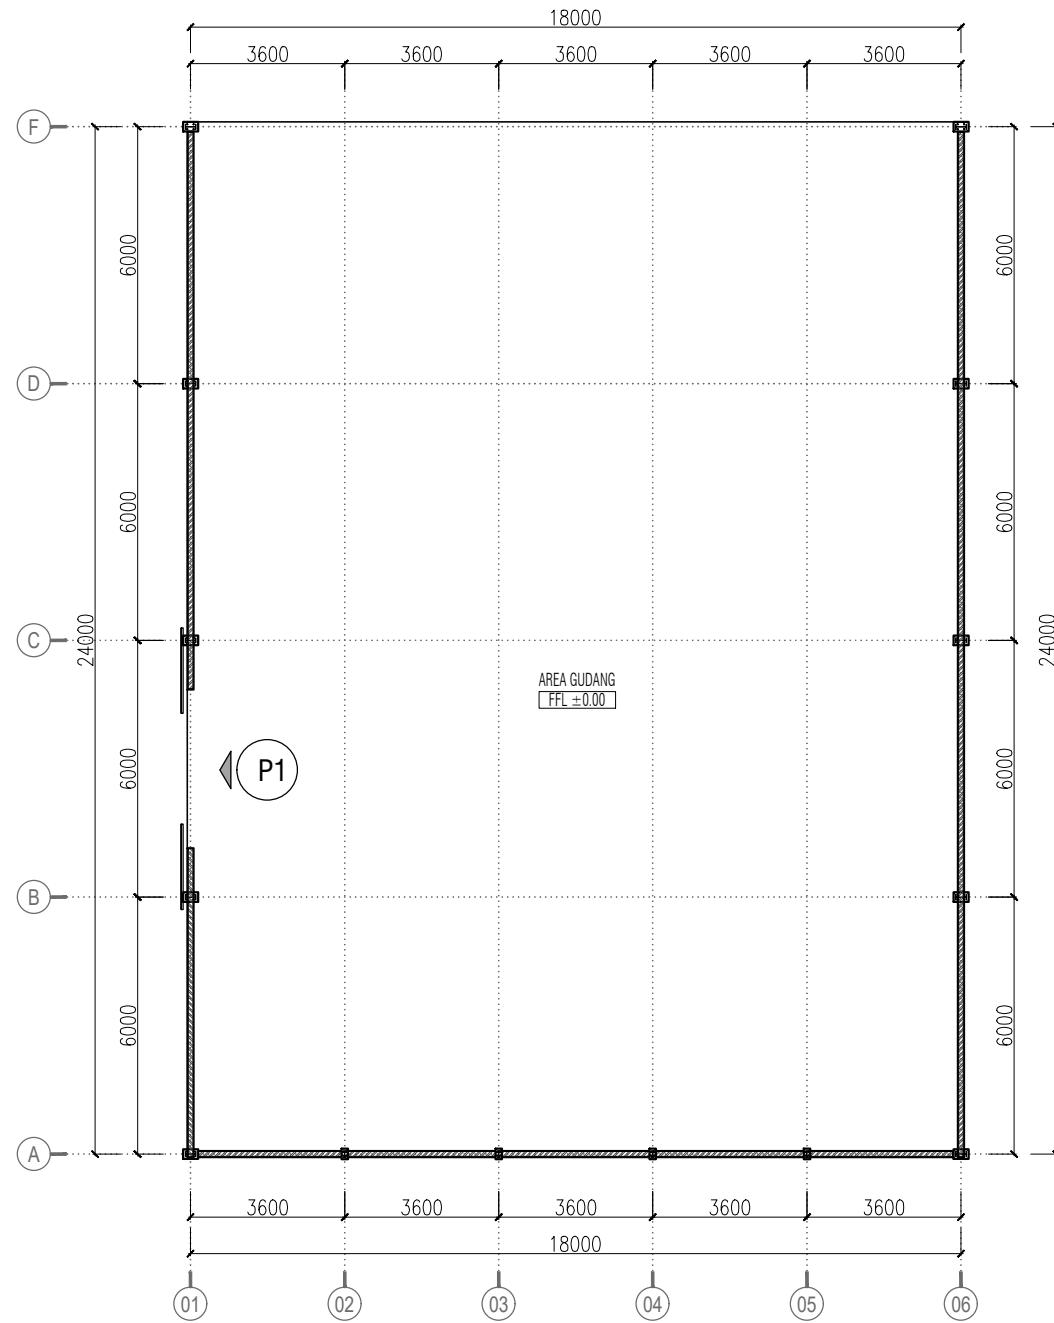


**DENAH POSISI PINTU**  
SKALA 1:100

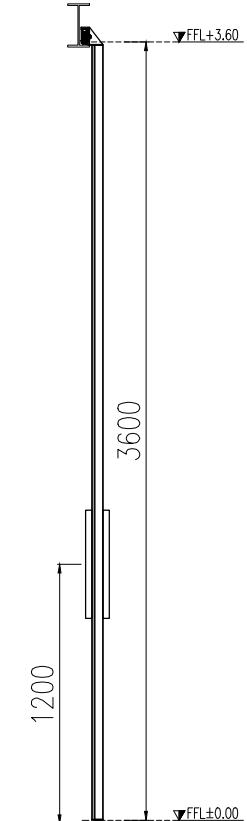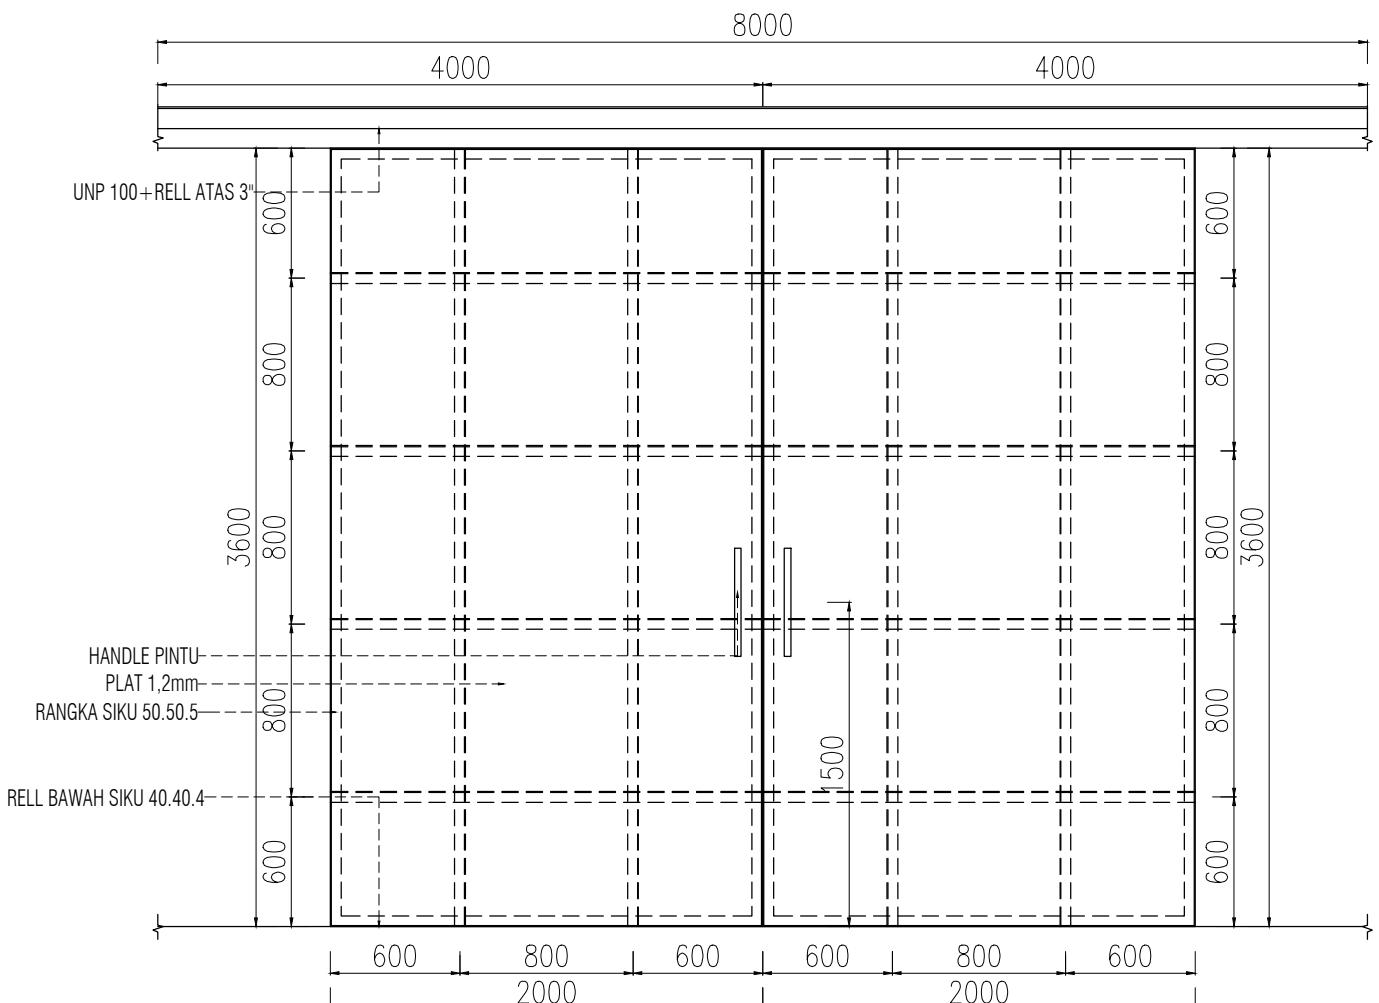

**DETAIL P1 = 1 PCS**

SKALA 1 : 25

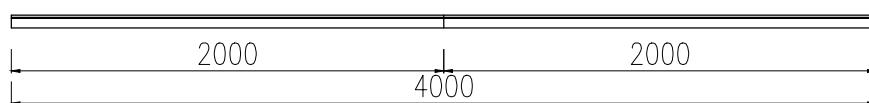

LOKASI	SAMPING KIRI BANGUNAN
JUMLAH	1 BUAH
KUSEN	FRAMELESS
DAUN PINTU	PLAT BESI 1,2mm
FINISHING	WARNA HITAM
JENIS PINTU	PINTU BESI SLADING

NAMA PROYEK	
<b>PROJECT GUDANG</b> PT. JOJOPLAST GEMILANG	
LOKASI PROYEK	
jl. Raya Sawangkring no.102 <b>Wonoayu, Sidoarjo - JATIM</b>	
PENANGGUNG JAWAB	
DIGAMBAR	PELAKSANA
DISETUJU	PEMILIK
CATATAN	
1. PELAKSANA ATAU SUBKON WAJIB MEMERIKSA KEMBALI KESESUAIN GAMBAR DENGAN KONDISI LAPANGAN	
JUDUL GAMBAR	SKALA
TANGGAL :	REVISI :
15 NOVEMBER 2024	<b>R1</b>
KODE GAMBAR	
ARS-08-33	
NO. LBR	JUMLAH LBR
33	33