


# DAFTAR GAMBAR

NOMER	NAMA GAMBAR	SKALA	KODE
<b>BAB.01</b>	<b>DAFTAR GAMBAR</b>		
1	DAFTAR GAMBAR 1	NTS	ARS-01-01
<b>BAB.02</b>	<b>ARSITEKTUR</b>		
2	DENAH GOR BADMINTON DAN DENAH ATAP	1:100	ARS-02-02
3	TAMPAK DEPAN	1:40	ARS-02-03
4	TAMPAK BELAKANG	1:40	ARS-02-04
5	TAMPAK SAMPING KANAN	1:50	ARS-02-05
6	TAMPAK SAMPING KIRI	1:50	ARS-02-06
7	POTONGAN A-A	1:50	ARS-02-07
8	POTONGAN B-B	1:50	ARS-02-08
9	POTONGAN C-C	1:50	ARS-02-09
10	POTONGAN D-D	1:50	ARS-02-10
<b>BAB.03</b>	<b>STRUKTUR</b>		
11	DENAH PILECAP SFL-1.00 (ELEVASI BOTTOM)	1:100	STR-03-11
12	DETAIL PONDASI PC 1	1:25	STR-03-12
13	DENAH SLOOF SFL±0.00	1:100	STR-03-13
14	DENAH PLAT DAN KOLOM SFL±0.00	1:100	STR-03-14
15	DETAIL SLOOF, BALOK, DAN KOLOM	1:25	STR-03-15
16	DENAH KOLOM BAJA SFL+1.00	1:100	STR-03-16
17	DENAH BALOK RELL PINTU SFL+3.25	1:100	STR-03-17
18	DENAH TIE BEAM SFL+7.00	1:100	STR-03-18
19	DENAH RAFTER/KUDA-KUDA	1:100	STR-03-19
20	DENAH RANGKA ATAP	1:100	STR-03-20
21	POTONGAN B-B (KEY SECTION)	1:50	STR-03-21
22	DETAIL 1 (BASEPLATE DAN ANGKUR)	1:25	STR-03-22
23	DETAIL 2 (SAMBUNGAN RAFTER)	1:10	STR-03-23
24	DETAIL 3 (SAMBUNGAN RAFTER DAN KOLOM)	1:10	STR-03-24
25	DETAIL 4 (SAMBUNGAN RAFTER DAN KOLOM)	1:10	STR-03-25
26	DETAIL PEMASANGAN SAGROD GORDING	1:10	STR-03-26
27	DETAIL TALANG	1:10	STR-03-27

# DAFTAR GAMBAR

NAMA PROYEK		
-		
LOKASI PROYEK		
-		
-		
PENANGGUNG JAWAB		
DIGAMBAR	PELAKSANA	
DISETUJUI	PEMILIK	
CATATAN		
1. PELAKSANA ATAU SUBKON WAJIB MEMERIKSA KEMBALI KESESUAIN GAMBAR DENGAN KONDISI LAPANGAN		
JUDUL GAMBAR		SKALA
1. DAFTAR GAMBAR		NTS
TANGGAL :		REVISI :
5 APRIL 2024		<b>R3</b>
KODE GAMBAR		
ARS-01-01		
NO. LBR	JUMLAH LBR	
01	35	

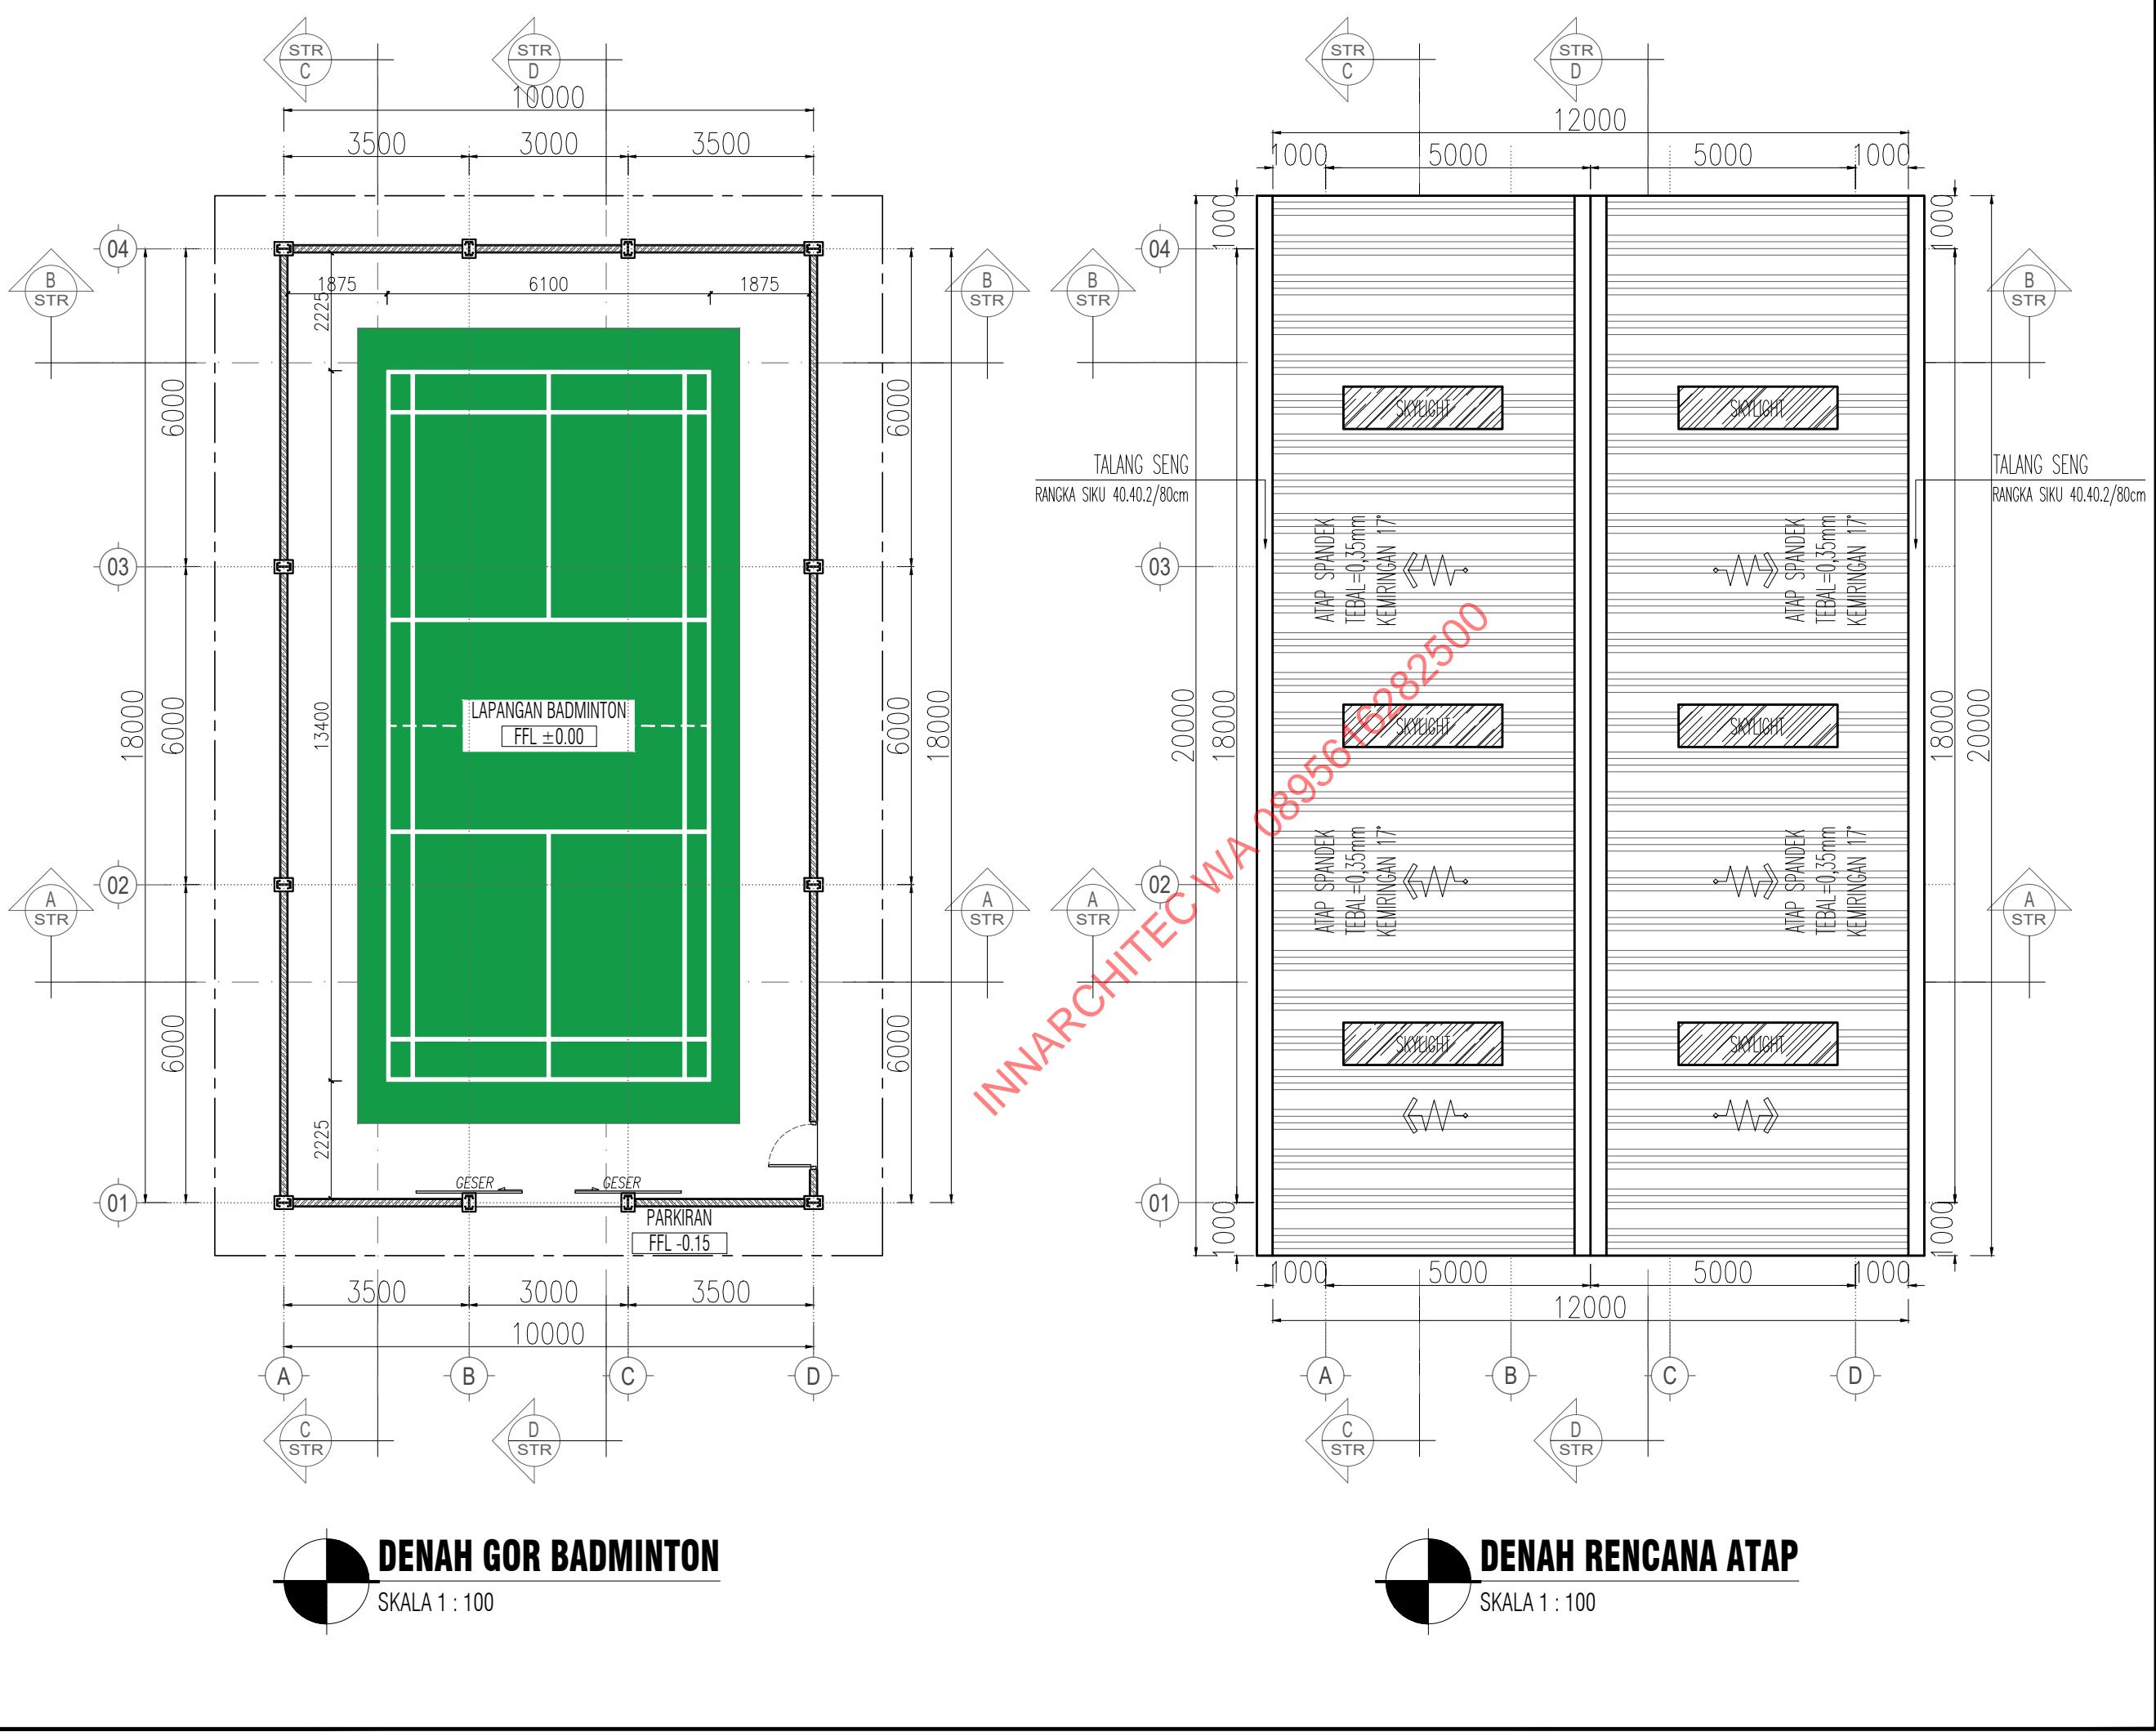


NAMA PROYEK	
-	
LOKASI PROYEK	
-	-
PENANGGUNG JAWAB	
DIGAMBAR	PELAKSANA
DISETUJUI	PEMILIK
CATATAN	
1. PELAKSANA ATAU SUBKON WAJIB MEMERIKSA KEMBALI KESESUAIN GAMBAR DENGAN KONDISI LAPANGAN	
JUDUL GAMBAR	SKALA
1.DENAH LANTAI 1 2.DENAH ATAP	1 : 100 1 : 100
TANGGAL :	REVISI :
5 APRIL 2024	R3
KODE GAMBAR	
ARS-02-02	
NO. LBR	JUMLAH LBR
02	35

NOK V 0,25

ATAP SPANDEK TEBAL=0,35mm

LISTPLANK SPANDEK TEBAL=0,35mm

RANGKA SIKU 40.40.2/80cm

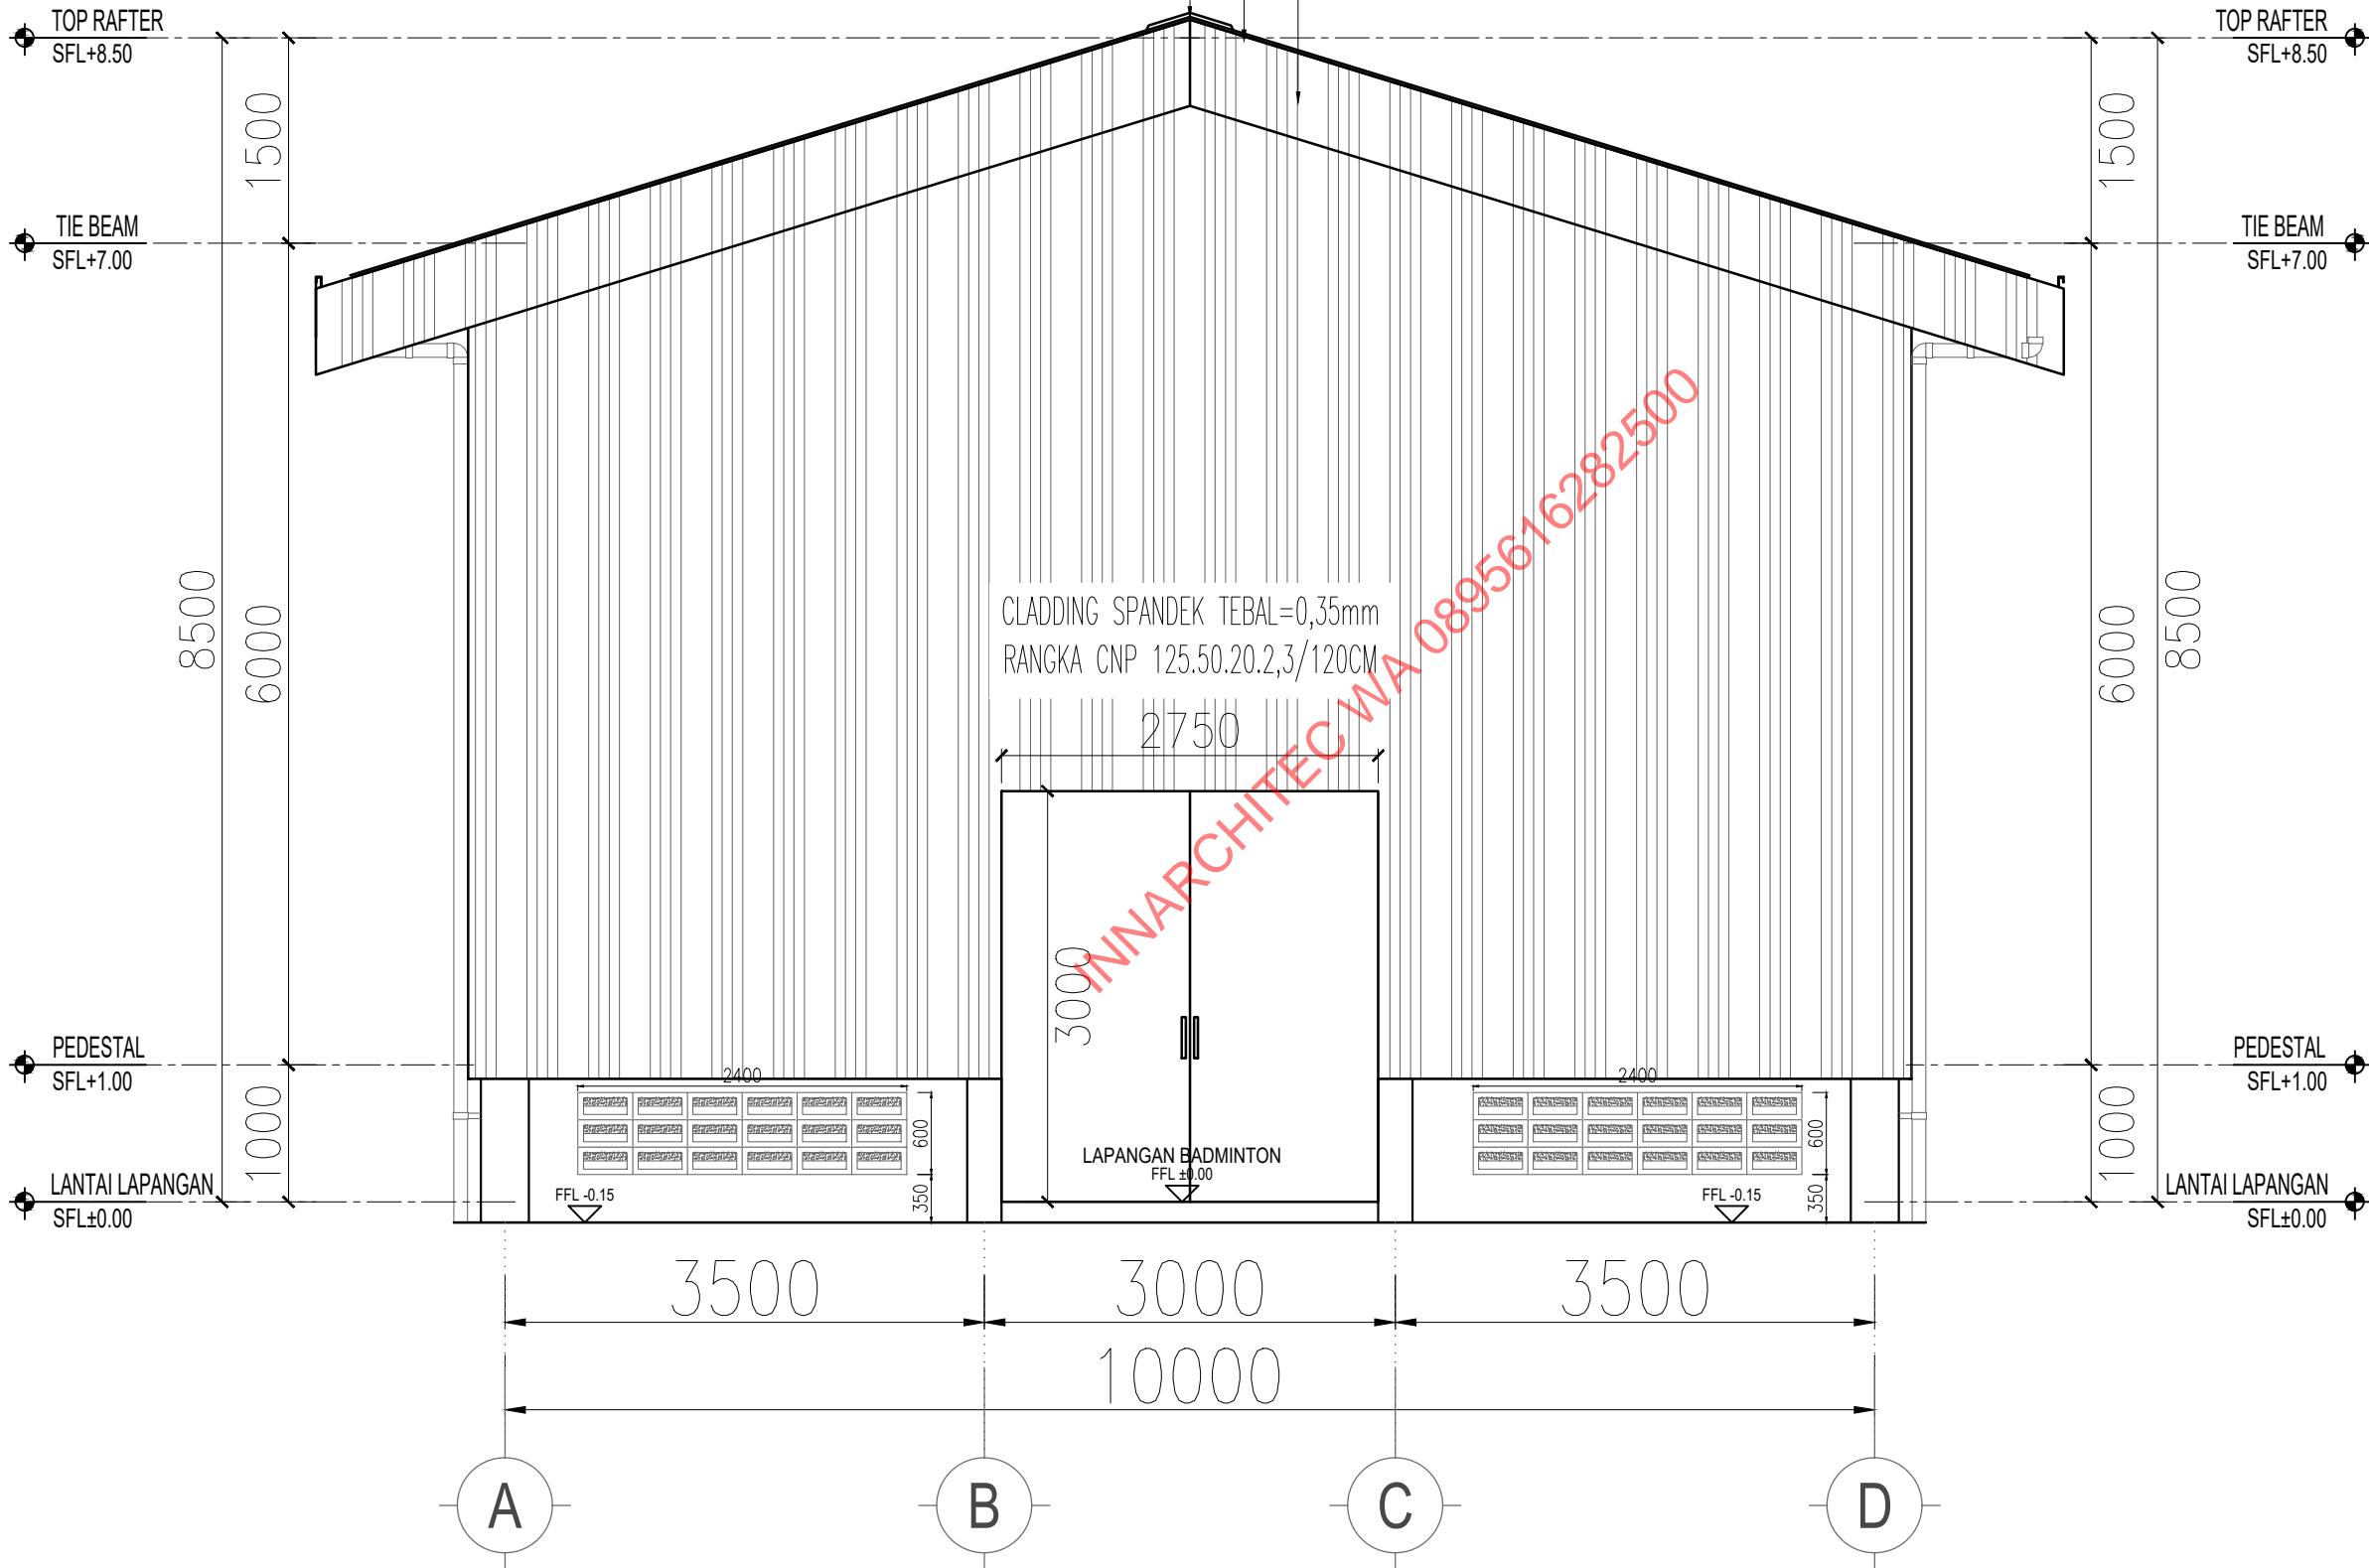


NAMA PROYEK	
-	
LOKASI PROYEK	
-	-
PENANGGUNG JAWAB	
DIGAMBAR	PELAKSANA
DISETUJUI	PEMILIK
CATATAN	
1. PELAKSANA ATAU SUBKON WAJIB MEMERIKSA KEMBALI KESESUAIN GAMBAR DENGAN KONDISI LAPANGAN	
-	
JUDUL GAMBAR	SKALA
1.TAMPAK DEPAN	1 : 40
TANGGAL :	REVISI :
5 APRIL 2024	<b>R3</b>
KODE GAMBAR	
ARS-02-03	
NO. LBR	JUMLAH LBR
03	35

NOK V 0,25

ATAP SPANDEK TEBAL=0,35mm

LISTPLANK SPANDEK TEBAL=0,35mm

RANGKA SIKU 40.40.2/80cm

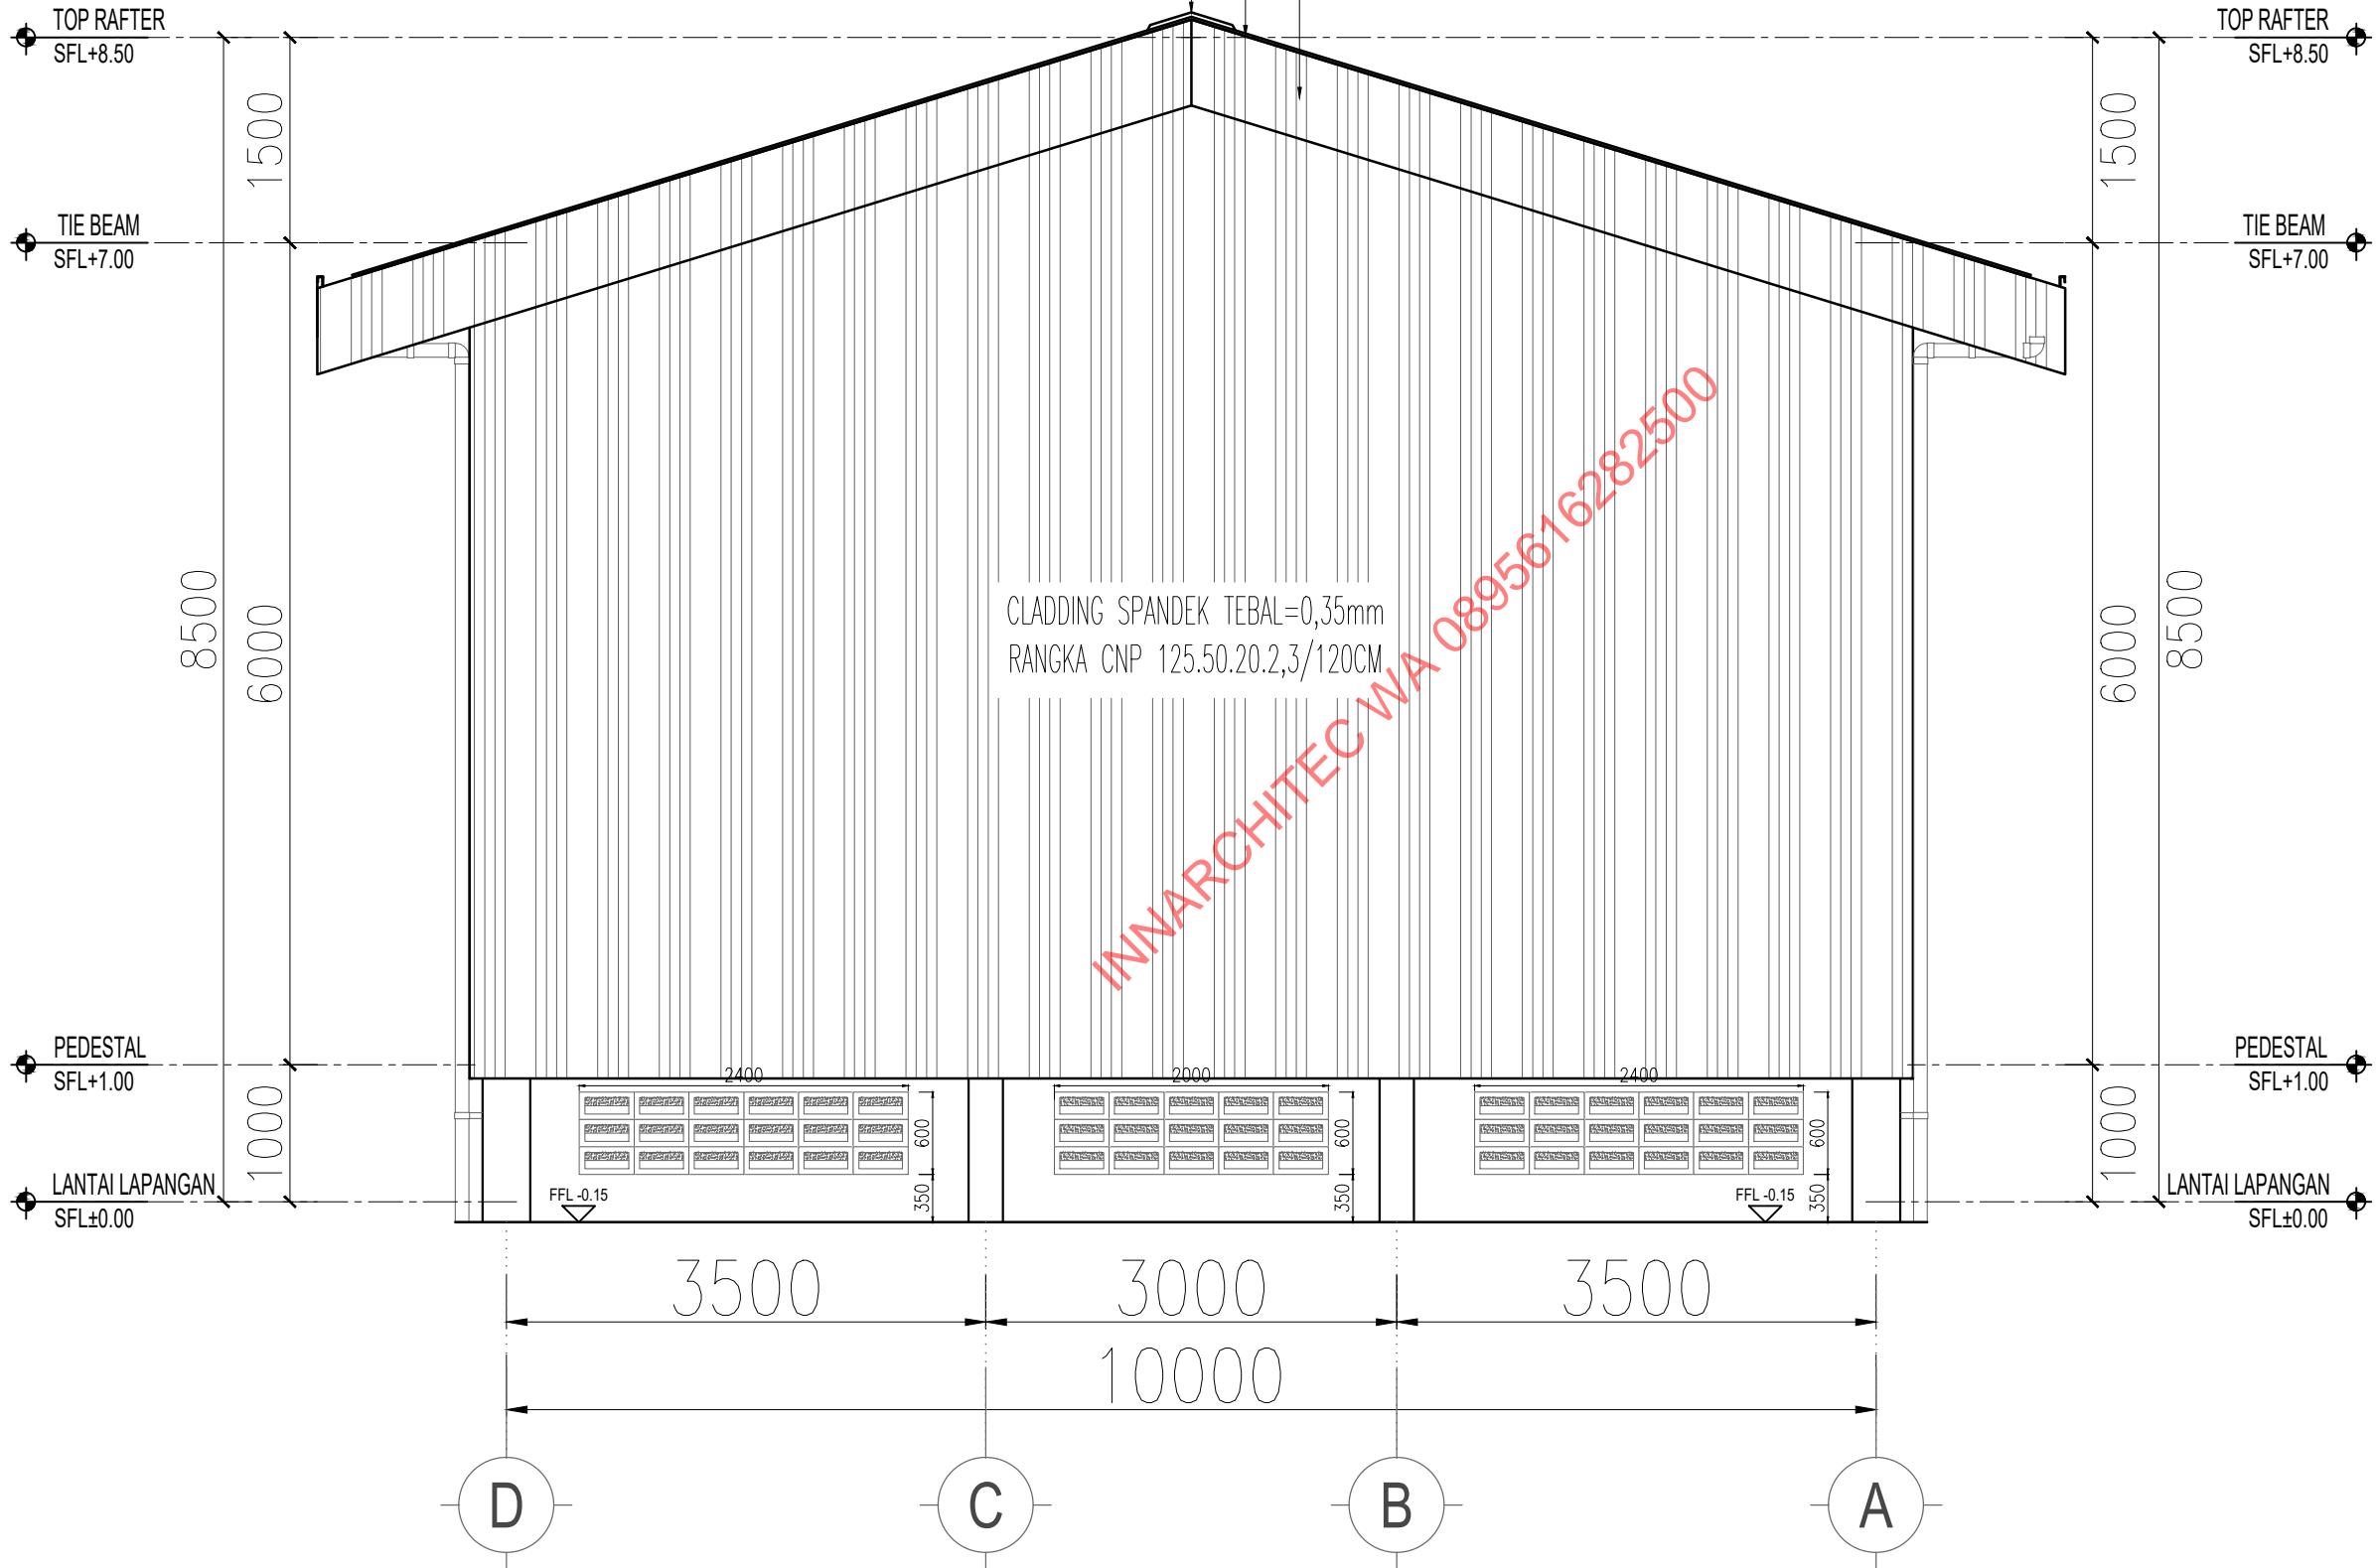

TAMPAK BELAKANG  
SKALA 1 : 40

NAMA PROYEK	
-	
LOKASI PROYEK	
-	-
PENANGGUNG JAWAB	
DIGAMBAR	PELAKSANA
DISETUVUT	PEMILIK
CATATAN	
1. PELAKSANA ATAU SUBKON WAJIB MEMERIKSA KEMBALI KESESUAIN GAMBAR DENGAN KONDISI LAPANGAN	
-	
JUDUL GAMBAR	SKALA
1.TAMPAK BELAKANG	1 : 40
TANGGAL :	REVISI :
5 APRIL 2024	R3
KODE GAMBAR	
ARS-02-04	
NO. LBR	JUMLAH LBR
04	35

NAMA PROYEK	
-	
LOKASI PROYEK	
-	-
PENANGGUNG JAWAB	
DIGAMBAR	PELAKSANA
DISETUJUI	PEMILIK
CATATAN	
1. PELAKSANA ATAU SUBKON WAJIB MEMERIKSA KEMBALI KESESUAIN GAMBAR DENGAN KONDISI LAPANGAN	
INWARCITEC WA 09861626500	
JUDUL GAMBAR	SKALA
1.POTONGAN A-A	1 : 50
TANGGAL :	REVISI :
5 APRIL 2024	R3
KODE GAMBAR	
ARS-02-07	
NO. LBR	JUMLAH LBR
07	35

