


DAFTAR GAMBAR

NOMER	NAMA GAMBAR	SKALA	KODE
BAB.01	DAFTAR GAMBAR		
1	DAFTAR GAMBAR	NTS	ARS-01-01
BAB.02	SITE PLAN		
2	SITE PLAN	1:100	ARS-02-02
BAB.03	ARSITEKTUR		
3	DENAH RENCANA GUDANG	1:100	ARS-03-03
4	DENAH RENCANA ATAP	1:100	ARS-03-04
5	TAMPAK DEPAN	1:50	ARS-03-05
6	TAMPAK BELAKANG	1:50	ARS-03-06
7	TAMPAK SAMPING KIRI	1:50	ARS-03-07
8	TAMPAK SAMPING KANAN	1:50	ARS-03-08
9	POTONGAN A-A	1:50	ARS-03-09
10	POTONGAN B-B	1:50	ARS-03-10
11	POTONGAN C-C	1:50	ARS-03-11
12	POTONGAN D-D	1:50	ARS-03-12
BAB.04	STRUKTUR		
13	DENAH PILECAP SFL-1.00 (ELEVASI BOTTOM)	1:100	STR-04-13
14	DETAIL PONDASI PC 1 DAN PC 2	1:25	STR-04-14
15	DENAH SLOOF SFL±0.00	1:100	STR-04-15
16	DENAH PLAT DAN KOLOM SFL±0.00	1:100	STR-04-16
17	DETAIL SLOOF, BALOK, DAN KOLOM	1:25	STR-04-17
18	DENAH KOLOM BAJA SFL+1.00	1:100	STR-04-18
19	DENAH BALOK RELL PINTU SFL+3.80	1:100	STR-04-19
20	DENAH REGEL SFL+7.00	1:100	STR-04-20
21	DENAH RAFTER/KUDA-KUDA	1:100	STR-04-21
22	DENAH RANGKA ATAP	1:100	STR-04-22


DAFTAR GAMBAR

NAMA PROYEK	
<p style="text-align: center;">PROJECT GUDANG</p> <p style="text-align: center;">PT. JOJOPLAST GEMILANG</p>	
LOKASI PROYEK	
<p style="text-align: center;">jl. Raya Sawocangkring no.102</p> <p style="text-align: center;">Wonoayu, Sidoarjo - JATIM</p>	
PENANGGUNG JAWAB	
DIGAMBAR	PELAKSANA
DISETUJUI	PEMILIK
CATATAN	
<p>1. PELAKSANA ATAU SUBKON WAJIB MEMERIKSA KEMBALI KESESUAIN GAMBAR DENGAN KONDISI LAPANGAN</p>	
JUDUL GAMBAR	SKALA
1. DAFTAR GAMBAR	NTS
TANGGAL :	REVISI :
15 NOVEMBER 2024	R1
KODE GAMBAR	
ARS-01-01	
NO. LBR	JUMLAH LBR
01	33

NAMA PROYEK	
PROJECT GUDANG PT. JOJOPLAST GEMILANG	
LOKASI PROYEK	
jl. Raya Sawocangkring no.102 Wonoayu, Sidoarjo - JATIM	
PENANGGUNG JAWAB	
DIGAMBAR	PELAKSANA
DISETUJU	PEMILIK
CATATAN	
1. PELAKSANA ATAU SUBKON WAJIB MEMERIKSA KEMBALI KESESUAIN GAMBAR DENGAN KONDISI LAPANGAN	
JUDUL GAMBAR	SKALA
TANGGAL :	REVISI :
15 NOVEMBER 2024	R1
KODE GAMBAR	
STR-03-03	
NO. LBR	JUMLAH LBR
03	33

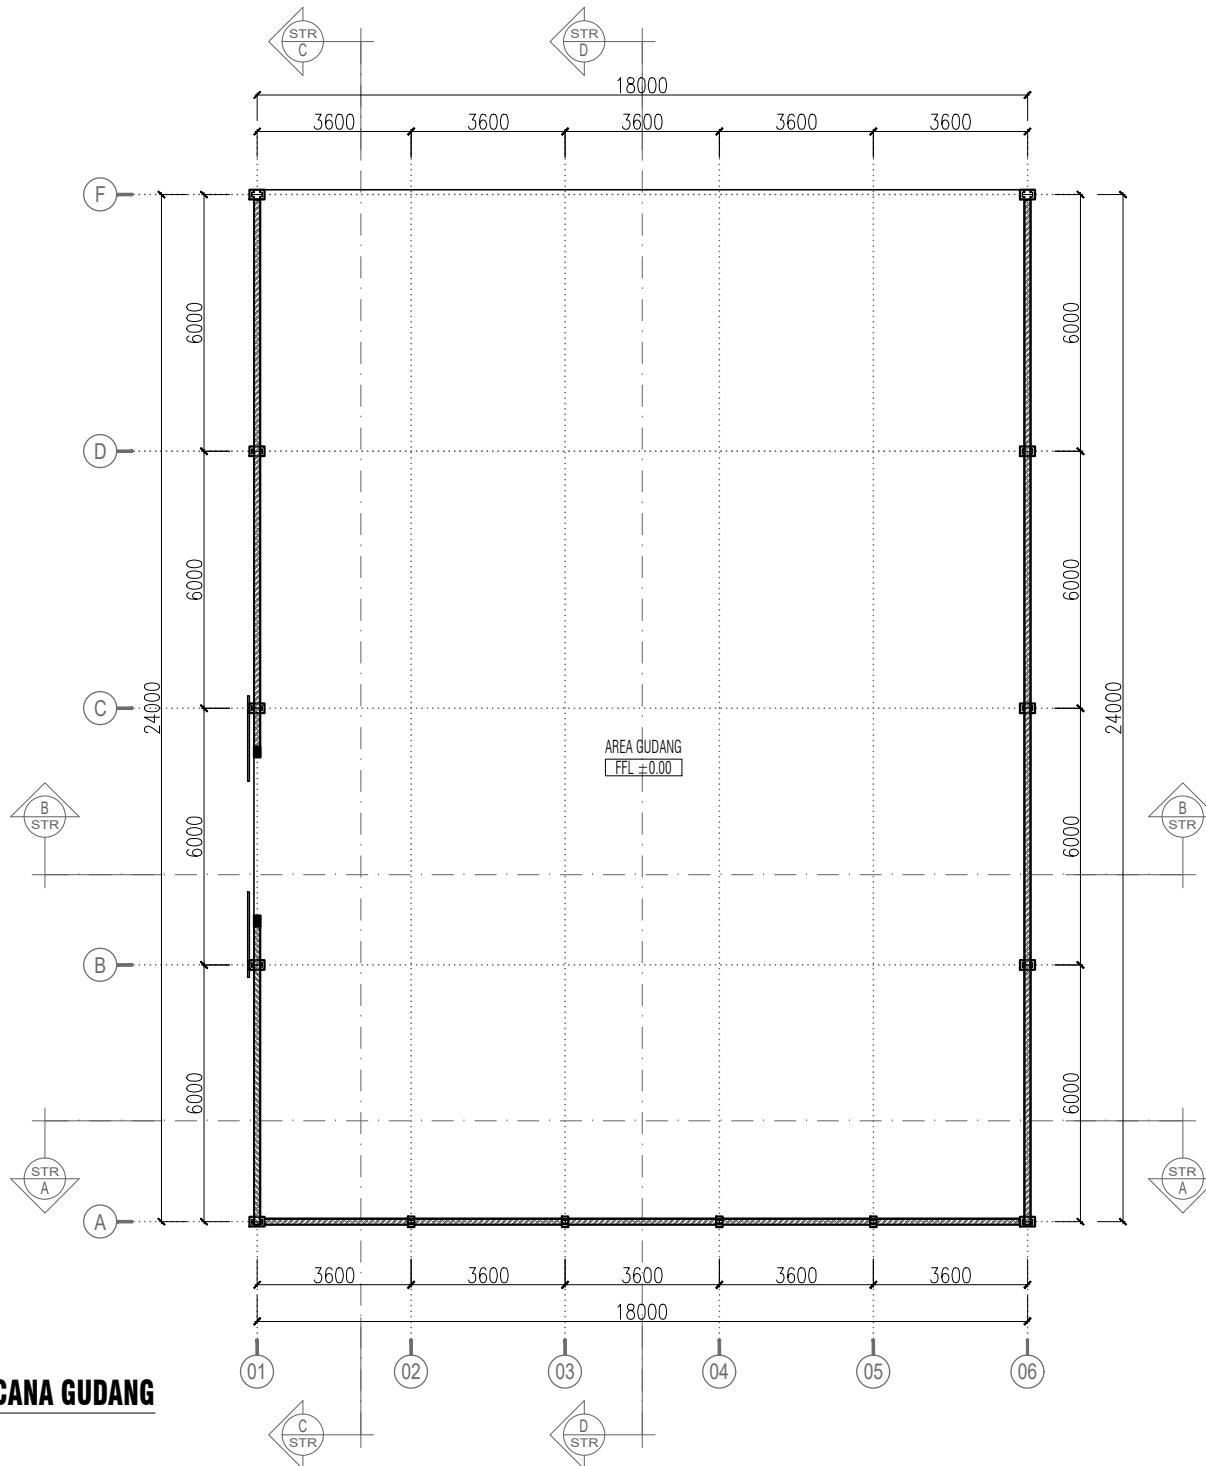

NAMA PROYEK	
PROJECT GUDANG PT. JOJOPLAST GEMILANG	
LOKASI PROYEK	
jl. Raya Sawocangkring no.102 Wonoayu, Sidoarjo - JATIM	
PENANGGUNG JAWAB	
DIGAMBAR	PELAKSANA
DISETUJU	PEMILIK
CATATAN	
1. PELAKSANA ATAU SUBKON WAJIB MEMERIKSA KEMBALI KESESUAIN GAMBAR DENGAN KONDISI LAPANGAN	
JUDUL GAMBAR	SKALA
TANGGAL :	REVISI :
15 NOVEMBER 2024	R1
KODE GAMBAR	
STR-03-05	
NO. LBR	JUMLAH LBR
05	33

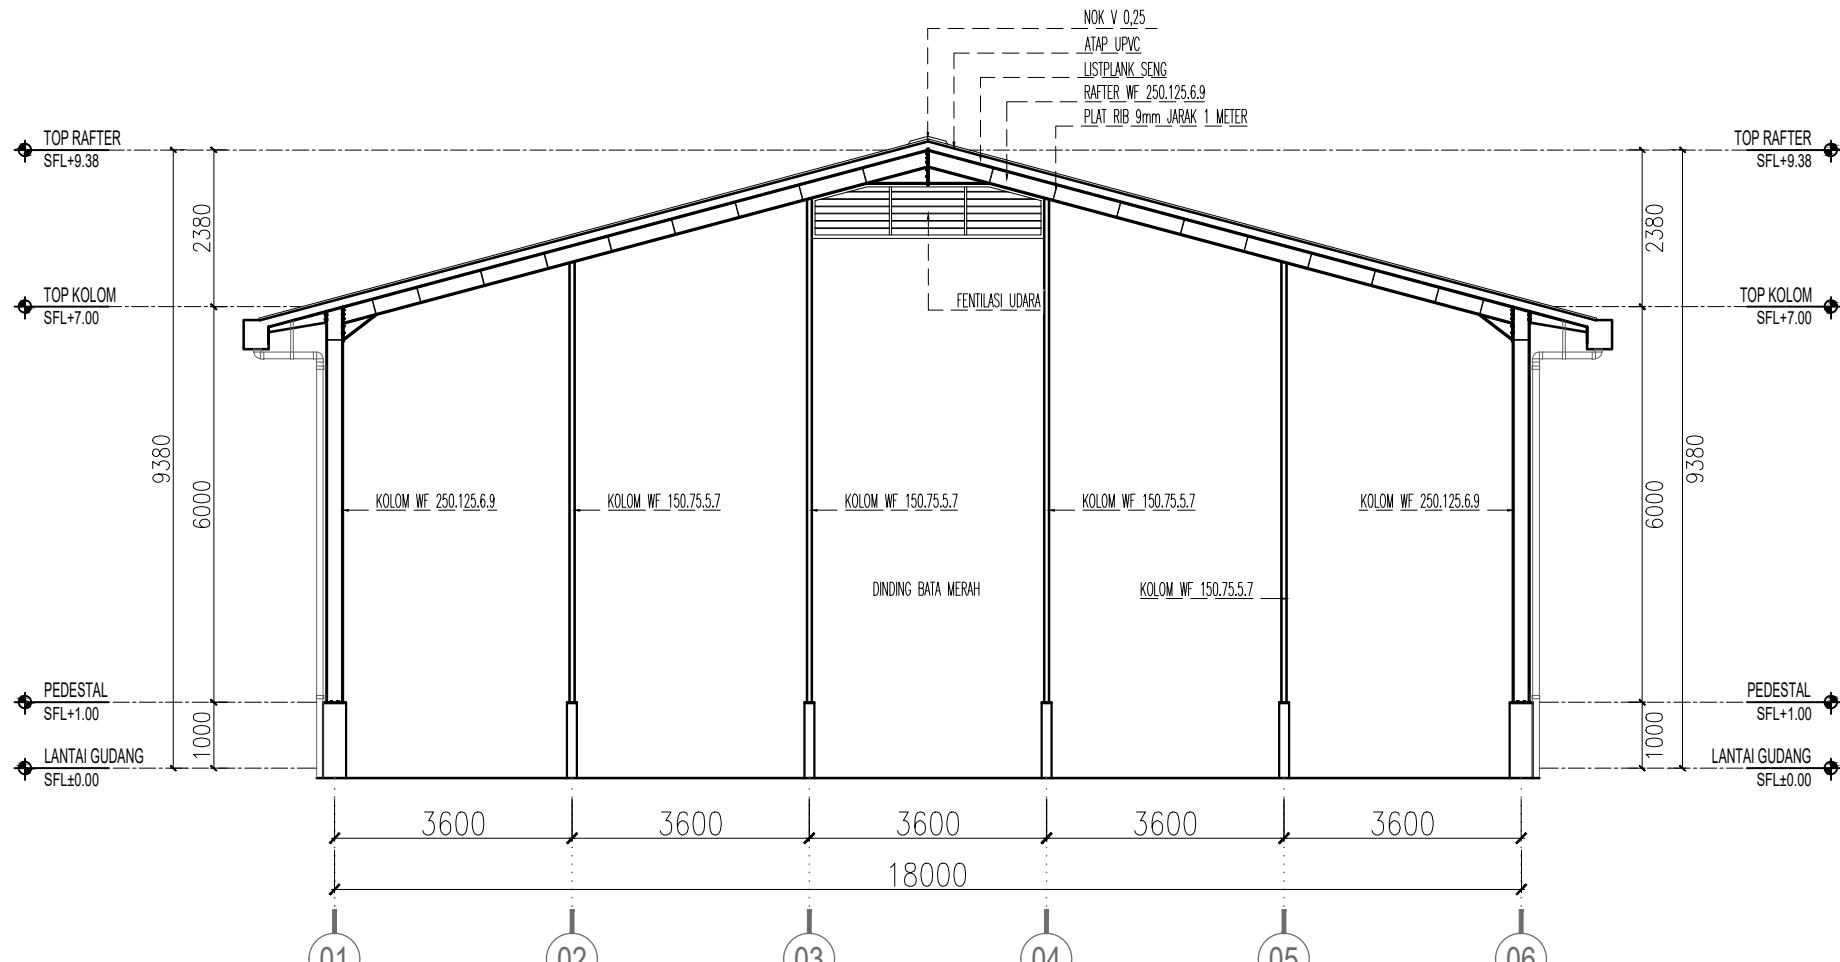

Tampak depan

NAMA PROYEK	
PROJECT GUDANG PT. JOJOPLAST GEMILANG	
LOKASI PROYEK	
jl. Raya Sawocangkring no.102 Wonoayu, Sidoarjo - JATIM	
PENANGGUNG JAWAB	
DIGAMBAR	PELAKSANA
DISETUJU	PEMILIK
CATATAN	
1. PELAKSANA ATAU SUBKON WAJIB MEMERIKSA KEMBALI KESESUAIN GAMBAR DENGAN KONDISI LAPANGAN	
JUDUL GAMBAR	SKALA
TANGGAL :	REVISI :
15 NOVEMBER 2024	R1
KODE GAMBAR	
STR-03-06	
NO. LBR	JUMLAH LBR
06	33

