


# DAFTAR GAMBAR

NOMER	NAMA GAMBAR	SKALA	KODE
<b>BAB.01</b>	<b>DAFTAR GAMBAR</b>		
1	DAFTAR GAMBAR 1	NTS	ARS-01-01
<b>BAB.02</b>	<b>ARSITEKTUR</b>		
2	DENAH GOR BADMINTON DAN DENAH ATAP	1:100	ARS-02-02
3	TAMPAK DEPAN	1:40	ARS-02-03
4	TAMPAK BELAKANG	1:40	ARS-02-04
5	TAMPAK SAMPING KANAN	1:50	ARS-02-05
6	TAMPAK SAMPING KIRI	1:50	ARS-02-06
7	POTONGAN A-A	1:50	ARS-02-07
8	POTONGAN B-B	1:50	ARS-02-08
9	POTONGAN C-C	1:50	ARS-02-09
10	POTONGAN D-D	1:50	ARS-02-10
<b>BAB.03</b>	<b>STRUKTUR</b>		
11	DENAH PILECAP SFL-1.00 (ELEVASI BOTTOM)	1:100	STR-03-11
12	DETAIL PONDASI PC 1	1:25	STR-03-12
13	DENAH SLOOR SFL±0.00	1:100	STR-03-13
14	DENAH PLAT DAN KOLOM SFL±0.00	1:100	STR-03-14
15	DETAIL SLOOR, BALOK, DAN KOLOM	1:25	STR-03-15
16	DENAH KOLOM BAJA SFL+1.00	1:100	STR-03-16
17	DENAH BALOK RELL PINTU SFL+3.25	1:100	STR-03-17
18	DENAH TIE BEAM SFL+7.00	1:100	STR-03-18
19	DENAH RAFTER/KUDA-KUDA	1:100	STR-03-19
20	DENAH RANGKA ATAP	1:100	STR-03-20
21	POTONGAN B-B (KEY SECTION)	1:50	STR-03-21
22	DETAIL 1 (BASEPLATE DAN ANGKUR)	1:25	STR-03-22
23	DETAIL 2 (SAMBUNGAN RAFTER)	1:10	STR-03-23
24	DETAIL 3 (SAMBUNGAN RAFTER DAN KOLOM)	1:10	STR-03-24
25	DETAIL 4 (SAMBUNGAN RAFTER DAN KOLOM)	1:10	STR-03-25
26	DETAIL PEMASANGAN SAGROD GORDING	1:10	STR-03-26
27	DETAIL TALANG	1:10	STR-03-27

## DAFTAR GAMBAR

<b>NAMA PROYEK</b>	
-	
<b>LOKASI PROYEK</b>	
-	
<b>PENANGGUNG JAWAB</b>	
<u>DIGAMBAR</u>	<u>PELAKSANA</u>
<u>DISETJUUI</u>	<u>PEMILIK</u>
<b>CATATAN</b>	
<p>1. PELAKSANA ATAU SUBKON WAJIB MEMERIKSA KEMBALI KESESUAIN GAMBAR DENGAN KONDISI LAPANGAN</p>	
<b>JUDUL GAMBAR</b>	
SKALA	
1. DAFTAR GAMBAR	
NTS	
<b>TANGGAL :</b>	
REVISI :	
5 APRIL 2024	
<b>R3</b>	
<b>KODE GAMBAR</b>	
ARS-01-01	
<b>NO. LBR</b>	<b>JUMLAH LBR</b>
01	35

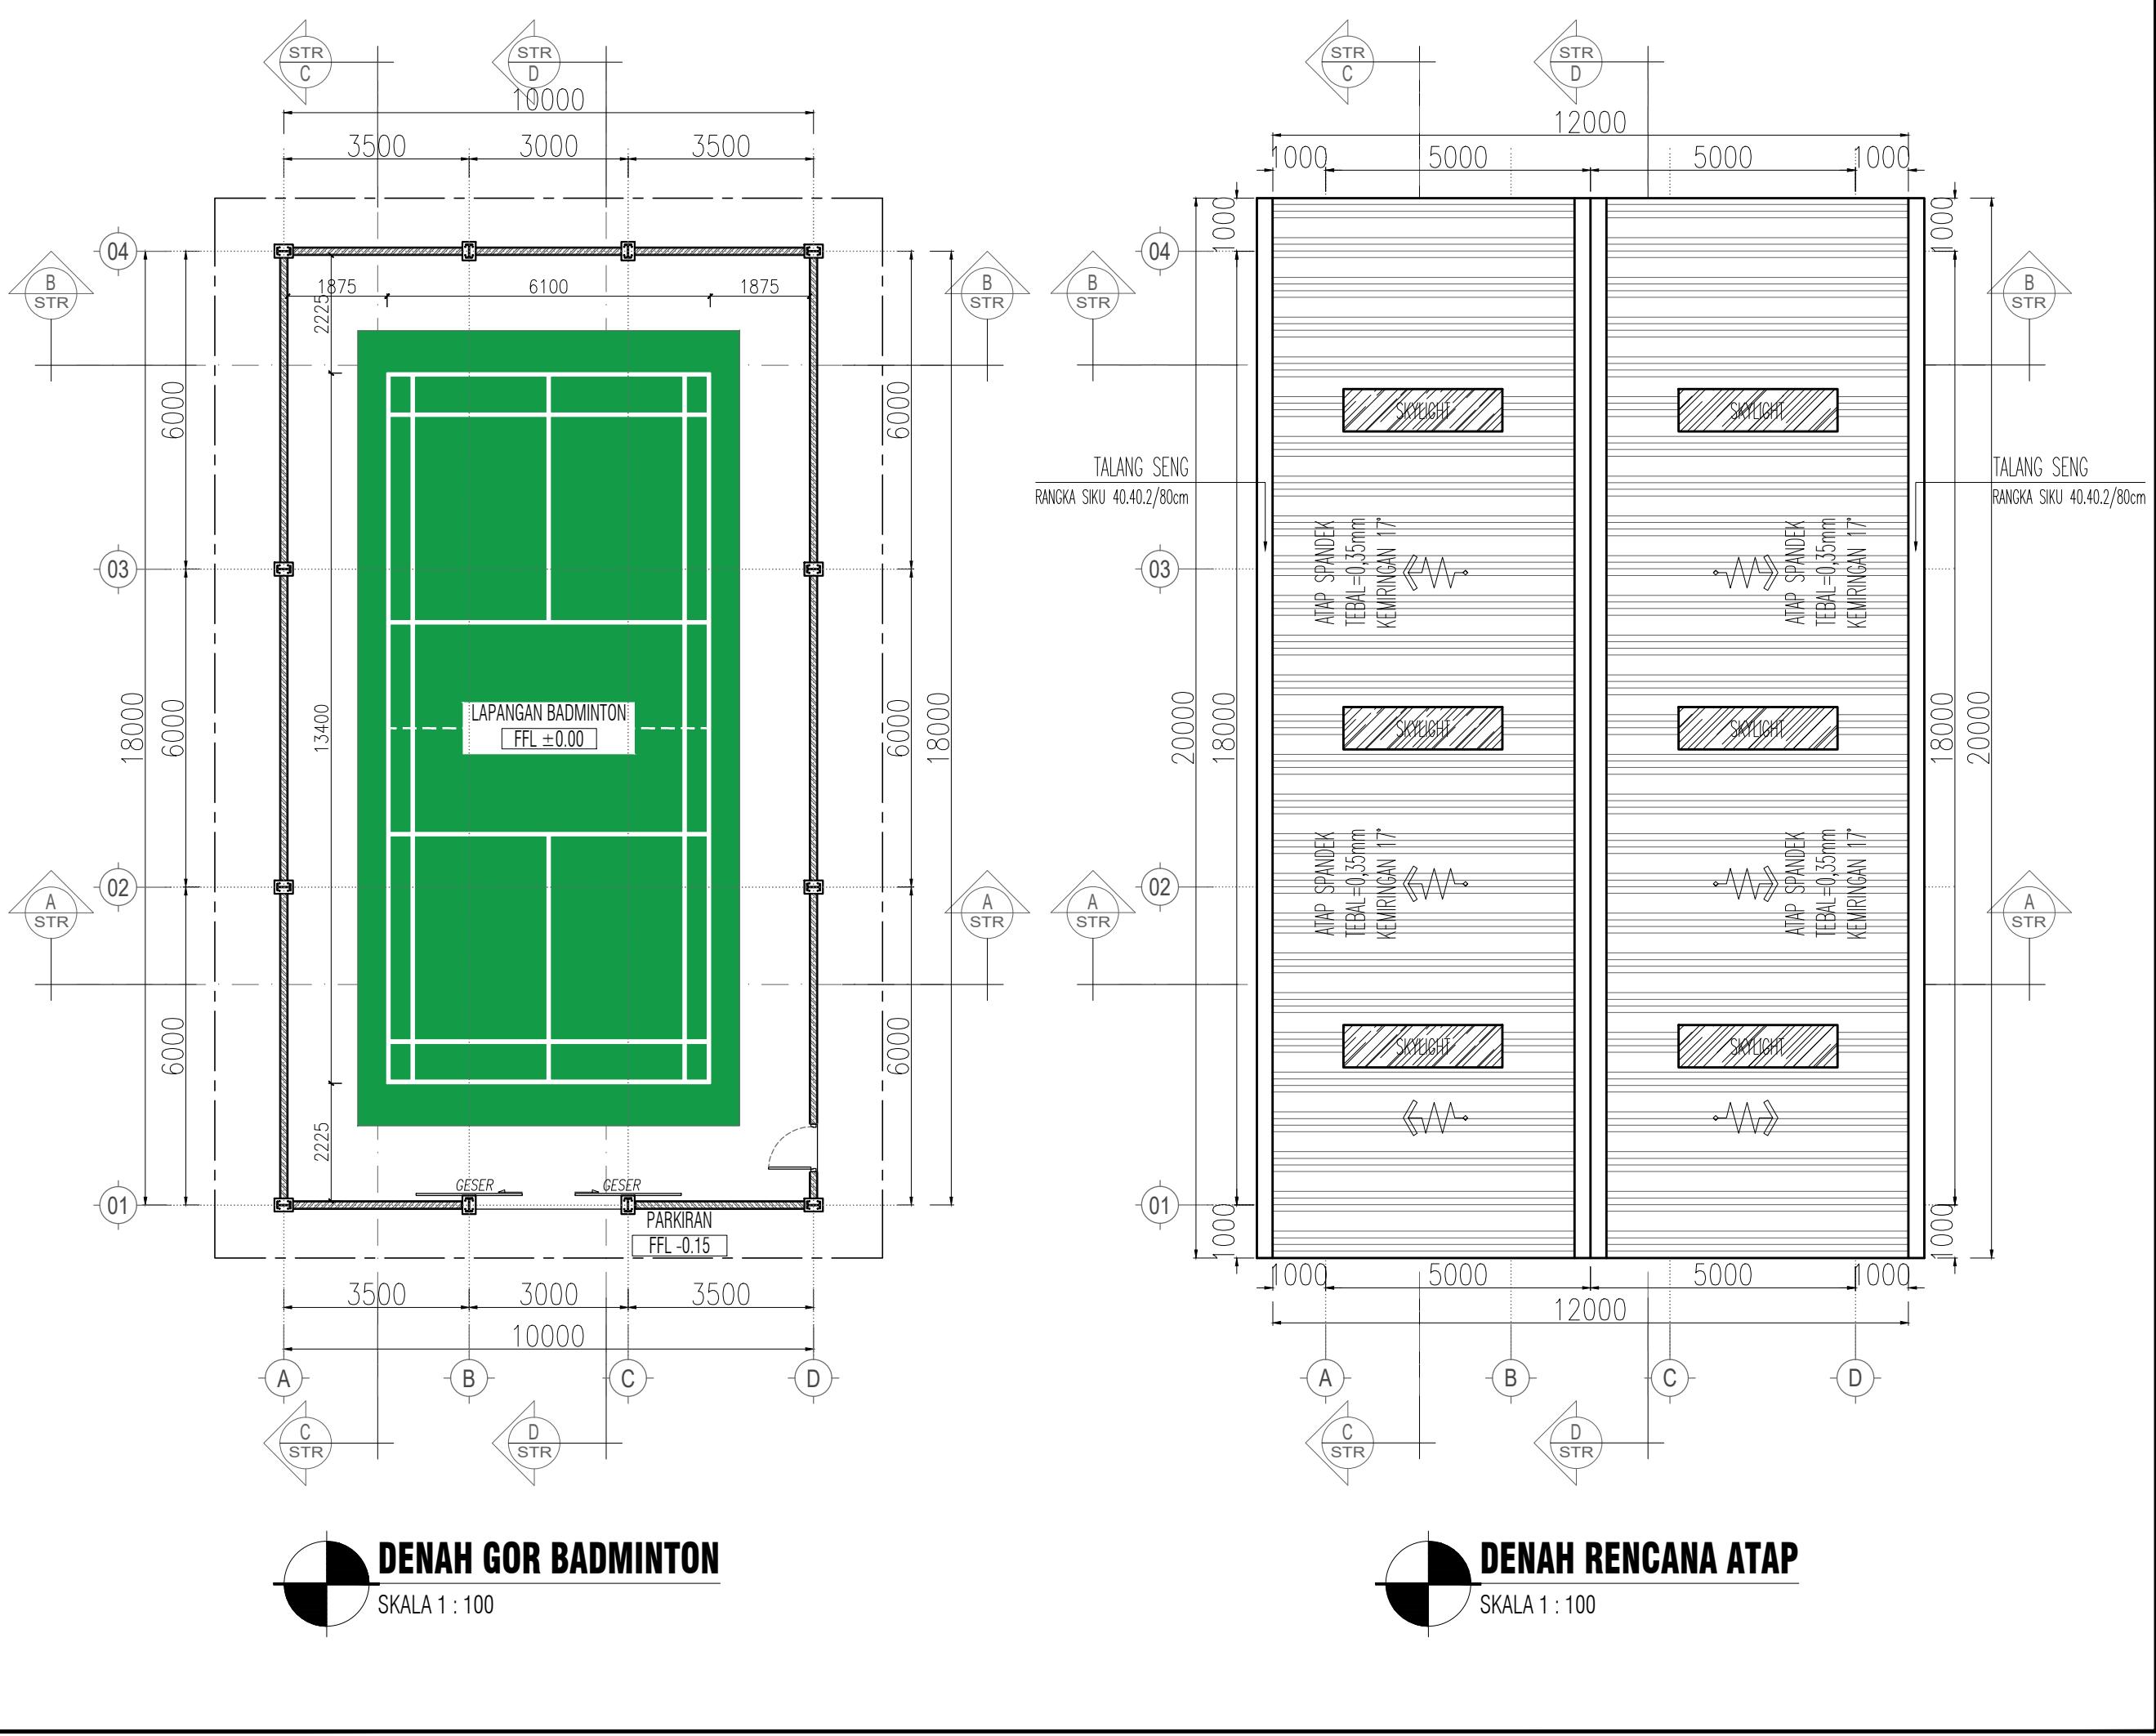


NOK V 0,25

ATAP SPANDEK TEBAL=0,35mm

## LISTPLANK SPANDEK TEBAL=0,35mm

RANGKA SIKU 40.40.2/80cm

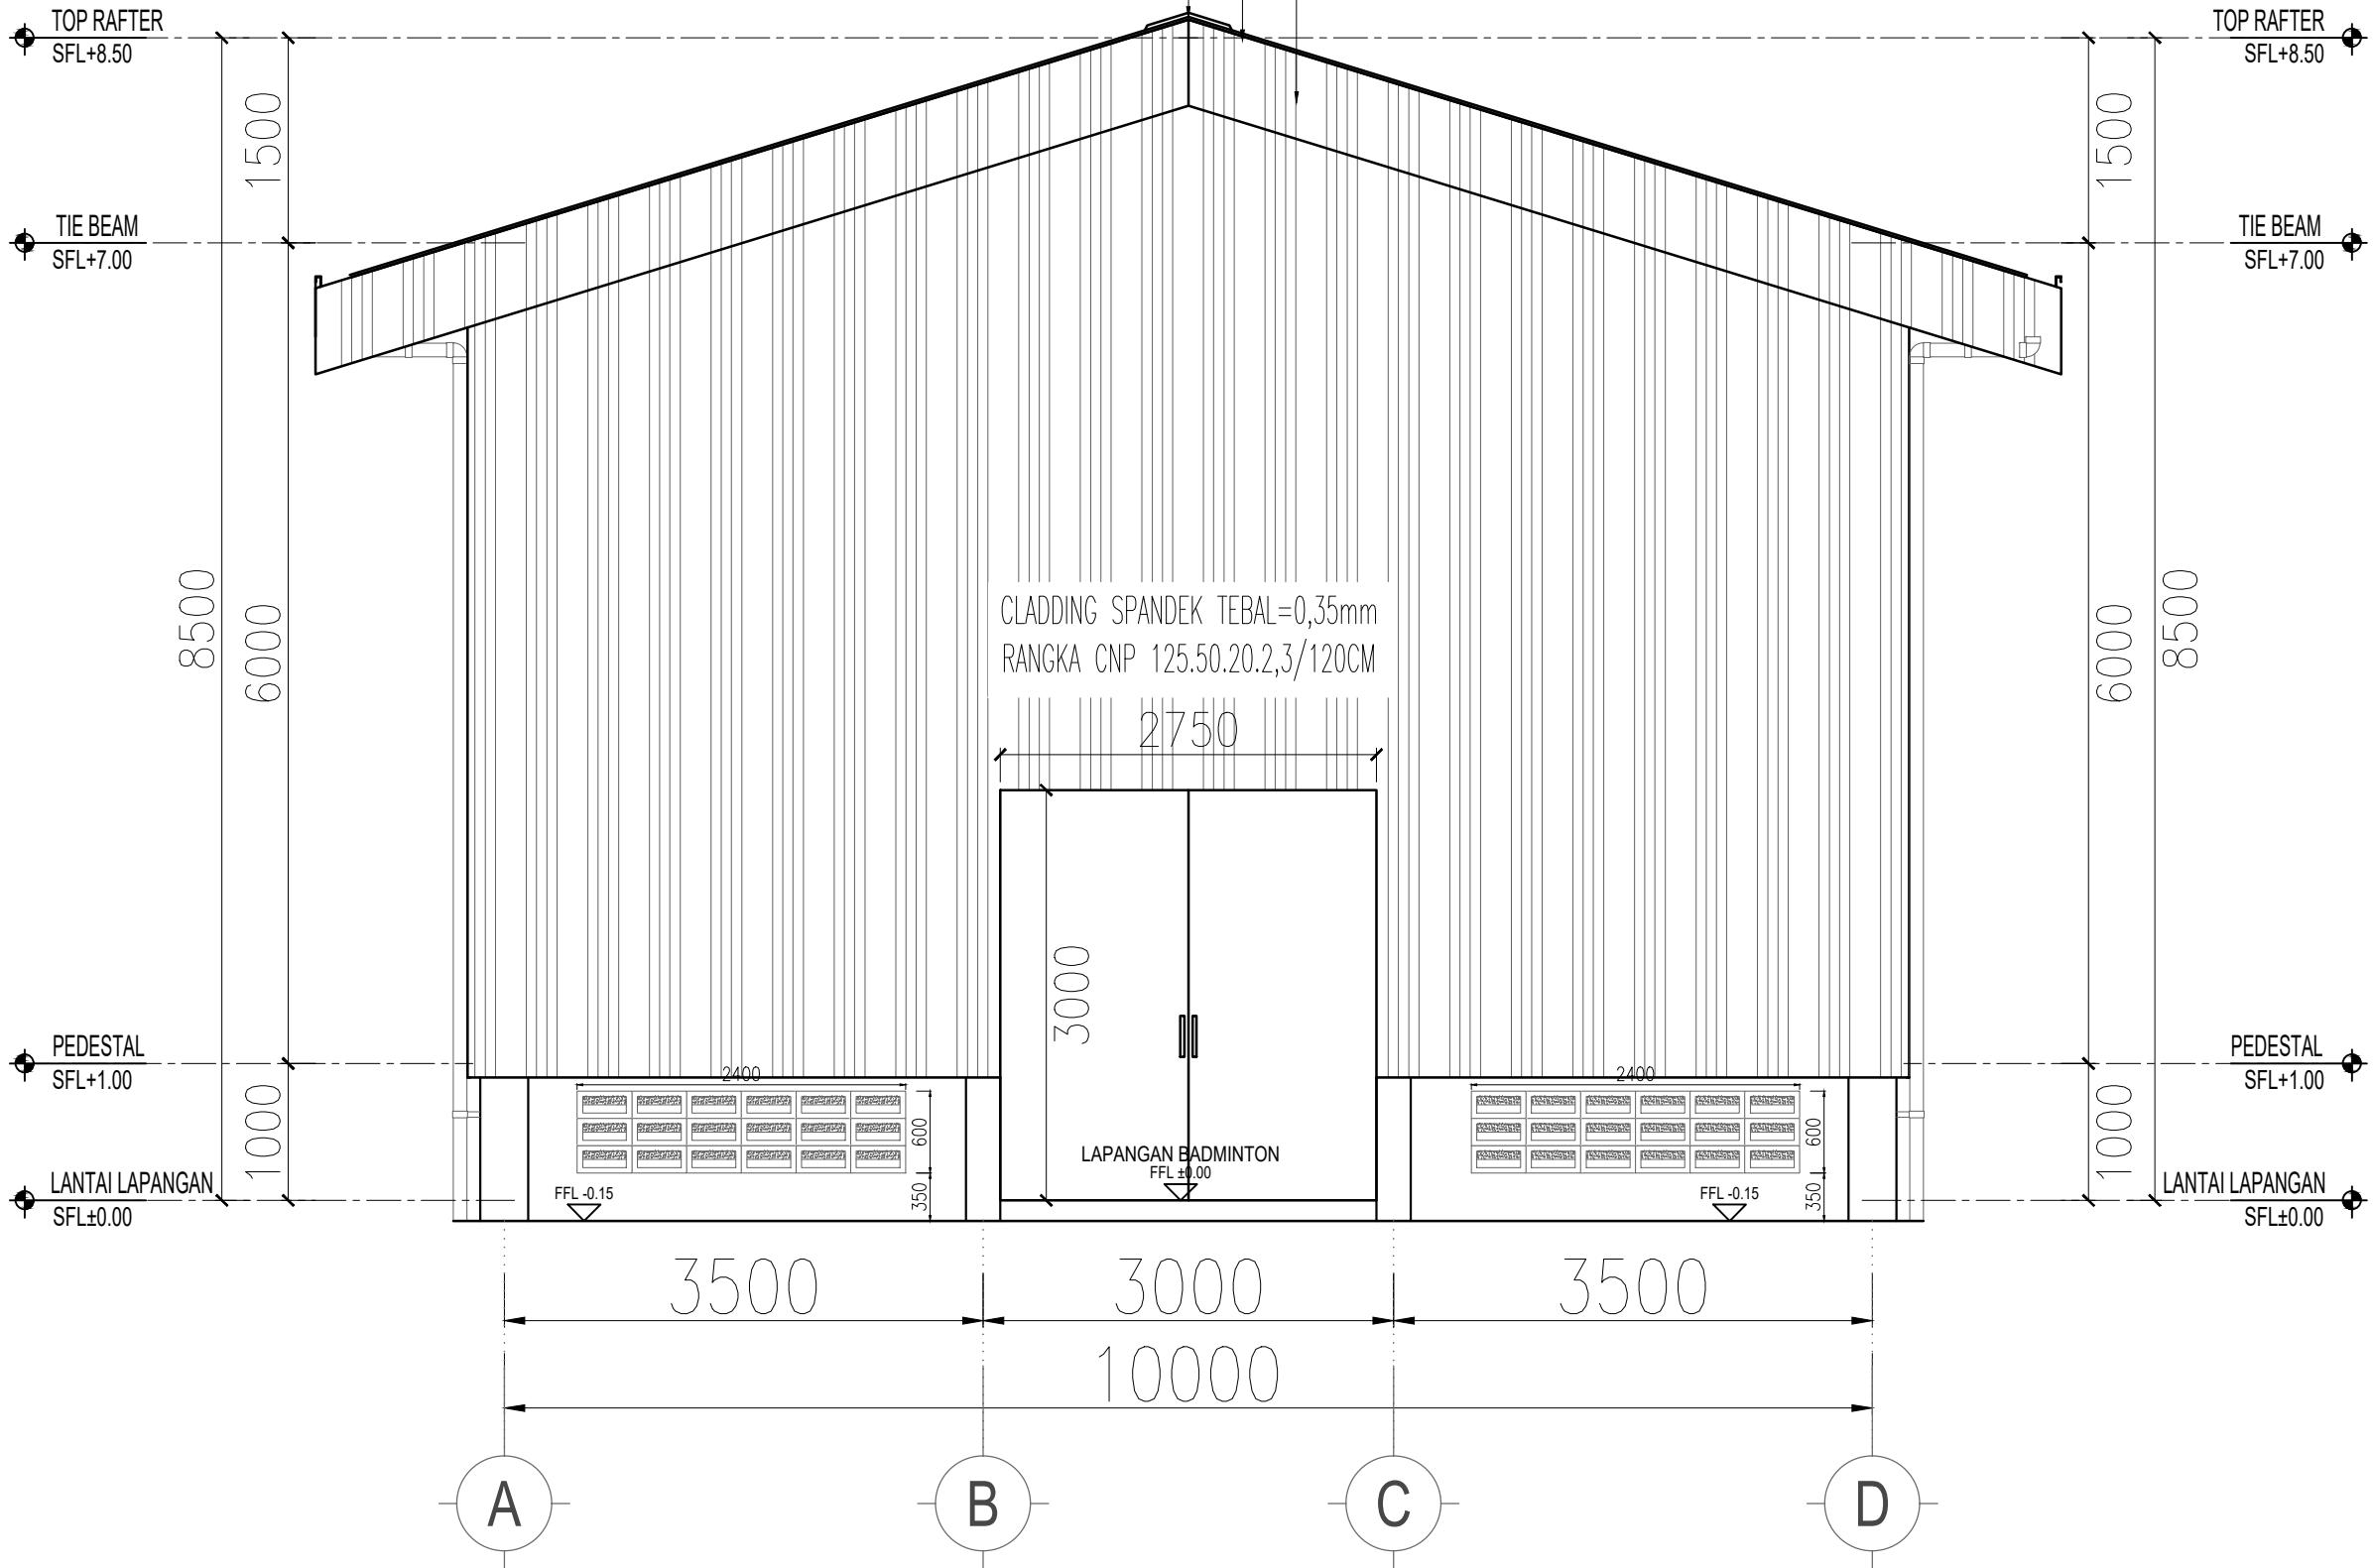

# TAMPAK DEPAN

---

SKALA 1 : 40


NAMA PROYEK	
-	
LOKASI PROYEK	
-	
-	
PENANGGUNG JAWAB	
DIGAMBAR	PELAKSANA
DISETUJUI	PEMILIK
CATATAN	
<p>1. PELAKSANA ATAU SUBKON WAJIB MEMERIKSA KEMBALI KESESUAIN GAMBAR DENGAN KONDISI LAPANGAN</p>	
JUDUL GAMBAR	
SKALA	
1.TAMPAK DEPAN	
1 : 40	
TANGGAL :	
REVISI :	
5 APRIL 2024	
<b>R3</b>	
KODE GAMBAR	
ARS-02-03	
NO. LBR	JUMLAH LBR
03	35

NOK V 0,25

ATAP SPANDEK TEBAL=0,35mm

LISTPLANK SPANDEK TEBAL=0,35mm

RANGKA SIKU 40.40.2/80cm

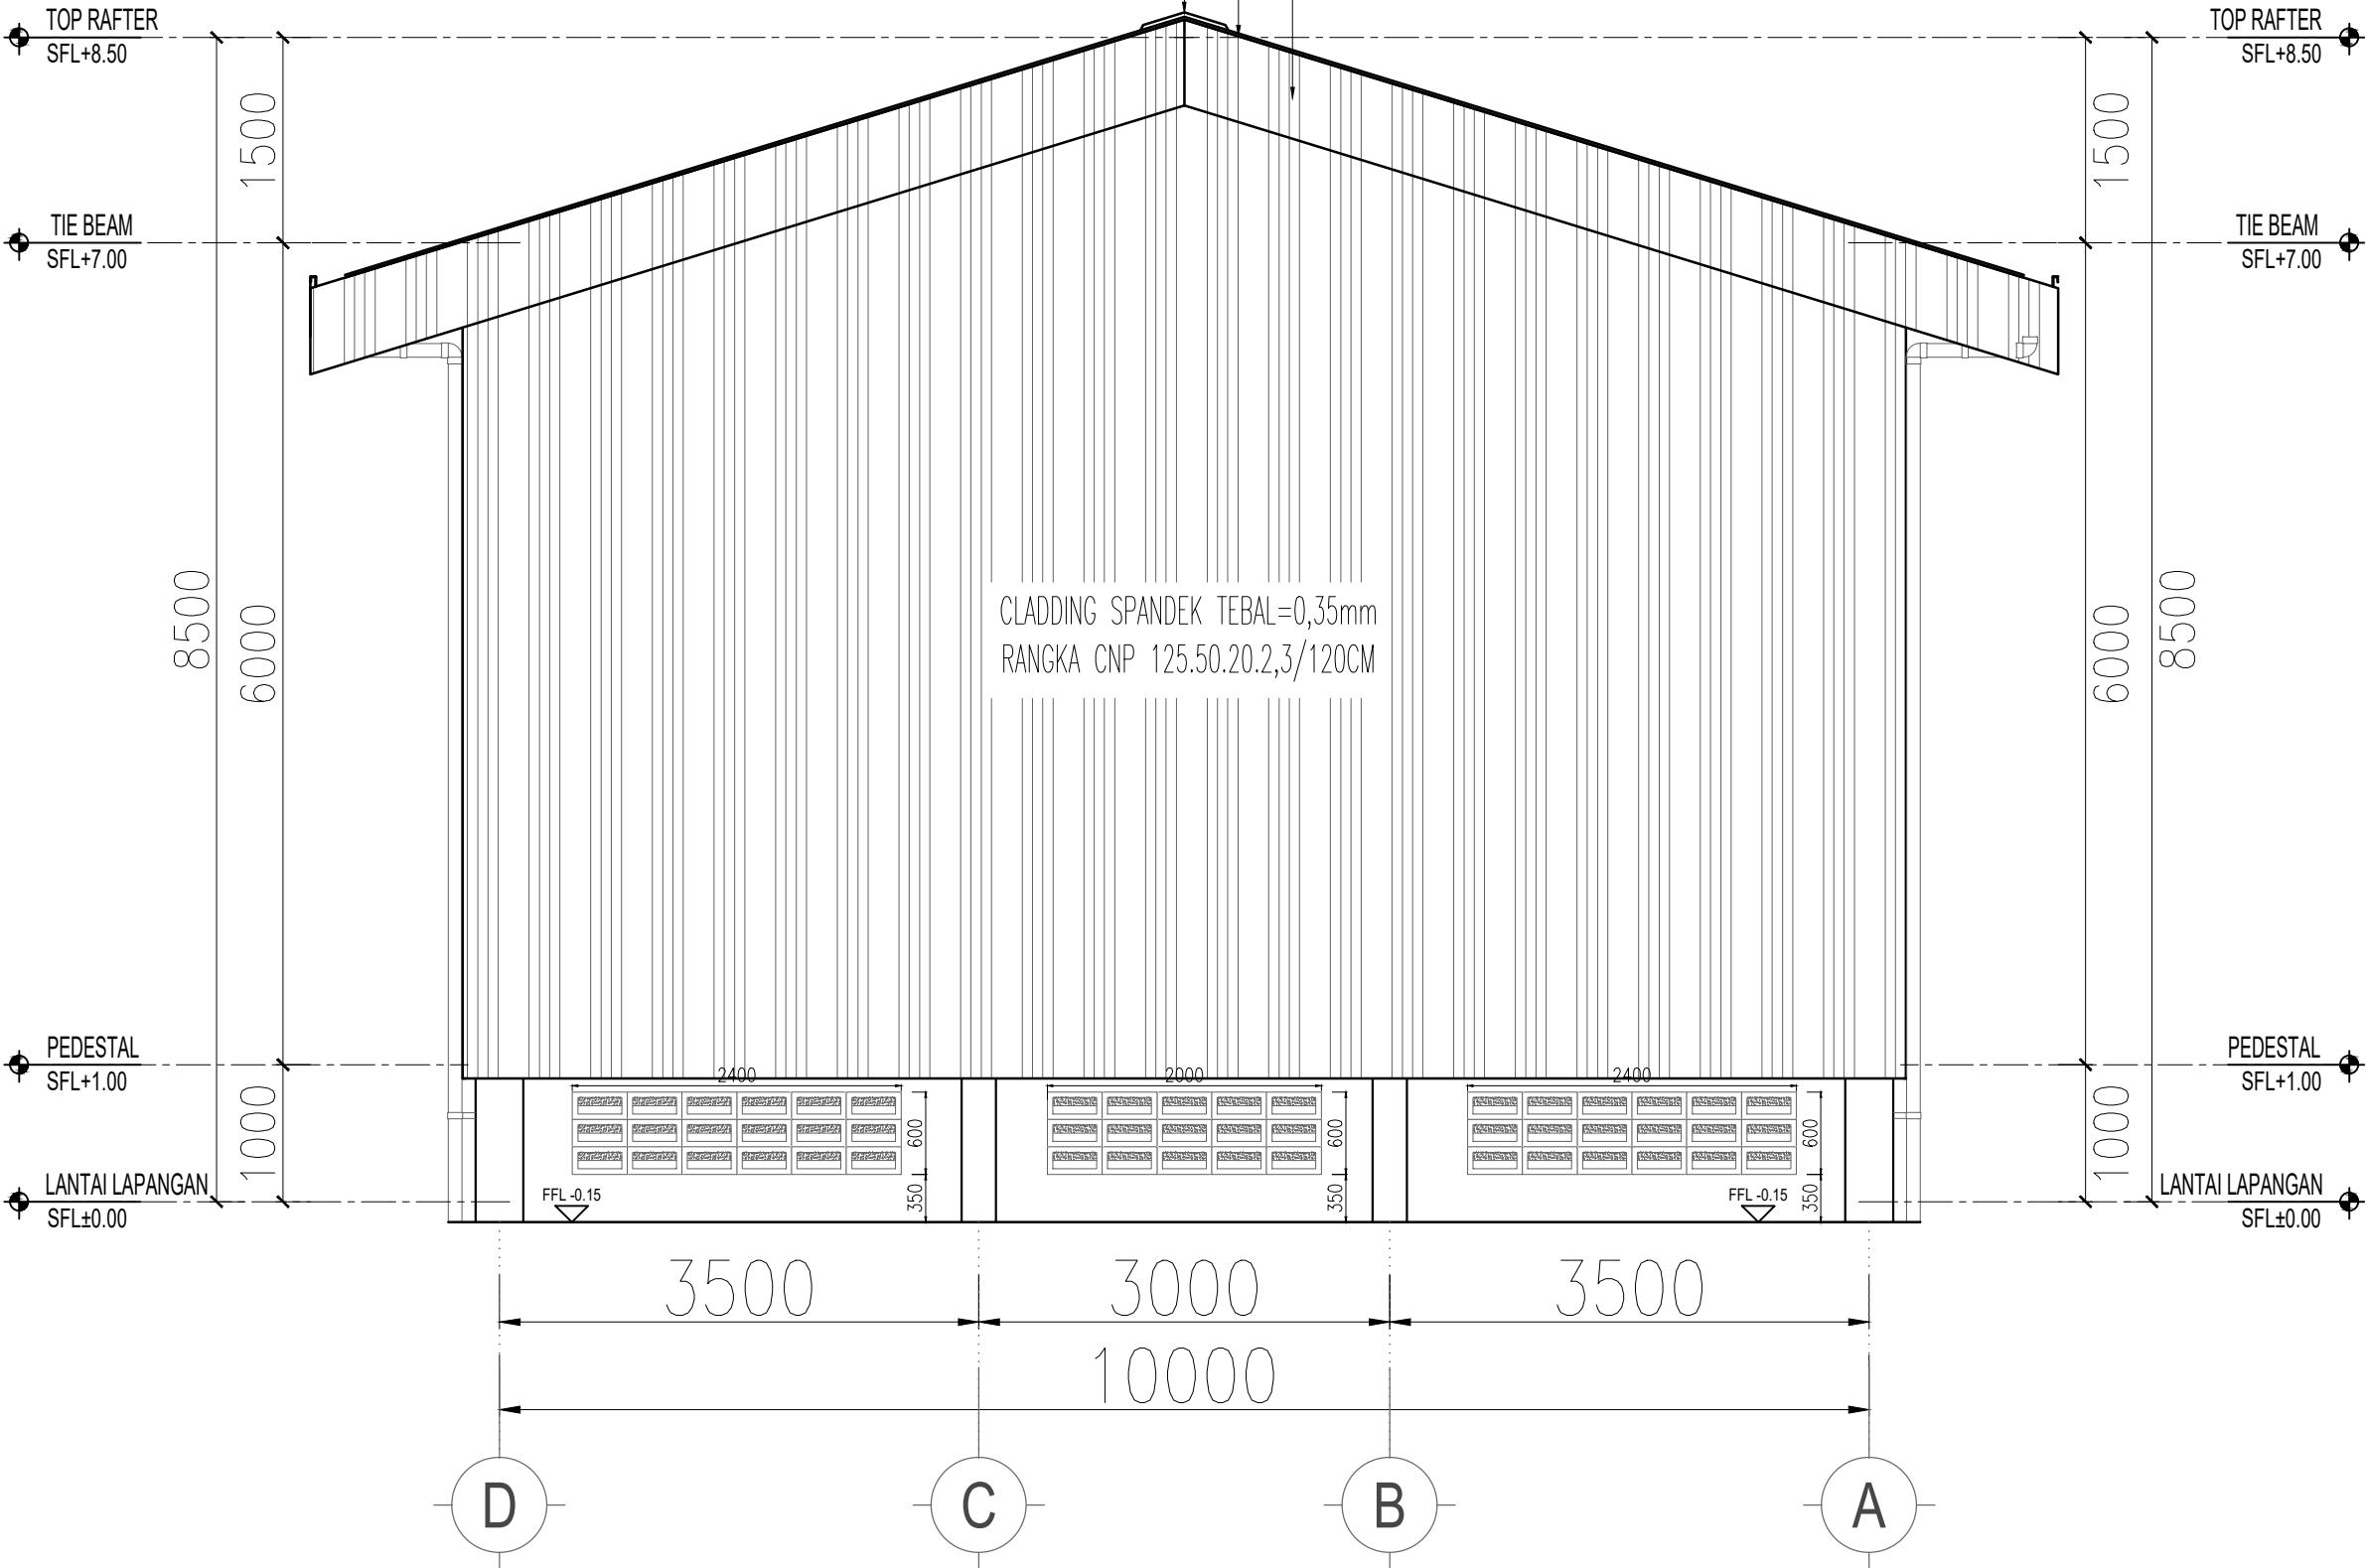

**TAMPAK BELAKANG**

SKALA 1 : 40

NAMA PROYEK	
-	
LOKASI PROYEK	
-	-
PENANGGUNG JAWAB	
DIGAMBAR	PELAKSANA
DISETUVUT	PEMILIK
CATATAN	
1. PELAKSANA ATAU SUBKON WAJIB MEMERIKSA KEMBALI KESESUAIN GAMBAR DENGAN KONDISI LAPANGAN	
-	
JUDUL GAMBAR	SKALA
1.TAMPAK BELAKANG	1 : 40
TANGGAL :	REVISI :
5 APRIL 2024	<b>R3</b>
KODE GAMBAR	
ARS-02-04	
NO. LBR	JUMLAH LBR
04	35

NAMA PROYEK	
-	
LOKASI PROYEK	
-	-
PENANGGUNG JAWAB	
DIGAMBAR	PELAKSANA
DISETUJUI	PEMILIK
CATATAN	
1. PELAKSANA ATAU SUBKON WAJIB MEMERIKSA KEMBALI KESESUAIN GAMBAR DENGAN KONDISI LAPANGAN	
-	
JUDUL GAMBAR	SKALA
1.POTONGAN A-A	1 : 50
TANGGAL :	REVISI :
5 APRIL 2024	R3
KODE GAMBAR	
ARS-02-07	
NO. LBR	JUMLAH LBR
07	35

