


DAFTAR GAMBAR

NOMER	NAMA GAMBAR	SKALA	KODE
BAB.01	DAFTAR GAMBAR		
1	DAFTAR GAMBAR 1	NTS	ARS-01-01
BAB.02	ARSITEKTUR		
2	DENAH GOR BADMINTON DAN DENAH ATAP	1:100	ARS-02-02
3	TAMPAK DEPAN	1:40	ARS-02-03
4	TAMPAK BELAKANG	1:40	ARS-02-04
5	TAMPAK SAMPING KANAN	1:50	ARS-02-05
6	TAMPAK SAMPING KIRI	1:50	ARS-02-06
7	POTONGAN A-A	1:50	ARS-02-07
8	POTONGAN B-B	1:50	ARS-02-08
9	POTONGAN C-C	1:50	ARS-02-09
10	POTONGAN D-D	1:50	ARS-02-10
BAB.03	STRUKTUR		
11	DENAH PILECAP SFL-1.00 (ELEVASI BOTTOM)	1:100	STR-03-11
12	DETAIL PONDASI PC 1	1:25	STR-03-12
13	DENAH SLOOR SFL±0.00	1:100	STR-03-13
14	DENAH PLAT DAN KOLOM SFL±0.00	1:100	STR-03-14
15	DETAIL SLOOR, BALOK, DAN KOLOM	1:25	STR-03-15
16	DENAH KOLOM BAJA SFL+1.00	1:100	STR-03-16
17	DENAH BALOK RELL PINTU SFL+3.25	1:100	STR-03-17
18	DENAH TIE BEAM SFL+7.00	1:100	STR-03-18
19	DENAH RAFTER/KUDA-KUDA	1:100	STR-03-19
20	DENAH RANGKA ATAP	1:100	STR-03-20
21	POTONGAN B-B (KEY SECTION)	1:50	STR-03-21
22	DETAIL 1 (BASEPLATE DAN ANGKUR)	1:25	STR-03-22
23	DETAIL 2 (SAMBUNGAN RAFTER)	1:10	STR-03-23
24	DETAIL 3 (SAMBUNGAN RAFTER DAN KOLOM)	1:10	STR-03-24
25	DETAIL 4 (SAMBUNGAN RAFTER DAN KOLOM)	1:10	STR-03-25
26	DETAIL PEMASANGAN SAGROD GORDING	1:10	STR-03-26
27	DETAIL TALANG	1:10	STR-03-27

DAFTAR GAMBAR

NAMA PROYEK	
-	
LOKASI PROYEK	
-	
-	
PENANGGUNG JAWAB	
<u>DIGAMBAR</u>	<u>PELAKSANA</u>
<u>DISETUJUI</u>	<u>PEMILIK</u>
CATATAN	
<p>1. PELAKSANA ATAU SUBKON WAJIB MEMERIKSA KEMBALI KESESUAIN GAMBAR DENGAN KONDISI LAPANGAN</p>	
JUDUL GAMBAR	
SKALA	
1. DAFTAR GAMBAR	
NTS	
TANGGAL :	
REVISI :	
5 APRIL 2024	
R3	
KODE GAMBAR	
ARS-01-01	
NO. LBR	JUMLAH LBR
01	35

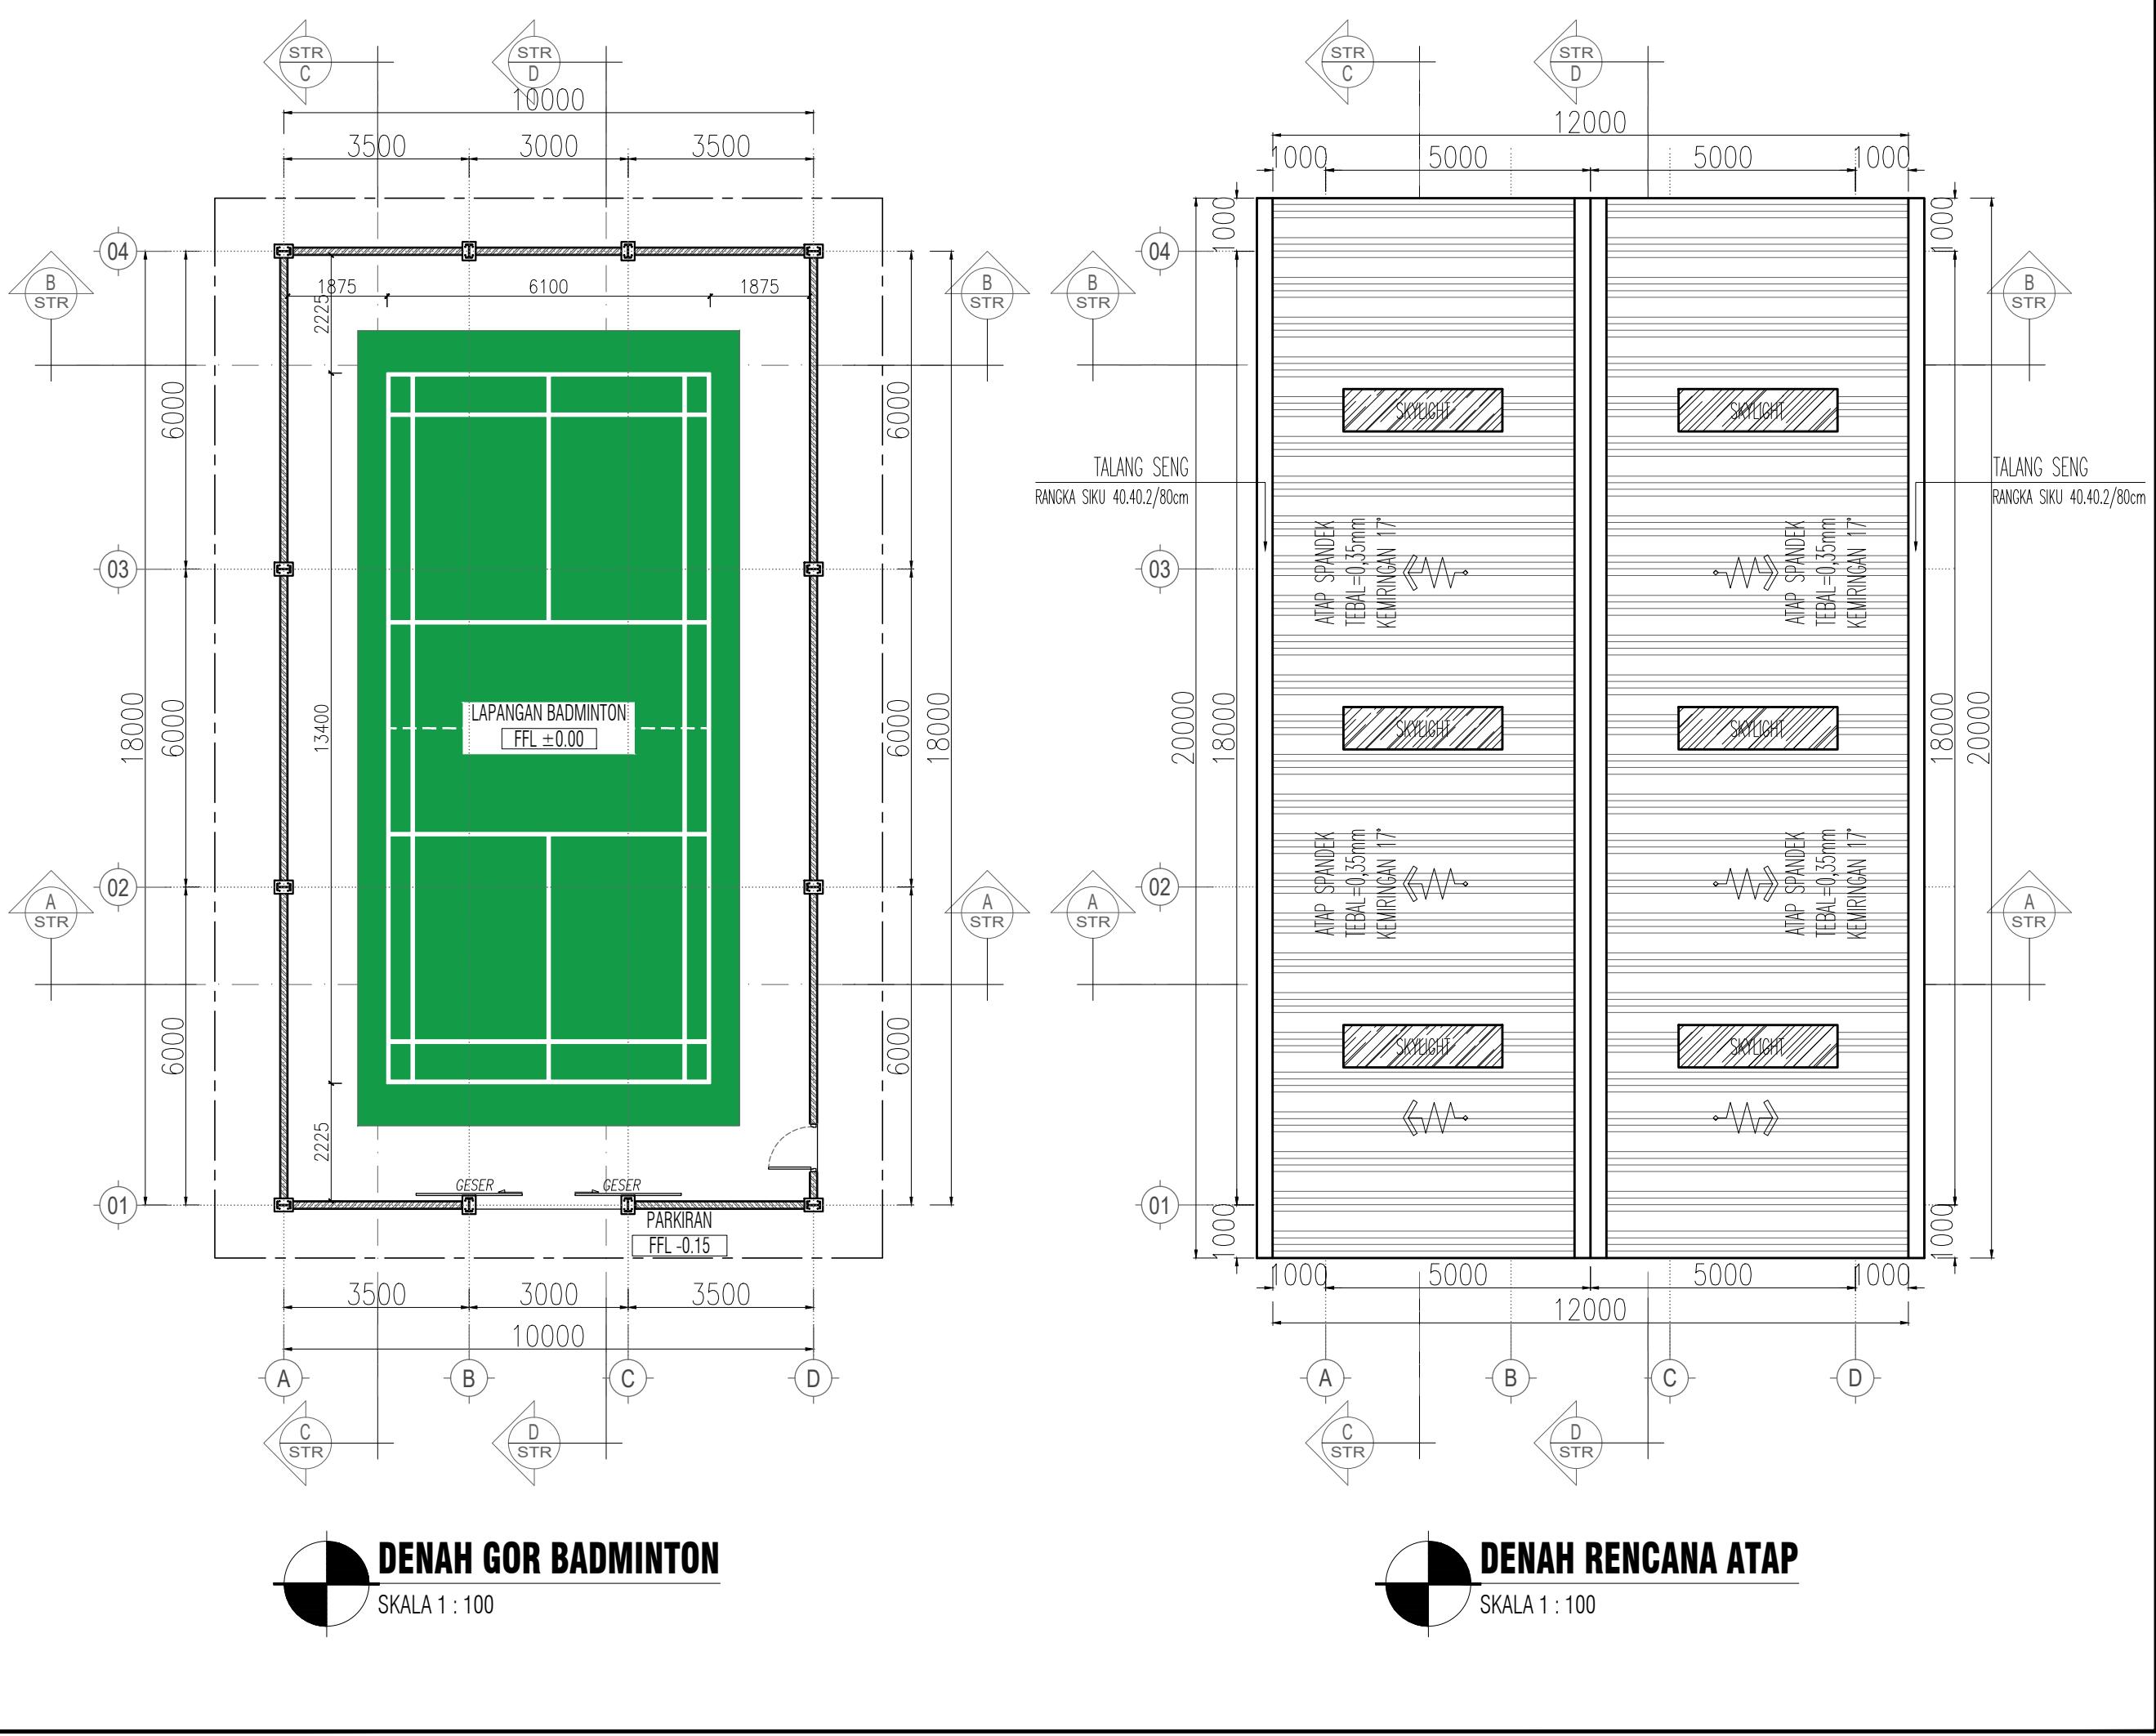


NOK V 0,25

ATAP SPANDEK TEBAL=0,35mm

LISTPLANK SPANDEK TEBAL=0,35mm

RANGKA SIKU 40.40.2/80cm

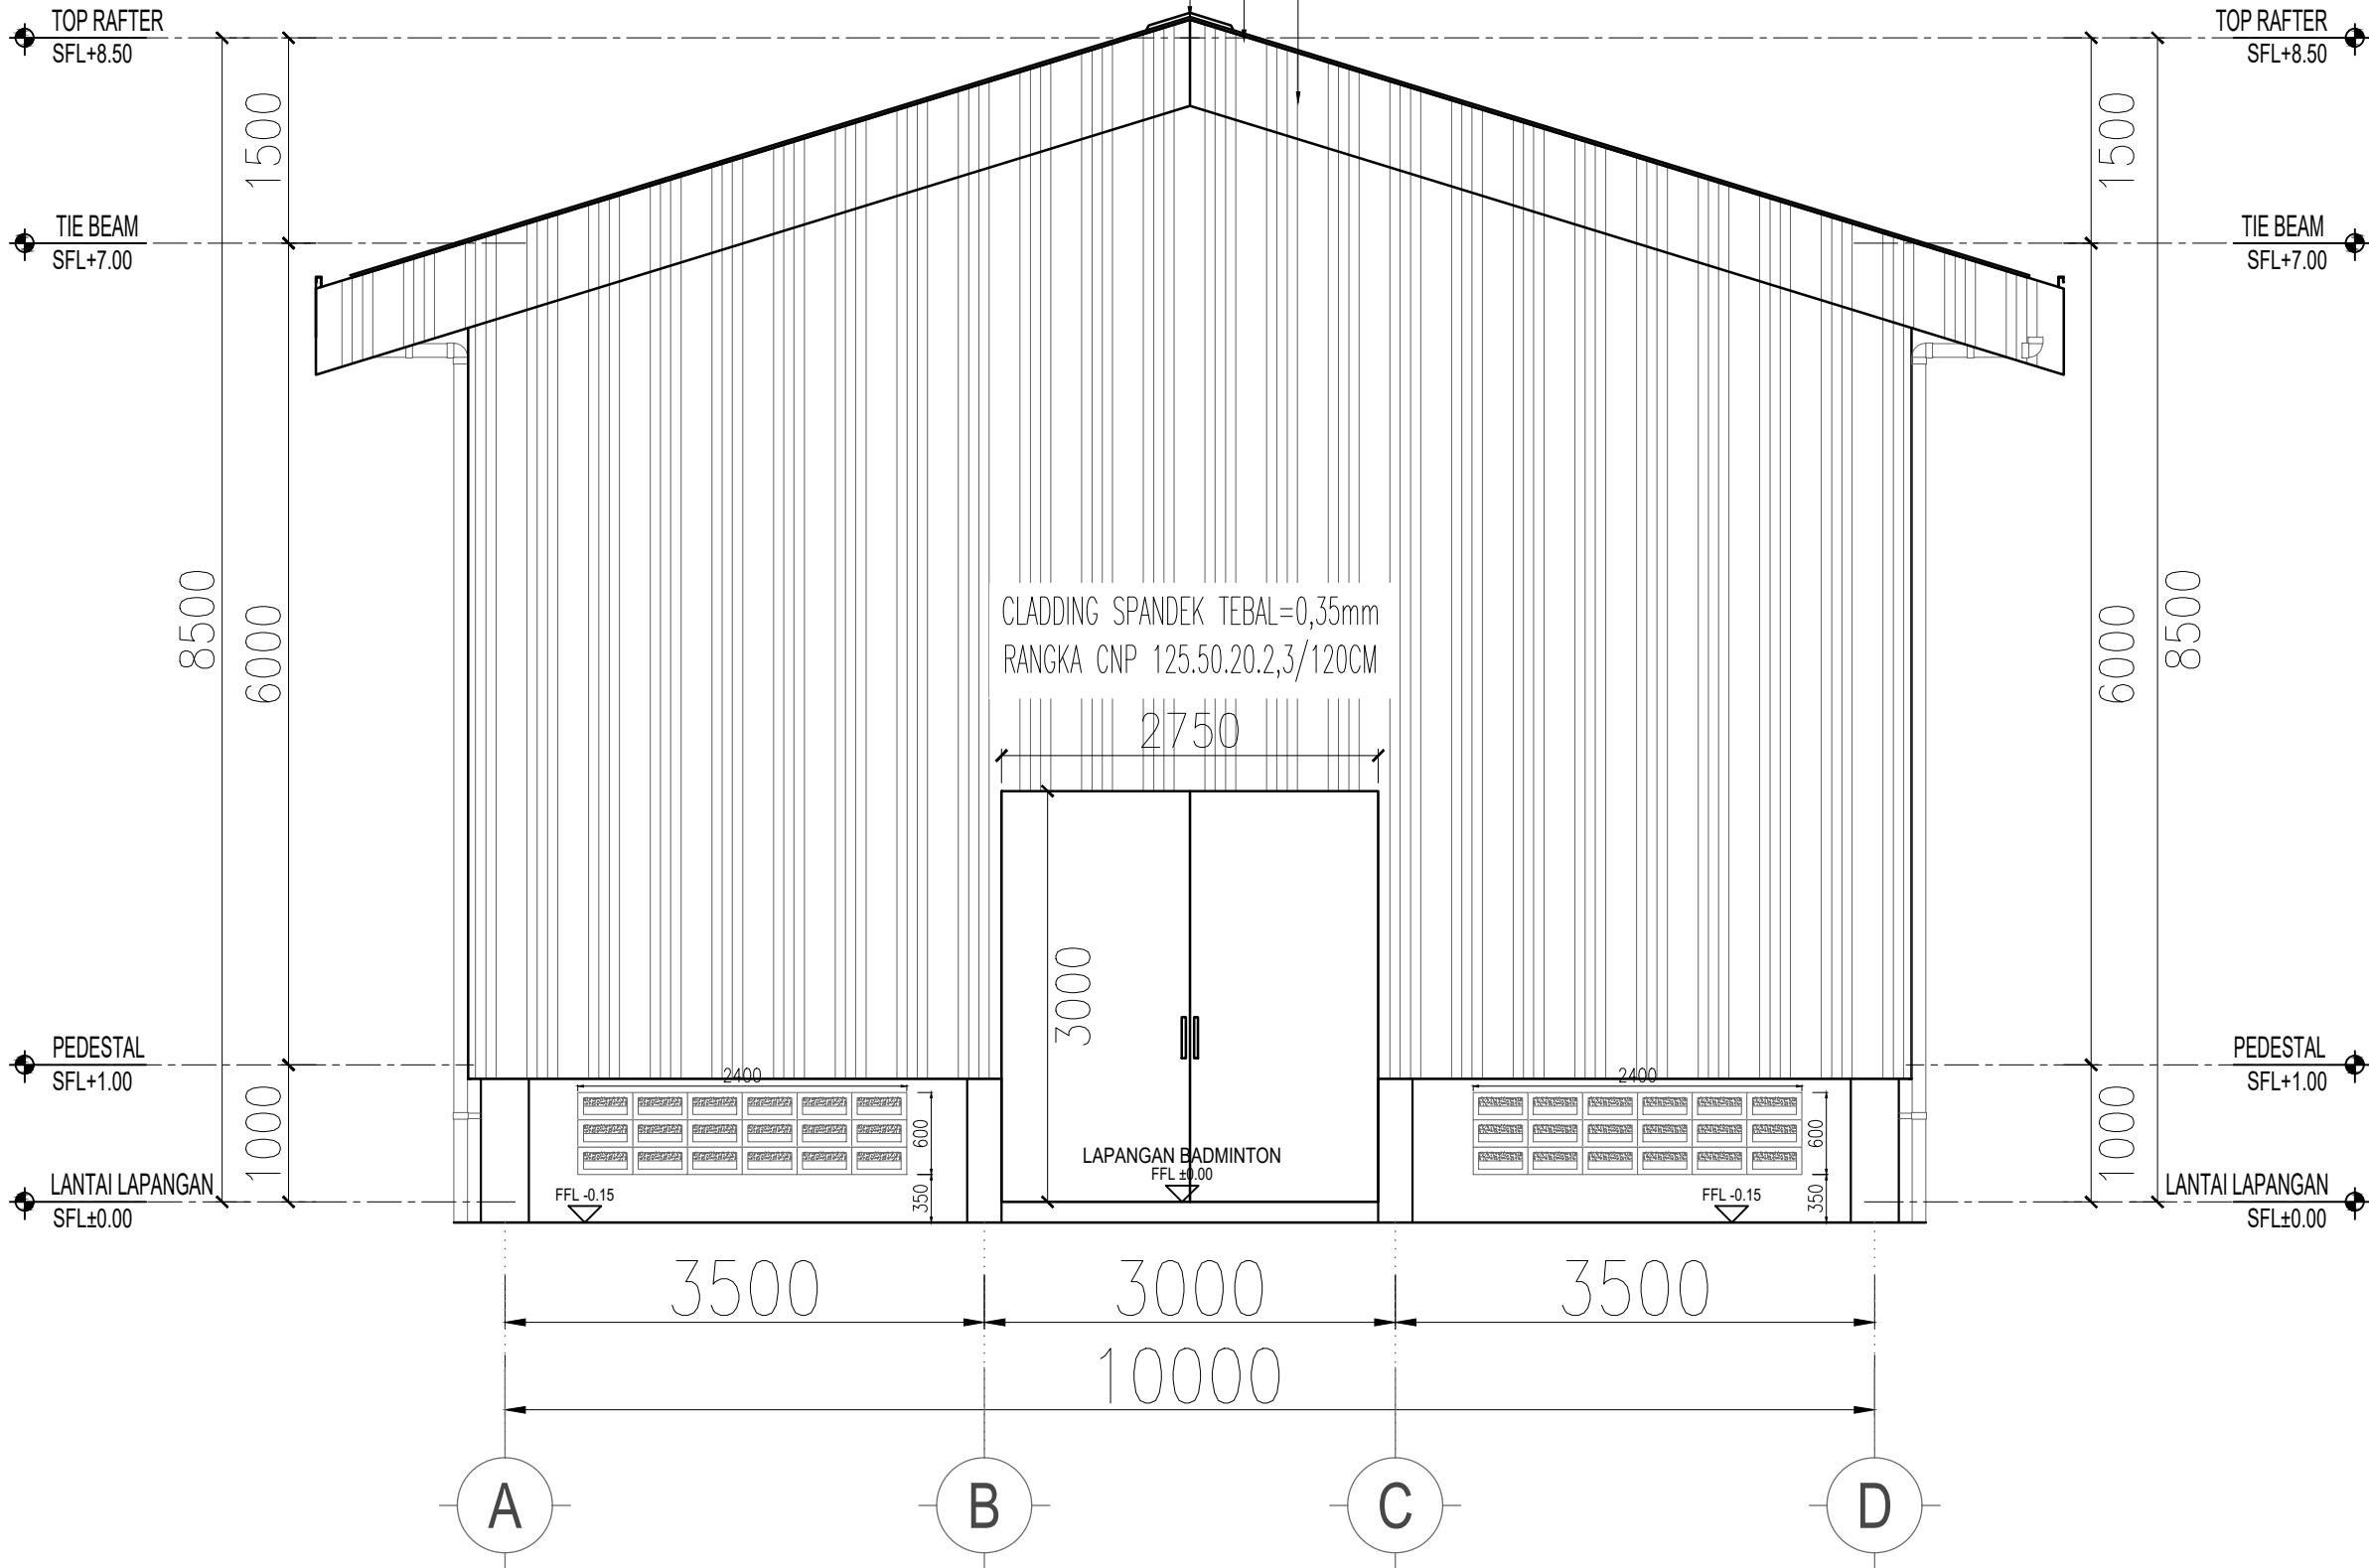

NAMA PROYEK	
-	
LOKASI PROYEK	
-	-
PENANGGUNG JAWAB	
DIGAMBAR	PELAKSANA
DISETUVUT	PEMILIK
CATATAN	
1. PELAKSANA ATAU SUBKON WAJIB MEMERIKSA KEMBALI KESESUAIN GAMBAR DENGAN KONDISI LAPANGAN	
-	
JUDUL GAMBAR	SKALA
1.TAMPAK DEPAN	1 : 40
TANGGAL :	REVISI :
5 APRIL 2024	R3
KODE GAMBAR	
ARS-02-03	
NO. LBR	JUMLAH LBR
03	35

TAMPAK DEPAN


SKALA 1 : 40

NOK V 0,25

ATAP SPANDEK TEBAL=0,35mm

LISTPLANK SPANDEK TEBAL=0,35mm

RANGKA SIKU 40.40.2/80cm

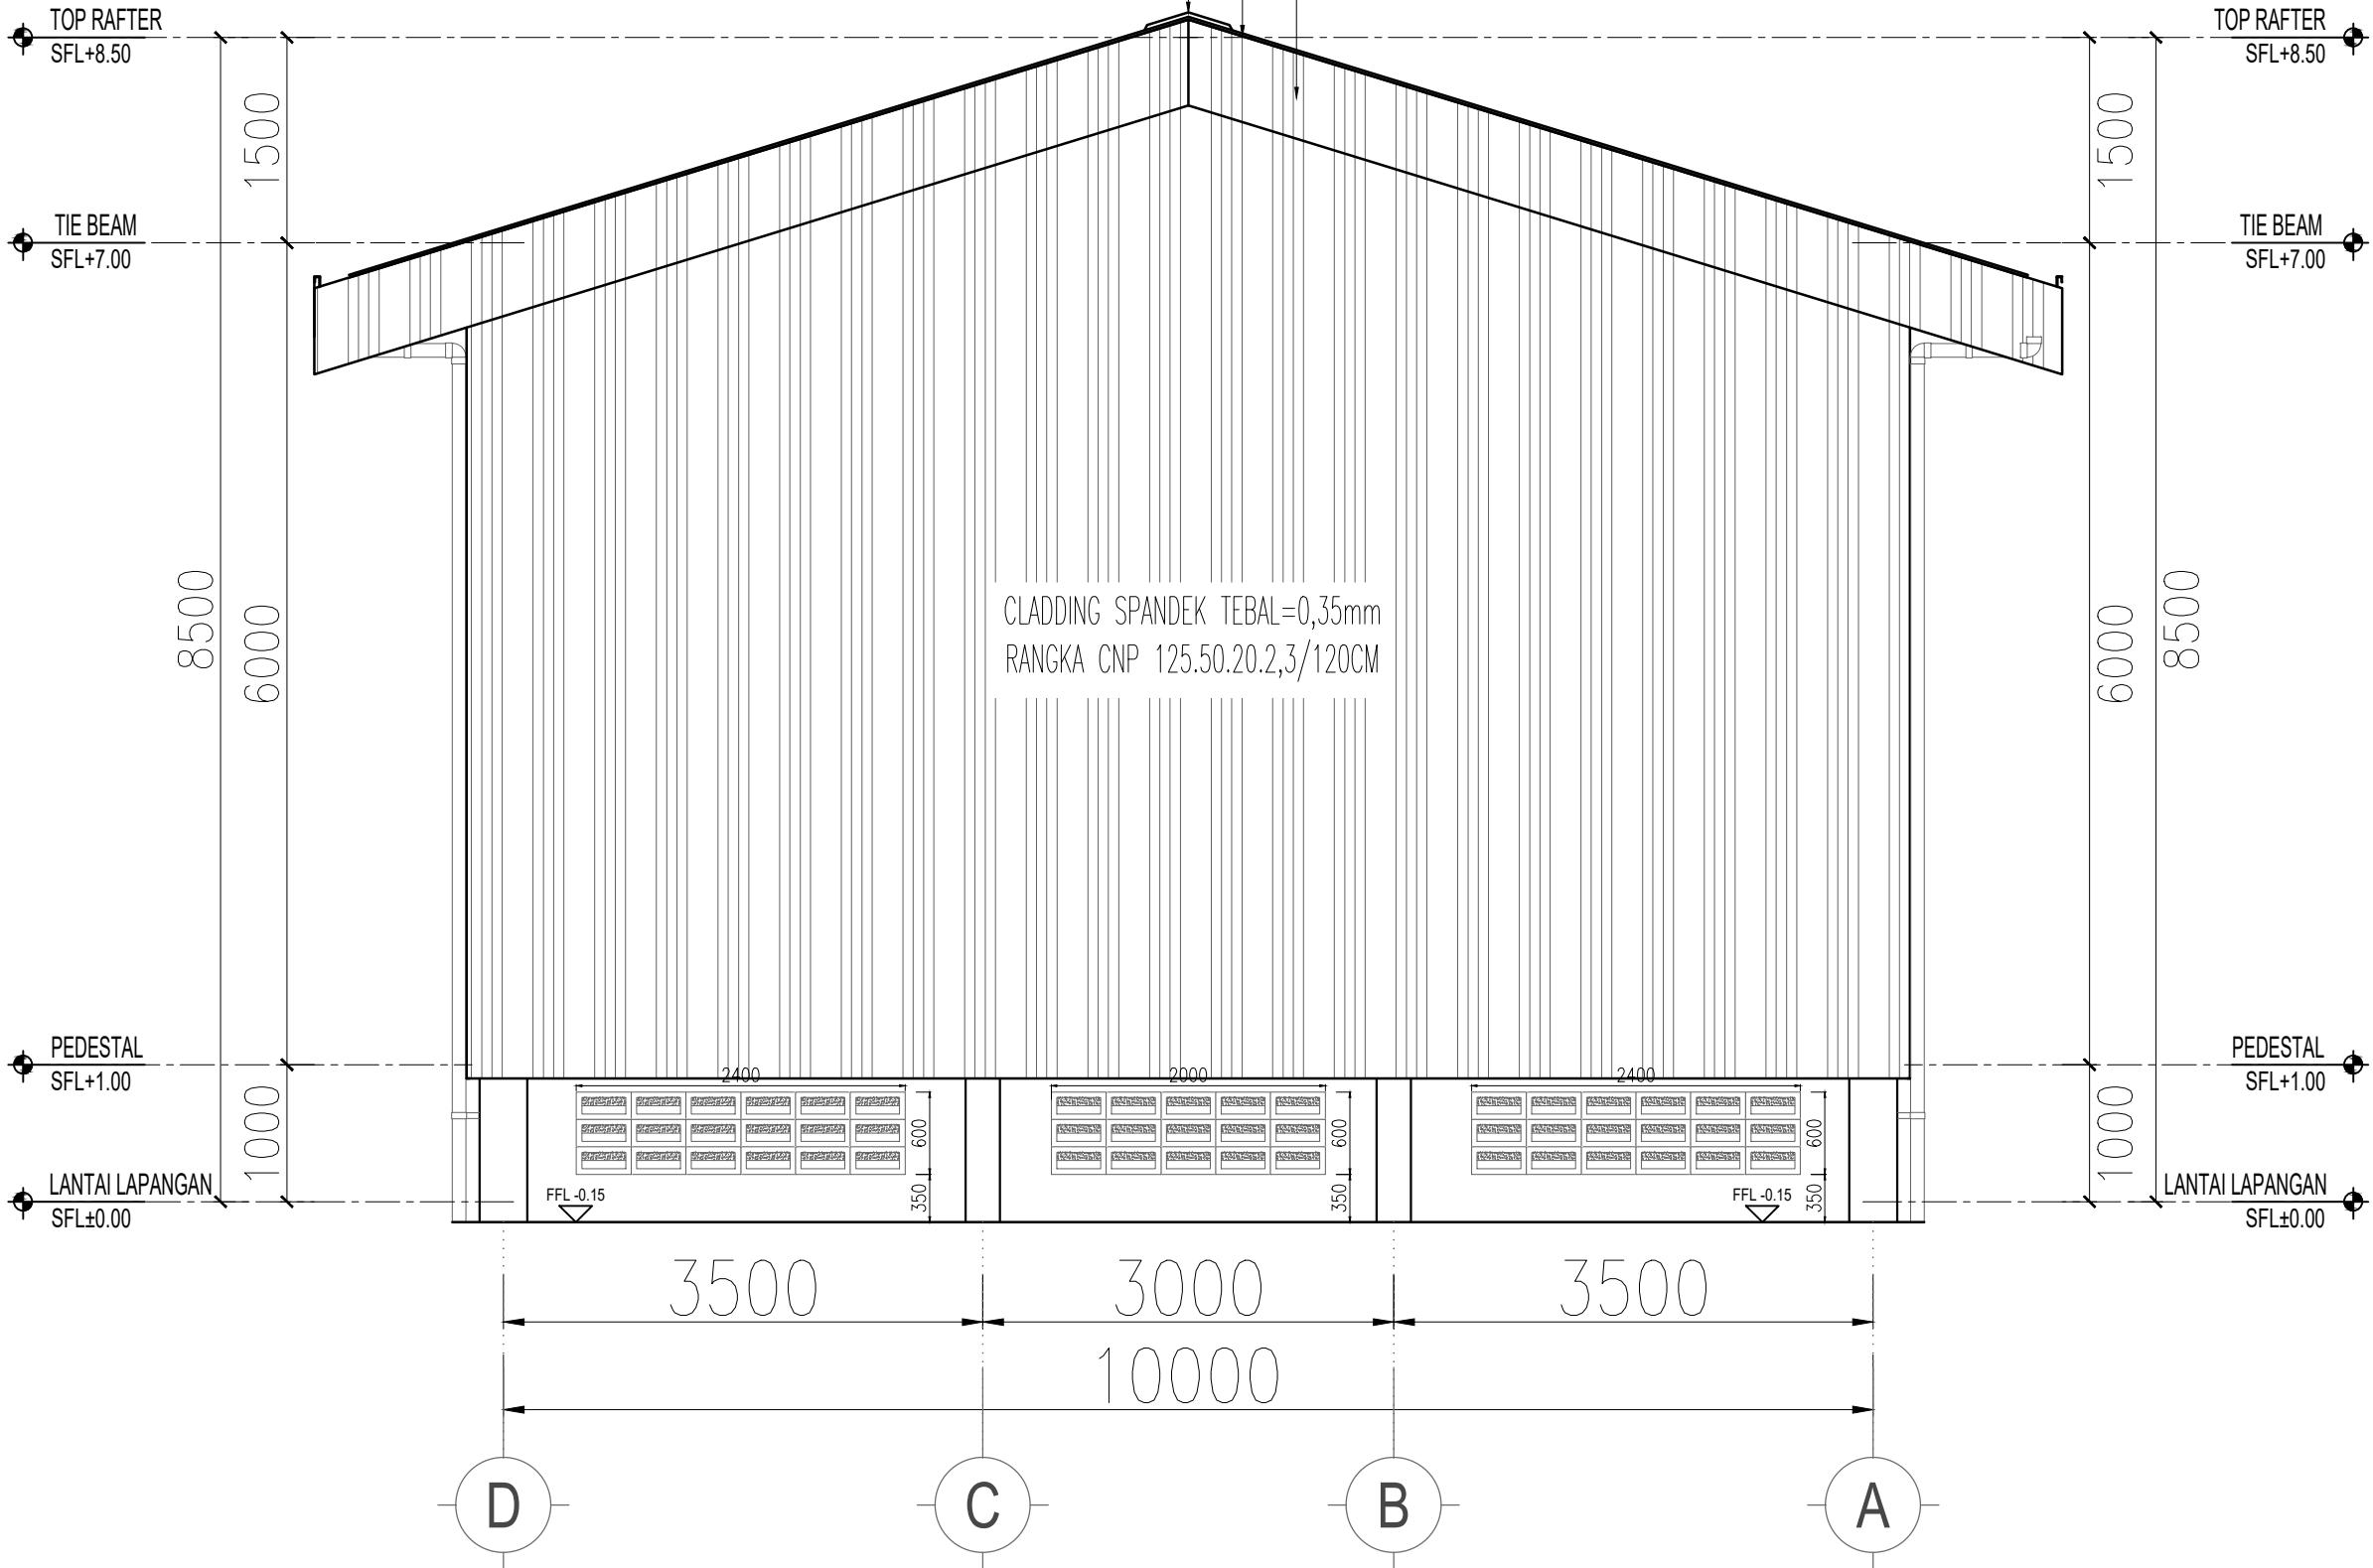


TAMPAK BELAKANG

SKALA 1 : 40

NAMA PROYEK	
-	
LOKASI PROYEK	
-	-
PENANGGUNG JAWAB	
DIGAMBAR	PELAKSANA
DISETUVUT	PEMILIK
CATATAN	
1. PELAKSANA ATAU SUBKON WAJIB MEMERIKSA KEMBALI KESESUAIN GAMBAR DENGAN KONDISI LAPANGAN	
-	
JUDUL GAMBAR	SKALA
1.TAMPAK BELAKANG	1 : 40
TANGGAL :	REVISI :
5 APRIL 2024	R3
KODE GAMBAR	
ARS-02-04	
NO. LBR	JUMLAH LBR
04	35


NAMA PROYEK	
-	
LOKASI PROYEK	
-	
-	
PENANGGUNG JAWAB	
DIGAMBAR	PELAKSANA
DISETUJUI	PEMILIK
CATATAN	
<p>1. PELAKSANA ATAU SUBKON WAJIB MEMERIKSA KEMBALI KESESUAIN GAMBAR DENGAN KONDISI LAPANGAN</p>	
JUDUL GAMBAR	
SKALA	
1.TAMPAK SAMPING KANAN	
1 : 50	
TANGGAL :	
REVISI :	
5 APRIL 2024	
R3	
KODE GAMBAR	
ARS-02-05	
NO. LBR	JUMLAH LBR
05	35

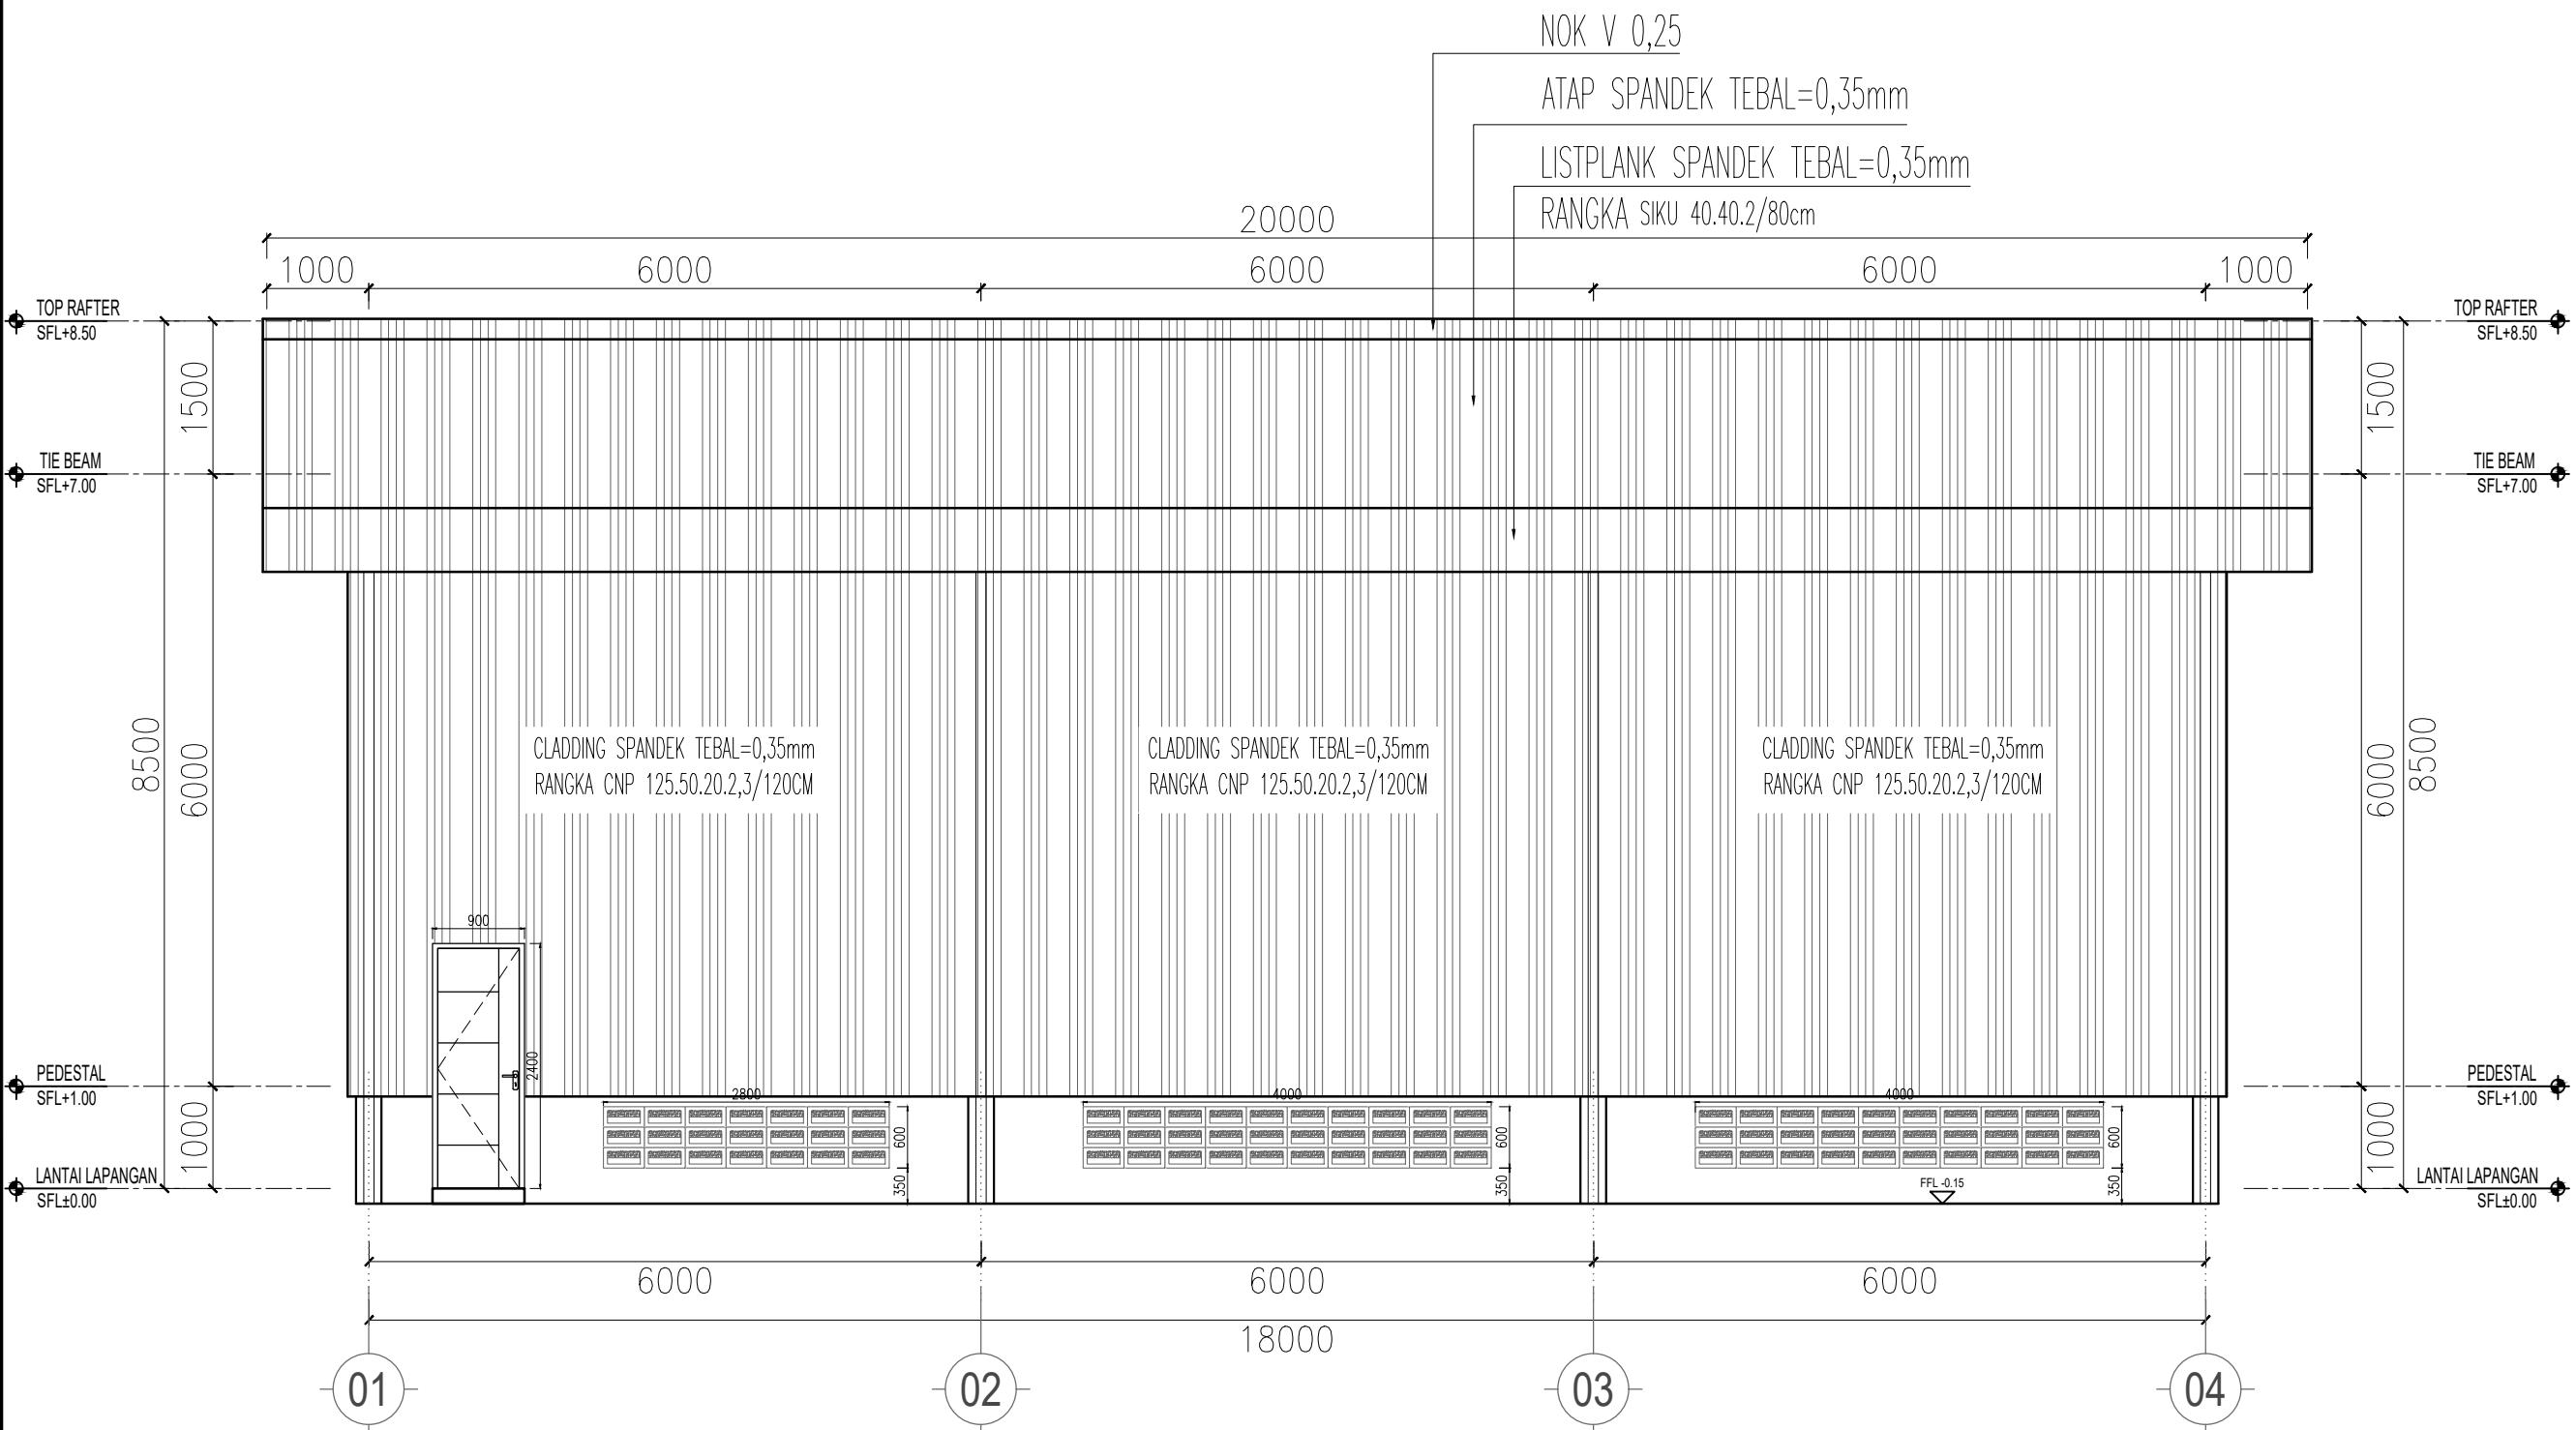

TAMPAK SAMPING KANAN

SKALA 1 : 50


NAMA PROYEK	
-	
LOKASI PROYEK	
-	-
PENANGGUNG JAWAB	
-	-
DIGAMBAR	PELAKSANA
-	-
DISETUJUI	PEMILIK
-	-
CATATAN	
1. PELAKSANA ATAU SUBKON WAJIB MEMERIKSA KEMBALI KESESUAIN GAMBAR DENGAN KONDISI LAPANGAN	
-	
JUDUL GAMBAR	SKALA
1.TAMPAK SAMPING KIRI	1 : 50
TANGGAL :	REVISI :
5 APRIL 2024	R3
KODE GAMBAR	
ARS-02-06	
NO. LBR	JUMLAH LBR
06	35

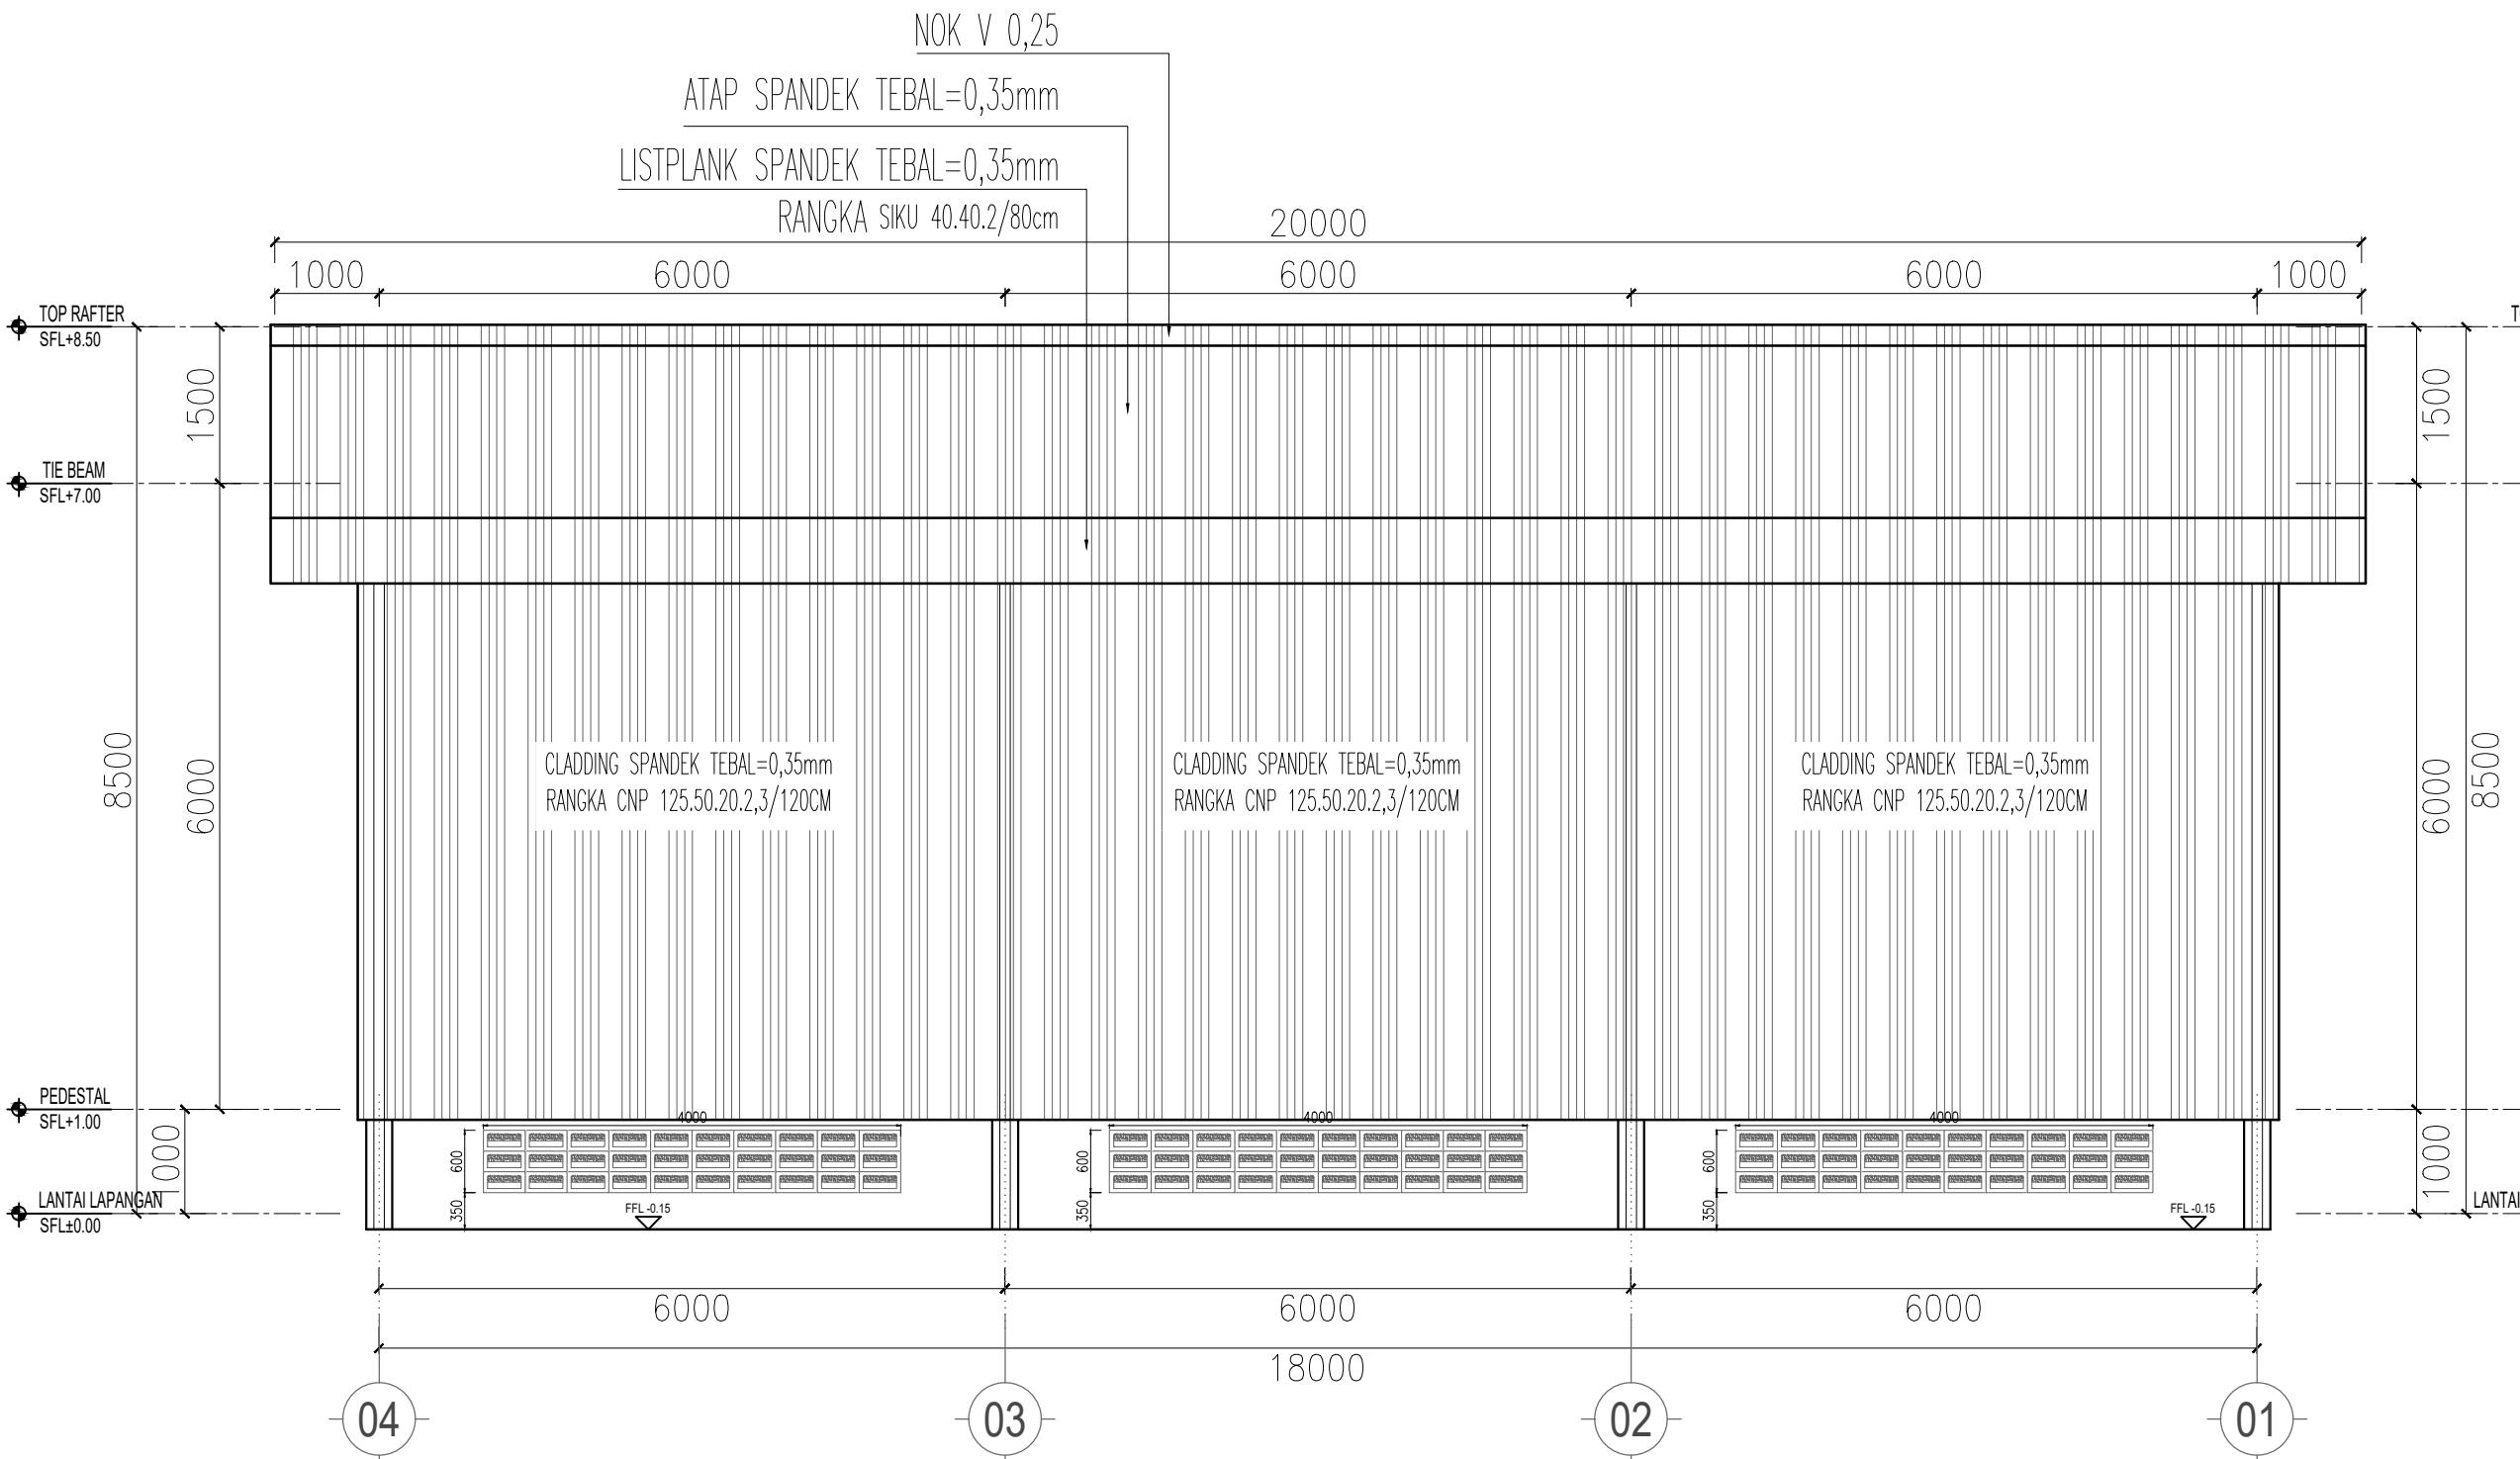


TAMPAK SAMPING KIRI


SKALA 1 : 50

NAMA PROYEK	
-	
LOKASI PROYEK	
-	-
PENANGGUNG JAWAB	
DIGAMBAR	PELAKSANA
DISETUJUI	PEMILIK
CATATAN	
1. PELAKSANA ATAU SUBKON WAJIB MEMERIKSA KEMBALI KESESUAIN GAMBAR DENGAN KONDISI LAPANGAN	
-	
JUDUL GAMBAR	SKALA
1.POTONGAN A-A	1 : 50
TANGGAL :	REVISI :
5 APRIL 2024	R3
KODE GAMBAR	
ARS-02-07	
NO. LBR	JUMLAH LBR
07	35

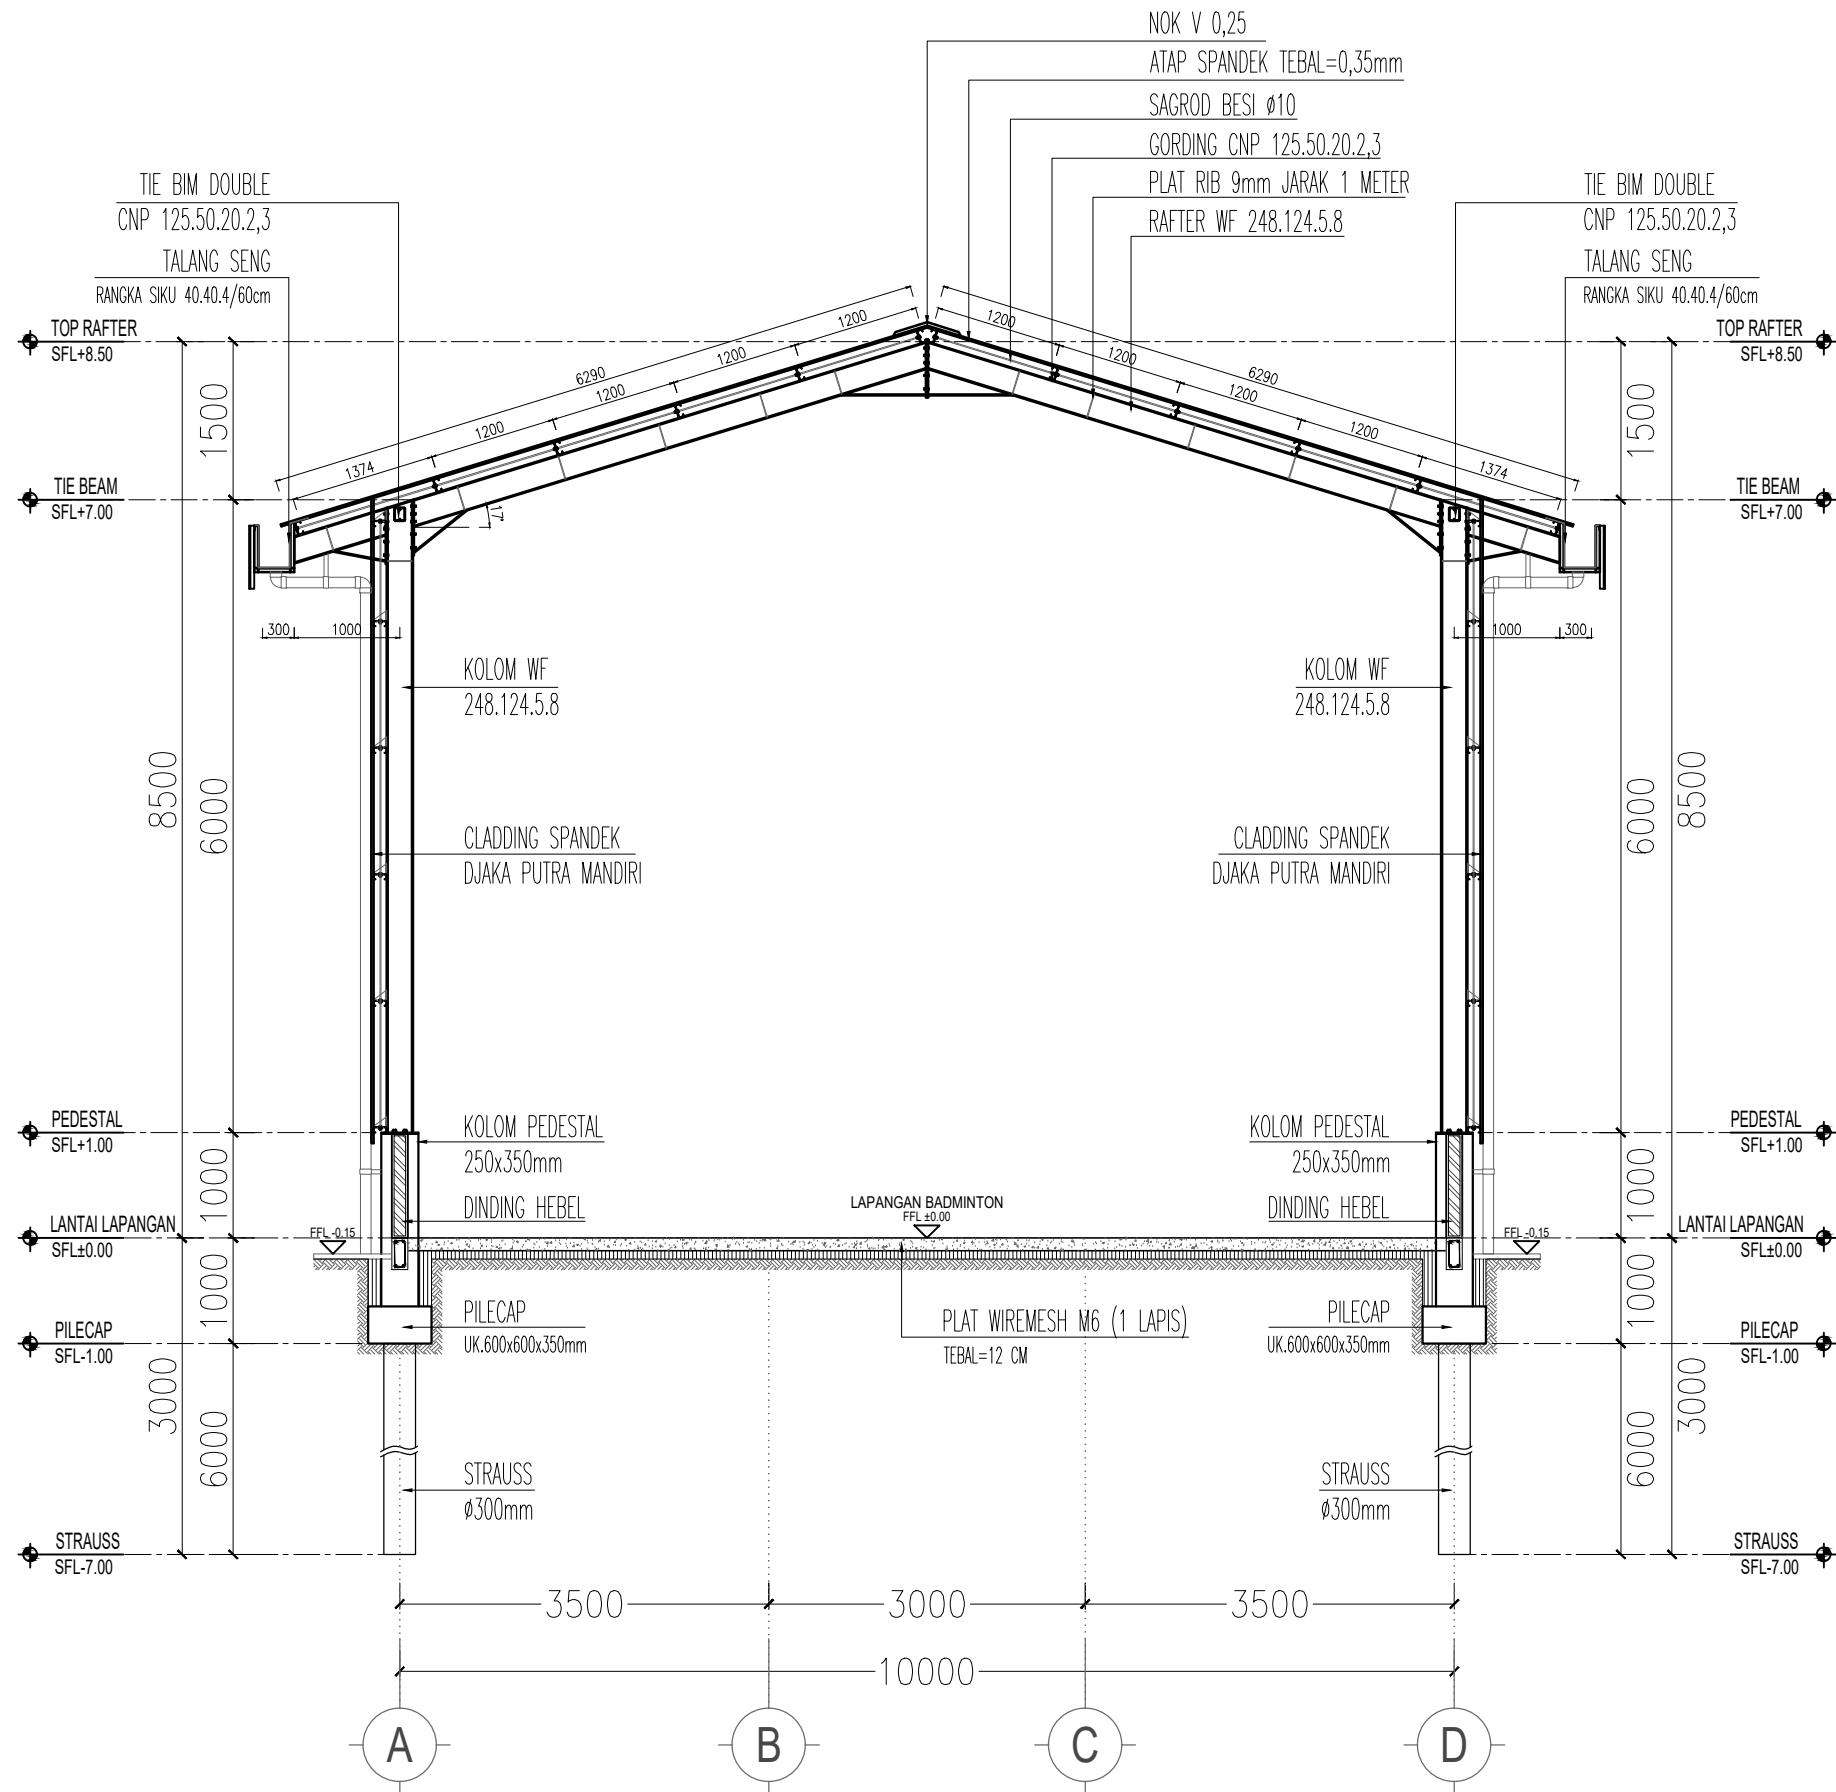


NAMA PROYEK	
-	
LOKASI PROYEK	
-	-
PENANGGUNG JAWAB	
DIGAMBAR	PELAKSANA
DISETUJUI	PEMILIK
CATATAN	
1. PELAKSANA ATAU SUBKON WAJIB MEMERIKSA KEMBALI KESESUAIN GAMBAR DENGAN KONDISI LAPANGAN	
JUDUL GAMBAR	SKALA
1.POTONGAN B-B	1 : 50
TANGGAL :	REVISI :
5 APRIL 2024	R3
KODE GAMBAR	
ARS-02-08	
NO. LBR	JUMLAH LBR
08	35

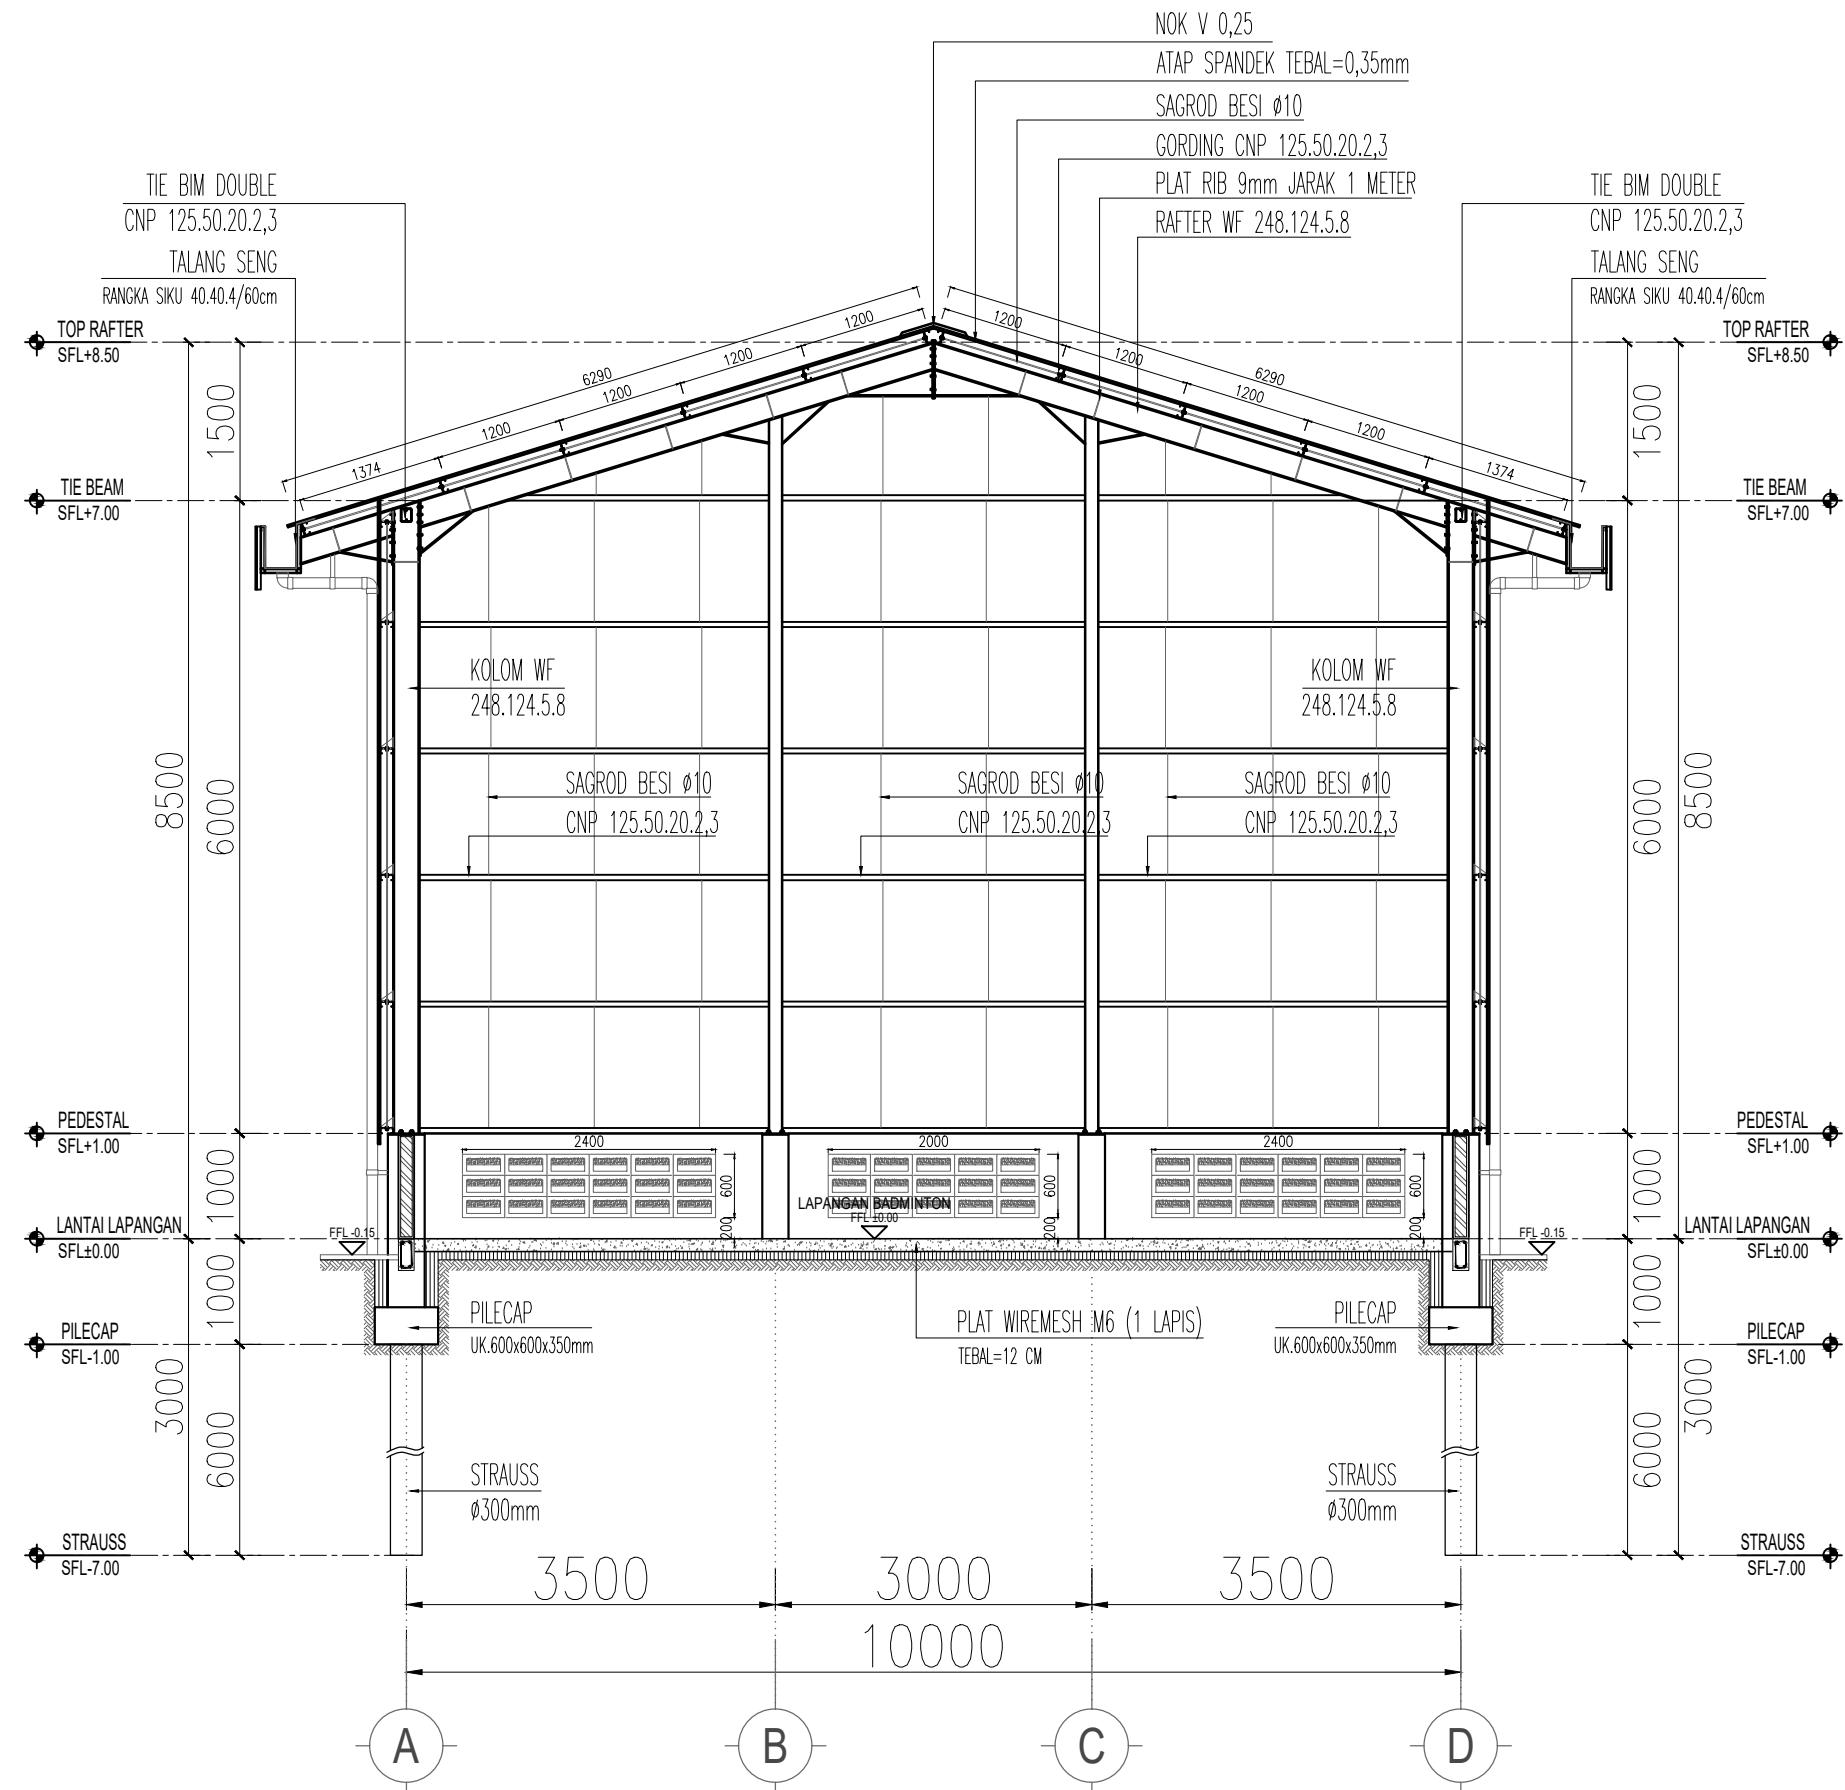


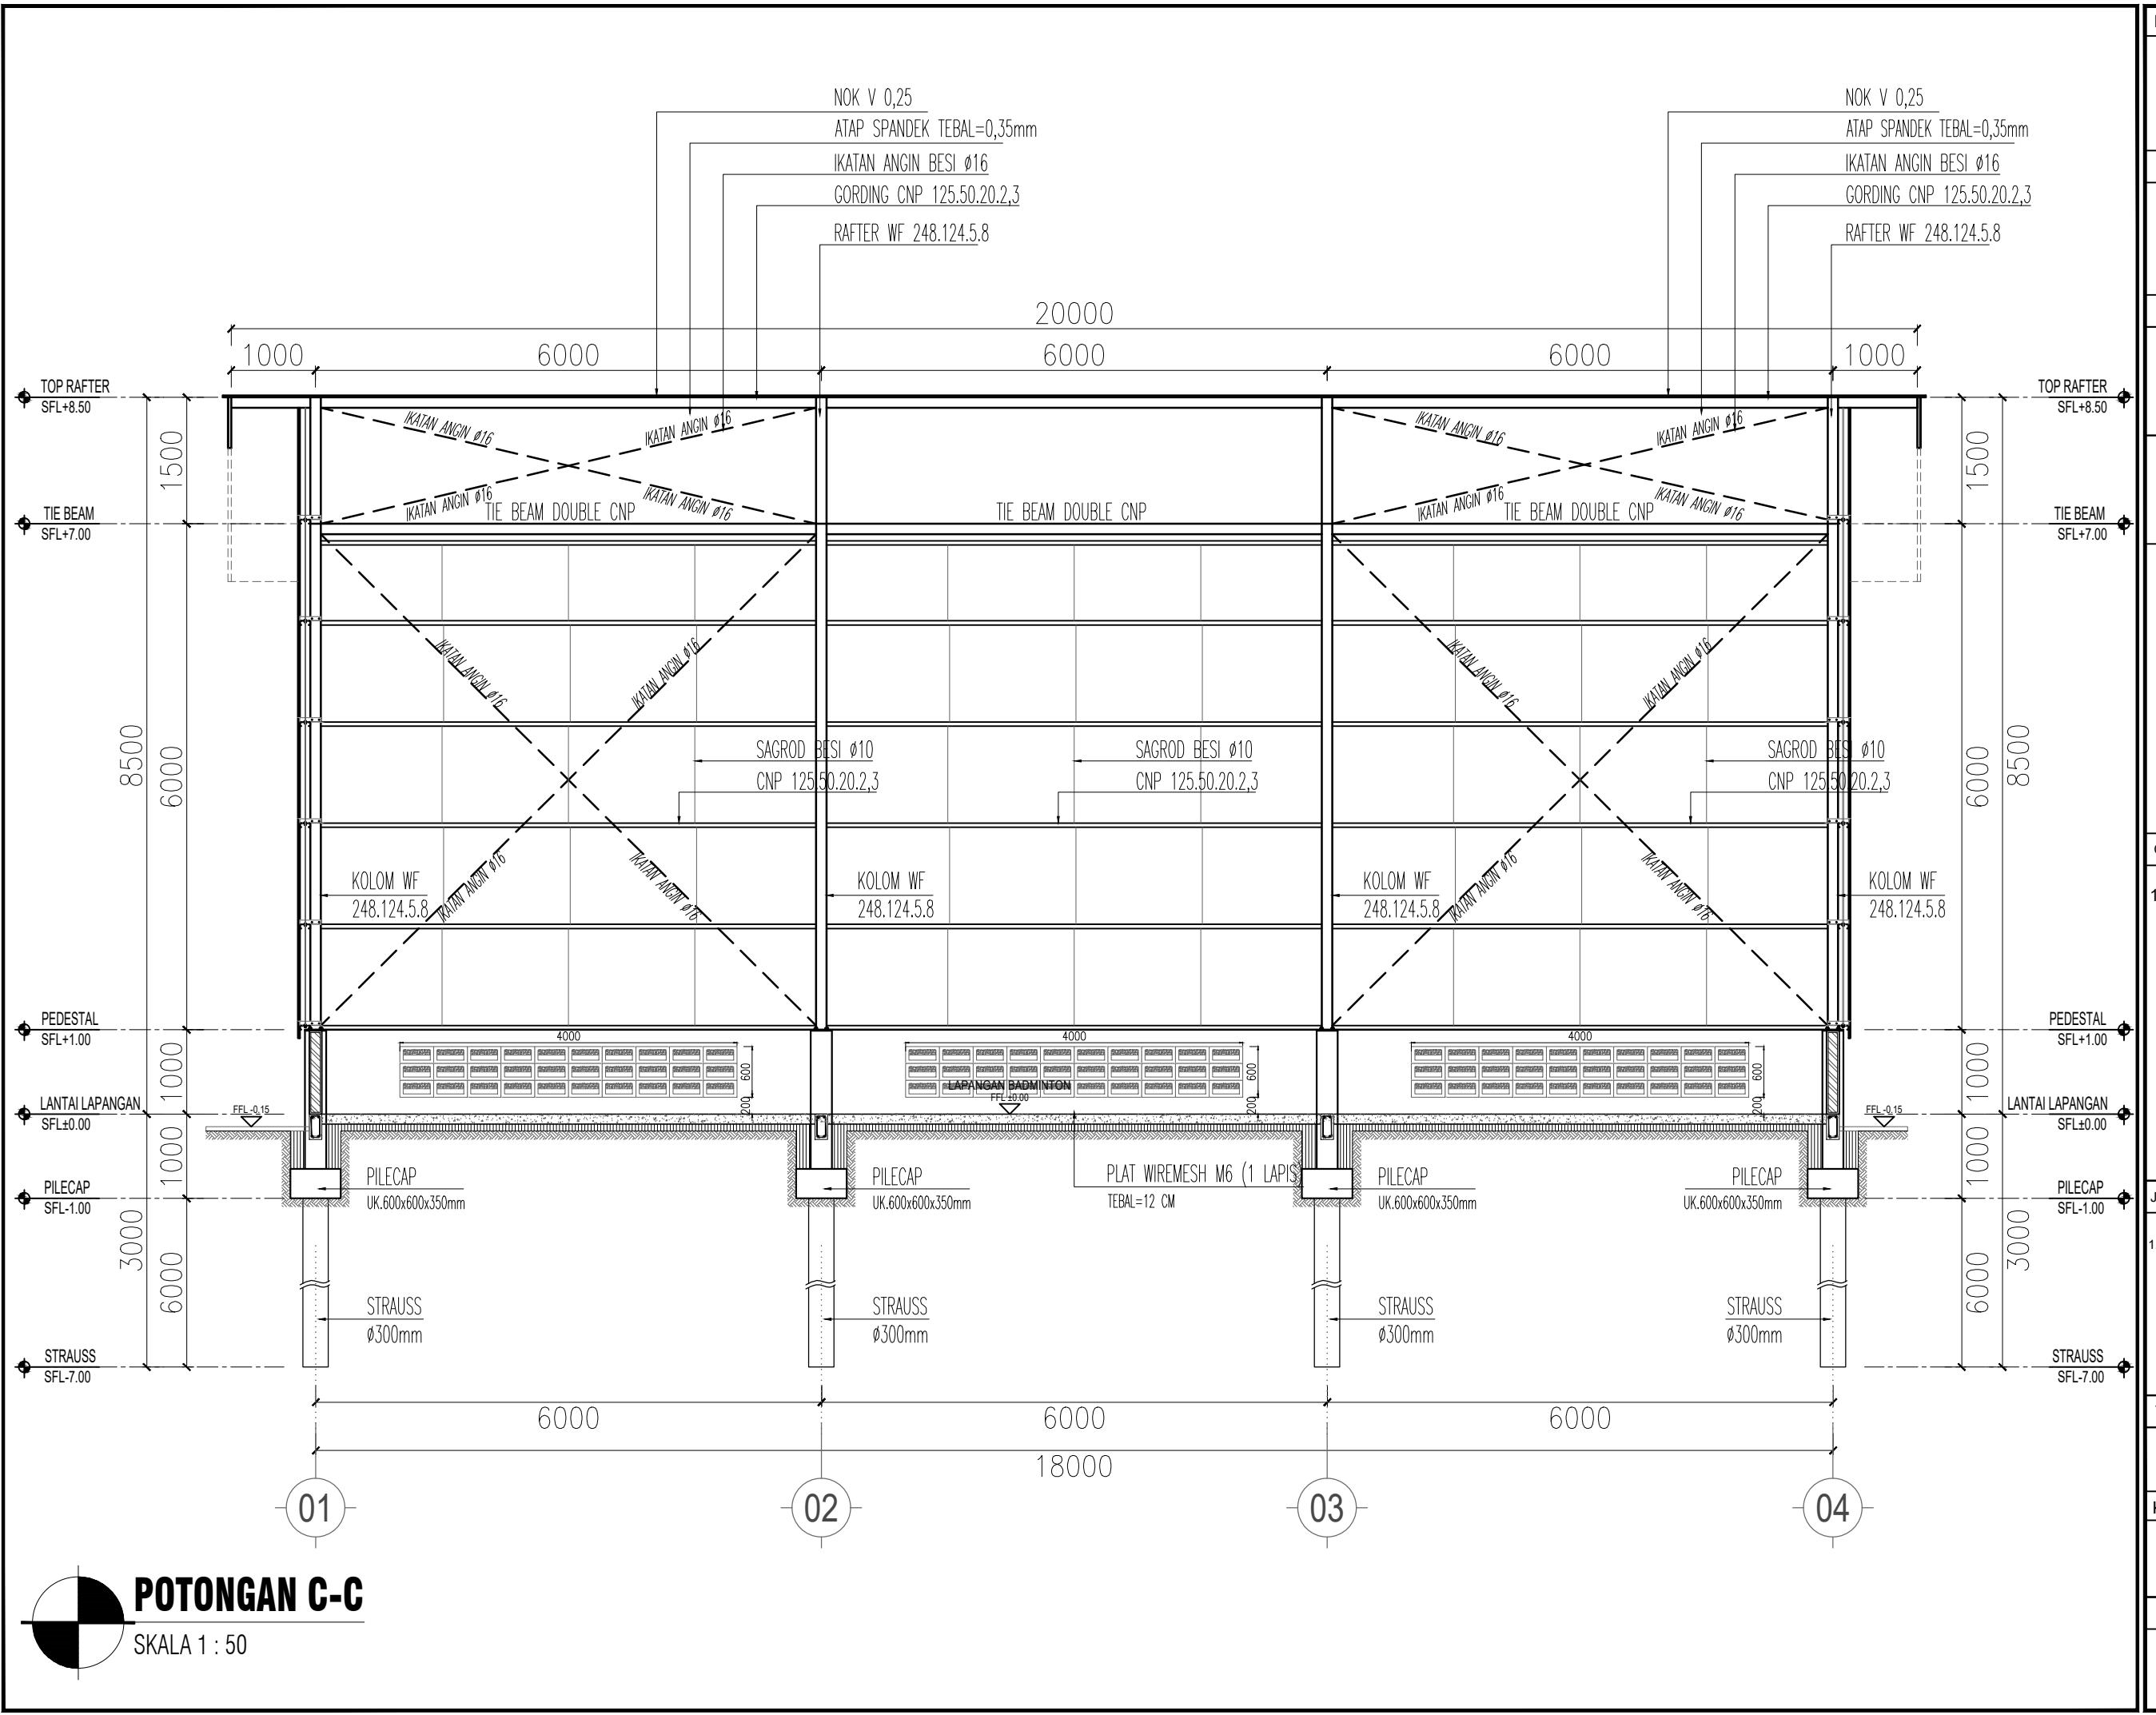


NAMA PROYEK	
LOKASI PROYEK	
PENANGGUNG JAWAB	
DIGAMBAR	PELAKSANA
DISETUJUI	PEMILIK
CATATAN	
1. PELAKSANA ATAU SUBKON WAJIB MEMERIKSA KEMBALI KESESUAIN GAMBAR DENGAN KONDISI LAPANGAN	
UDUL GAMBAR	SKALA
POTONGAN C-C	1 : 50
TANGGAL :	REVISI :
5 APRIL 2024	R3
KODE GAMBAR	
ARS-02-09	
NO. LBR	JUMLAH LBR
09	35

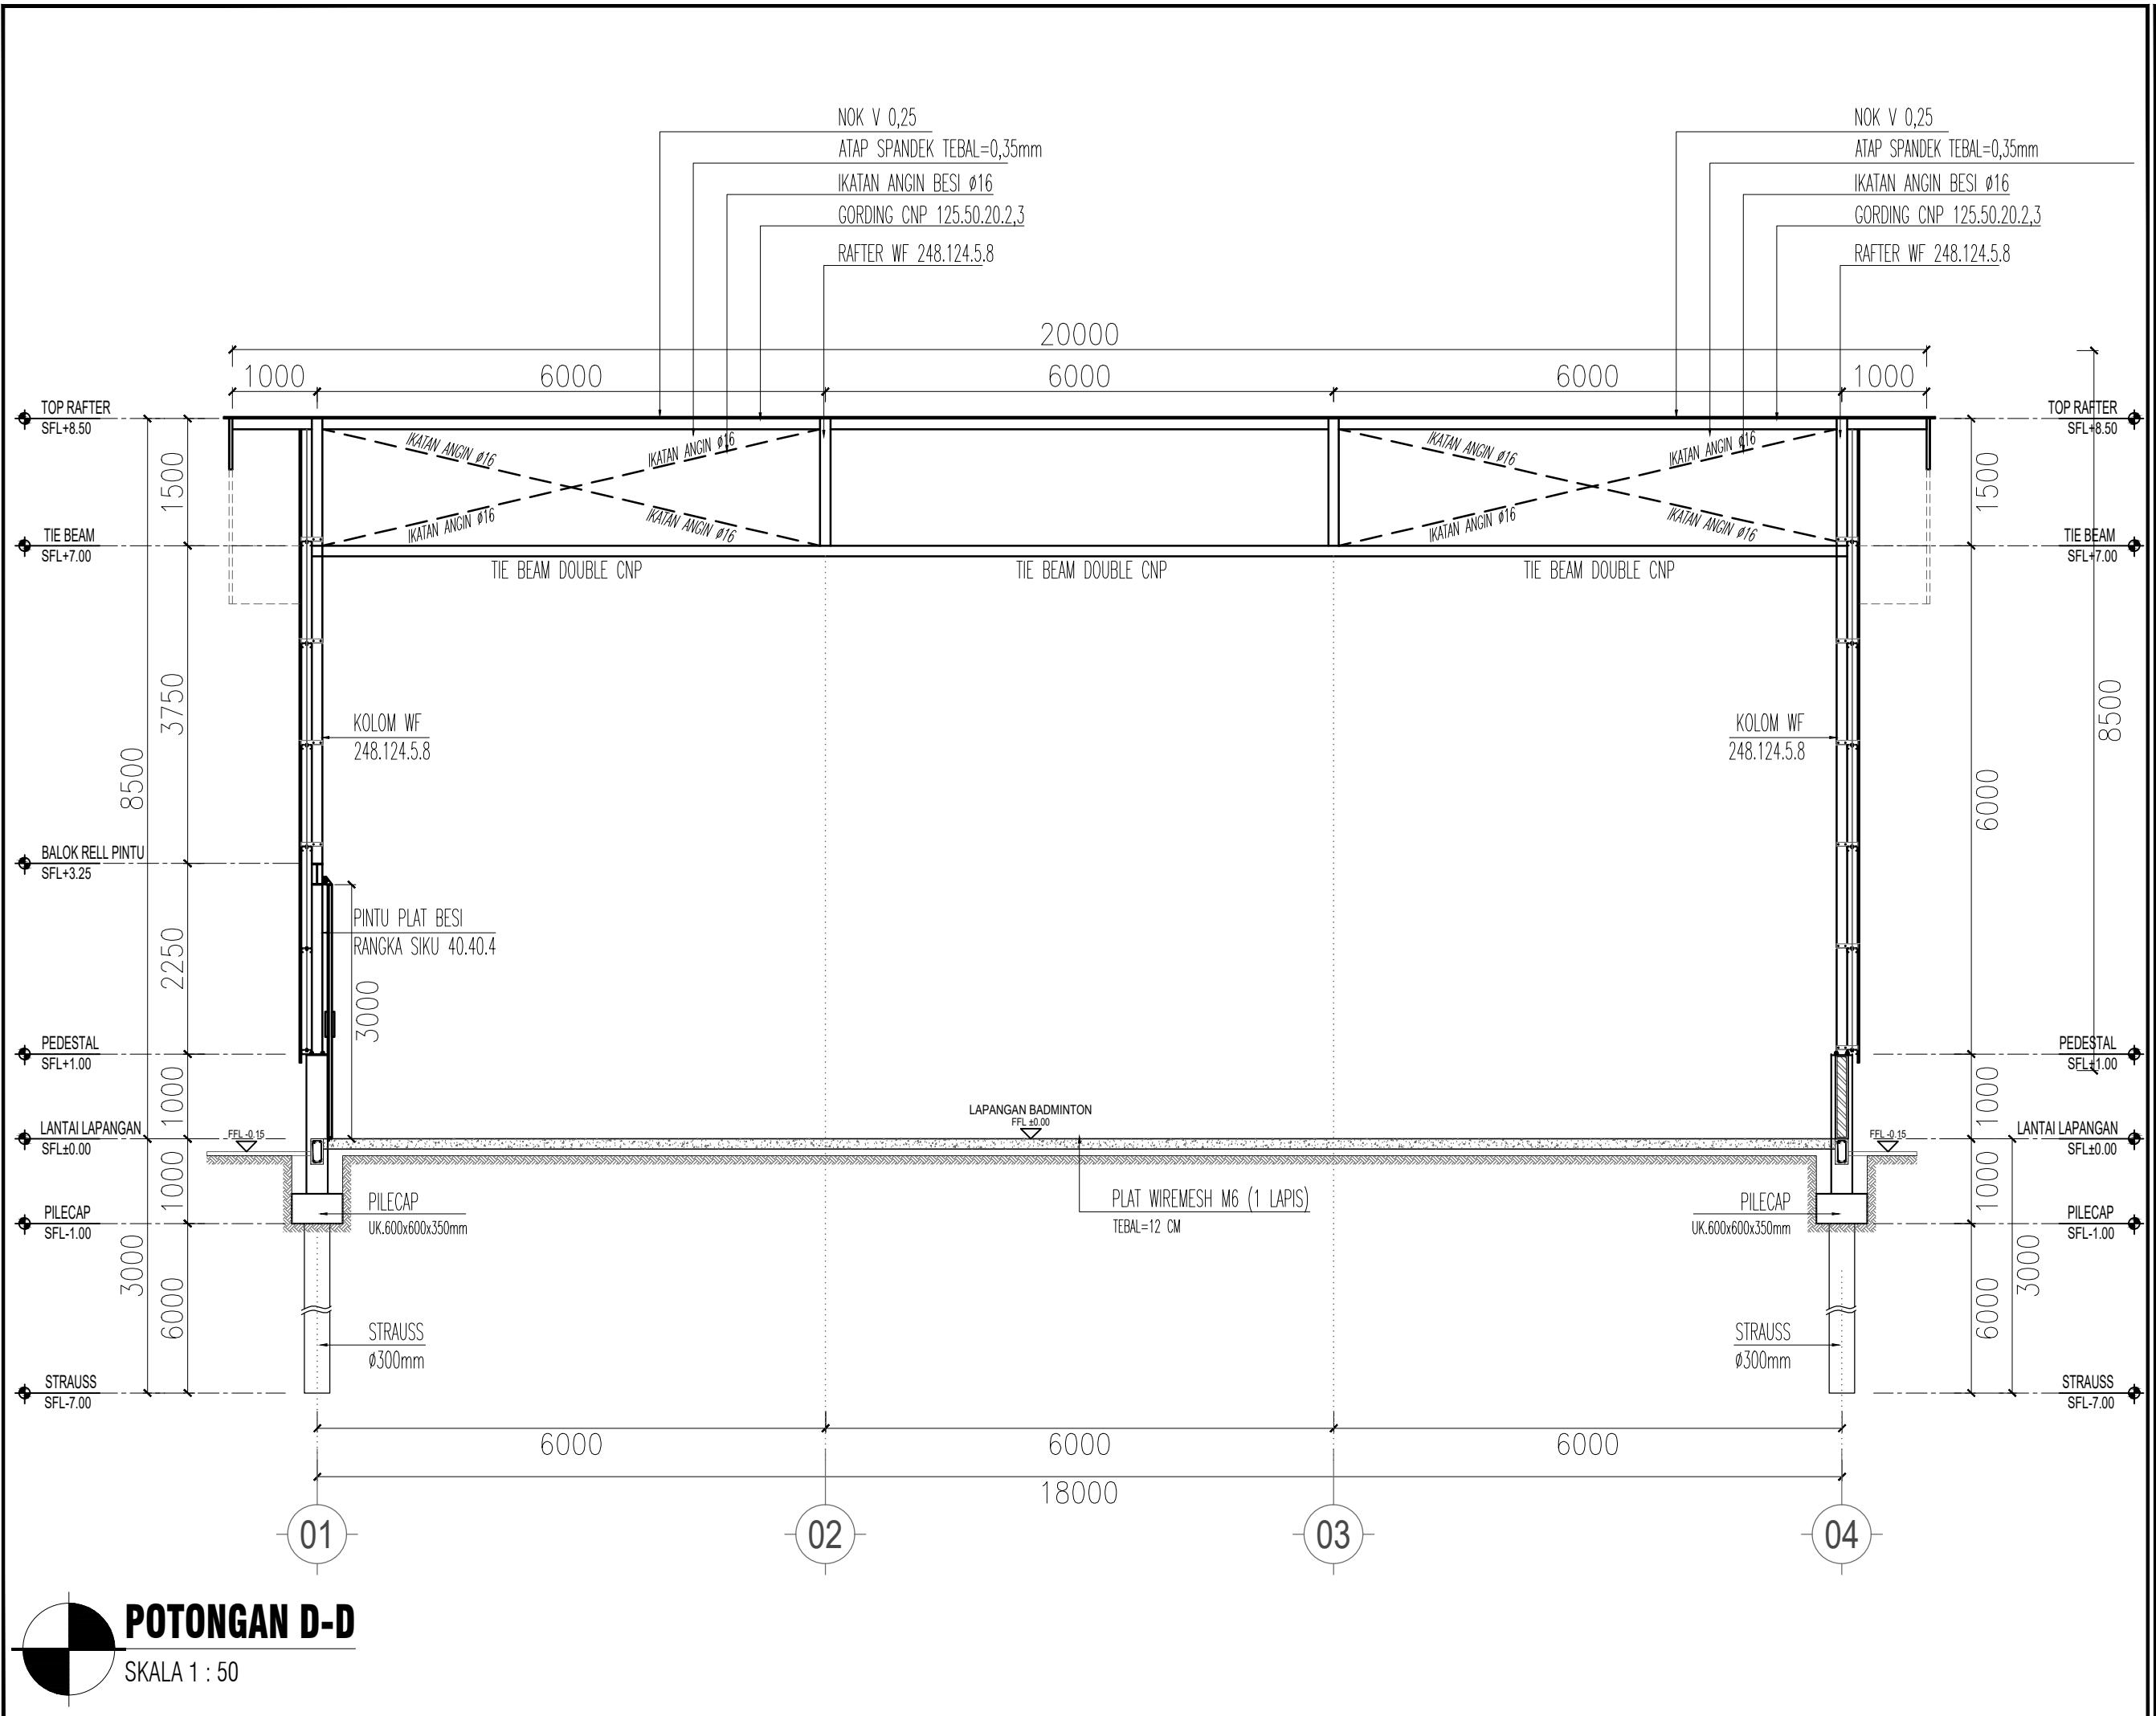

NAMA PROYEK	
LOKASI PROYEK	
PENANGGUNG JAWAB	
<u>DIGAMBAR</u>	<u>PELAKSANA</u>
<u>DISETUJUI</u>	<u>PEMILIK</u>
CATATAN	
1. PELAKSANA ATAU SUBKON WAJIB MEMERIKSA KEMBALI KESESUAIN GAMBAR DENGAN KONDISI LAPANGAN	
JUDUL GAMBAR	SKALA
1.POTONGAN D-D	1 : 50
TANGGAL :	REVISI :
5 APRIL 2024	R3
KODE GAMBAR	
ARS-02-10	
NO. LBR	JUMLAH LBR
10	35

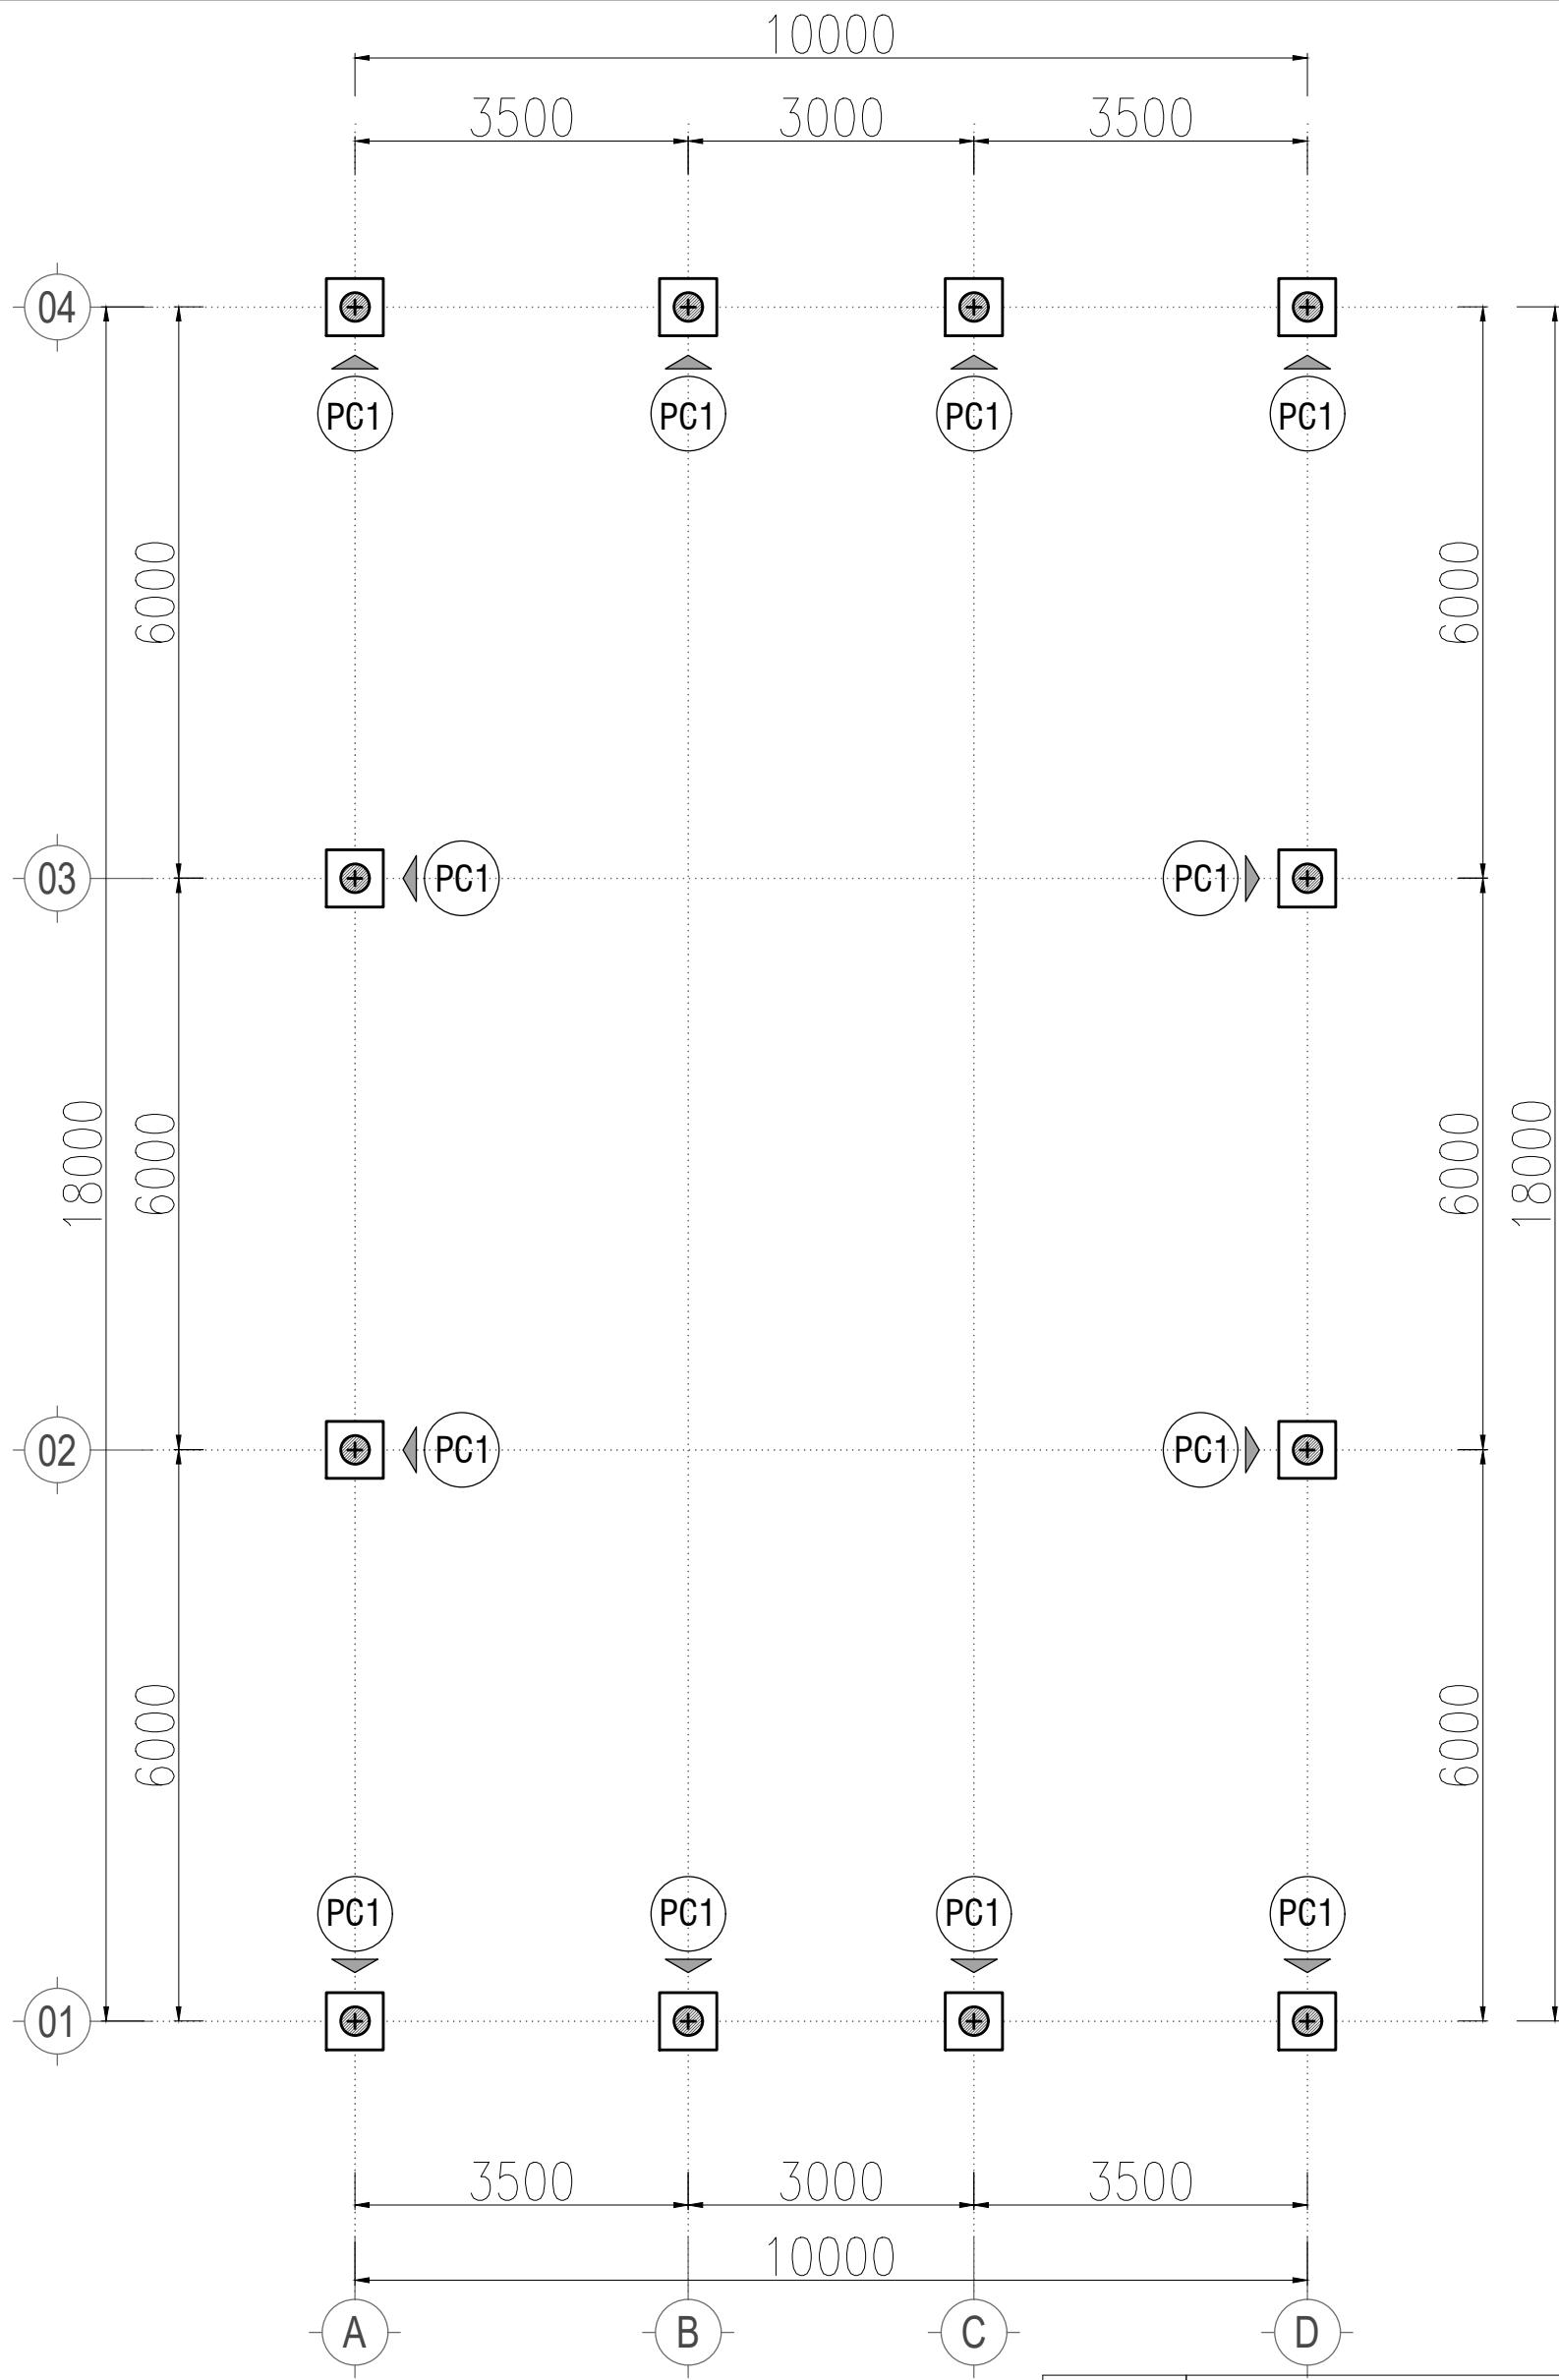

NOTASI	KETERANGAN JENIS PONDASI	JUMLAH
(PC1)	PILECAP UK.600x600x300mm + STRAUSS Ø300 DALAM 6m	12

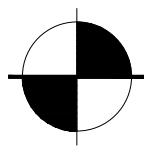

DENAH PILECAP SFL-1.00 (ELEVASI BOTTOM)


SKALA 1 : 100


CATATAN
1. PELAKSANA ATAU SUBKON WAJIB
MEMERIKSA KEMBALI KESESUAIN
GAMBAR DENGAN KONDISI
LAPANGAN

JUDUL GAMBAR	SKALA
1.DENAH PILECAP SFL-1.00 (ELEVASI BOTTOM)	1 : 100

NAMA PROYEK	LOKASI PROYEK	PENANGGUNG JAWAB
-	-	-
-	-	-
-	-	-
-	-	-
STR-03-11	REVISI :	
5 APRIL 2024	R3	
KODE GAMBAR		
NO. LBR	JUMLAH LBR	
11	35	

NAMA PROYEK	
-	
LOKASI PROYEK	
-	-
PENANGGUNG JAWAB	
DIGAMBAR	PELAKSANA
DISETUJUI	PEMILIK
CATATAN	
1. PELAKSANA ATAU SUBKON WAJIB MEMERIKSA KEMBALI KESESUAIN GAMBAR DENGAN KONDISI LAPANGAN	
JUDUL GAMBAR	SKALA
1.DETAIL PONDASI PC1	1 : 25
TANGGAL :	REVISI :
5 APRIL 2024	R3
KODE GAMBAR	
STR-03-12	
NO. LBR	JUMLAH LBR
12	35

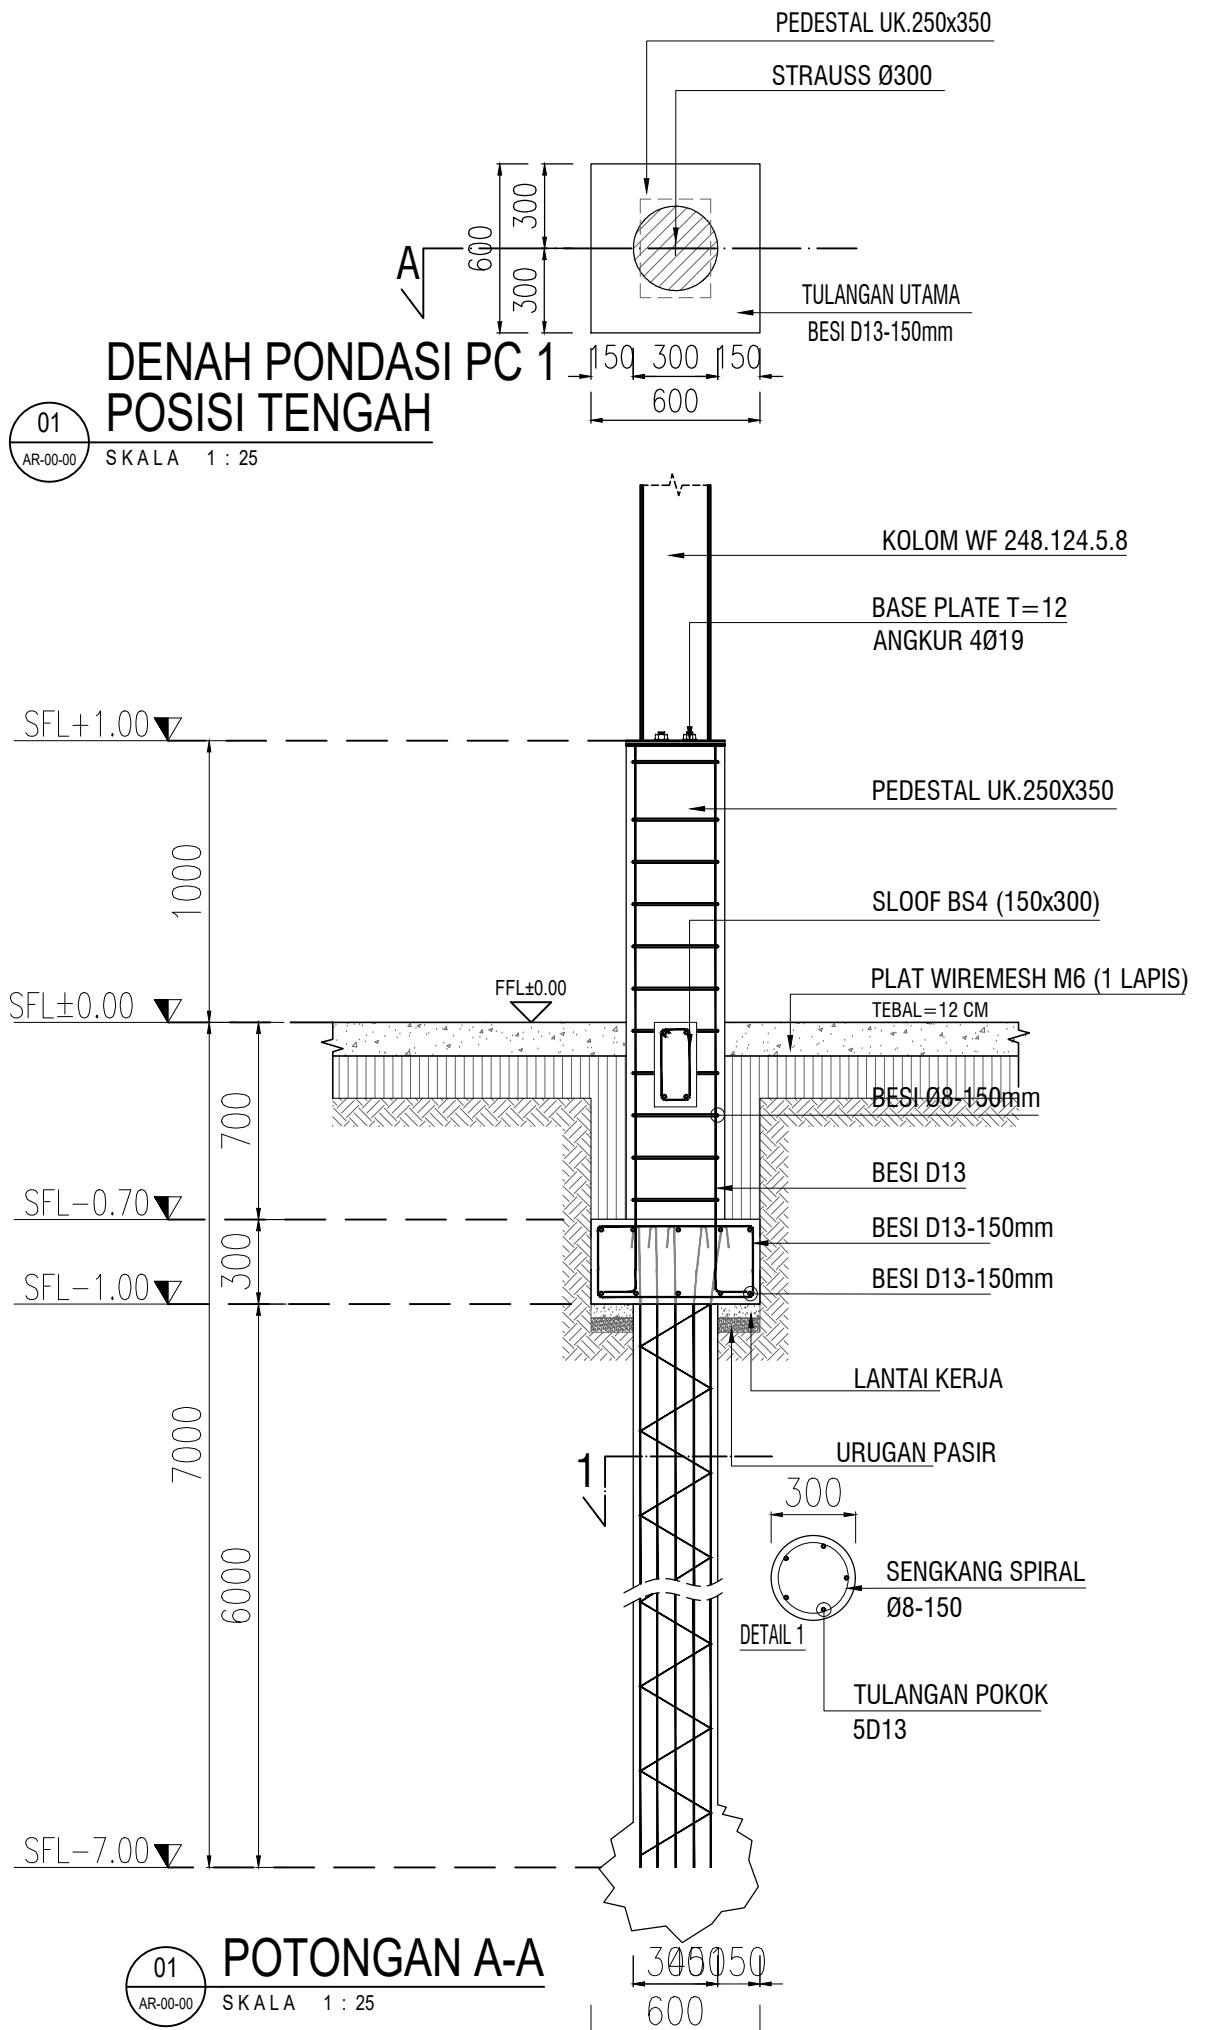

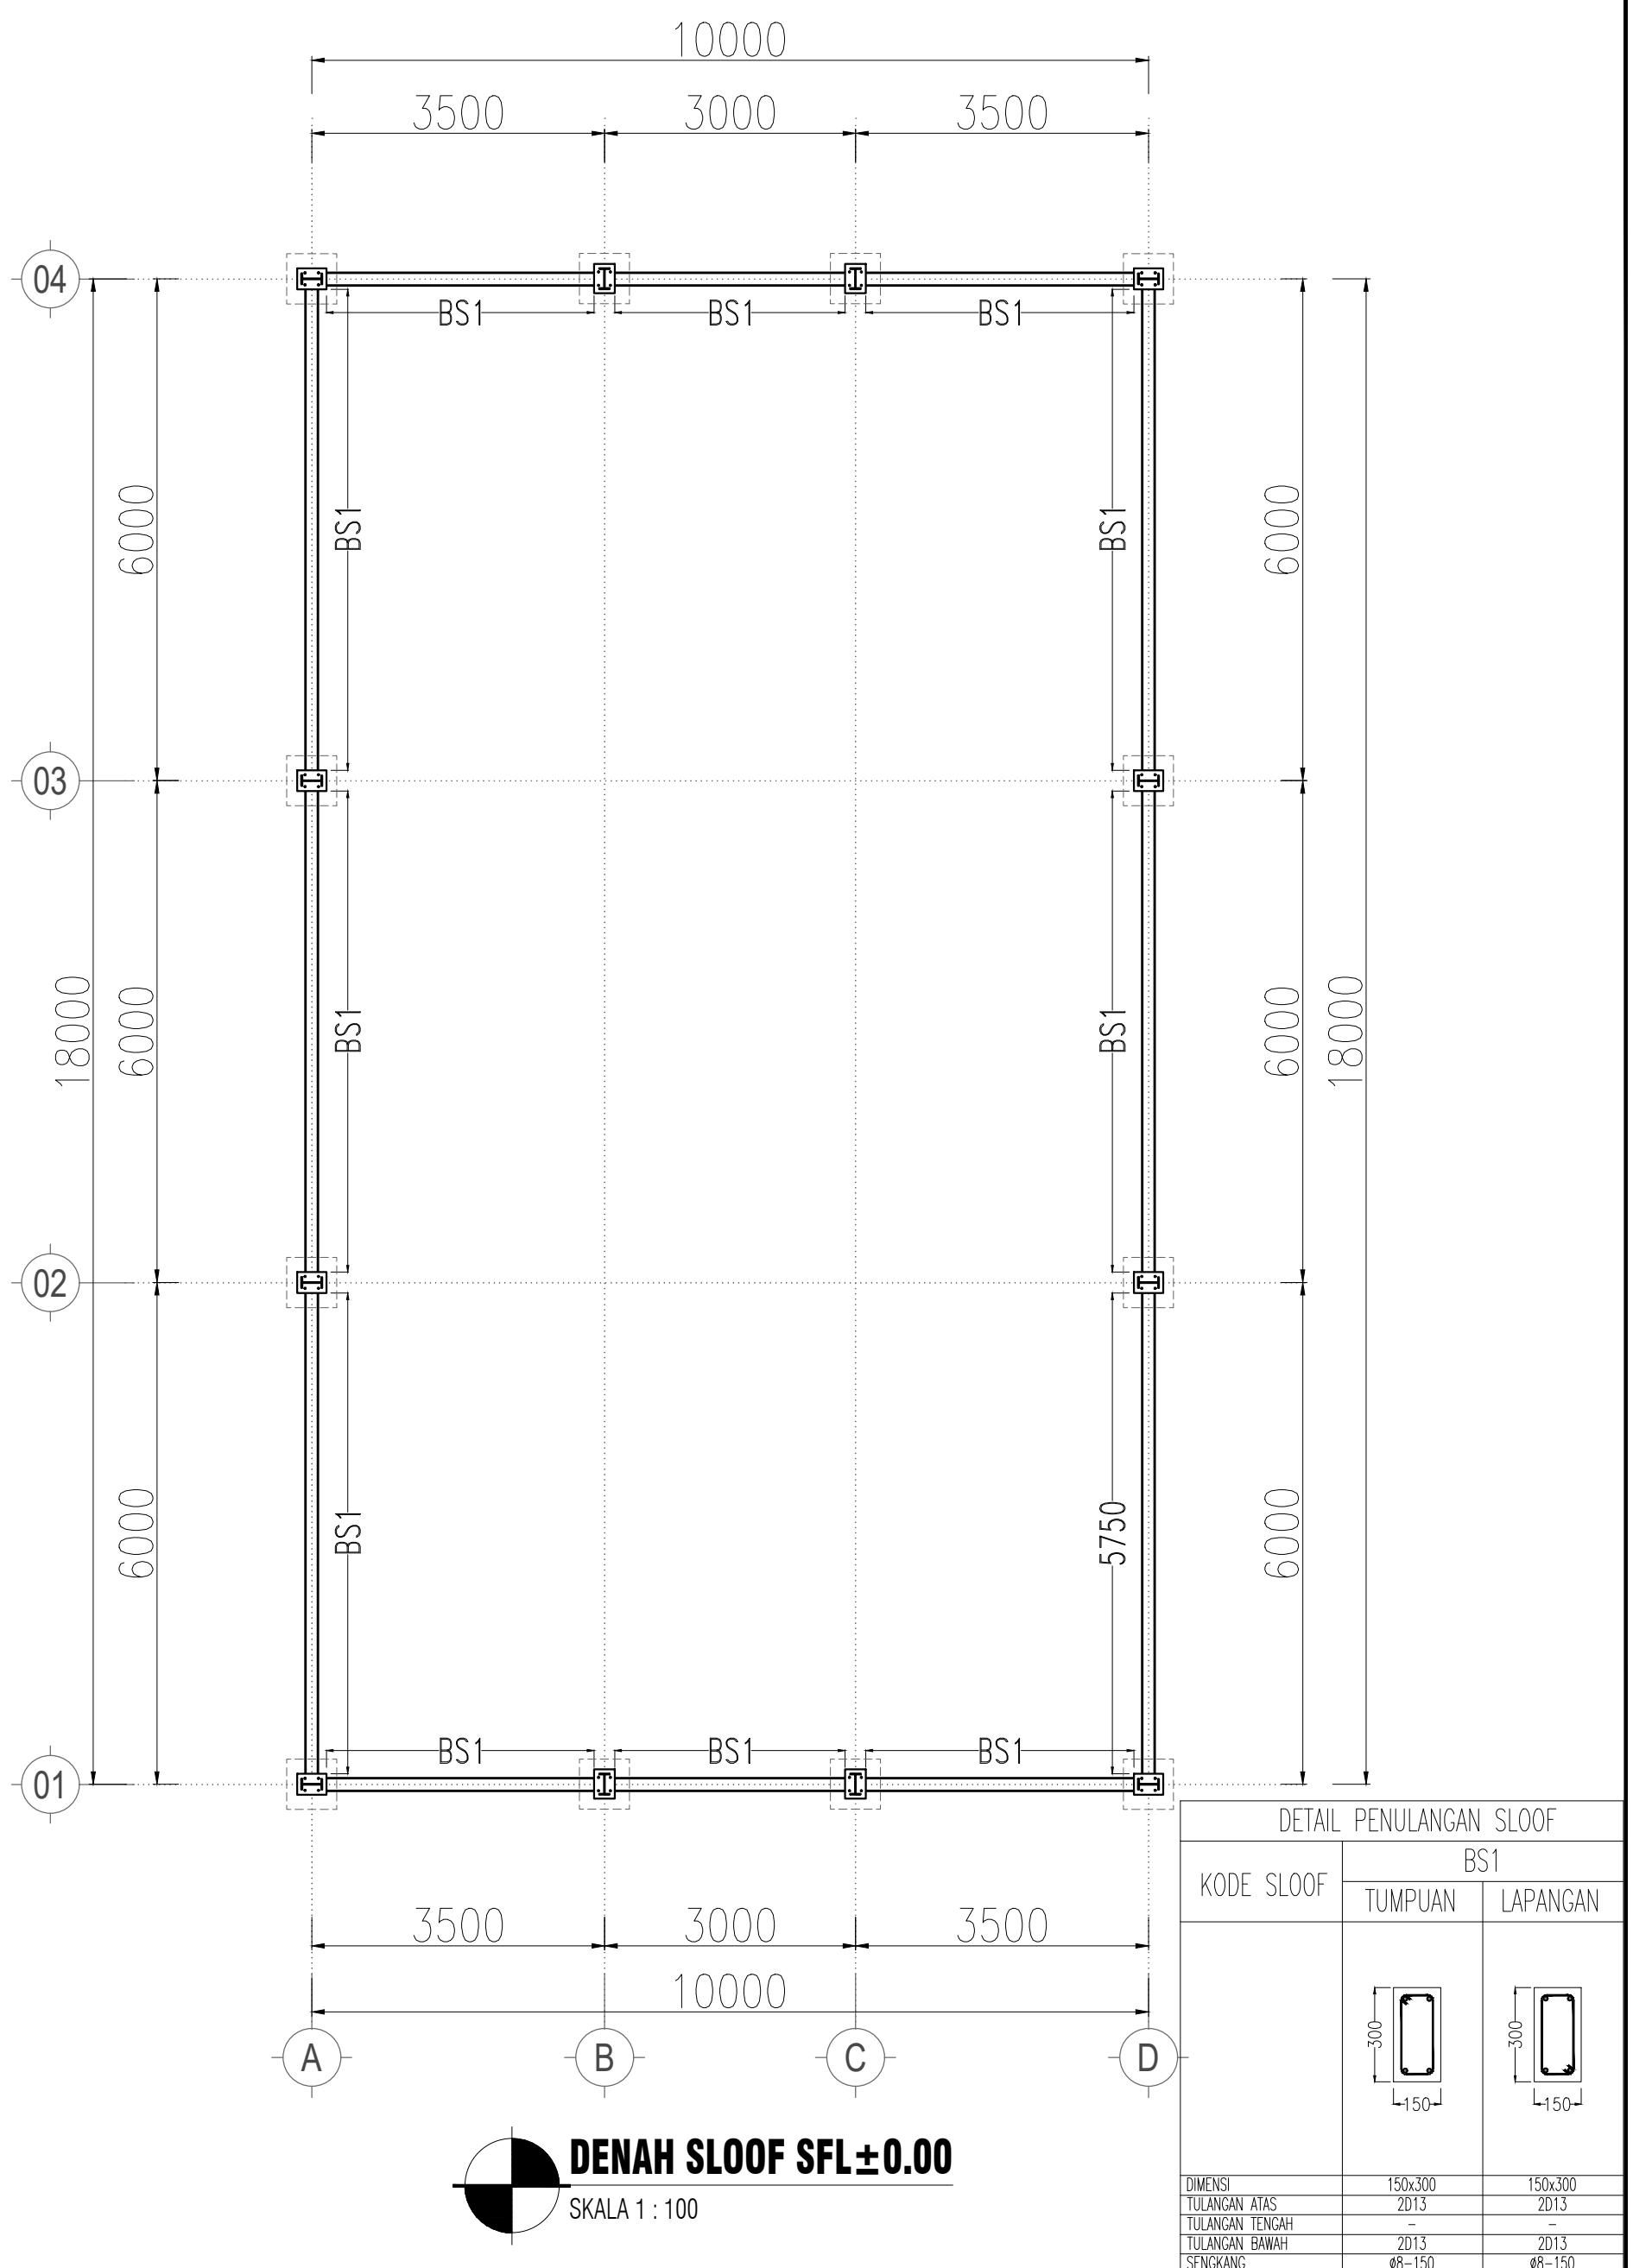

GEVÖRGENS 75-760 75-760

— 1 —

NA

AMERICAN
OPTICAL CORPORATION

МАК

AS, P

AMERICAN RAILROADS

OUPE

RC
EN
YE

ANSWER

ENGLISH

— 1 — < —

NOVEMBER 2013 VOL 41 / NO 11 • www.hopkinsmedicine.org • 11

J E G

AW

WA

B |

SAN

JA

For more information about the study, please contact Dr. John D. Cawley at (609) 258-4626 or via email at jdcawley@princeton.edu.

STR-03-13

JUDUL GAMBAR	SFL±0.00	1. DENAH SLOOF	1 : 100	SKALA
TANGGAL :				
5 APRIL 2024	R	REVISI		

SKALA 1 : 100


1. PELAKSANA ATAU SUBKON WAJIB MEMERIKSA KEMBALI KESUAIAN GAMBAR DENGAN KONDISI LAPANGAN

၁၁၅

DISETUVUI

PENGGUNG JAWAB

NAMA PROYEK

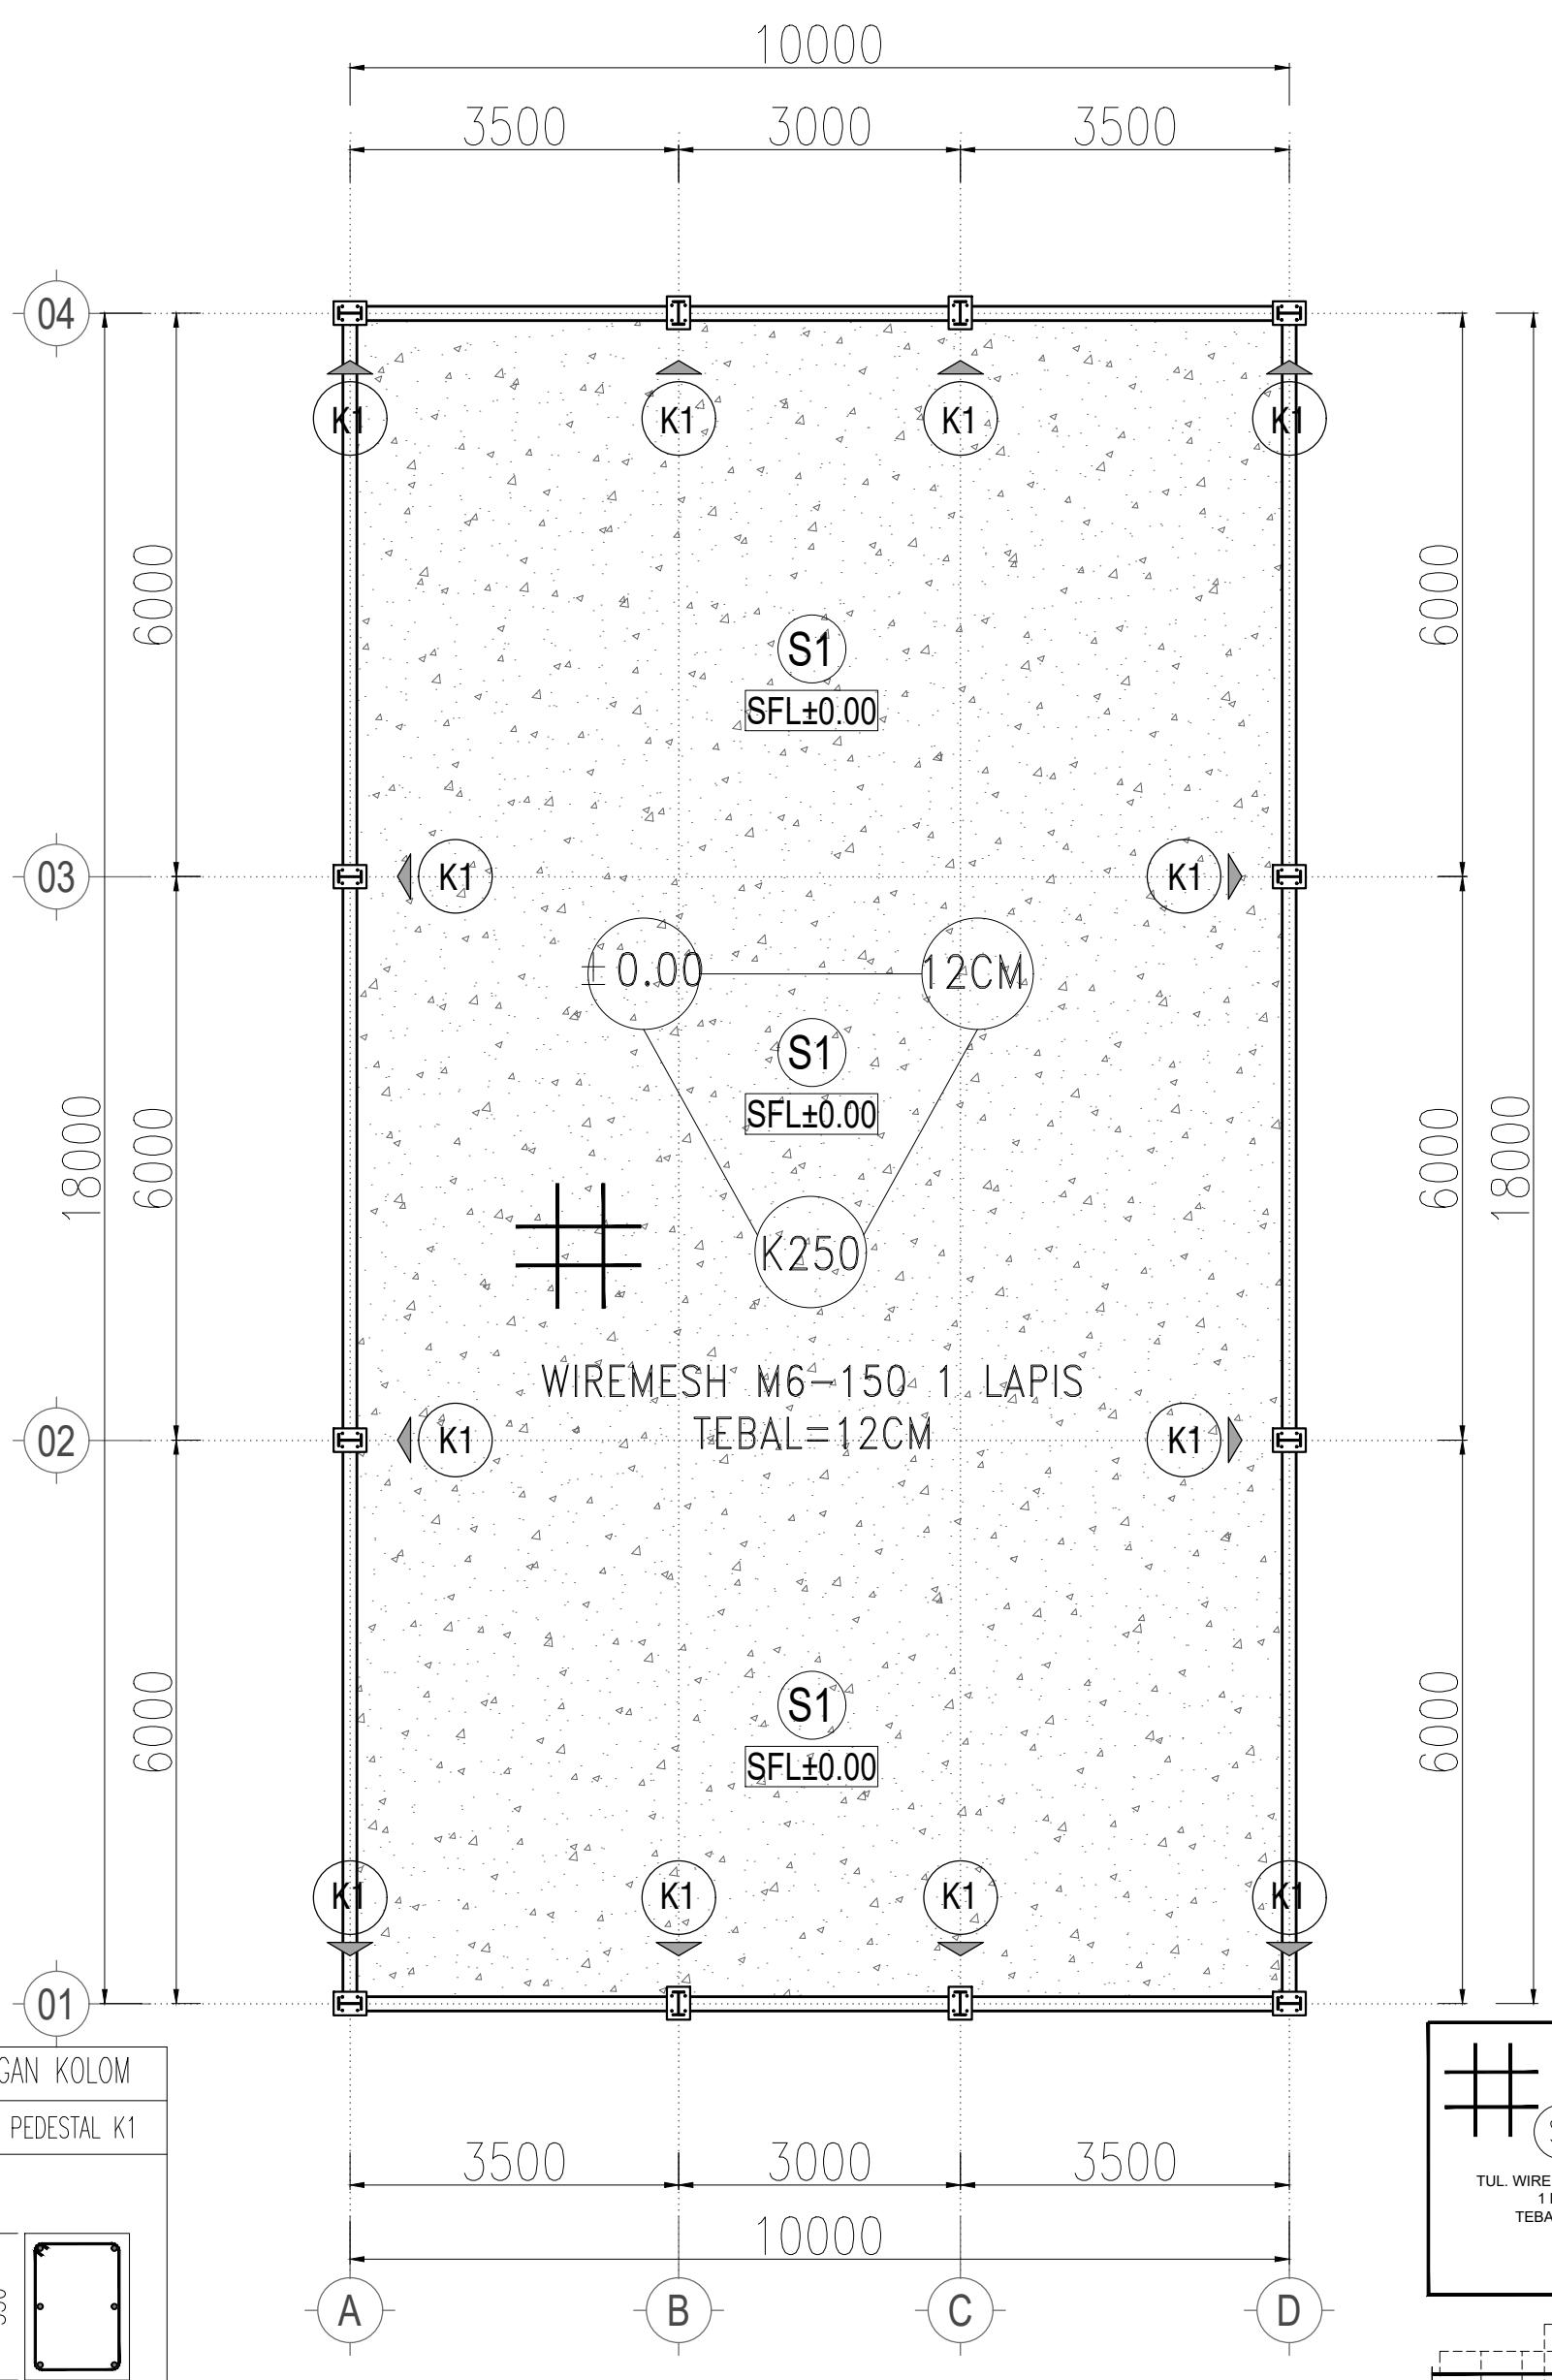

STR-03-14

JUDUL GAMBAR	SKALA
1.DENAH PLAT DAN KOLOM SFL±0.00	1 : 100

TANGGAL : 5 APRIL 2024

REVISI : R3



KODE GAMBAR

NO. LBR


JUMLAH LBR

NAMA PROYEK	
-	
LOKASI PROYEK	
-	-
PENANGGUNG JAWAB	
DIGAMBAR	PELAKSANA
-	-
DISETUJUI	PEMILIK
-	-
CATATAN	
1. PELAKSANA ATAU SUBKON WAJIB MEMERIKSA KEMBALI KESESUAIN GAMBAR DENGAN KONDISI LAPANGAN	
-	
JUDUL GAMBAR	
1.DETAIL SLOOF, BALOK DAN KOLOM	SKALA 1 : 5
-	
TANGGAL :	
5 APRIL 2024	REVISI : R3
KODE GAMBAR	
STR-03-15	
NO. LBR	
15	JUMLAH LBR 35

DETAIL PENULANGAN SLOOF

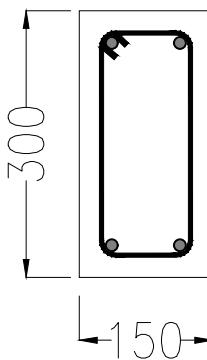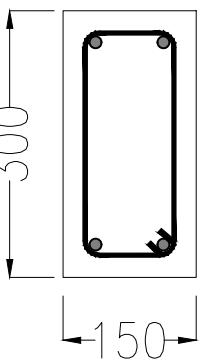KODE SLOOF	BS1	
	TUMPUAN	LAPANGAN
		
DIMENSI	150x300	150x300
TULANGAN ATAS	2D13	2D13
TULANGAN TENGAH	-	-
TULANGAN BAWAH	2D13	2D13
SENGKANG	Ø8-150	Ø8-150


DETAIL PENULANGAN KOLOM

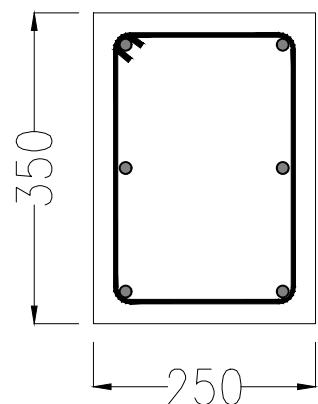KODE KOLOM	PEDESTAL K1
	
DIMENSI	250x350
TULANGAN UTAMA	6D13
SENGKANG	Ø8-150


DETAIL SLOOF, BALOK, DAN KOLOM

01
AR-00-00

SKALA 1 : 5

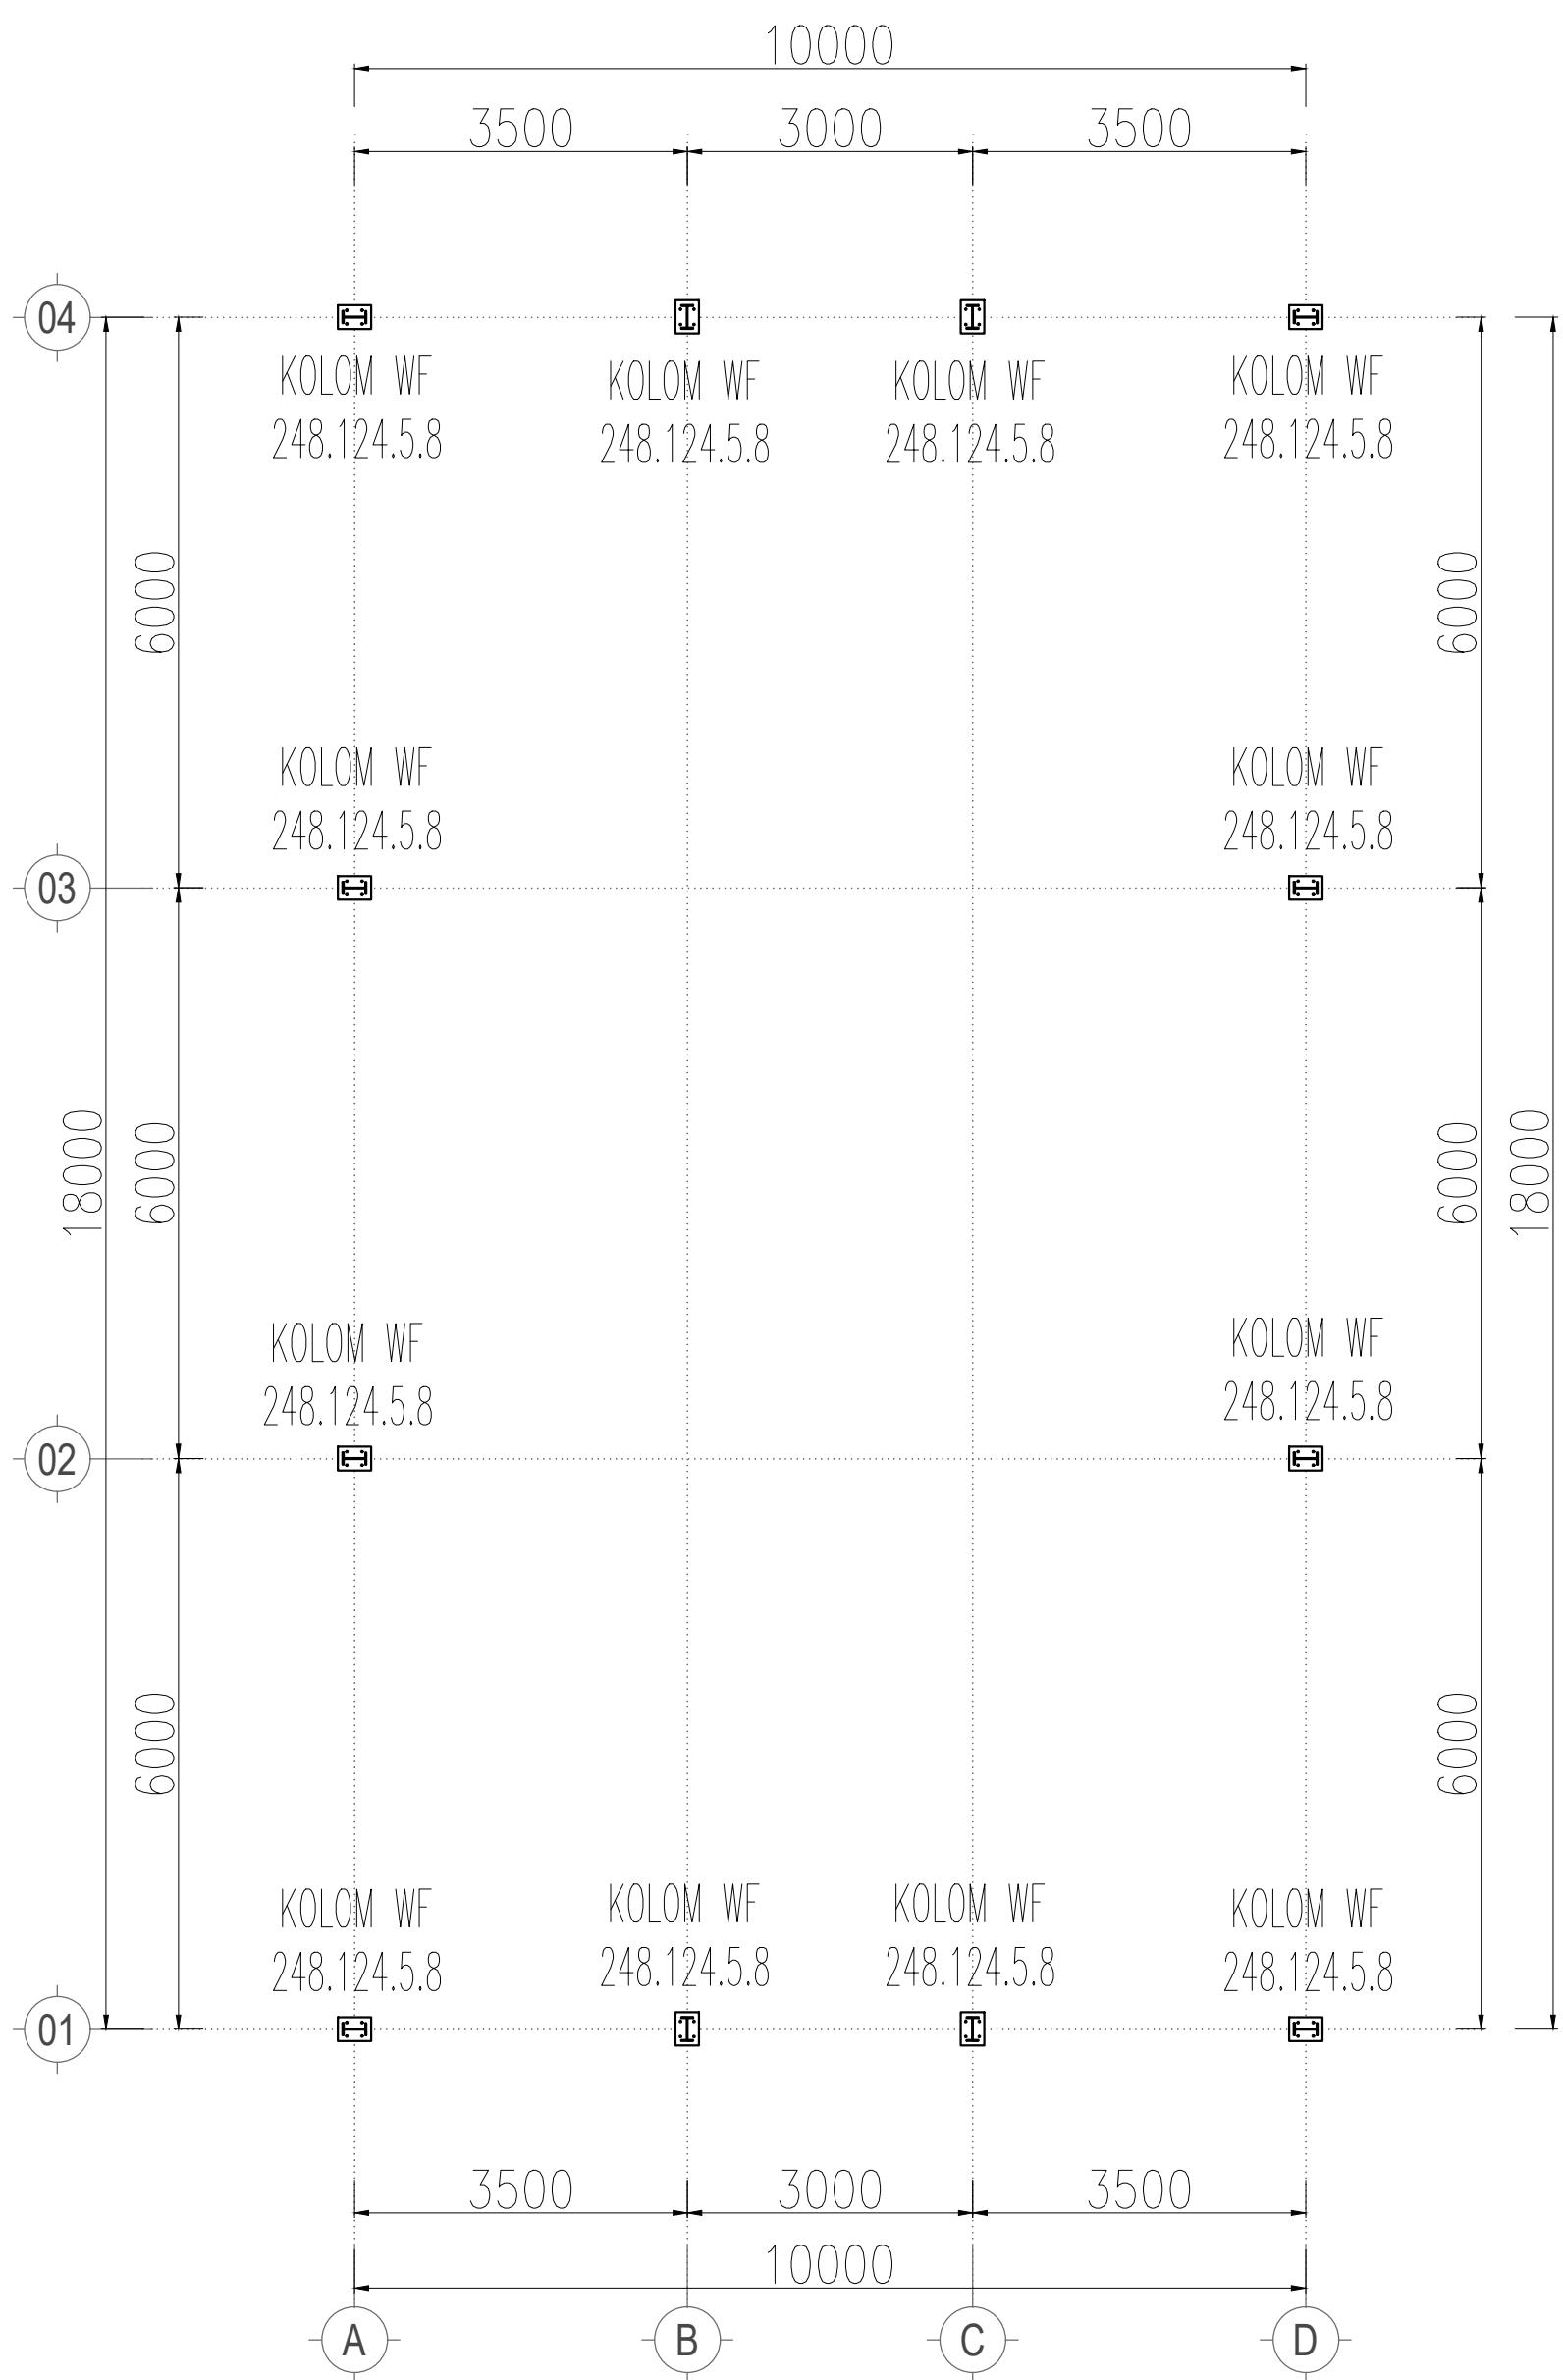

NO	ITEM KOLOM	KETERANGAN
1.		KOLOM WF 248.124.5.8

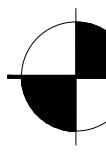


DENAH KOLOM BAJA SFL+1.00 (ELEVASI BOTTOM)

SKALA 1 : 100

1. PELAKSANA ATAU SUBKON WAJIB MEMERIKSA KEMBALI KESESUAIN GAMBAR DENGAN KONDISI LAPANGAN


NAMA PROYEK		-	
-		-	
LOKASI PROYEK		-	
-		-	
PENANGGUNG JAWAB		-	
-		-	
CATATAN		-	
-		-	
1. PELAKSANA ATAU SUBKON WAJIB MEMERIKSA KEMBALI KESESUAIN GAMBAR DENGAN KONDISI LAPANGAN		-	
-		-	
JUDUL GAMBAR	SKALA	-	
1.DENAHKOLOM BAJA 1 : 100 SFL+1.00 (ELEVASI BOTTOM)		-	
TANGGAL :	REVISI :	-	
5 APRIL 2024	R3	-	
KODE GAMBAR		-	
STR-03-16		-	
NO. LBR	JUMLAH LBR	-	
16	35	-	

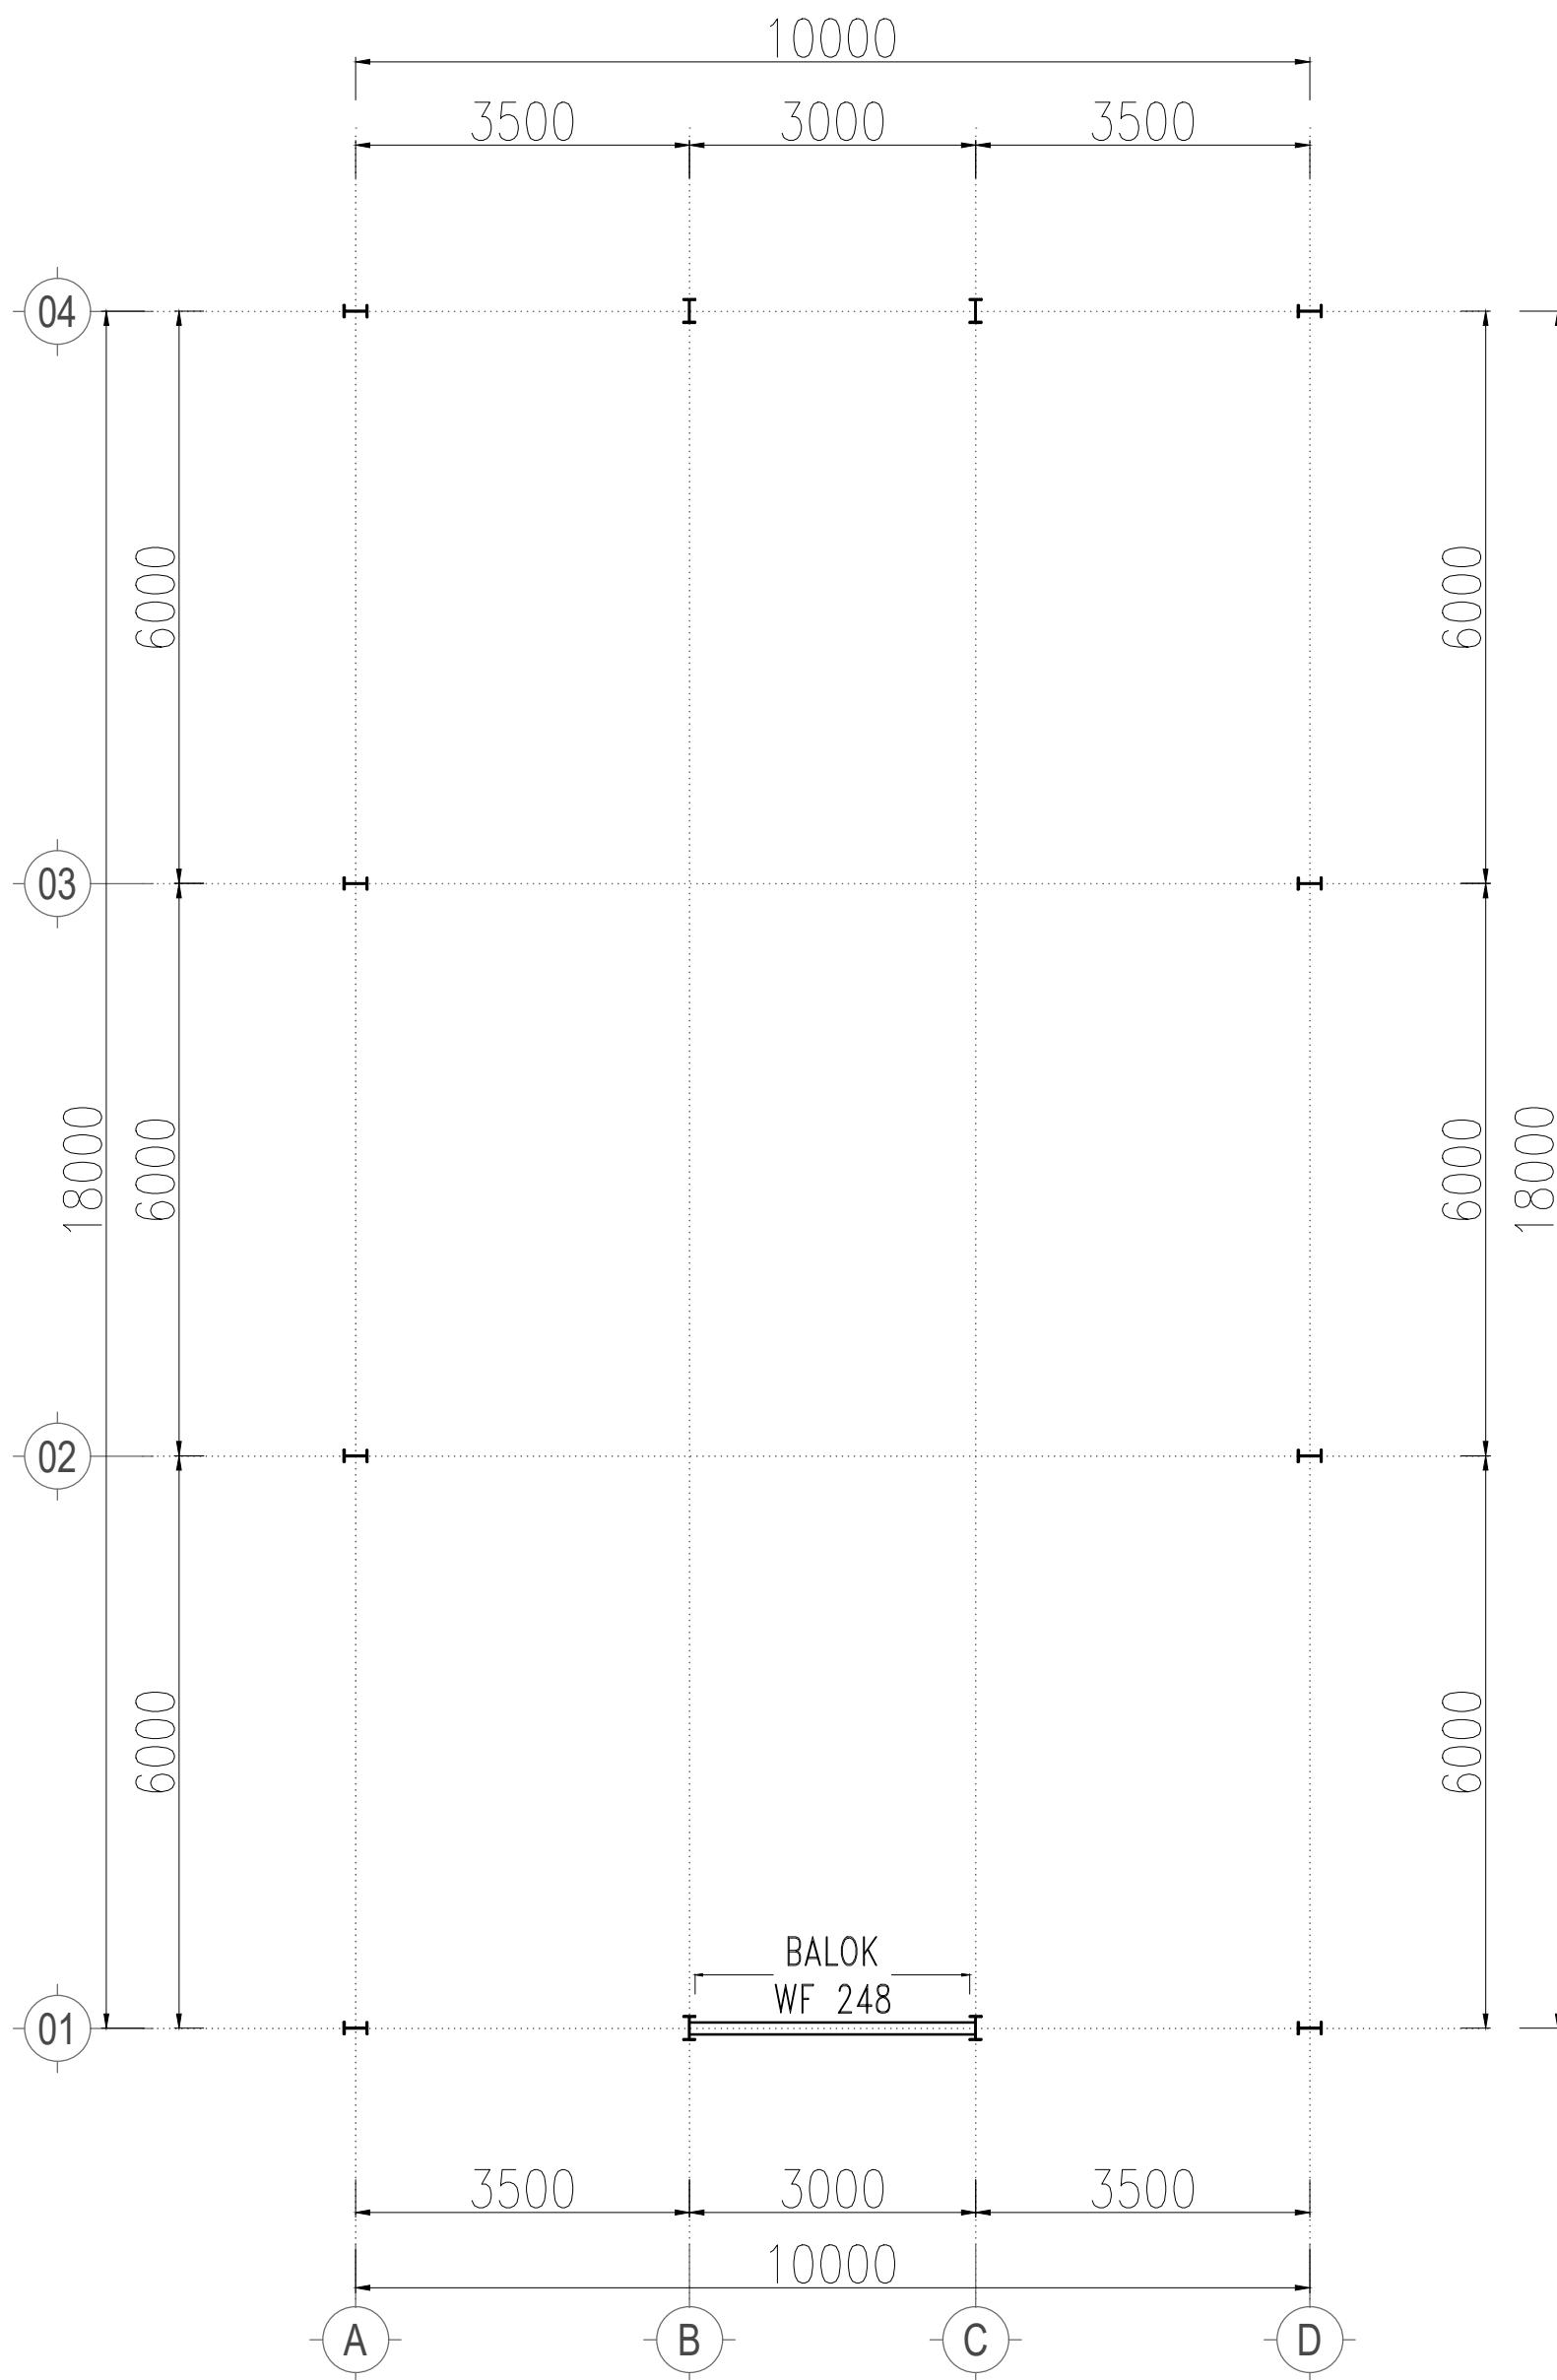

DENAH BALOK RELL PINTU SFL+3.25



CATATAN		LOKASI PROYEK	
1. PELAKSANA ATAU SUBKON WAJIB MEMERIKSA KEMBALI KESESUAIN GAMBAR DENGAN KONDISI LAPANGAN		PENANGGUNG JAWAB	
JUDUL GAMBAR	SKALA	DIGAMBAR	PELAKSANA
1.DENAH BALOK RELL PINTU SFL+3.25	1 : 100	DISETUJUJ	PEMILIK
TANGGAL :	REVISI :		
5 APRIL 2024	R3		
KODE GAMBAR			
STR-03-17			
NO. LBR	JUMLAH LBR		
17	35		

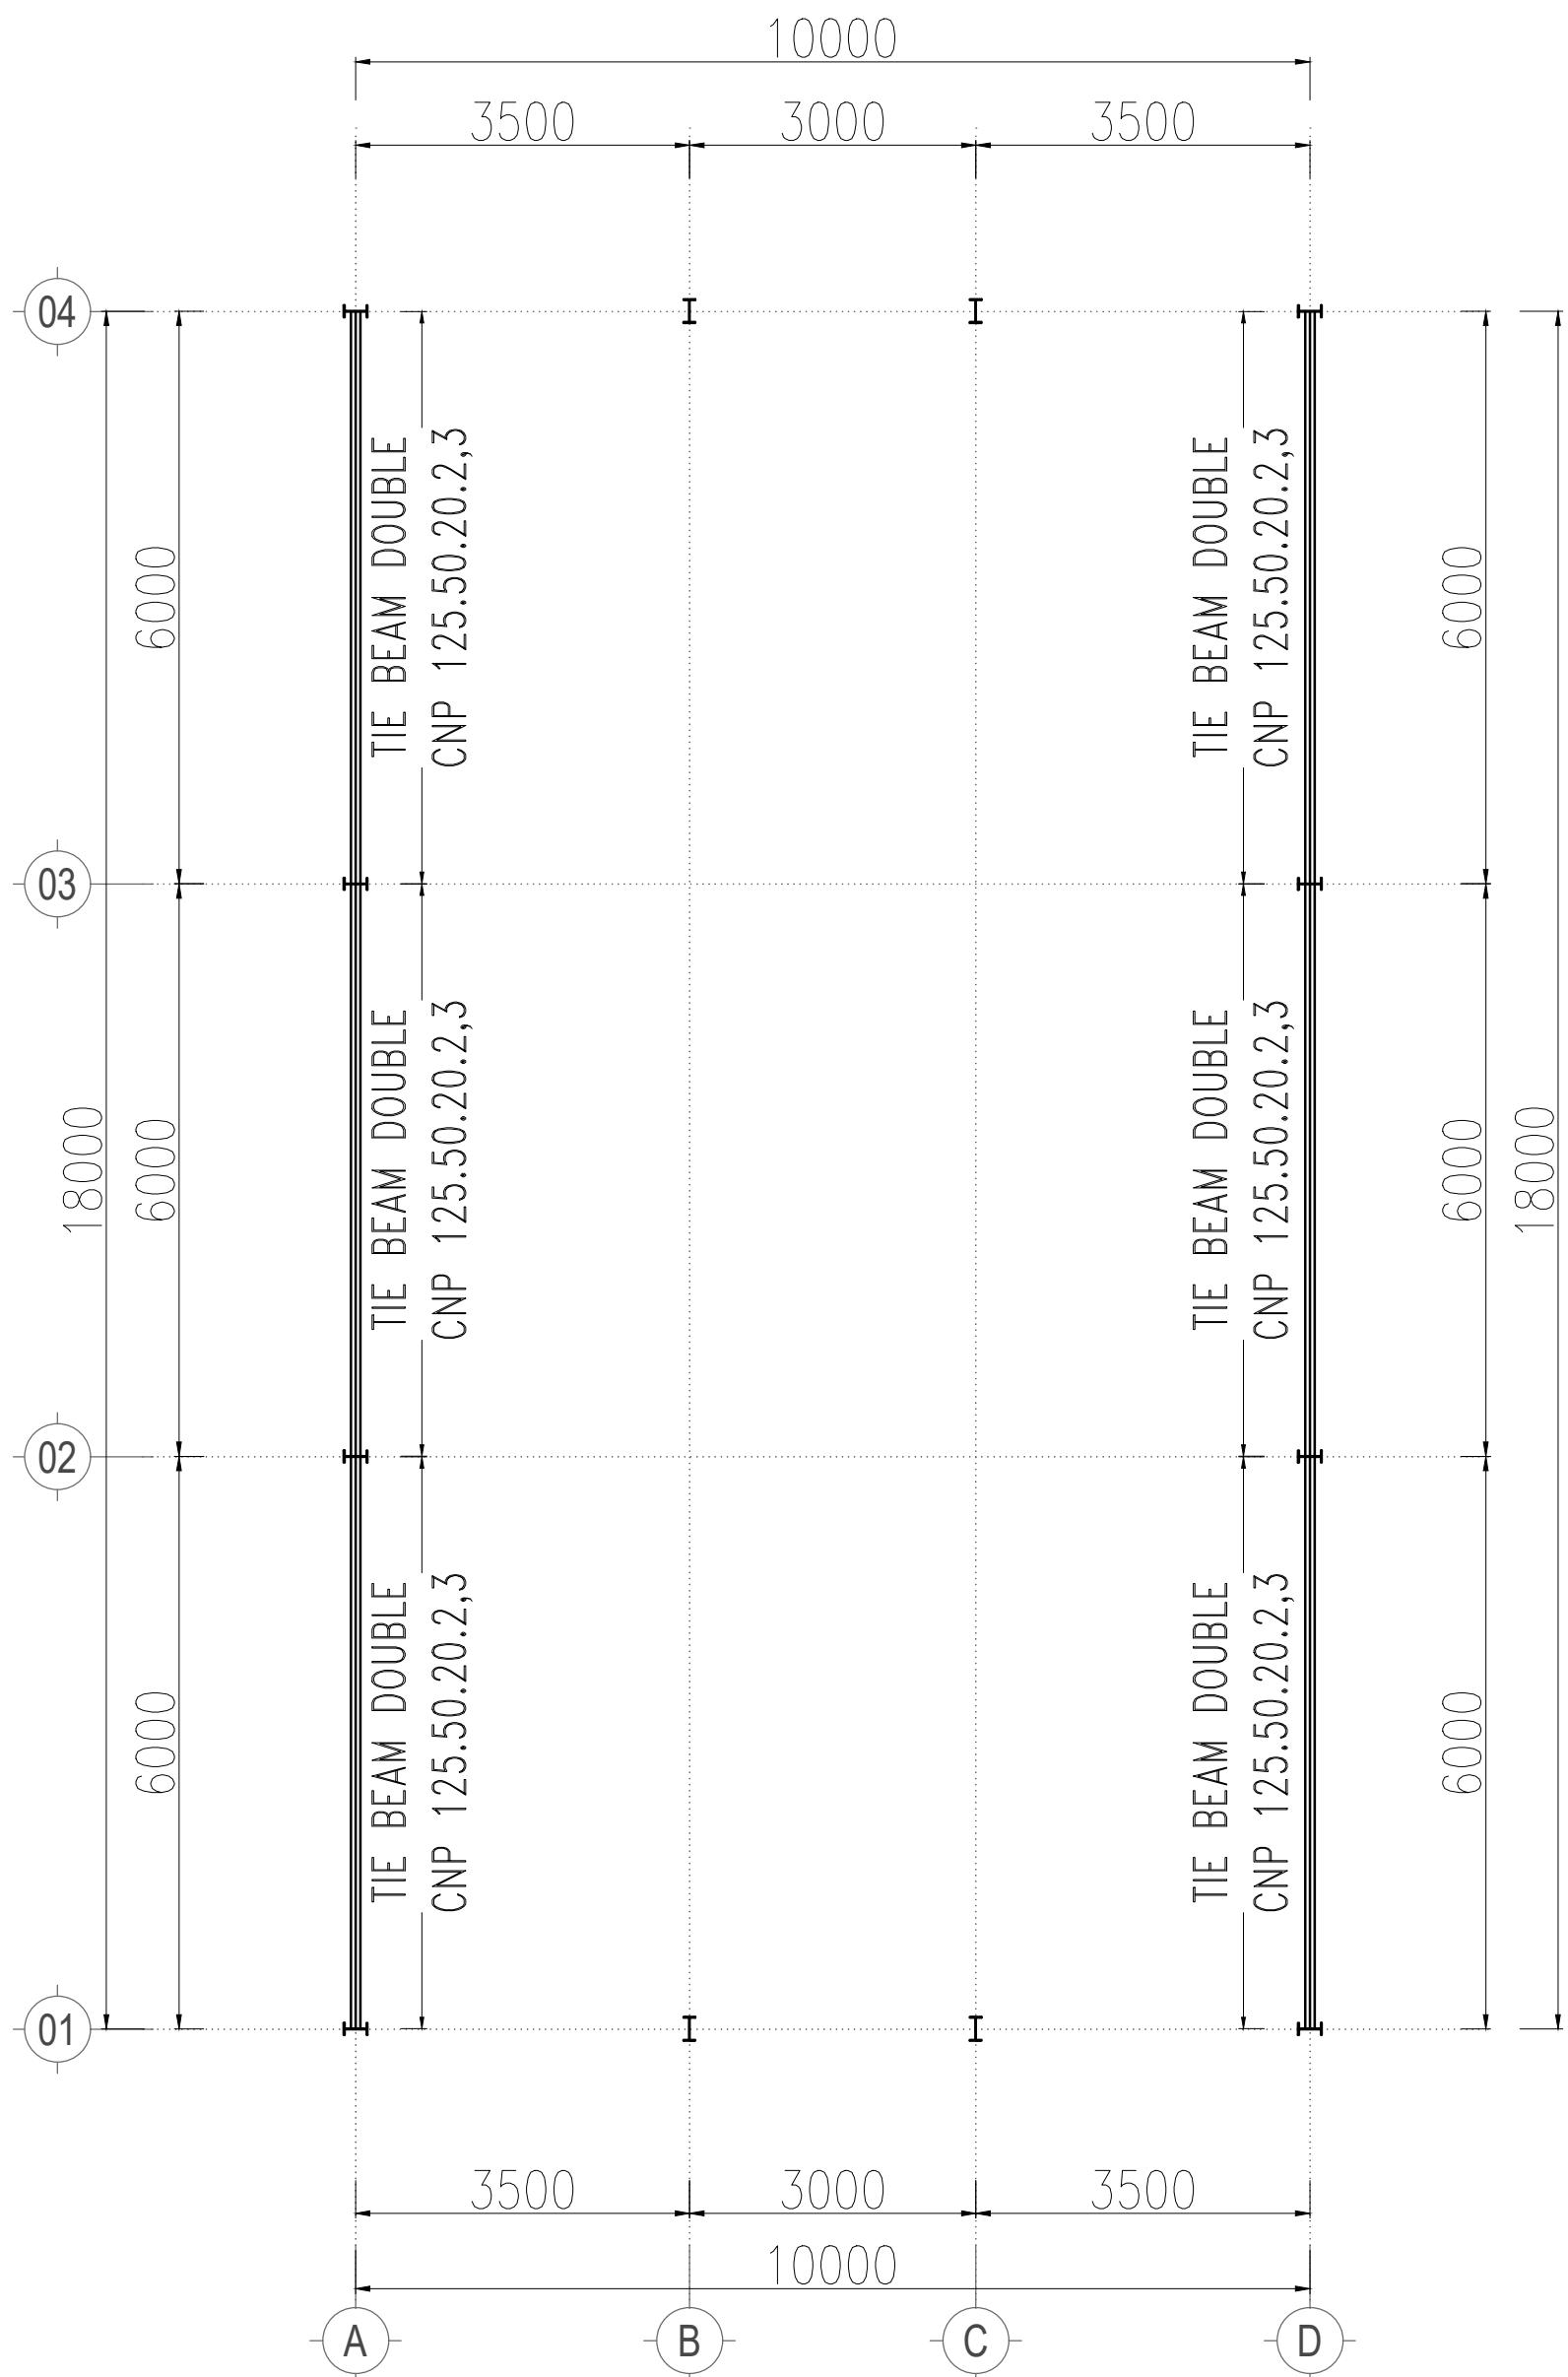


DENAH TIE BEAM SFL+7.00

SKALA 1 : 100

NO	ITEM TIE BEAM	KETERANGAN
1.		TIE BEAM DOUBLE CNP 125.50.2,3

NAMA PROYEK	-	
LOKASI PROYEK	-	
PENANGGUNG JAWAB	<div style="display: flex; justify-content: space-around;"> <div style="text-align: center;"> <p>DIGAMBAR</p> <p>PELAKSANA</p> </div> <div style="text-align: center;"> <p>DISETUJU</p> <p>PENULIK</p> </div> </div>	
CATATAN	<p>1. PELAKSANA ATAU SUBKON WAJIB MEMERIKSA KEMBALI KESESUAIN GAMBAR DENGAN KONDISI LAPANGAN</p>	
JUDUL GAMBAR	SKALA	
1.DENAH TIE BEAM SFL+7.00	1 : 100	
TANGGAL :	REVISI :	
5 APRIL 2024	R3	
KODE GAMBAR	STR-03-18	
NO. LBR	JUMLAH LBR	
18	35	

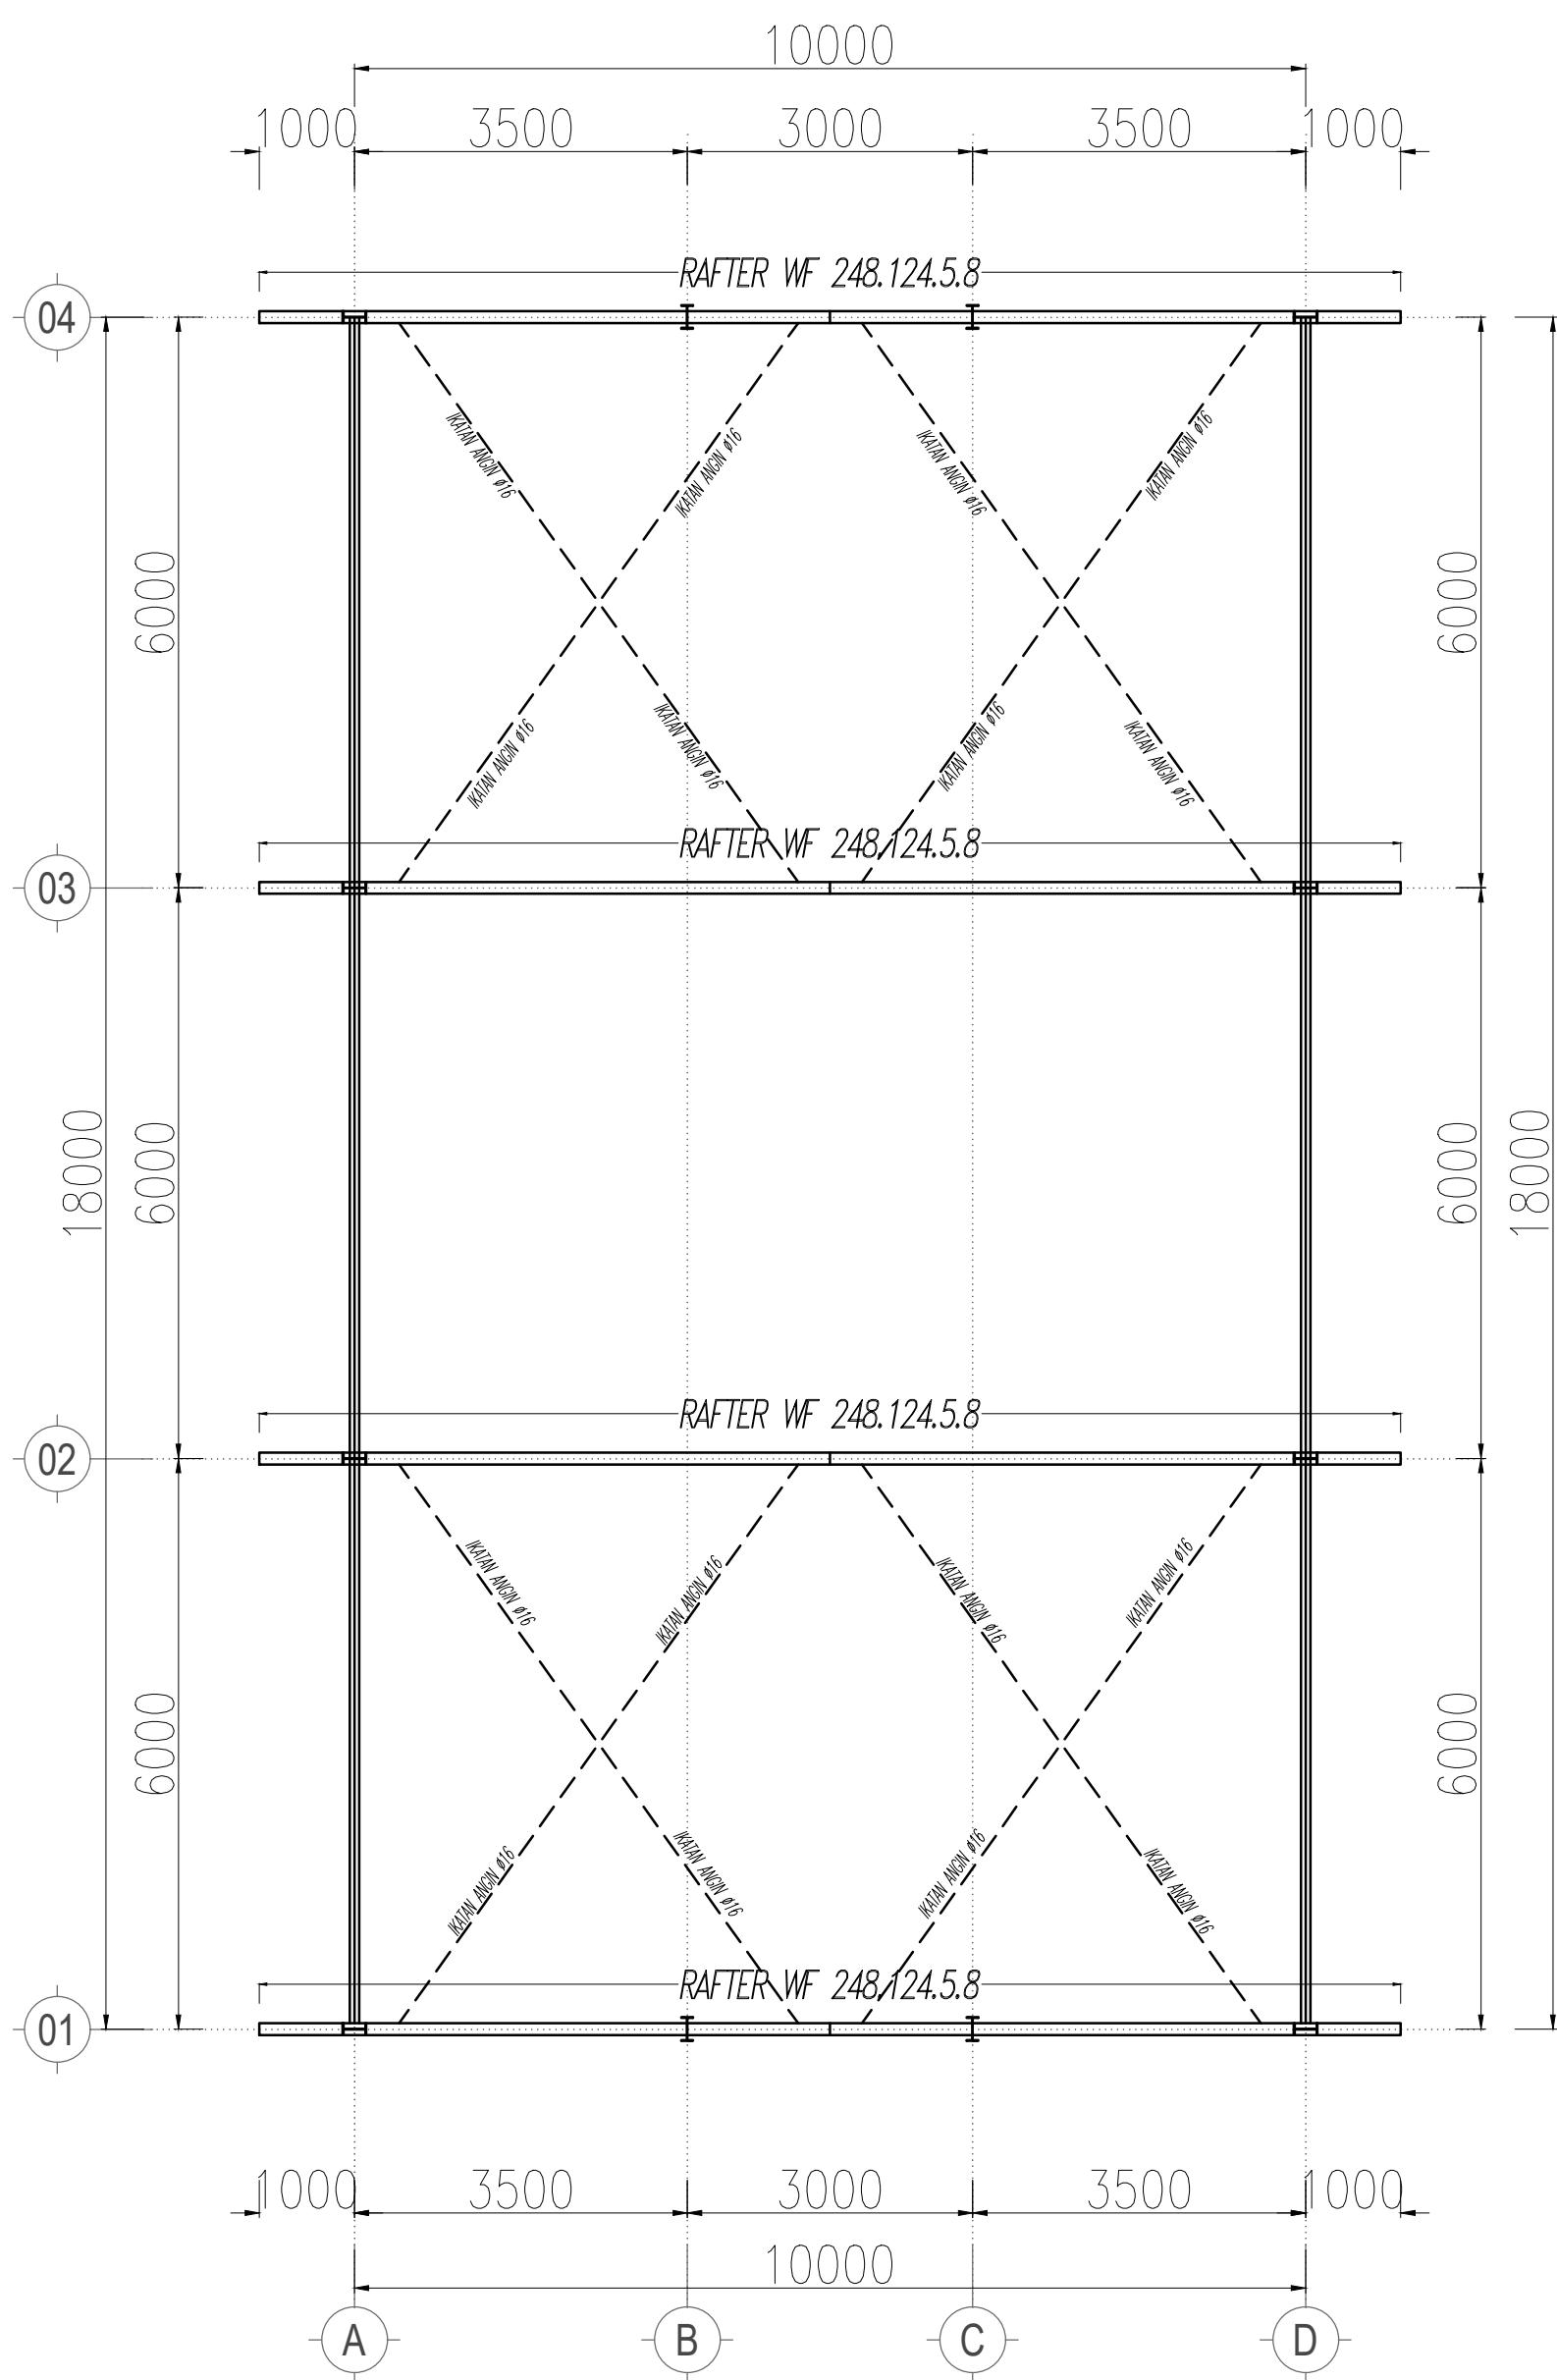

DENAH RAFTER/KUDA-KUDA
SKALA 1 : 100

NAMA PROYEK

LOKASI PROYEK

PENGANGGUNG JAWAB

DIGARBAR

PELAKSANA

DISETUJUJ

PEMILIK

1. PELAKSANA ATAU SUBKON WAJIB
MEMERIKSA KEMBALI KESESUAIN
GAMBAR DENGAN KONDISI
LAPANGAN


JUDUL GAMBAR	SKALA
1.DENA RAFTER/KUDA-KUDA	1 : 100

TANGGAL :	REVISI :
5 APRIL 2024	R3

KODE GAMBAR

STR-03-19

NO. LBR	JUMLAH LBR
19	35

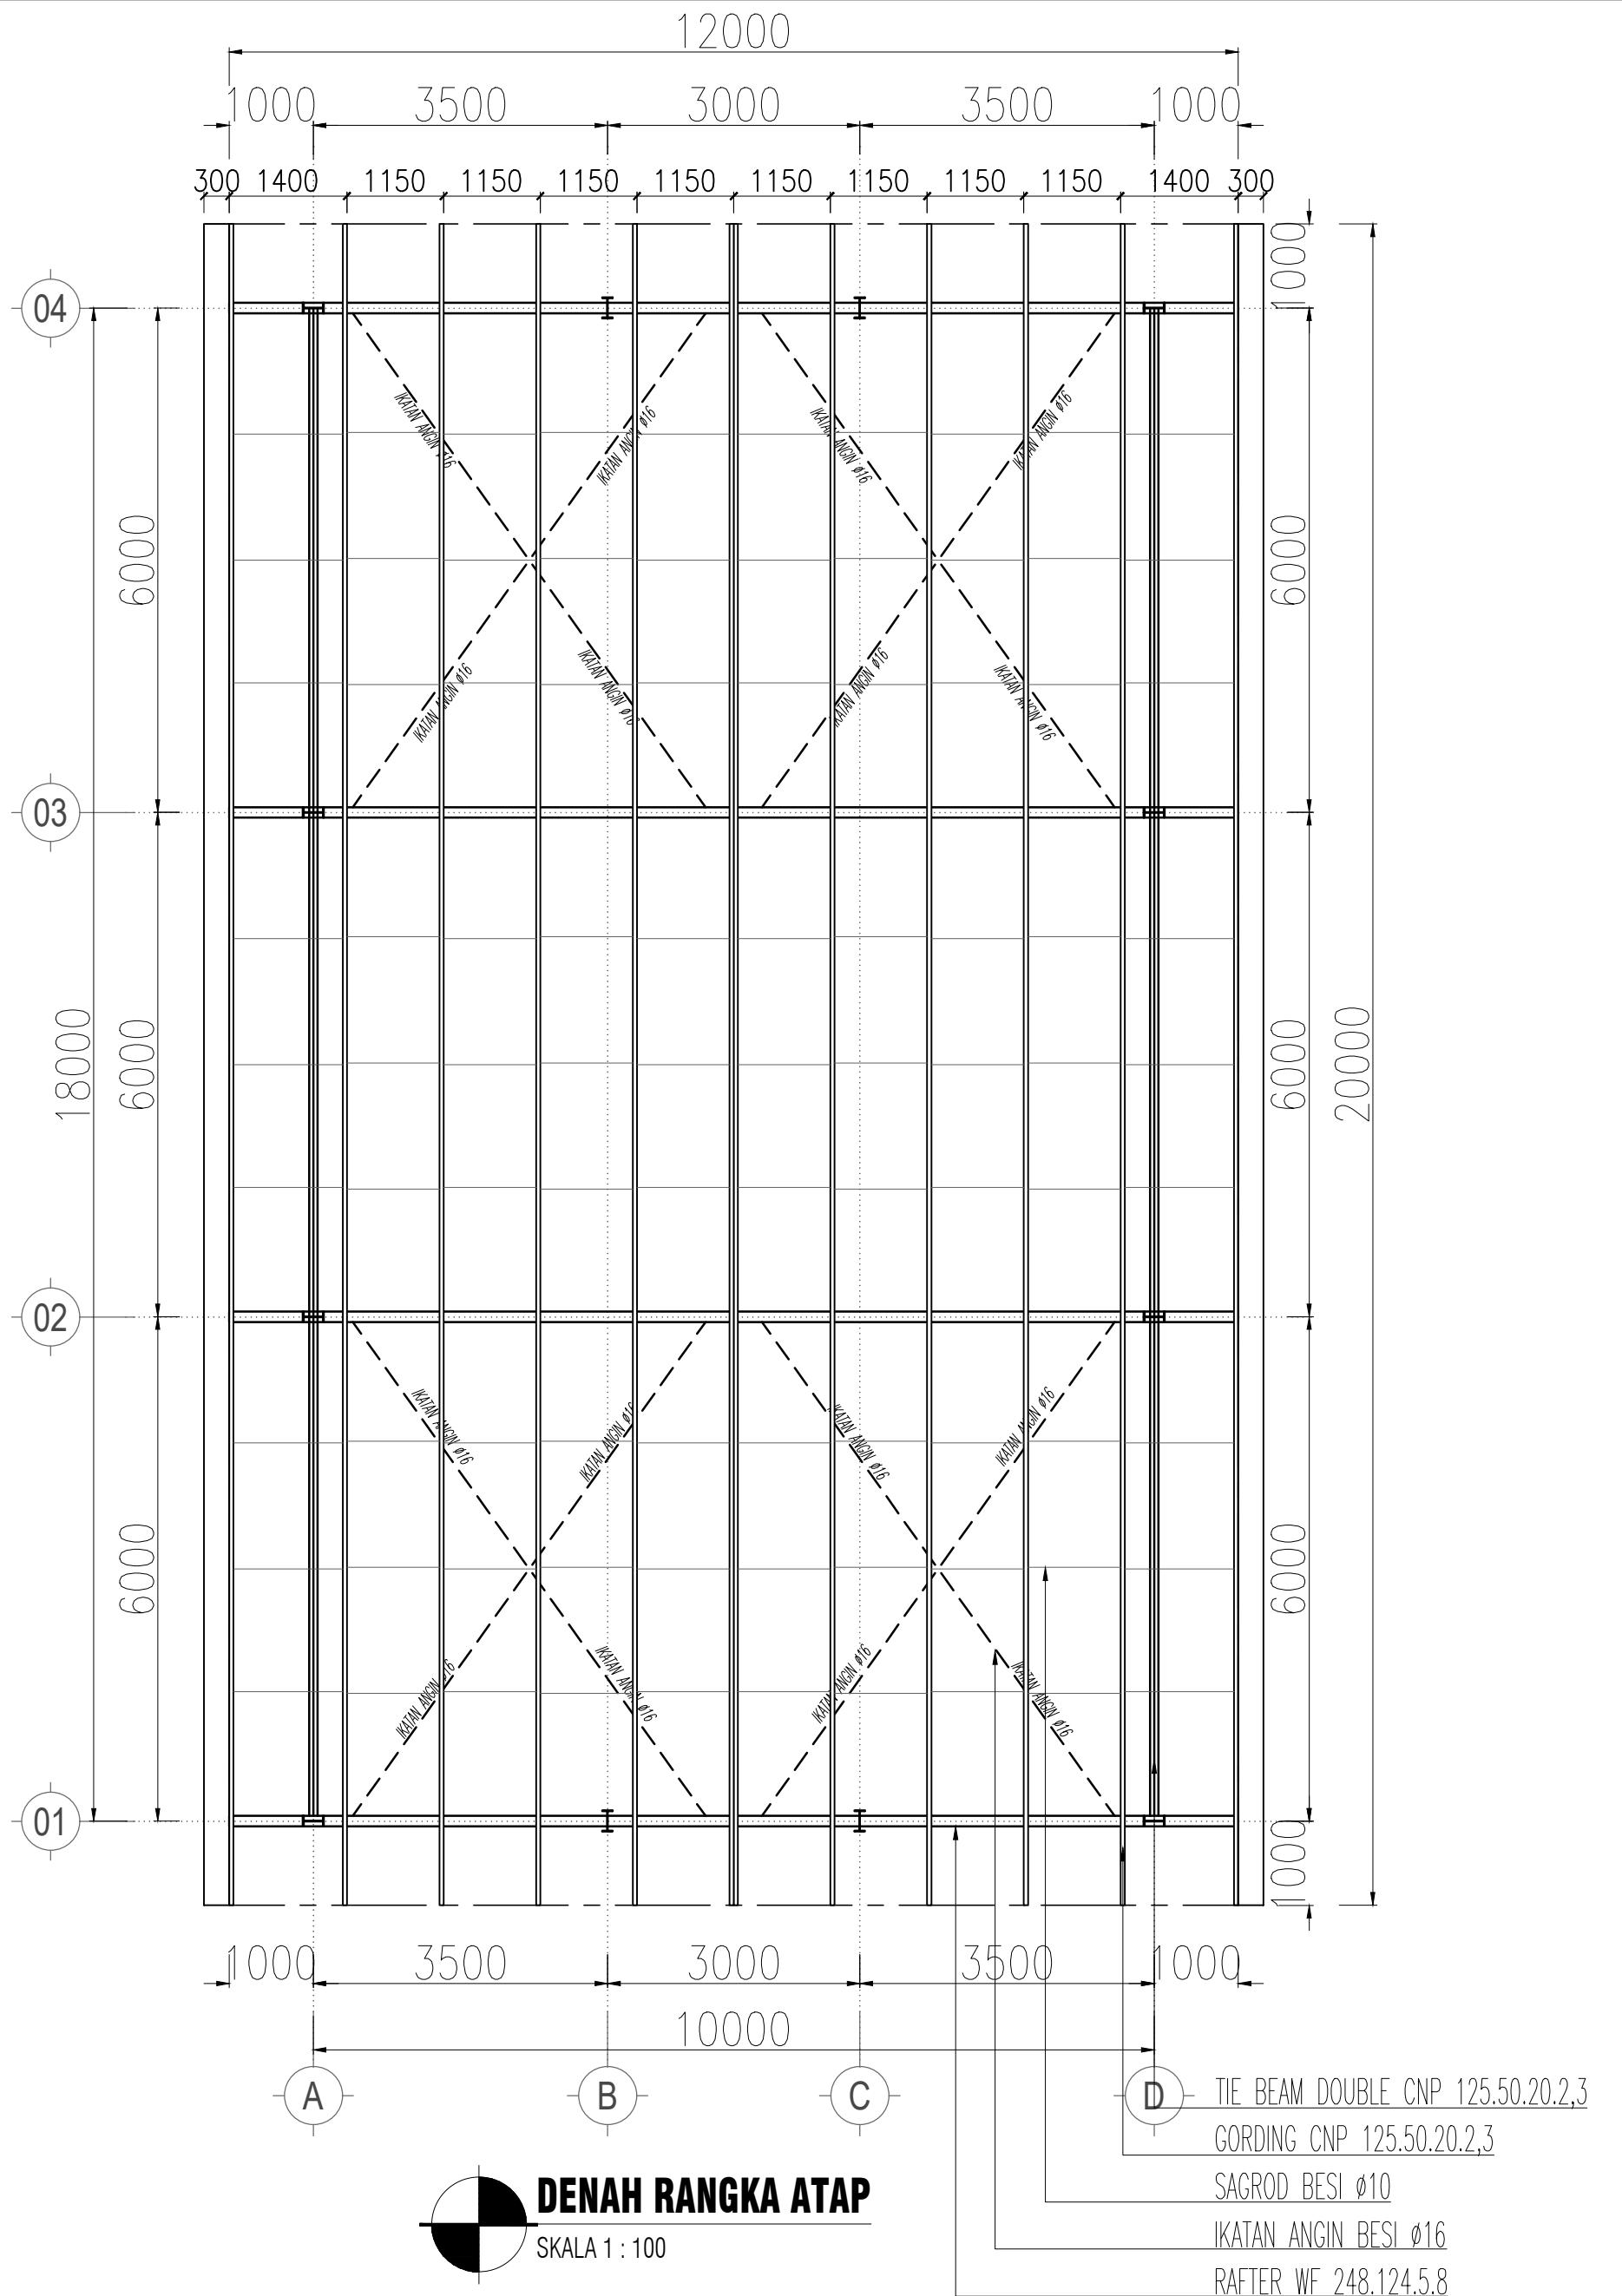



JUDUL GAMBAR		SKALA		
1.DENAH RANGKA ATAP		1 : 100		
TANGGAL :		REVISI :		
5 APRIL 2024		R3		
KODE GAMBAR				
STR-03-20				
NO. LBR	JUMLAH LBR			
20	35			

NAMA PROYEK

LOKASI PROYEK


NAMA PROYEK	
-	
LOKASI PROYEK	
-	-
PENANGGUNG JAWAB	
DIGAMBAR	PELAKSANA
-	-
DISETUJUI	PEMILIK
-	-
CATATAN	
1. PELAKSANA ATAU SUBKON WAJIB MEMERIKSA KEMBALI KESESUAIN GAMBAR DENGAN KONDISI LAPANGAN	
-	
JUDUL GAMBAR	SKALA
1.POTONGAN B-B (KEY SECTION)	1 : 50
TANGGAL :	REVISI :
5 APRIL 2024	R3
KODE GAMBAR	
STR-03-21	
NO. LBR	JUMLAH LBR
21	35

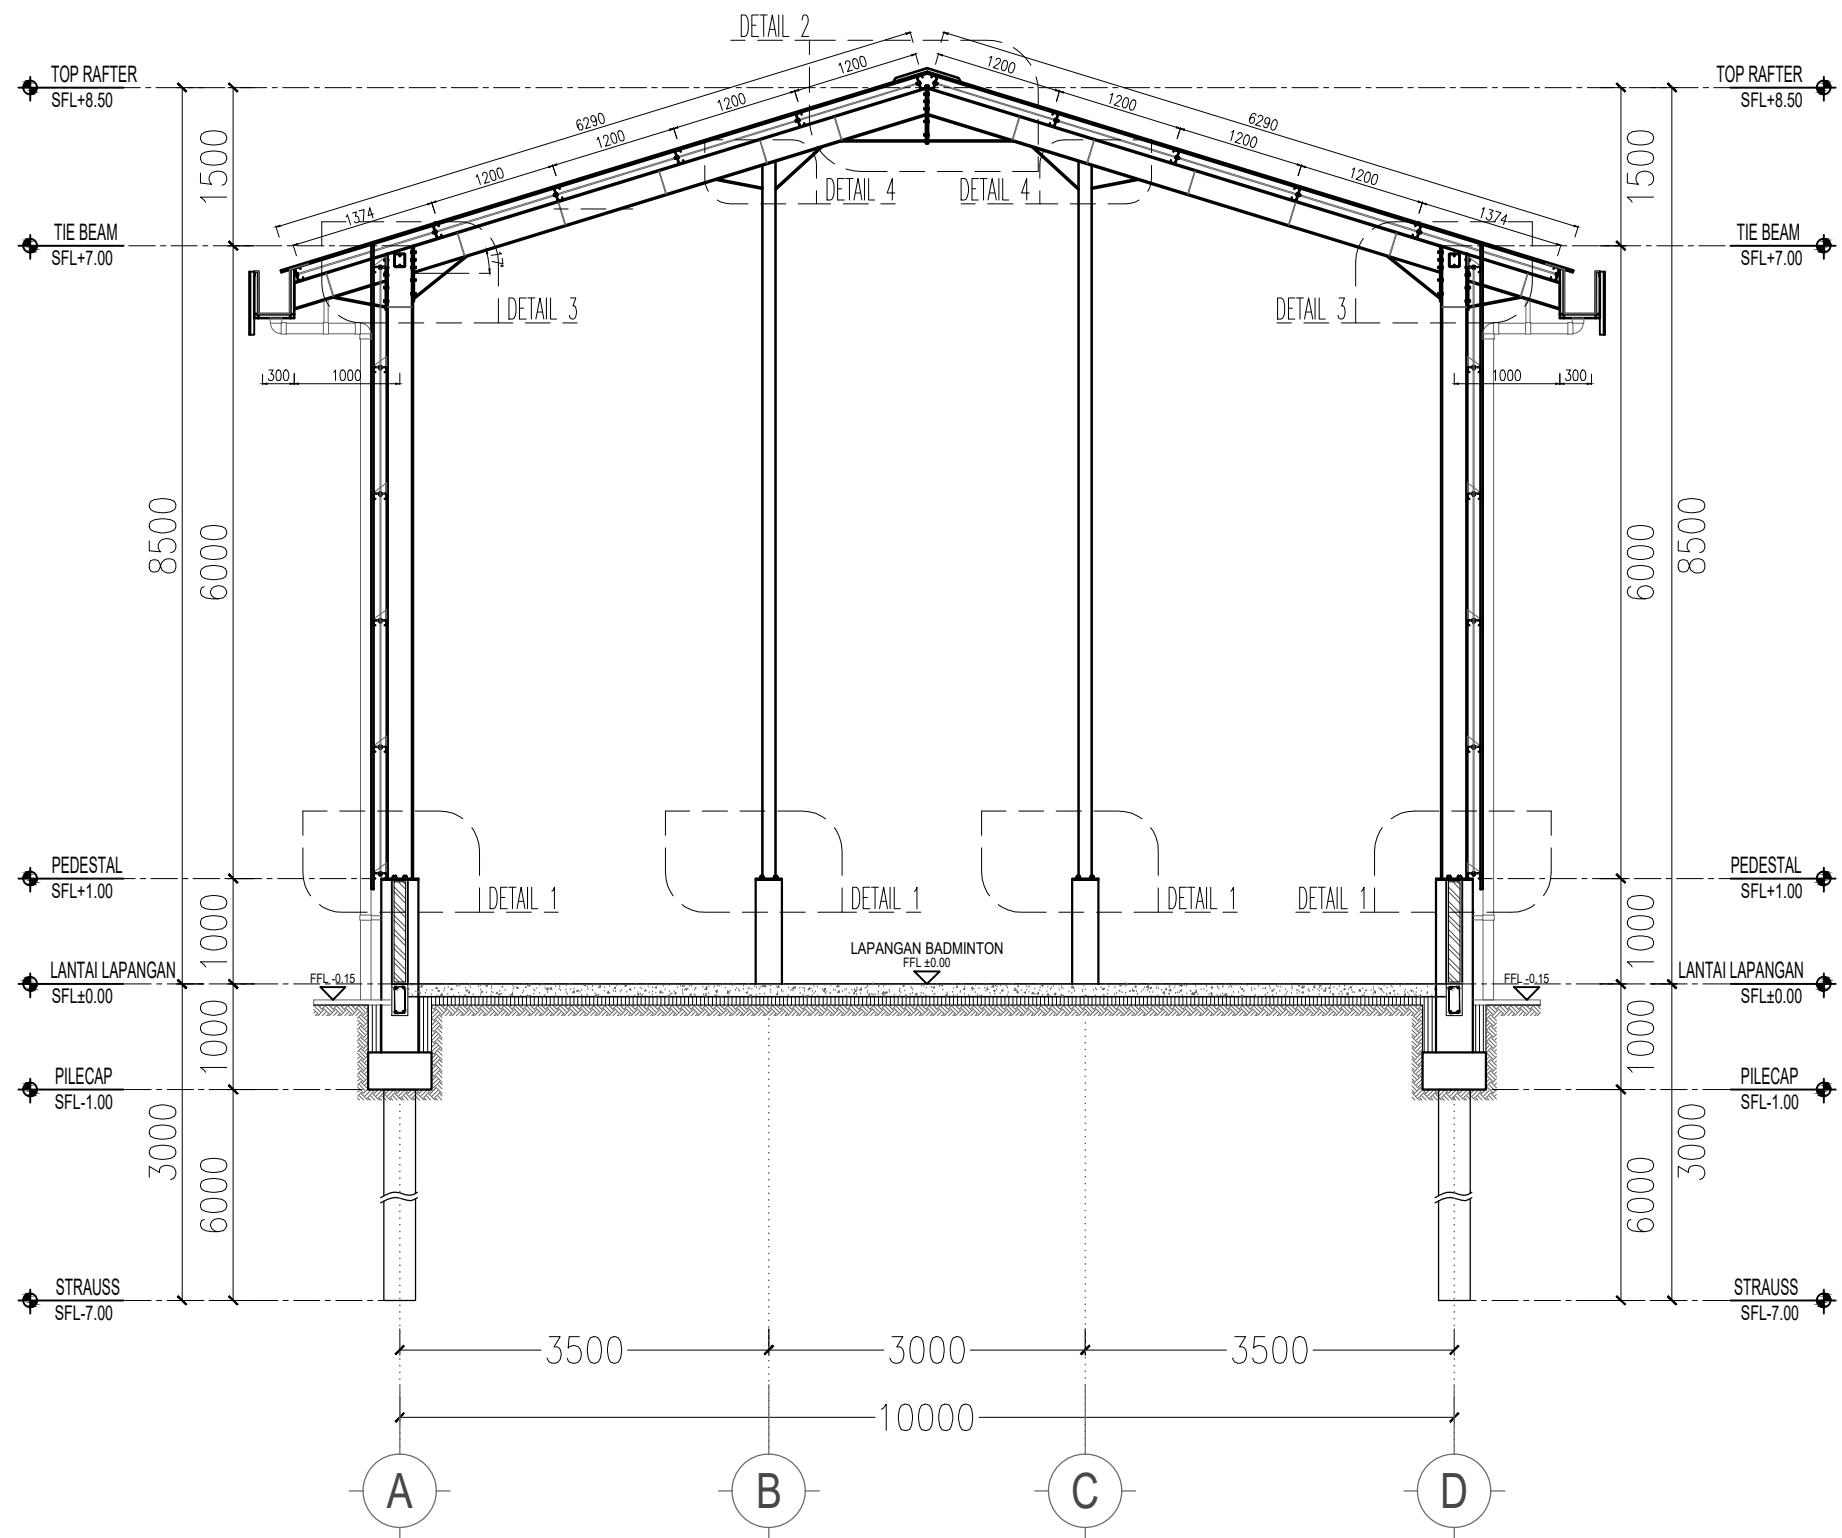

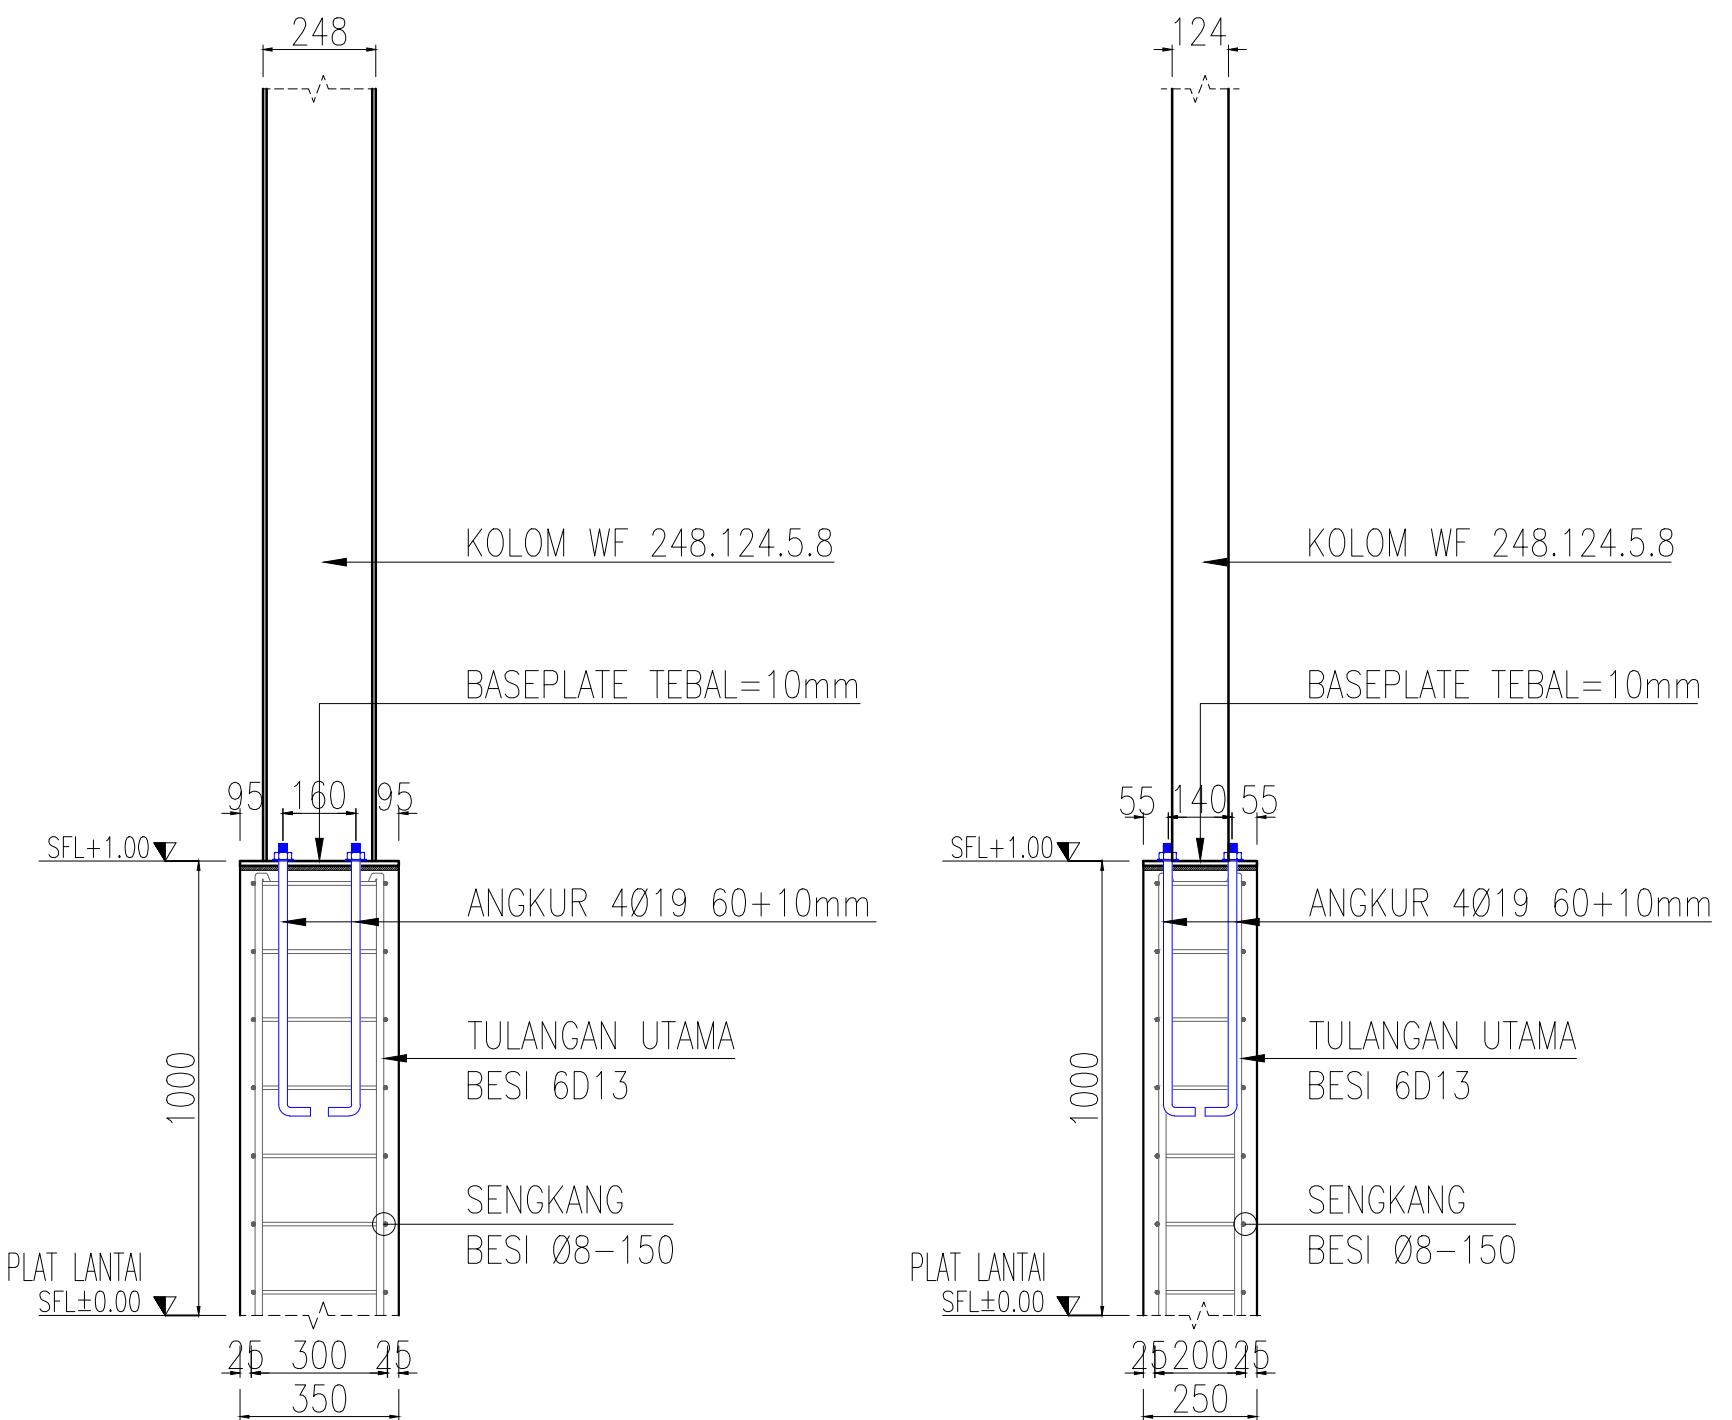

POTONGAN A-A

POTONGAN B-B

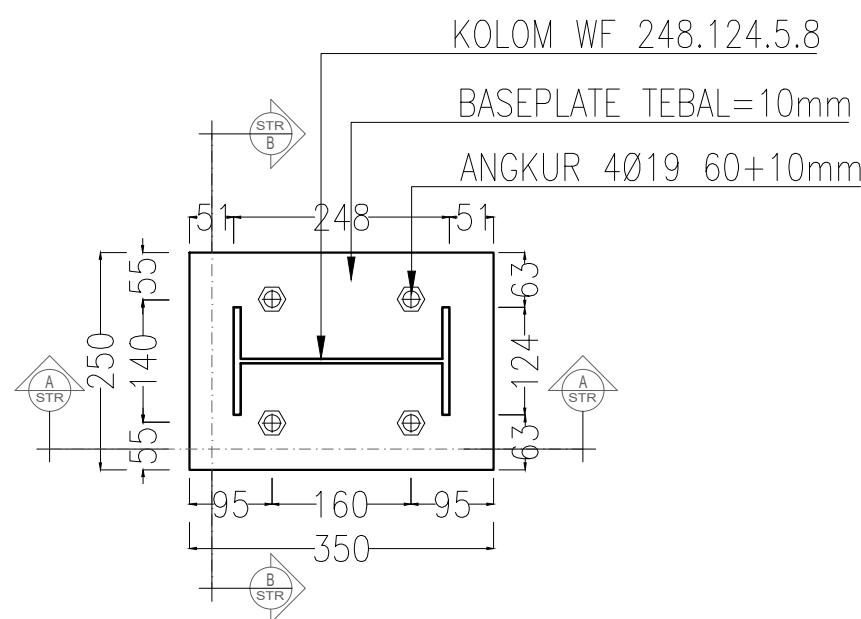

**DENAH BASEPLATE
KOLOM WF 248.124.5.8**

01
STR SKALA 1 : 25

1. PELAKSANA ATAU SUBKON WAJIB MEMERIKSA KEMBALI KESESUAIN GAMBAR DENGAN KONDISI LAPANGAN

NAMA PROYEK

LOKASI PROYEK

PENGANGGUNG JAWAB

DISETUJUJ

PELAKSANA

STR-03-22

TANGGAL : 5 APRIL 2024


REVISI : R3

JUDUL GAMBAR : 1.DETAIL 1 (BASEPLATE DAN ANGKUR)


SKALA : 1 : 25

NO. LBR : JUMLAH LBR


NAMA PROYEK	
LOKASI PROYEK	-
PENANGGUNG JAWAB	
DIGAMBAR	PELAKSANA
DISETUJUI	PEMILIK

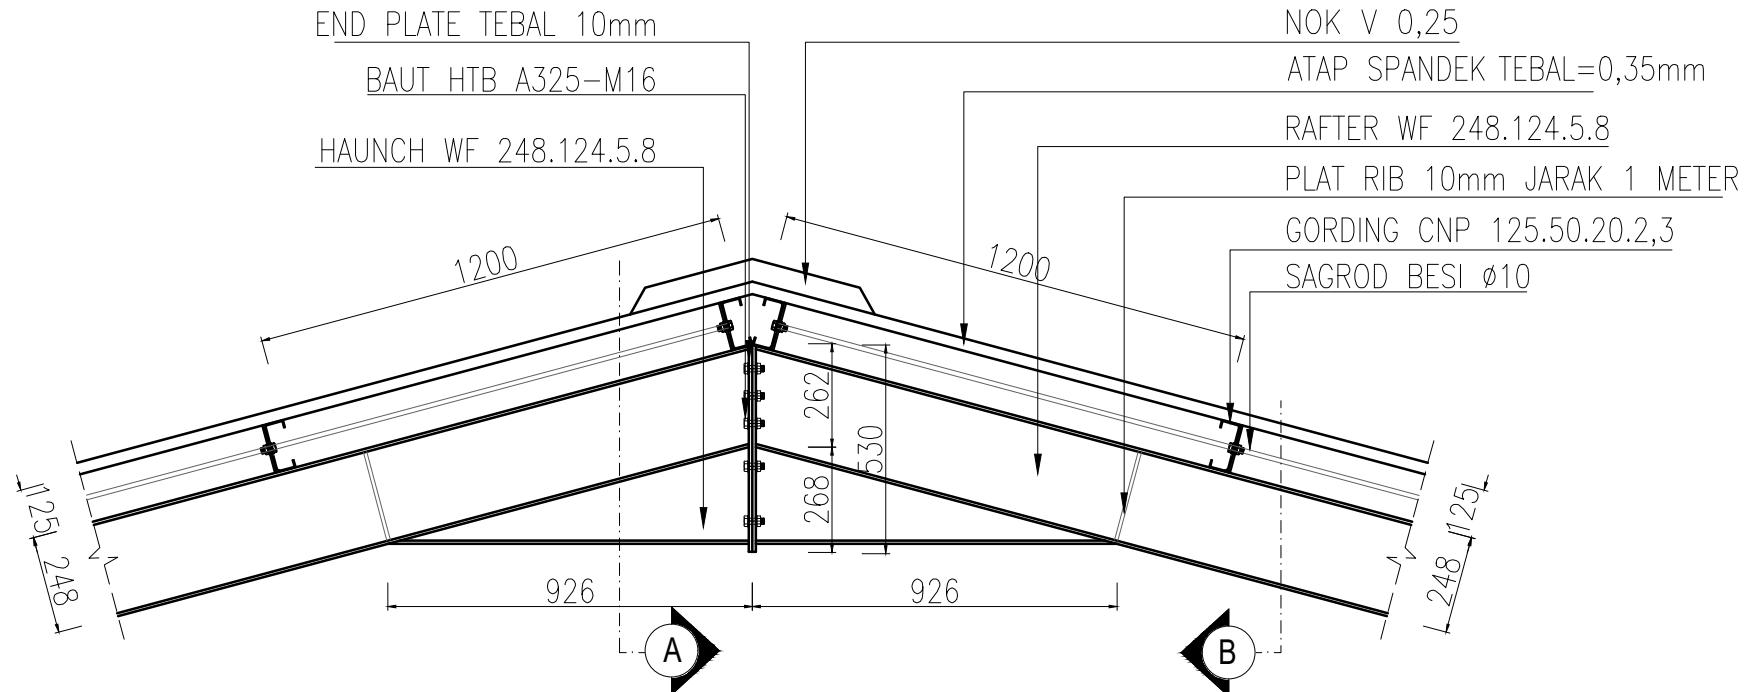


01
STR SKALA 1 : 10
DETAIL 2 (SAMBUNGAN RAFTER)

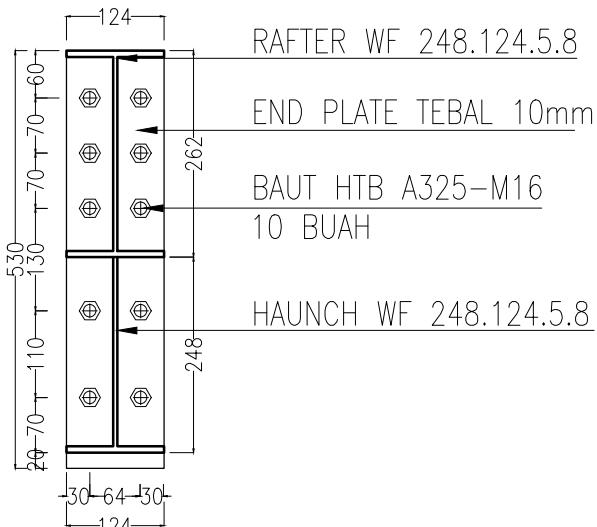

01
STR SKALA 1 : 5
POTONGAN A (END PLATE)

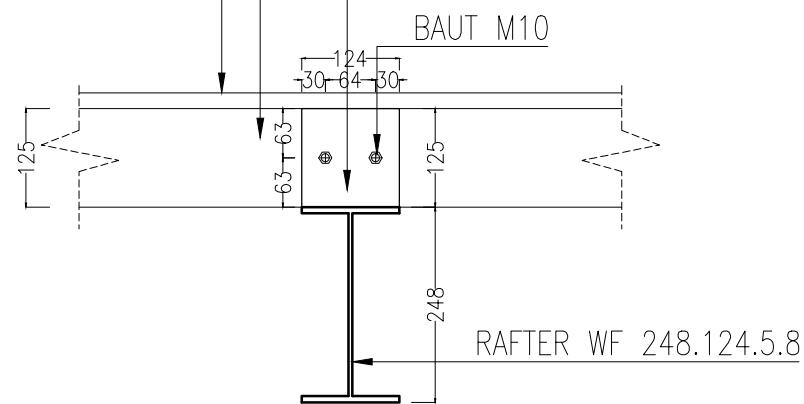

01
STR SKALA 1 : 5
POTONGAN B (PENYANGGA GORDING)

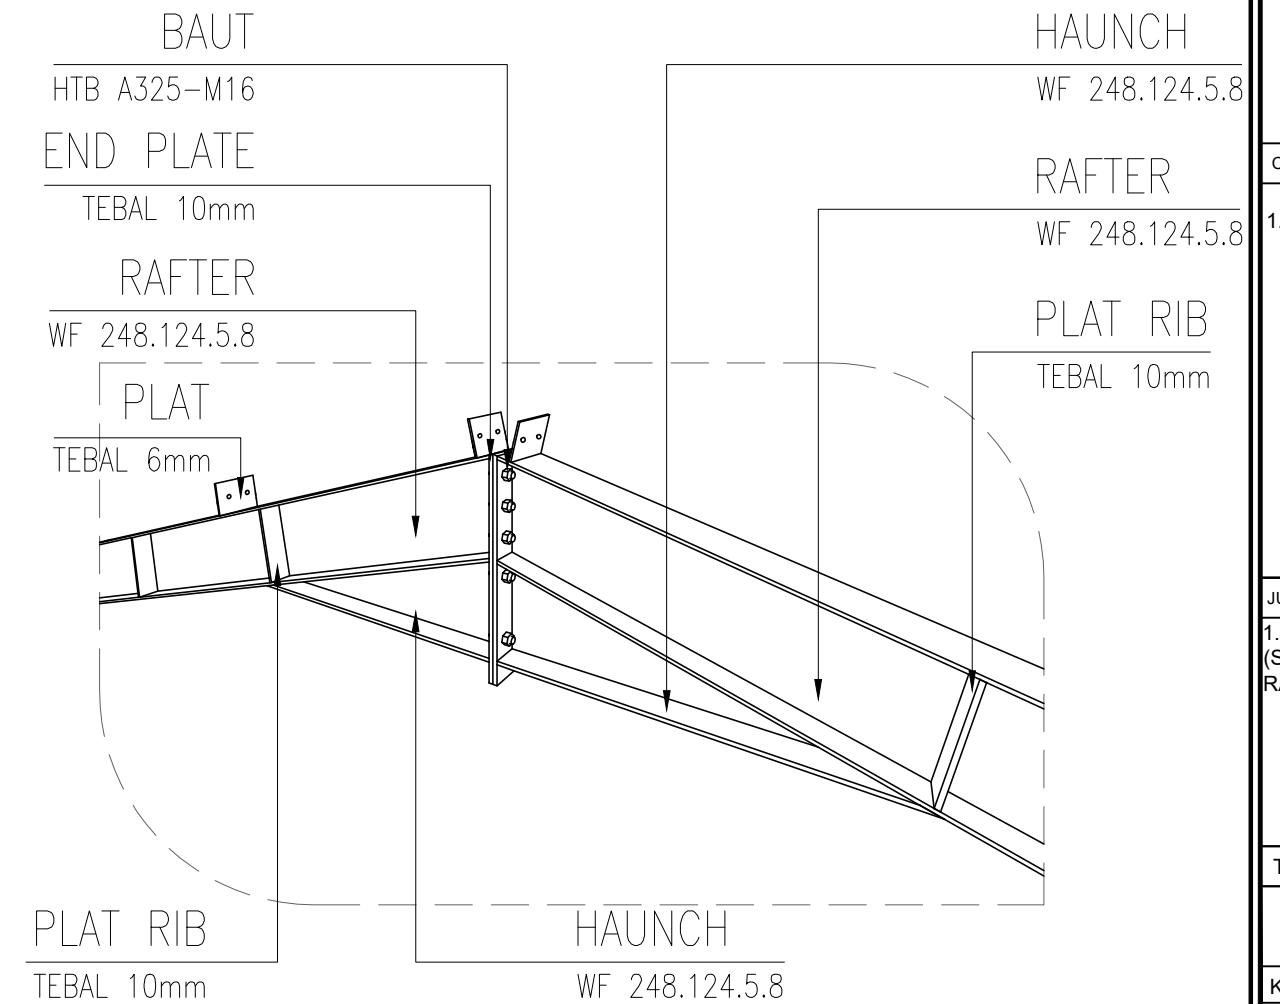

01
STR NTS
3D AKSONOMETRI 1 (SAMBUNGAN RAFTER)

CATATAN
1. PELAKSANA ATAU SUBKON WAJIB MEMERIKSA KEMBALI KESESUAIN GAMBAR DENGAN KONDISI LAPANGAN

JUDUL GAMBAR SKALA
1.DETAIL 2 (SAMBUNGAN RAFTER) 1 : 10

TANGGAL : REVISI :

5 APRIL 2024 R3


KODE GAMBAR

STR-03-23


NO. LBR JUMLAH LBR

23 35


NAMA PROYEK	
LOKASI PROYEK	-
PENANGGUNG JAWAB	
DIGAMBAR	PELAKSANA
DISETUJUI	PEMILIK
CATATAN	<p>1. PELAKSANA ATAU SUBKON WAJIB MEMERIKSA KEMBALI KESESUAIN GAMBAR DENGAN KONDISI LAPANGAN</p>
JUDUL GAMBAR	SKALA
1.DETAIL 3 (SAMBUNGAN RAFTER DGN KOLOM)	1 : 10
TANGGAL :	REVISI :
5 APRIL 2024	R3
KODE GAMBAR	
STR-03-24	
NO. LBR	JUMLAH LBR
24	35

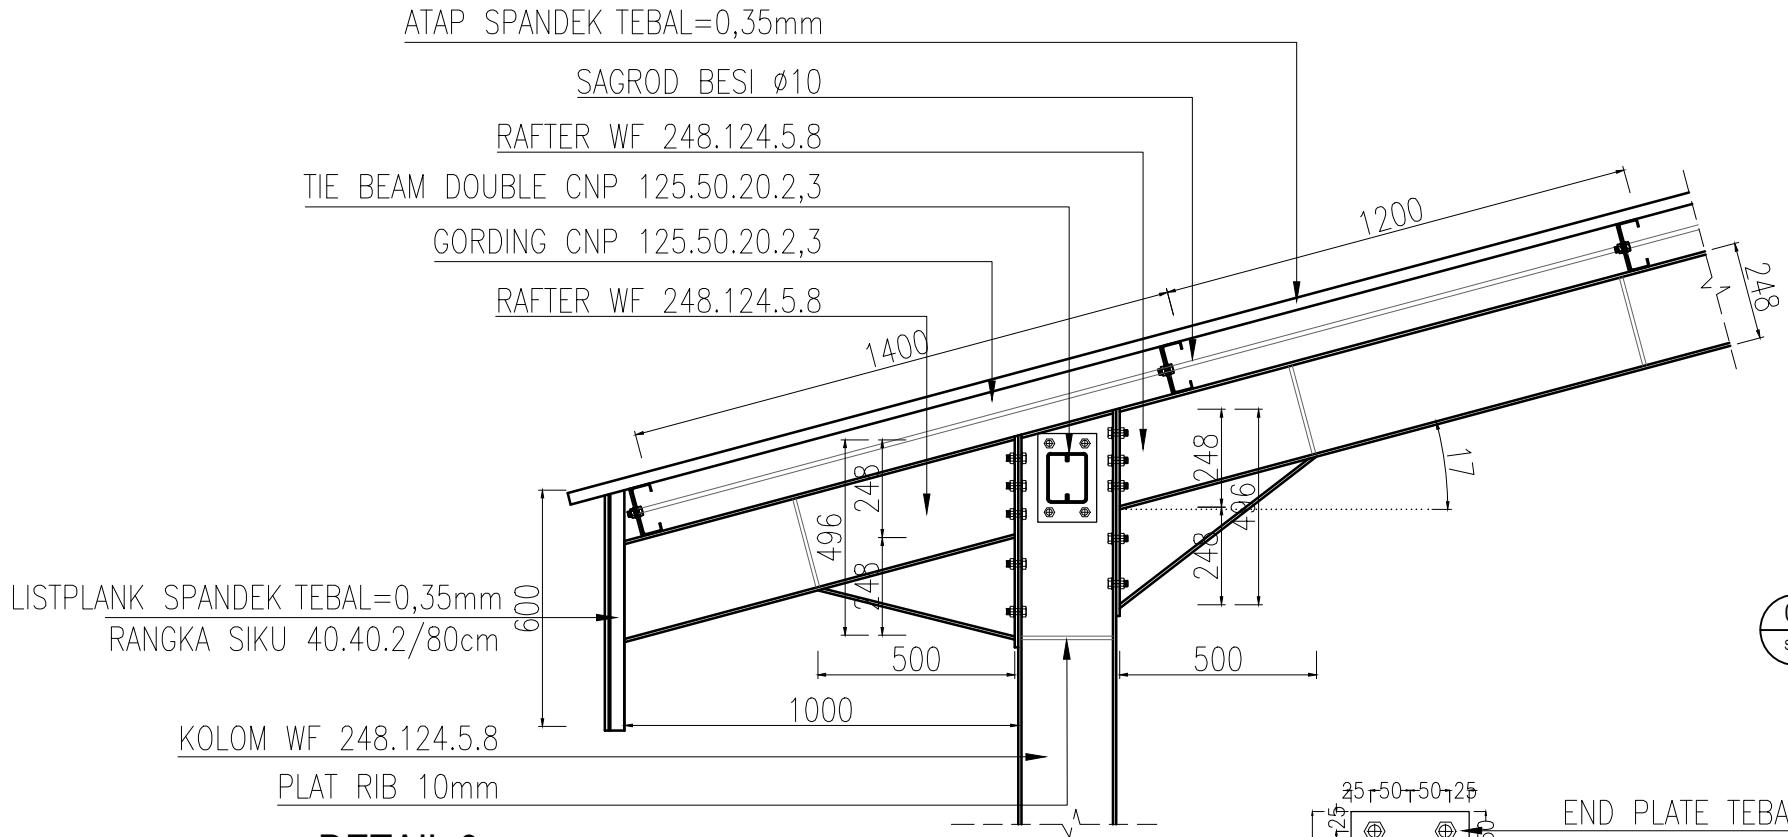


DETAIL 3
(SAMBUNGAN RAFTER DGN KOLOM)

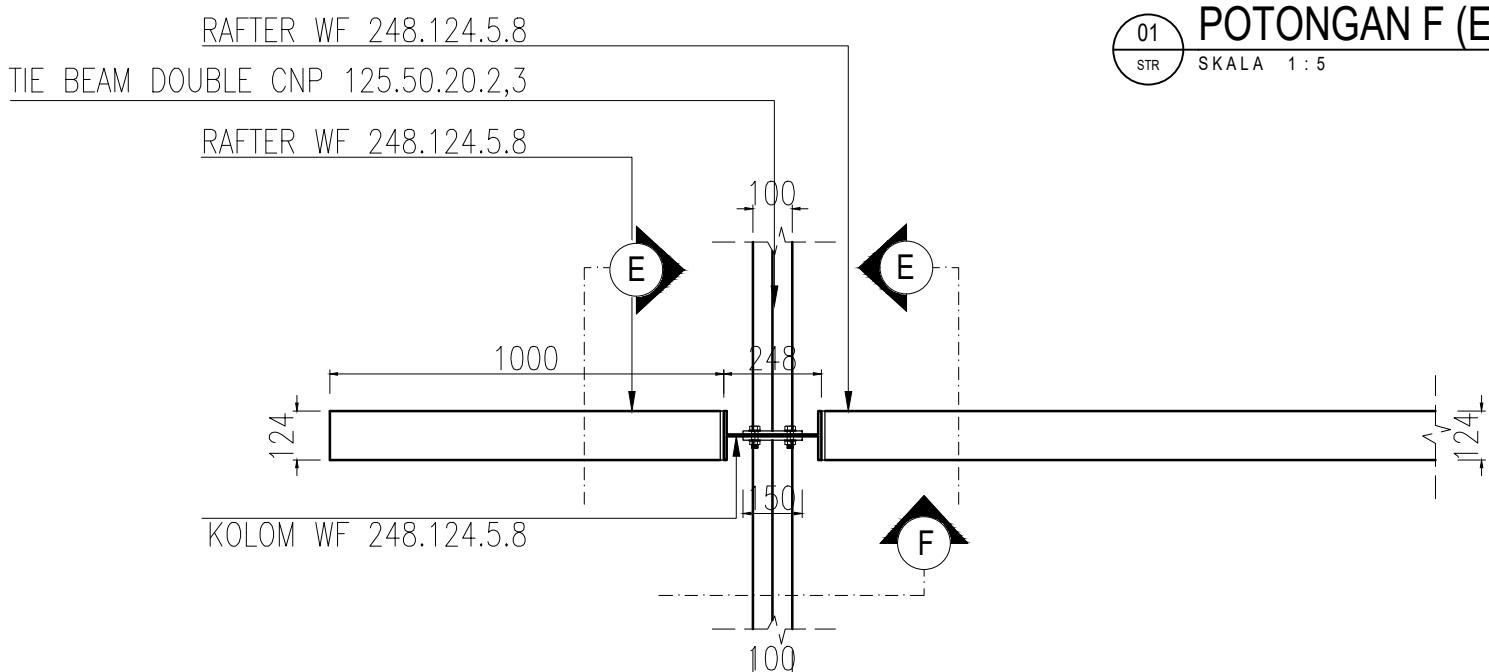


DETAIL DENAH 3
(SAMBUNGAN RAFTER DGN KOLOM)

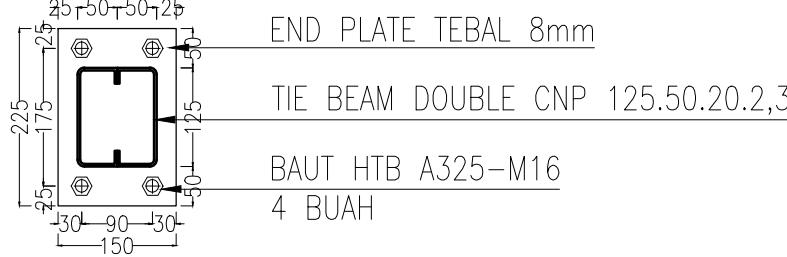

01
STR SKALA 1 : 5
POTONGAN E (END PLATE)

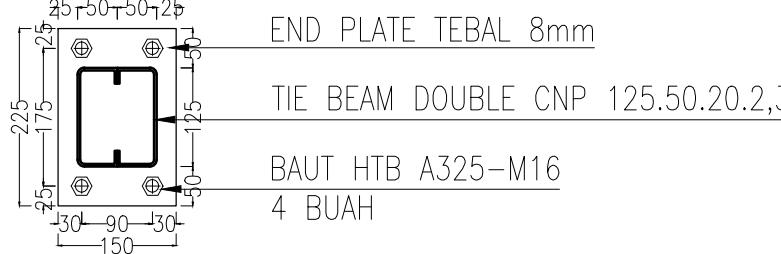

01
STR SKALA 1 : 5
POTONGAN F (END PLATE)

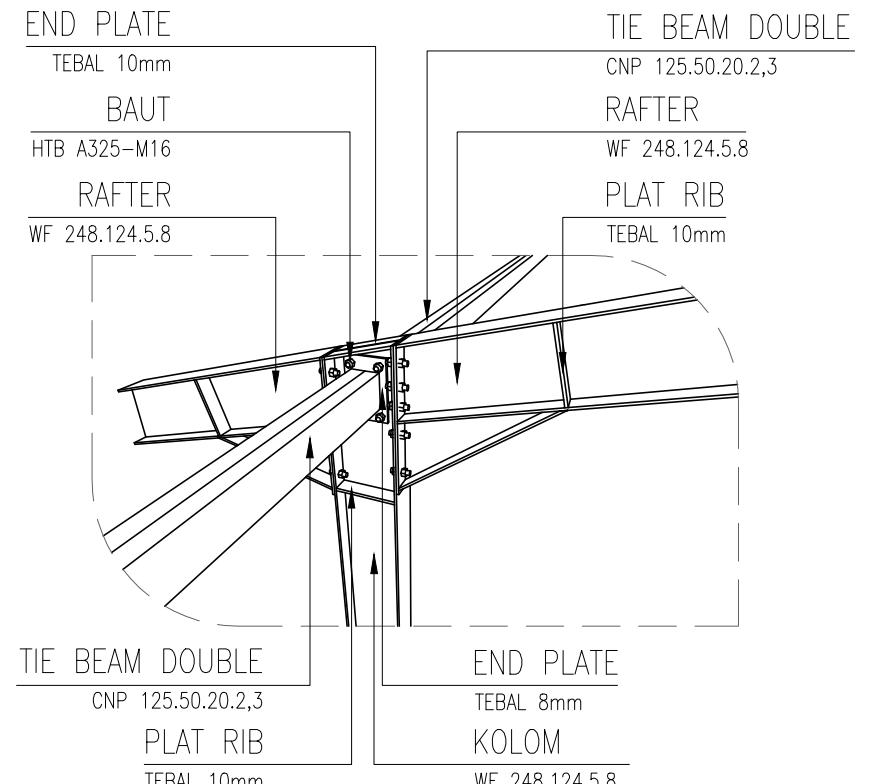

01
STR NTS
3D AKSONOMETRI 3
(SAMBUNGAN RAFTER DGN KOLOM)

ATAP SPANDEK TEBAL=0,35mm

SAGROD BESI ø10


HAUNCH WF 248.124.5.8

RFTER WF 248.124.5.8

HAUNCH WF 248.124.5.8

PLAT RIB 10mm

GORDING CNP 125.50.20.2,3

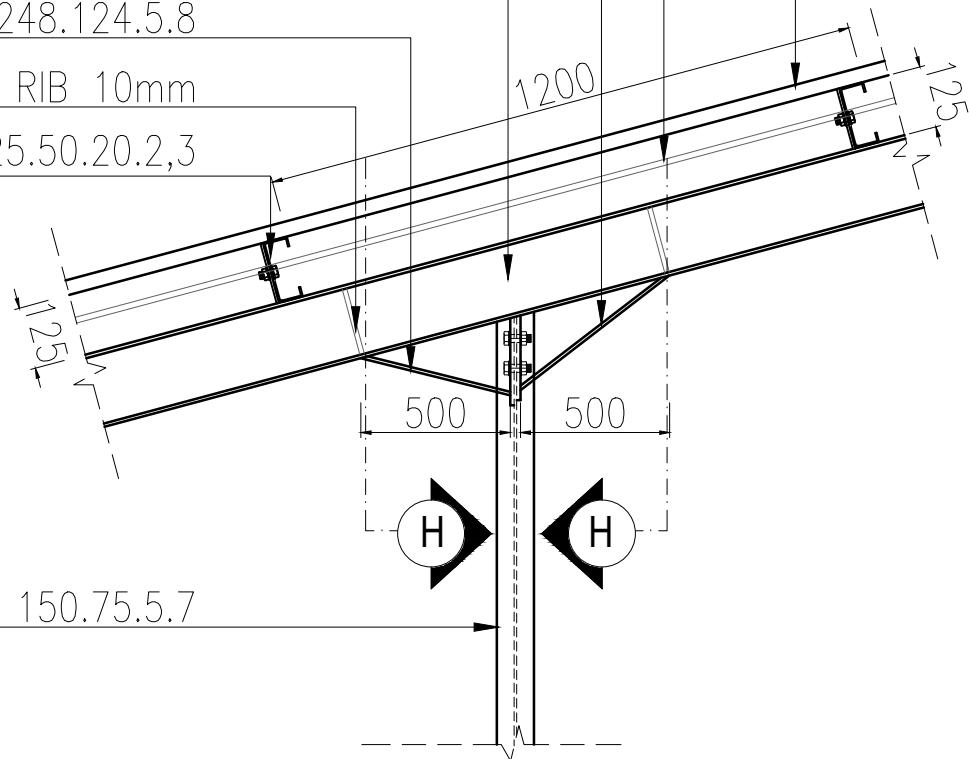


KOLOM WF 150.75.5.7

DETAIL 4 (SAMBUNGAN RFTER DGN KOLOM)

01
STR


SKALA 1 : 10

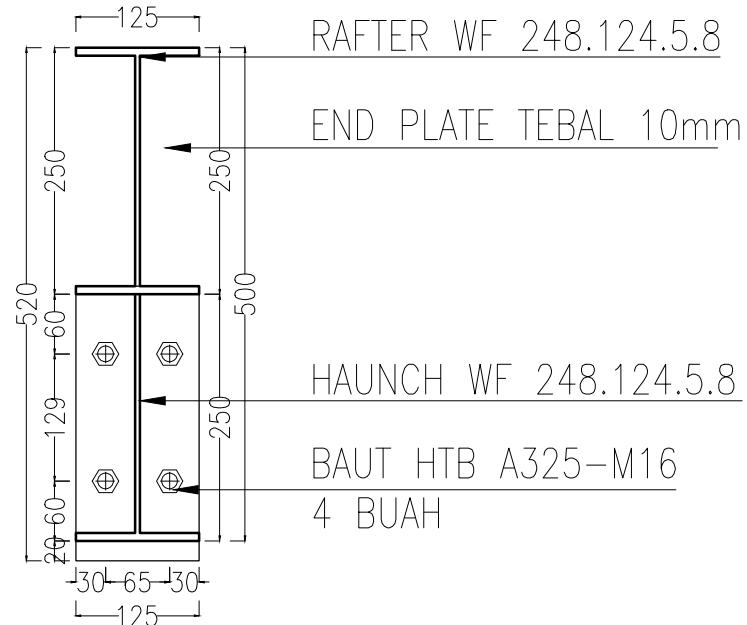

01
STR

POTONGAN H (END PLATE)

SKALA 1 : 5

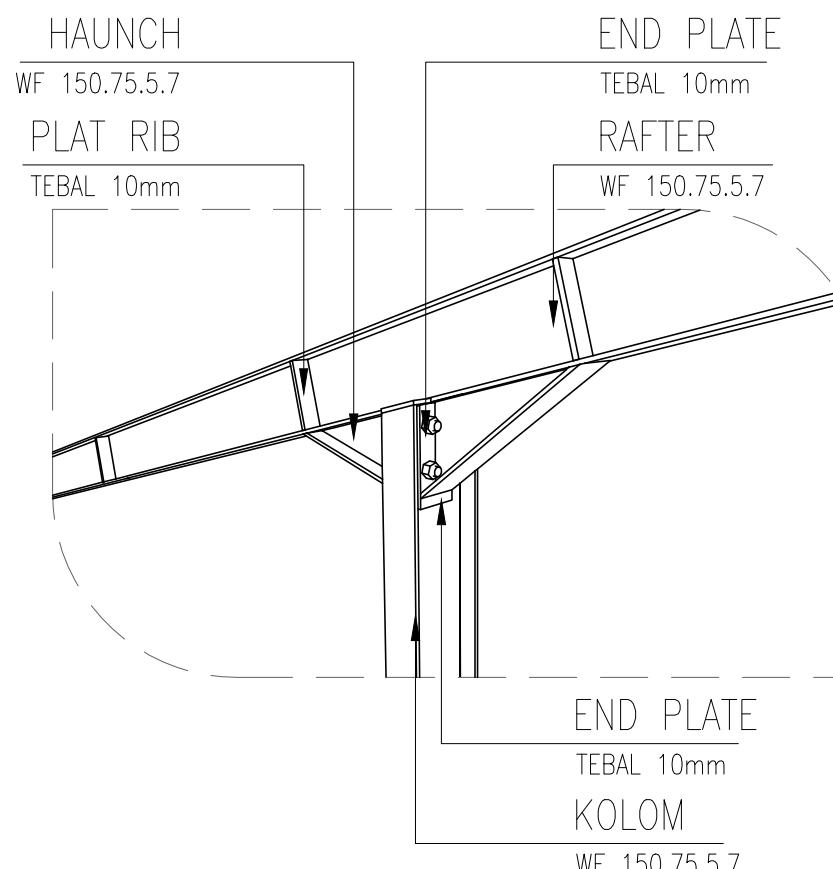


01
STR

NTS

3D AKSONOMETRI 5
(SAMBUNGAN RFTER DGN KOLOM)


NAMA PROYEK	
-	
LOKASI PROYEK	
-	-
PENANGGUNG JAWAB	
DIGAMBAR	PELAKSANA
DISETUJUI	PEMIKIR
CATATAN	
1. PELAKSANA ATAU SUBKON WAJIB MEMERIKSA KEMBALI KESESUAIN GAMBAR DENGAN KONDISI LAPANGAN	
JUDUL GAMBAR	SKALA
1.DETAIL 5 (SAMBUNGAN RFTER DGN KOLOM)	1 : 10
TANGGAL :	REVISI :
5 APRIL 2024	R3
KODE GAMBAR	
STR-03-25	
NO. LBR	JUMLAH LBR
25	35

NAMA PROYEK	
-	
LOKASI PROYEK	
-	-
PENANGGUNG JAWAB	
DIGAMBAR	PELAKSANA
-	-
DISETUJUI	PEMILIK
-	-
CATATAN	
1. PELAKSANA ATAU SUBKON WAJIB MEMERIKSA KEMBALI KESESUAIN GAMBAR DENGAN KONDISI LAPANGAN	
JUDUL GAMBAR	SKALA
1.PEMASANGAN SAGROD GORDING	1 : 10
TANGGAL :	REVISI :
5 APRIL 2024	R3
KODE GAMBAR	
STR-03-26	
NO. LBR	JUMLAH LBR
26	35

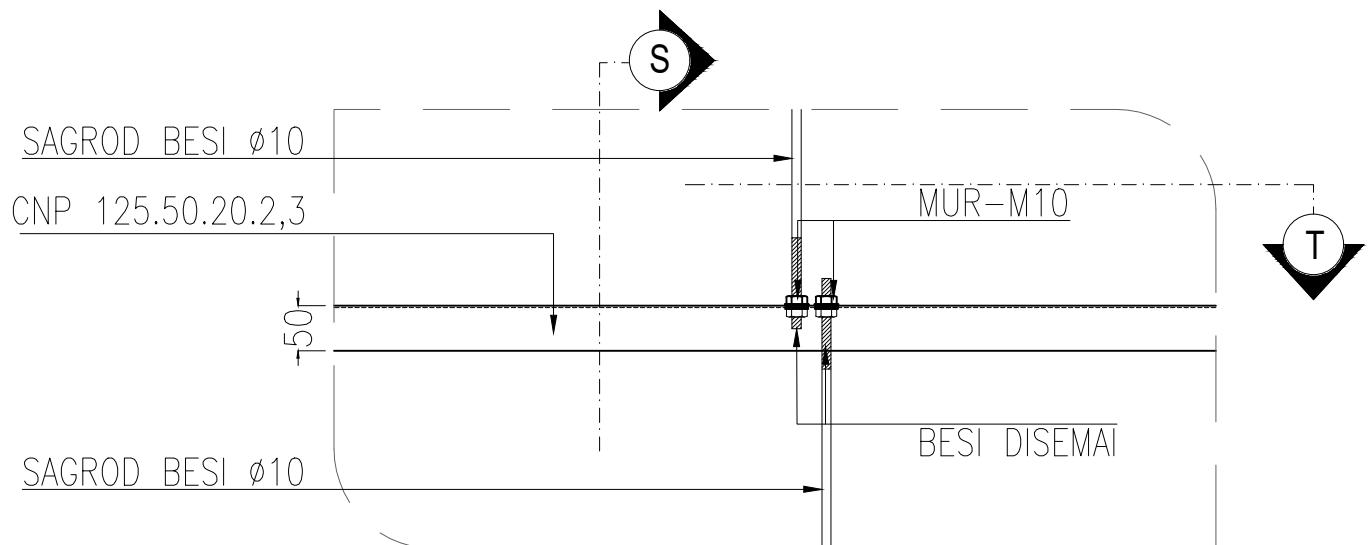


**DETAIL DENAH
(PEMASANGAN SAGROD GORDING)**

01
STR
NTS

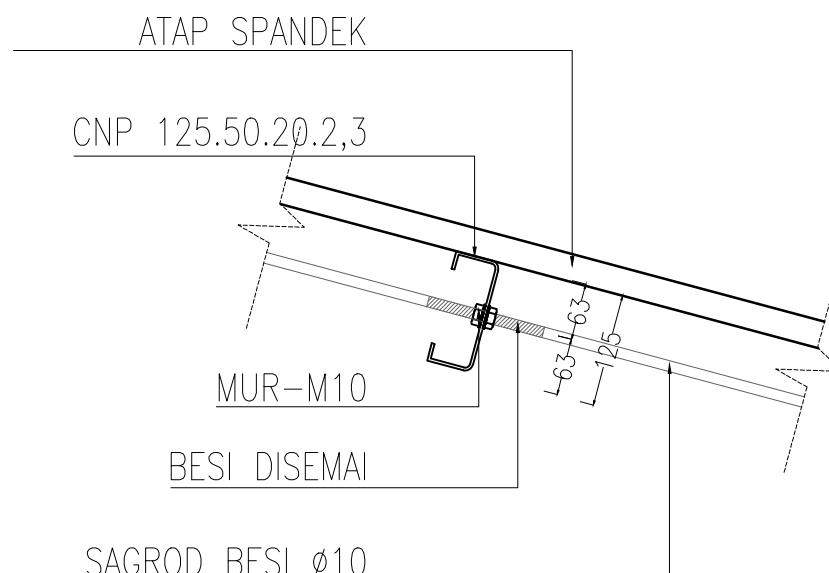


SAGROD BESI ø10

01
STR
SKALA 1 : 5

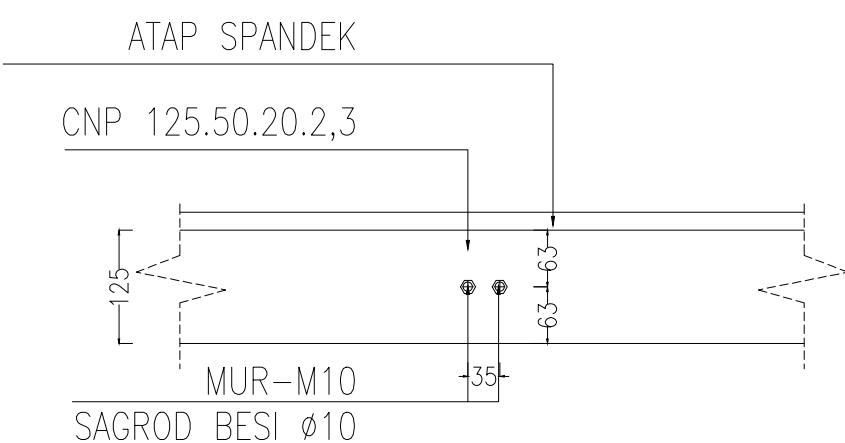


01
STR
SKALA 1 : 5

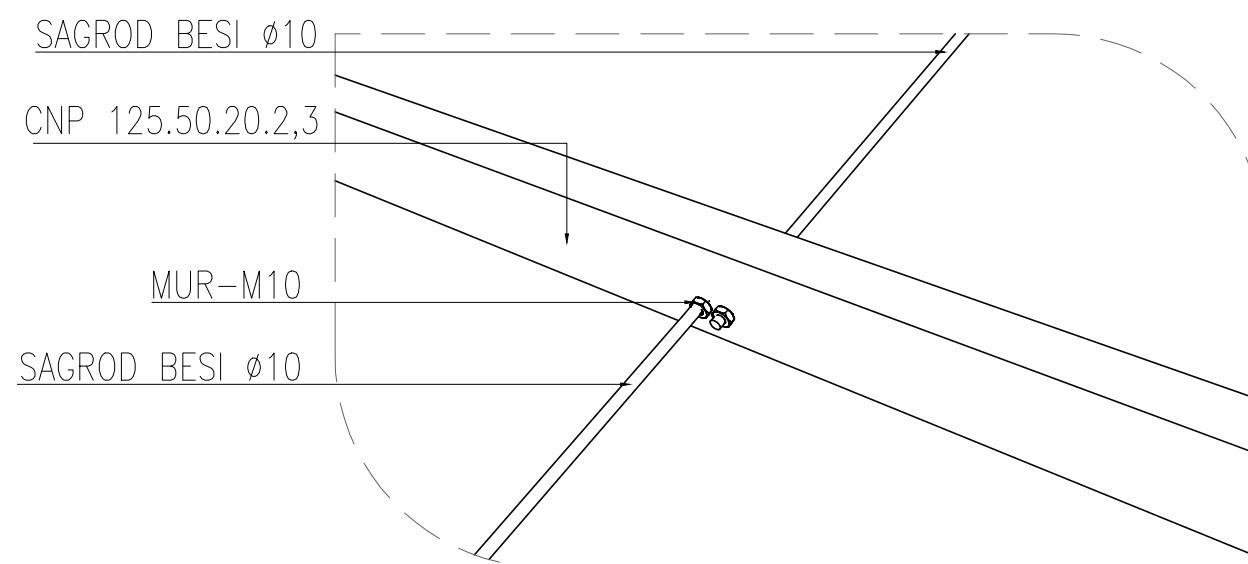

**3D AKSONOMETRI
(PEMASANGAN SAGROD GORDING)**

01
STR
NTS

NAMA PROYEK	
-	
LOKASI PROYEK	
-	-
PENANGGUNG JAWAB	
DIGAMBAR	PELAKSANA
-	-
DISETUJUI	PEMILIK
-	-
CATATAN	
1. PELAKSANA ATAU SUBKON WAJIB MEMERIKSA KEMBALI KESESUAIN GAMBAR DENGAN KONDISI LAPANGAN	
-	
JUDUL GAMBAR	SKALA
1.DETAIL TALANG	1 : 10
TANGGAL :	REVISI :
5 APRIL 2024	R3
KODE GAMBAR	
STR-03-27	
NO. LBR	JUMLAH LBR
27	35

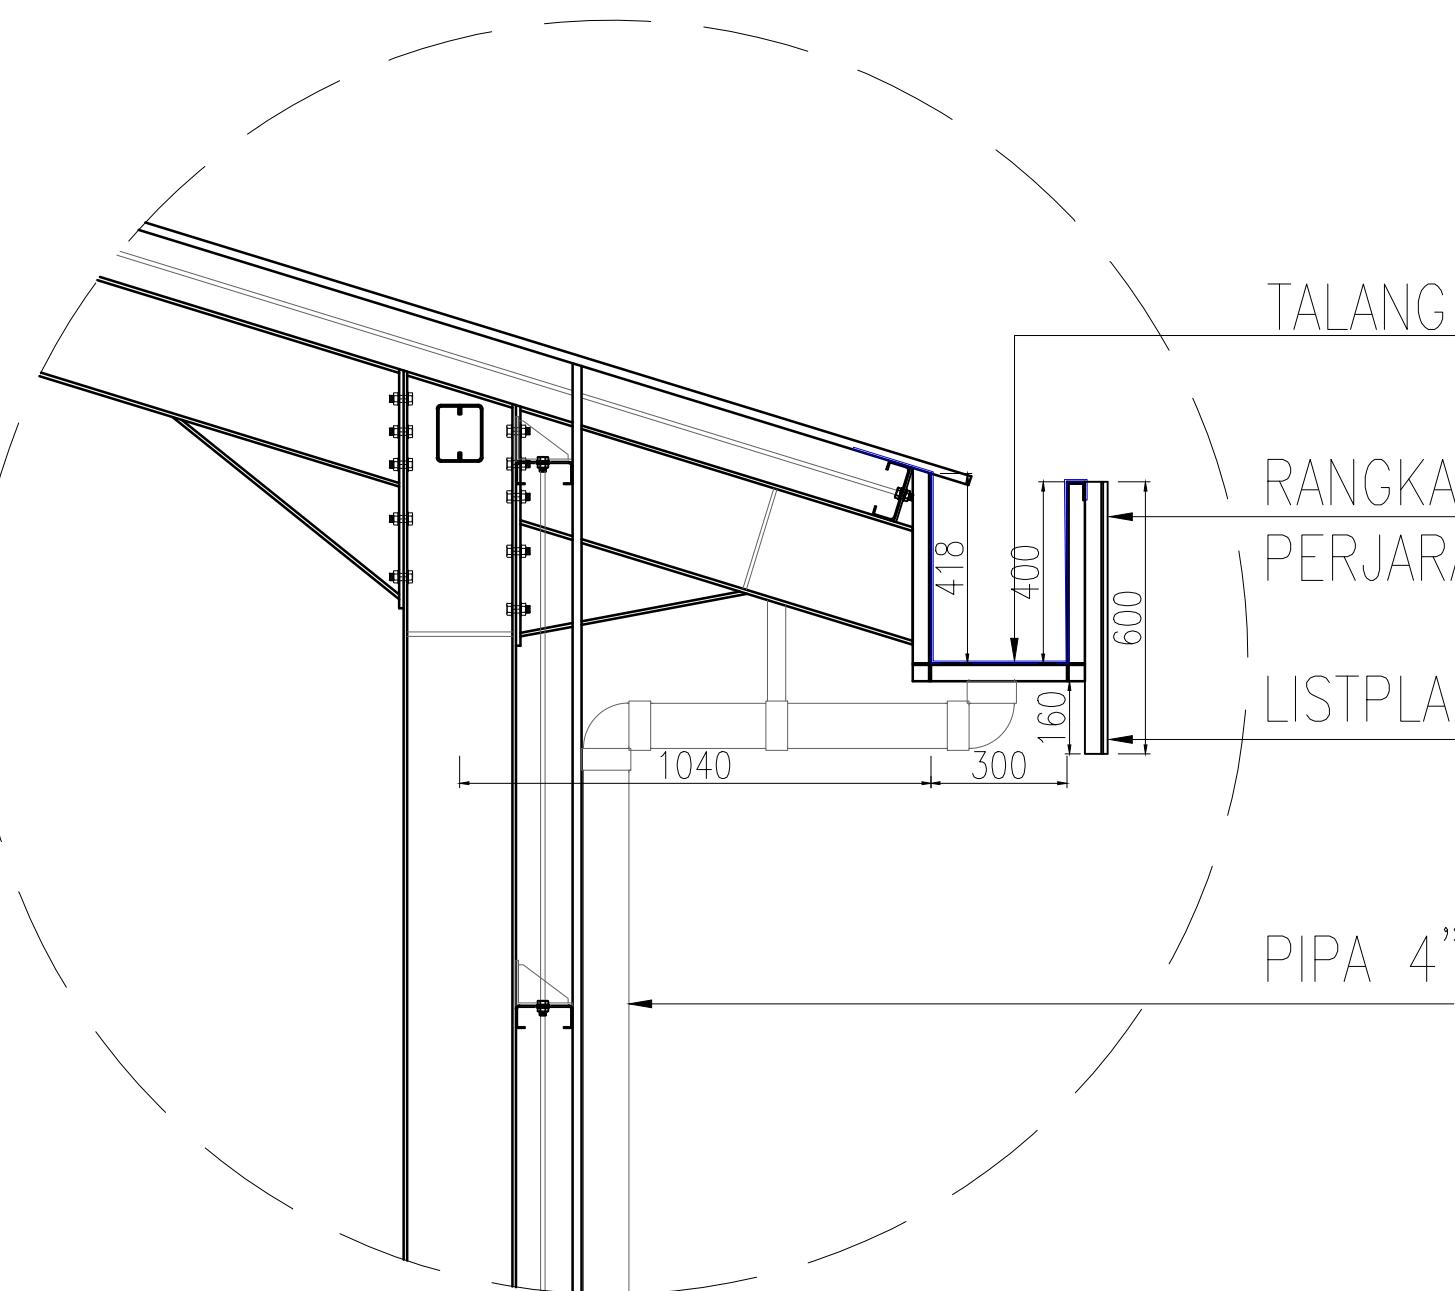


DETAIL TALANG

SKALA 1:10



01
STR

KEY PLAN TALANG

NTS

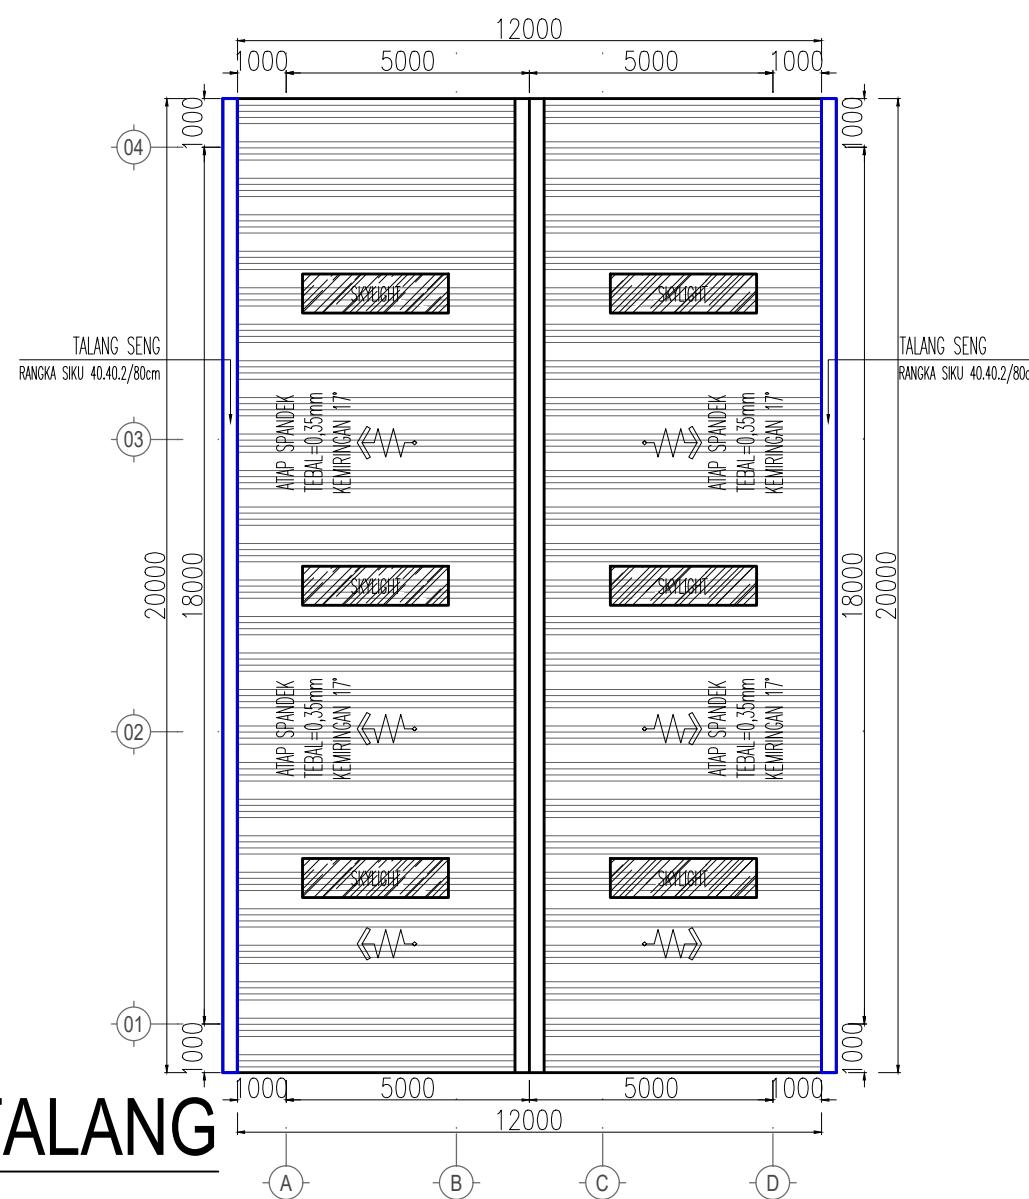

A B C D

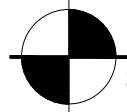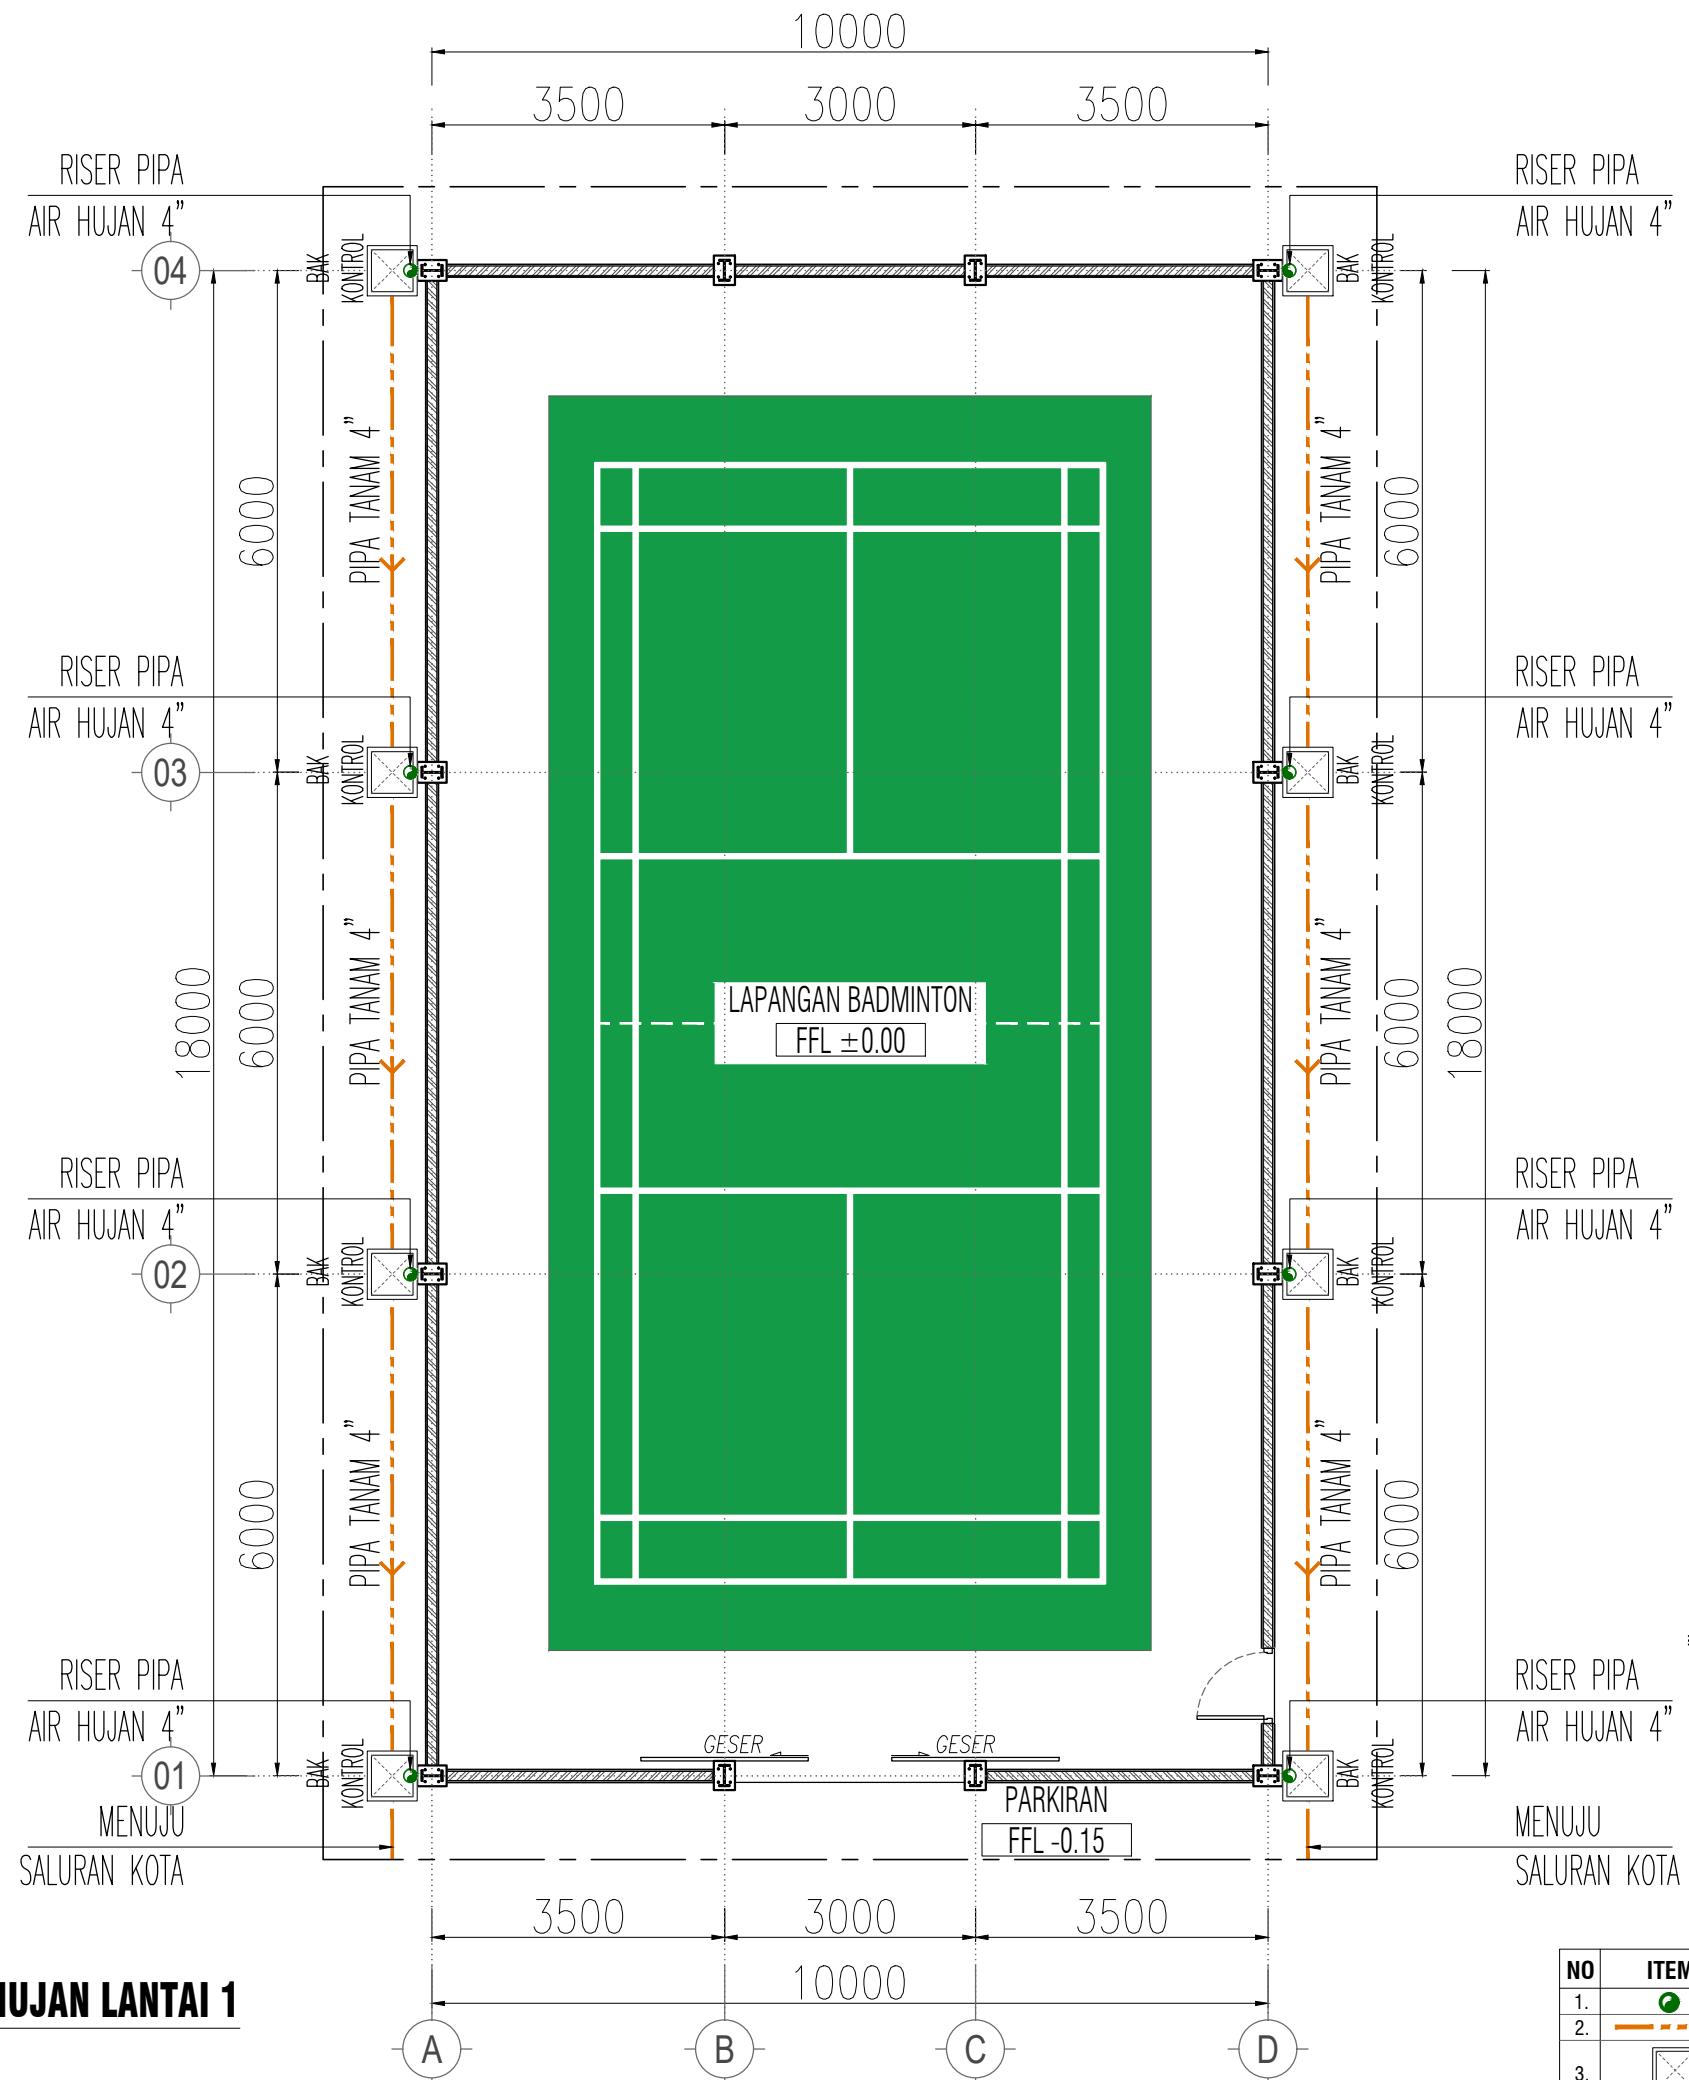


DENAH KOTOR DAN AIR HUJAN LANTAI 1


SKALA 1 : 100

NO	ITEM	KETERANGAN
1.		RISER PIPA AIR AIR HUJAN 4"
2.		PIPA AIR HUJAN 4"
3.		BAK KONTROL

NAMA PROYEK	
LOKASI PROYEK	
PENANGGUNG JAWAB	
DIGAMBAR	PELAKSANA
DISETUJUI	PEMILIK
CATATAN	
<p>1. PELAKSANA ATAU SUBKON WAJIB MEMERIKSA KEMBALI KESESUAIN GAMBAR DENGAN KONDISI LAPANGAN</p>	
JUDUL GAMBAR	SKALA
1.DENAH KOTOR DAN AIR HUJAN LANTAI 1	1 : 100
TANGGAL :	REVISI :
5 APRIL 2024	R3
KODE GAMBAR	
PL-04-28	
NO. LBR	JUMLAH LBR
28	35

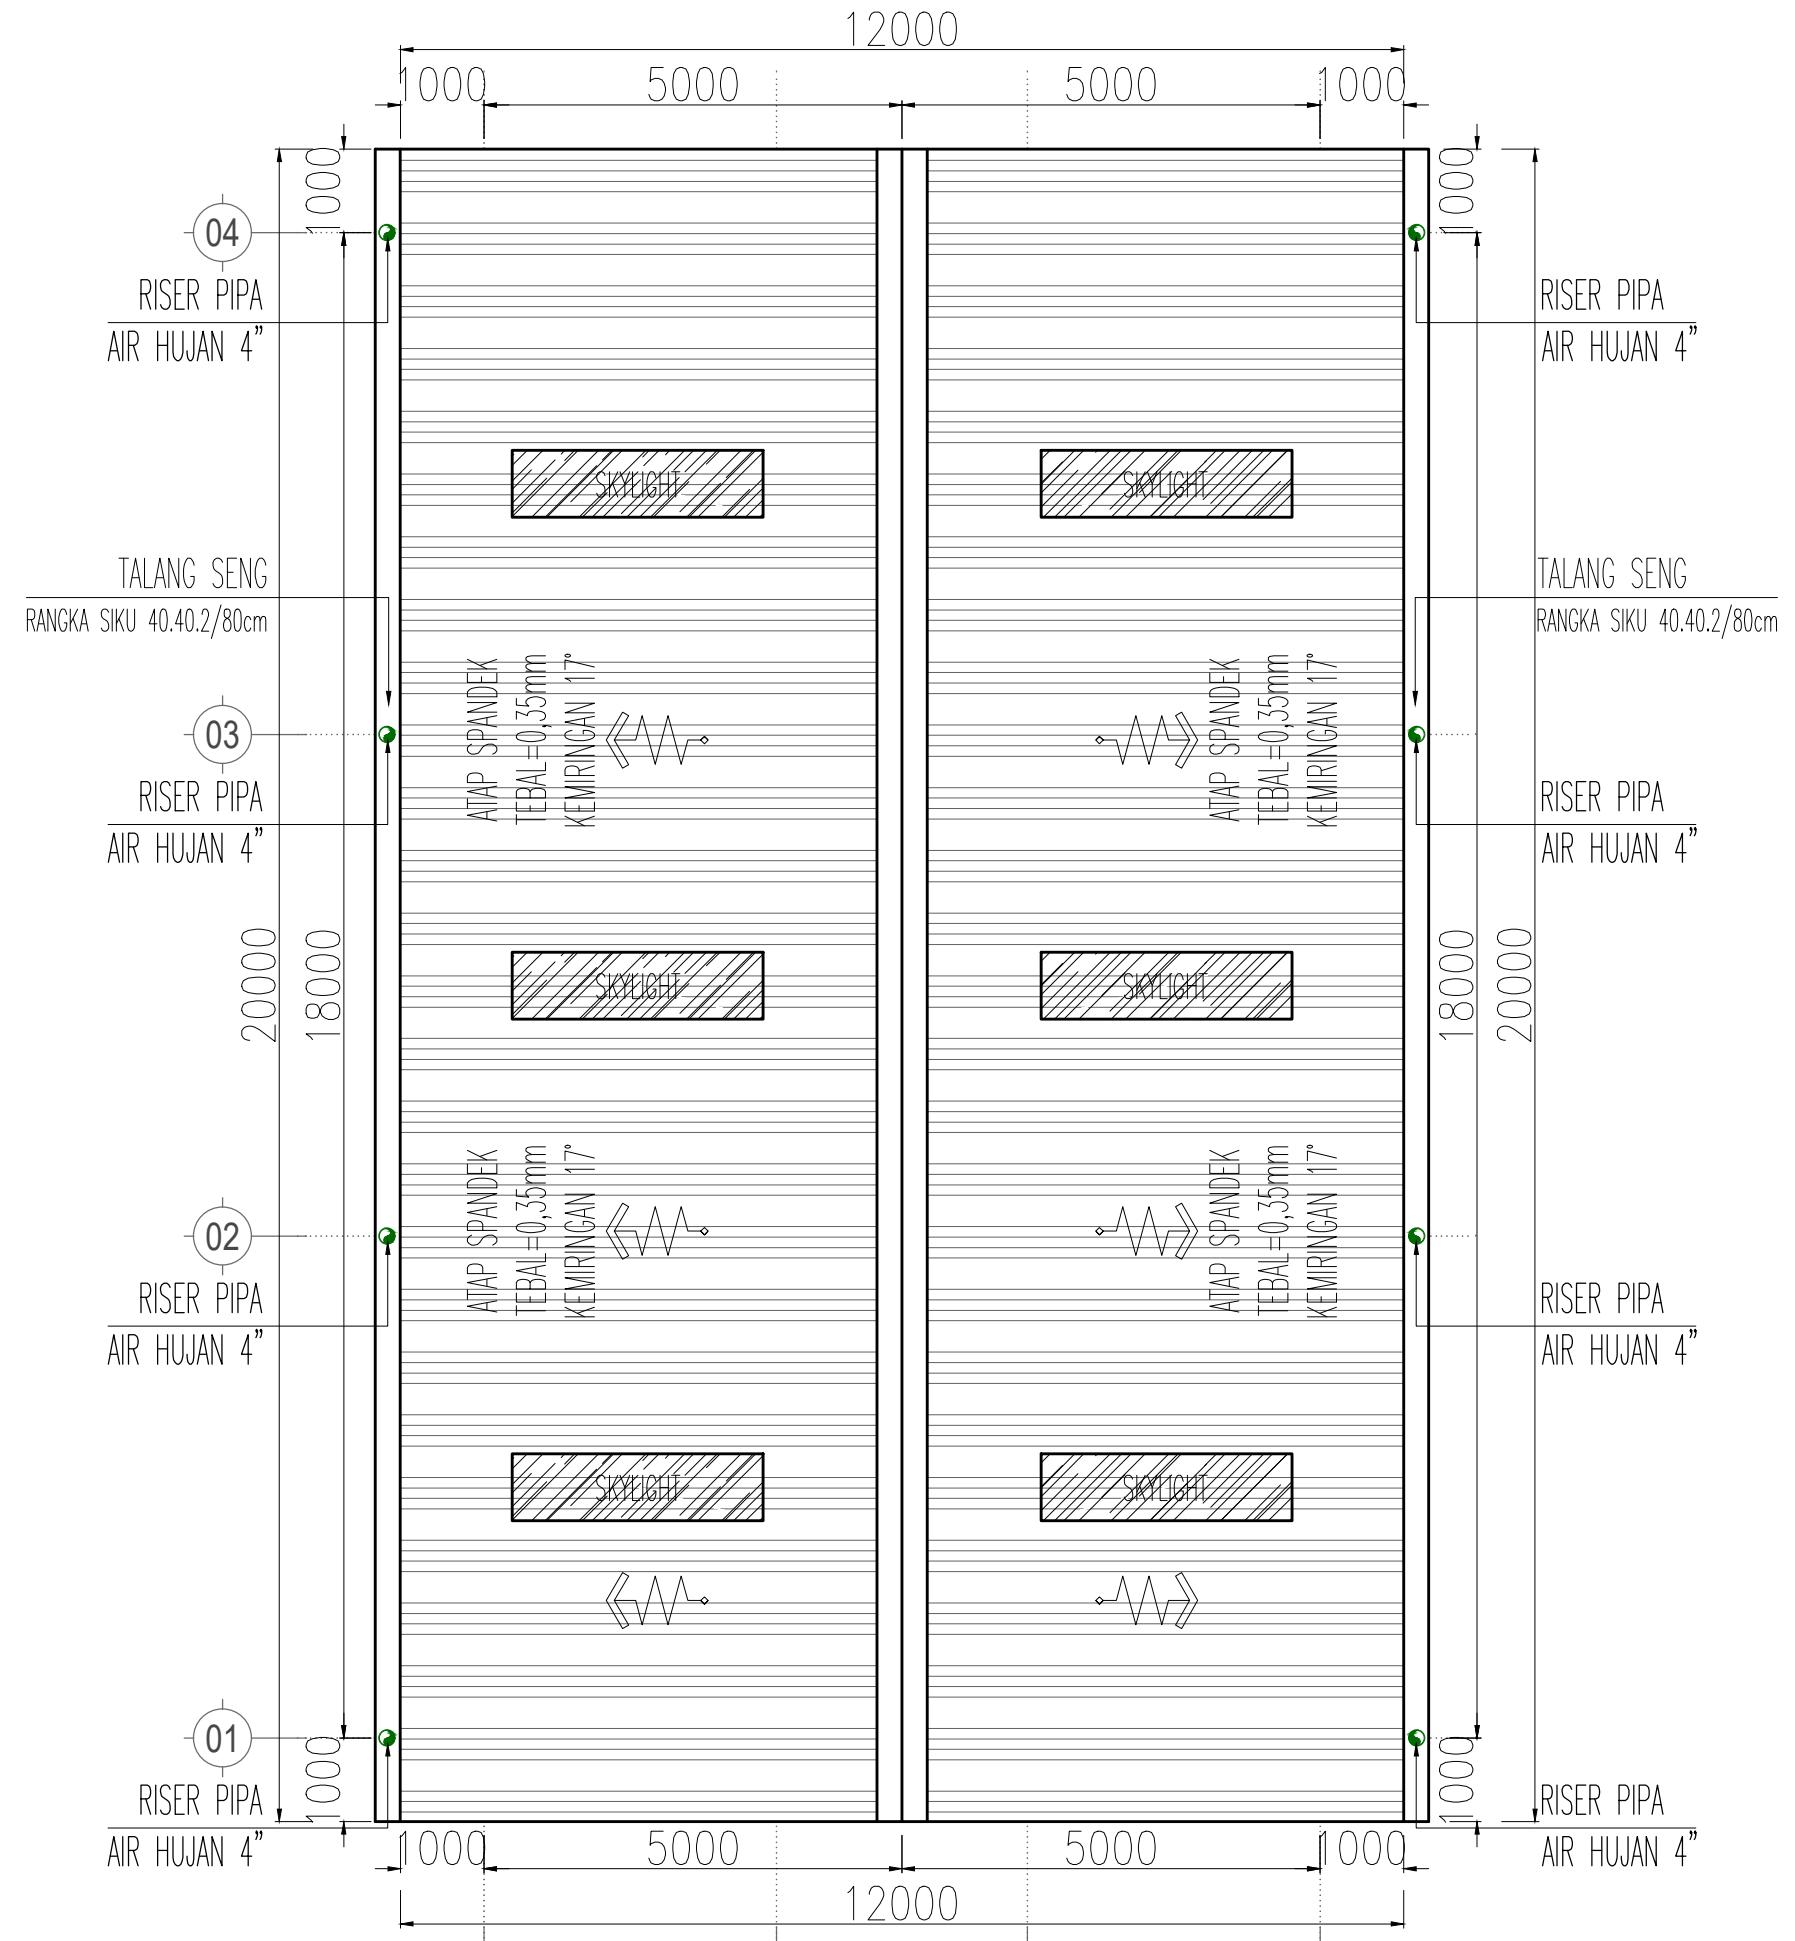


NO	ITEM	KETERANGAN
1.		RISER PIPA AIR AIR HUJAN 4"
2.		PIPA AIR HUJAN 4"
3.		BAK KONTROL

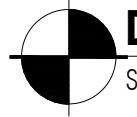

DENAH KOTOR DAN AIR HUJAN ATAP

SKALA 1 : 100


NAMA PROYEK	
LOKASI PROYEK	
PENANGGUNG JAWAB	
DIGAMBAR	PELAKSANA
DISETUJUI	PEMILIK
CATATAN	
<p>1. PELAKSANA ATAU SUBKON WAJIB MEMERIKSA KEMBALI KESESUAIN GAMBAR DENGAN KONDISI LAPANGAN</p>	
JUDUL GAMBAR	SKALA
1.DENAH KOTOR DAN AIR HUJAN ATAP	1 : 100
TANGGAL :	REVISI :
5 APRIL 2024	R3
KODE GAMBAR	
PL-04-29	
NO. LBR	JUMLAH LBR
29	35

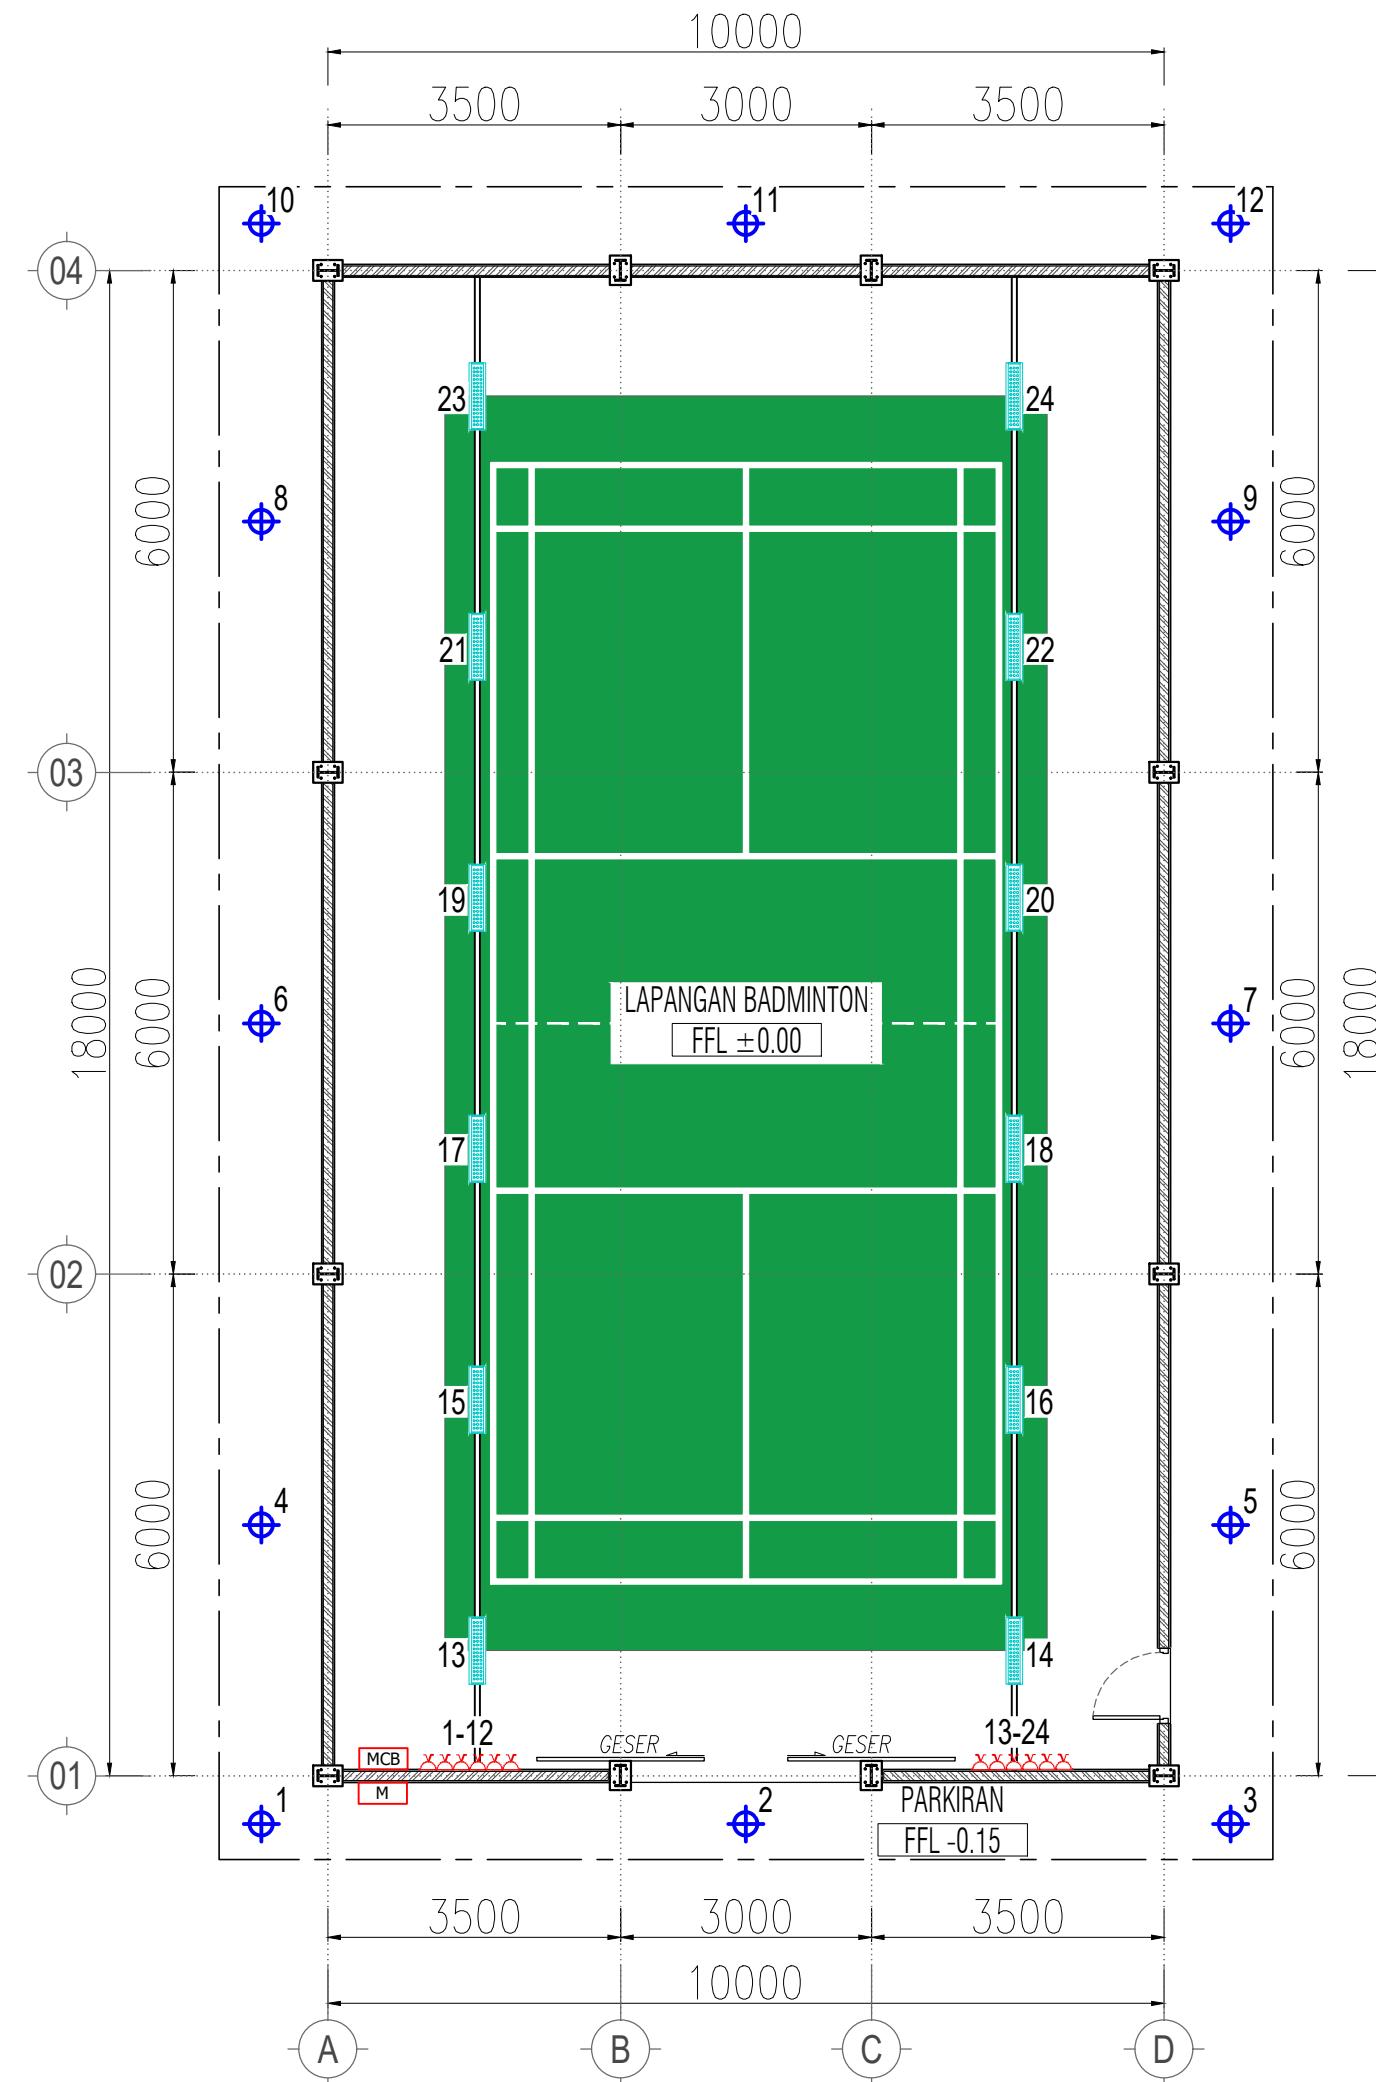


NOTASI	KETERANGAN	JUMLAH	TINGGI DARI LANTAI
	SAKLAR GANDA	12	130 CM
	SAKLAR TUNGGAL	0	130 CM
	DOWNLIGHT	12	-
	LAMPU SOROT	12	-
	METERAN LISTRIK	1	200 CM
	MCB	1	200 CM

NAMA PROYEK	
-	
LOKASI PROYEK	
-	
-	
PENANGGUNG JAWAB	
<u>DIGAMBAR</u>	<u>PELAKSANA</u>
<u>DISETUJUI</u>	<u>PEMILIK</u>
CATATAN	
1. PELAKSANA ATAU SUBKON WAJIB MEMERIKSA KEMBALI KESESUAIN GAMBAR DENGAN KONDISI LAPANGAN	
JUDUL GAMBAR	
SKALA	
1.DENAH TITIK LAMPU	
1 : 100	
TANGGAL :	
REVISI :	
5 APRIL 2024	
R3	
KODE GAMBAR	
ME-05-30	
NO. LBR	JUMLAH LBR
30	35



NAMA PROYEK	
-	
LOKASI PROYEK	
-	-
PENANGGUNG JAWAB	
DIGAMBAR	PELAKSANA
-	-
DISETUJUI	PEMILIK
-	-
CATATAN	
1. PELAKSANA ATAU SUBKON WAJIB MEMERIKSA KEMBALI KESESUAIN GAMBAR DENGAN KONDISI LAPANGAN	
-	
JUDUL GAMBAR	SKALA
1.DENAH STOP KONTAK	1 : 100
-	
TANGGAL :	REVISI :
5 APRIL 2024	R3
-	
KODE GAMBAR	
ME-05-31	
-	
NO. LBR	JUMLAH LBR
31	35

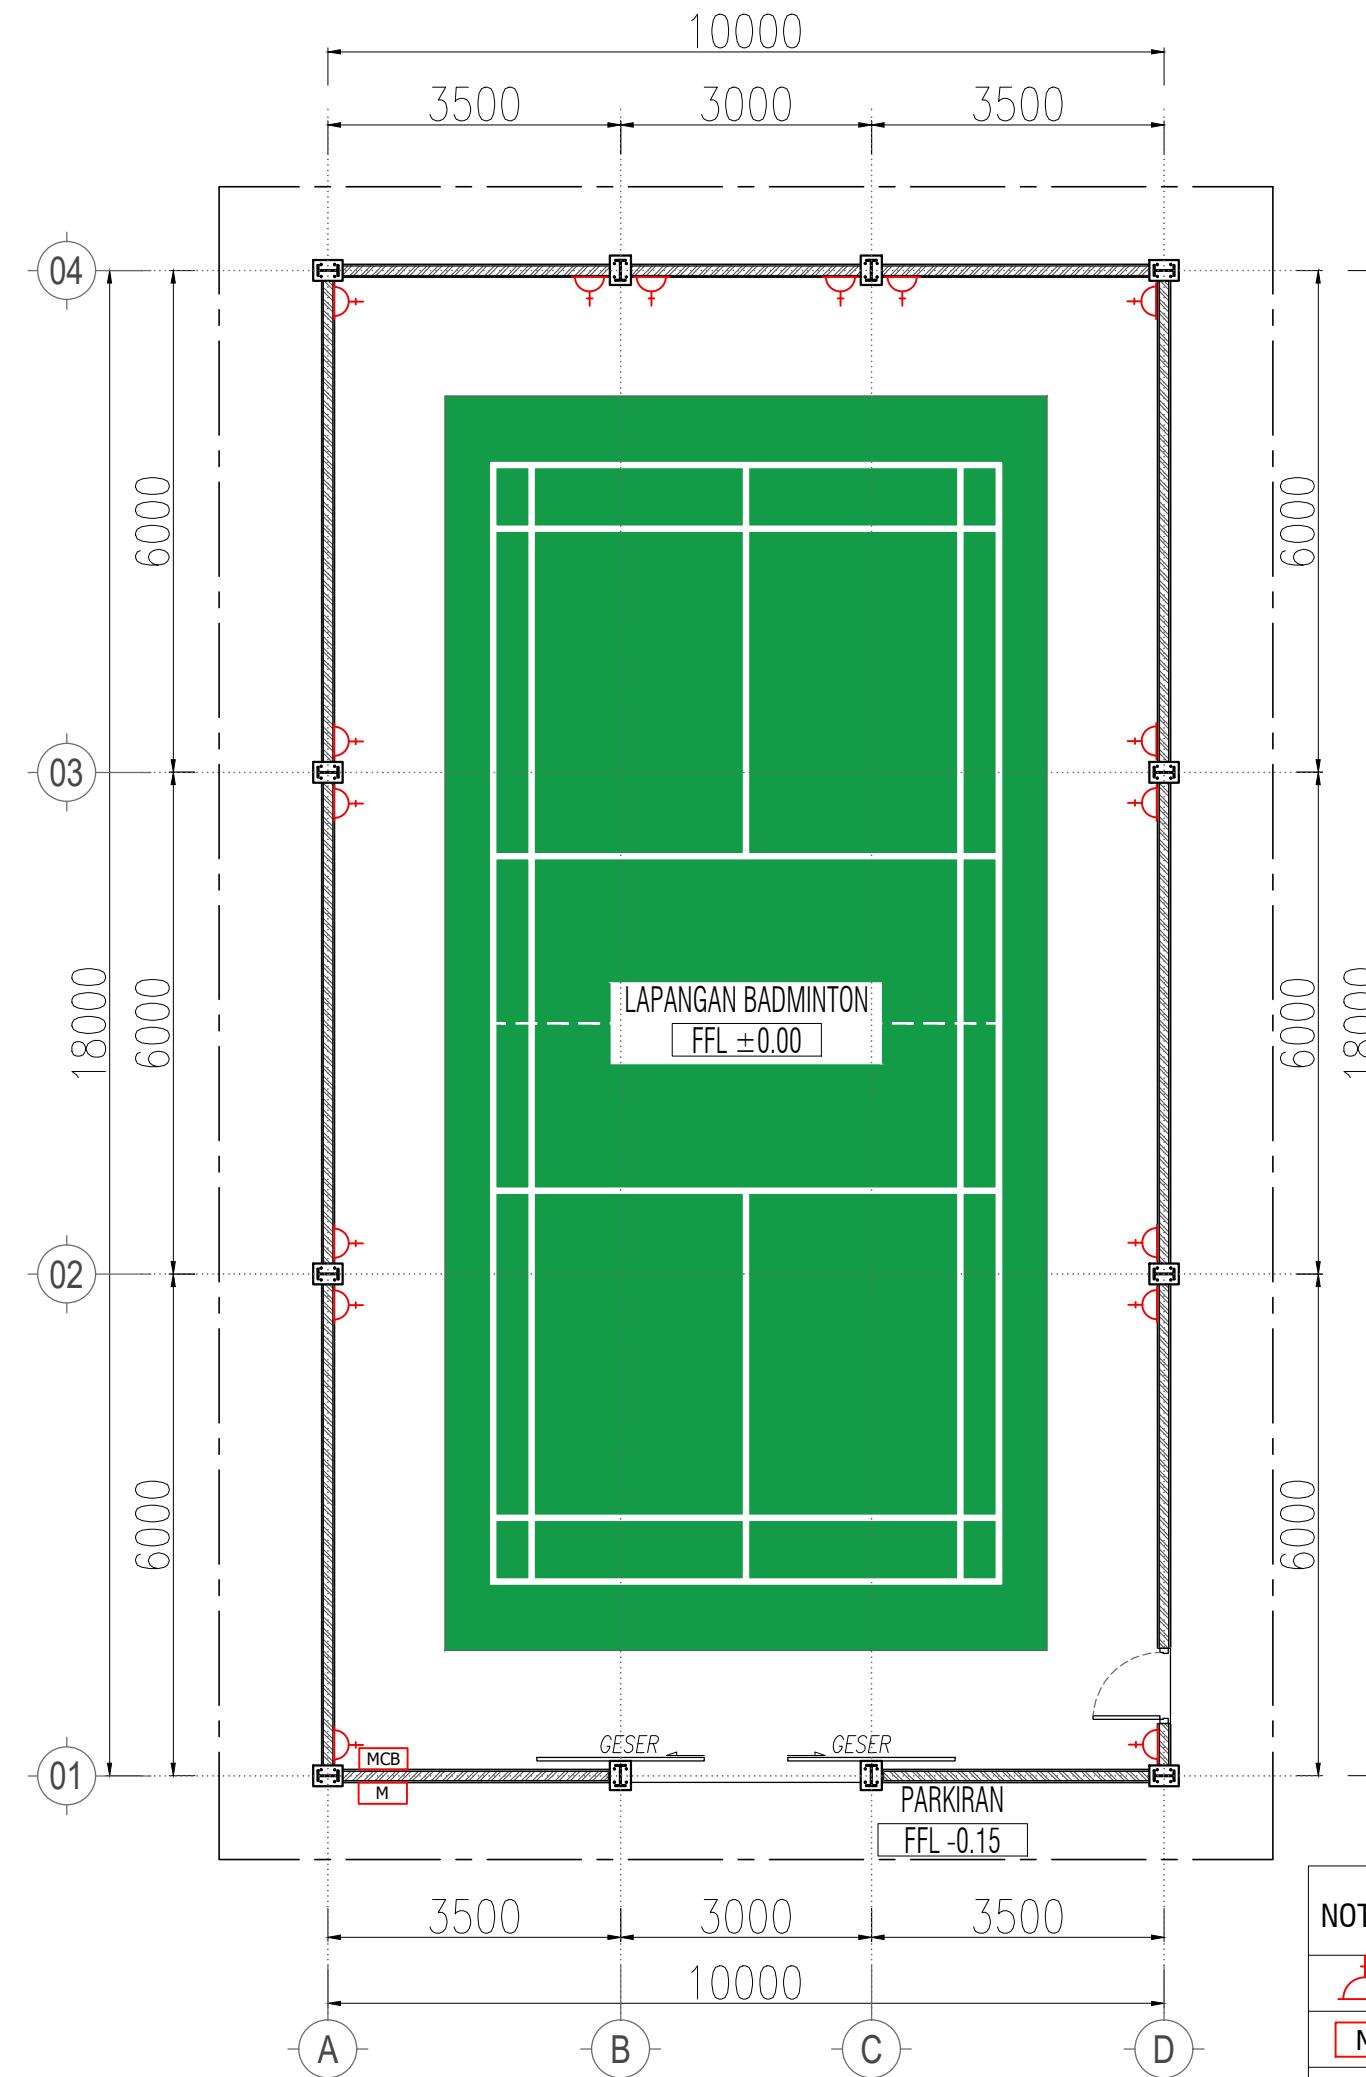

NAMA PROYEK	
-	
LOKASI PROYEK	
-	-
PENANGGUNG JAWAB	
DIGAMBAR	PELAKSANA
-	-
DISETUJUI	PEMILIK
-	-
CATATAN	
1. PELAKSANA ATAU SUBKON WAJIB MEMERIKSA KEMBALI KESESUAIN GAMBAR DENGAN KONDISI LAPANGAN	
JUDUL GAMBAR	SKALA
1.DENAH POSISI PINTU	1 : 100
TANGGAL :	REVISI :
5 APRIL 2024	R3
KODE GAMBAR	
ARS-06-32	
NO. LBR	JUMLAH LBR
32	35

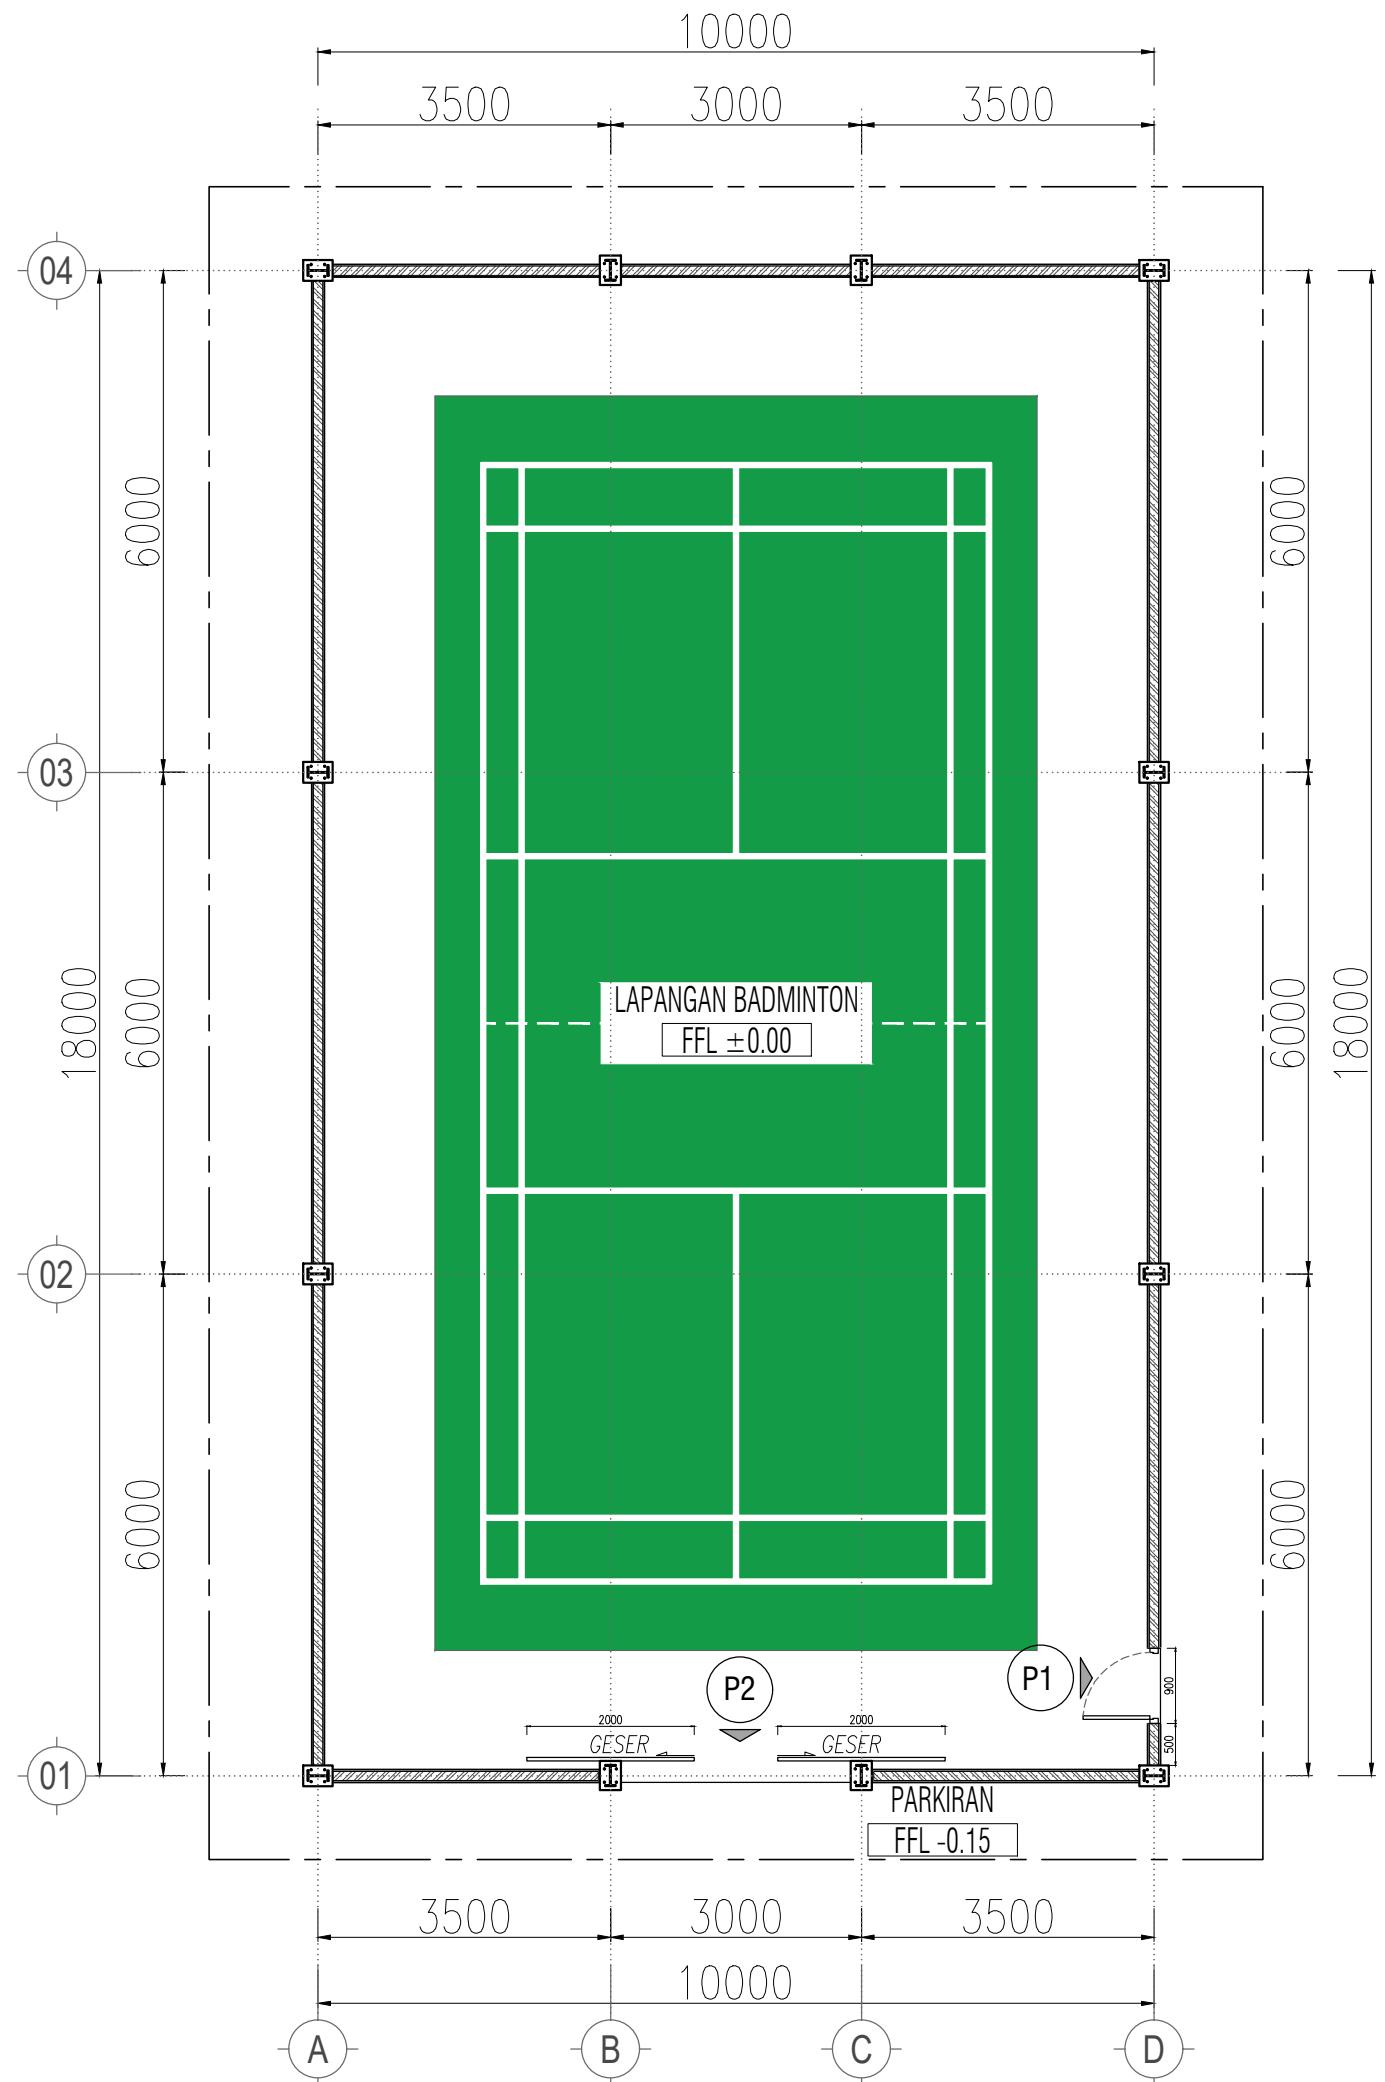

NAMA PROYEK	
-	
LOKASI PROYEK	
-	-
PENANGGUNG JAWAB	
DIGAMBAR	PELAKSANA
-	-
DISETUJUI	PEMILIK
-	-
CATATAN	
1. PELAKSANA ATAU SUBKON WAJIB MEMERIKSA KEMBALI KESESUAIN GAMBAR DENGAN KONDISI LAPANGAN	
-	
JUDUL GAMBAR	
1.DETAIL P1	SKALA
1 : 25	1 : 25
TANGGAL :	
5 APRIL 2024	REVISI :
R3	
KODE GAMBAR	
ARS-06-33	
NO. LBR	JUMLAH LBR
33	35

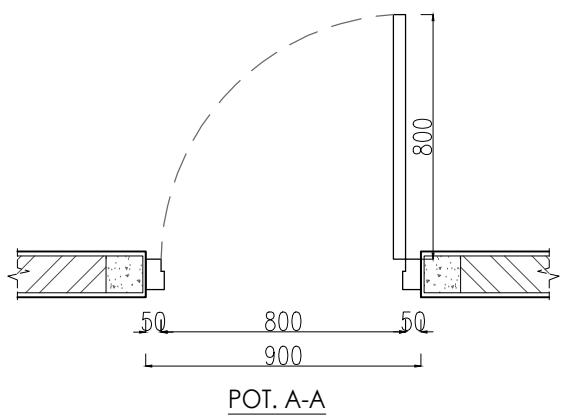
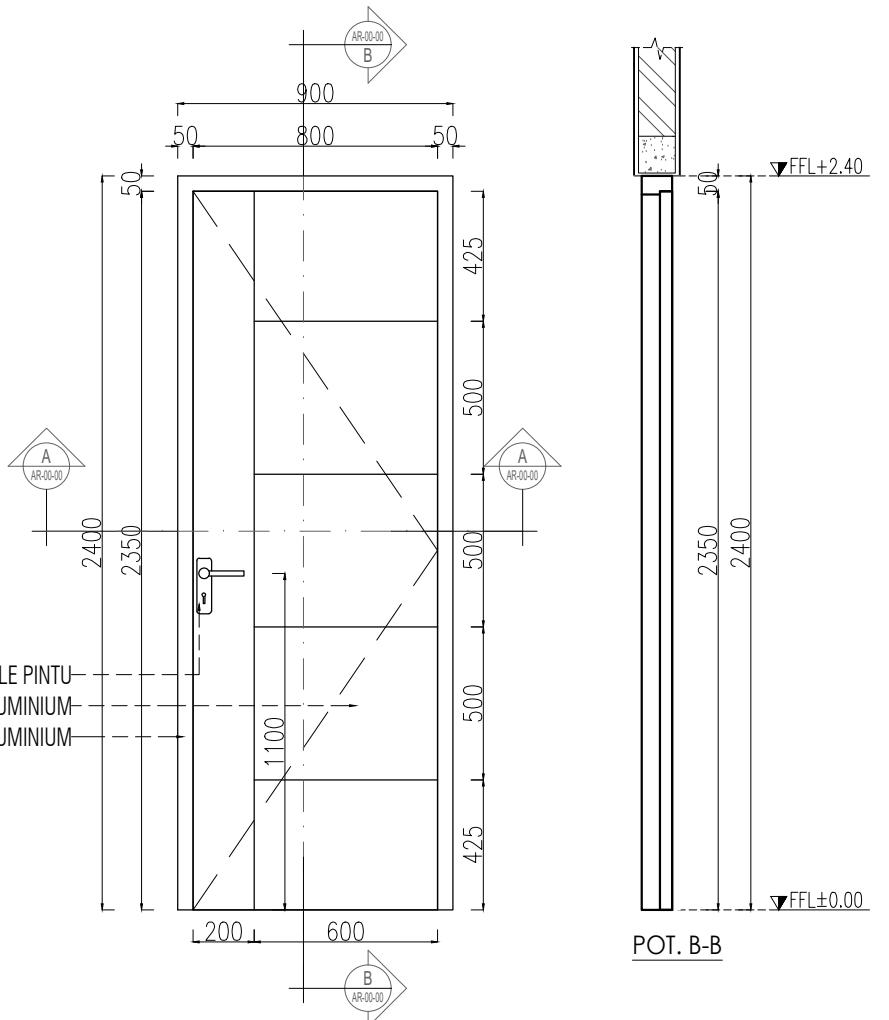


DETAIL P1 = 1 PCS

SKALA 1 : 25

LOKASI	DEPAN SAMPING KANAN
JUMLAH	1 BUAH
KUSEN	ALUMUNIUM
DAUN PINTU	ALUMUNIUM
FINISHING	WARNA HITAM
JENIS PINTU	ALUMINIUM SINGLE SWING




NAMA PROYEK	
-	
LOKASI PROYEK	
-	-
PENANGGUNG JAWAB	
DIGAMBAR	PELAKSANA
-	-
DISETUJUI	PEMILIK
-	-
CATATAN	
1. PELAKSANA ATAU SUBKON WAJIB MEMERIKSA KEMBALI KESESUAIN GAMBAR DENGAN KONDISI LAPANGAN	
-	
JUDUL GAMBAR	SKALA
2.DETAIL P2	1 : 25
TANGGAL :	REVISI :
5 APRIL 2024	R3
KODE GAMBAR	
ARS-06-34	
NO. LBR	JUMLAH LBR
34	35

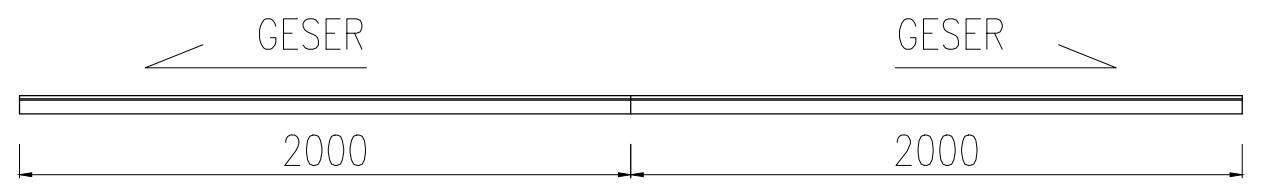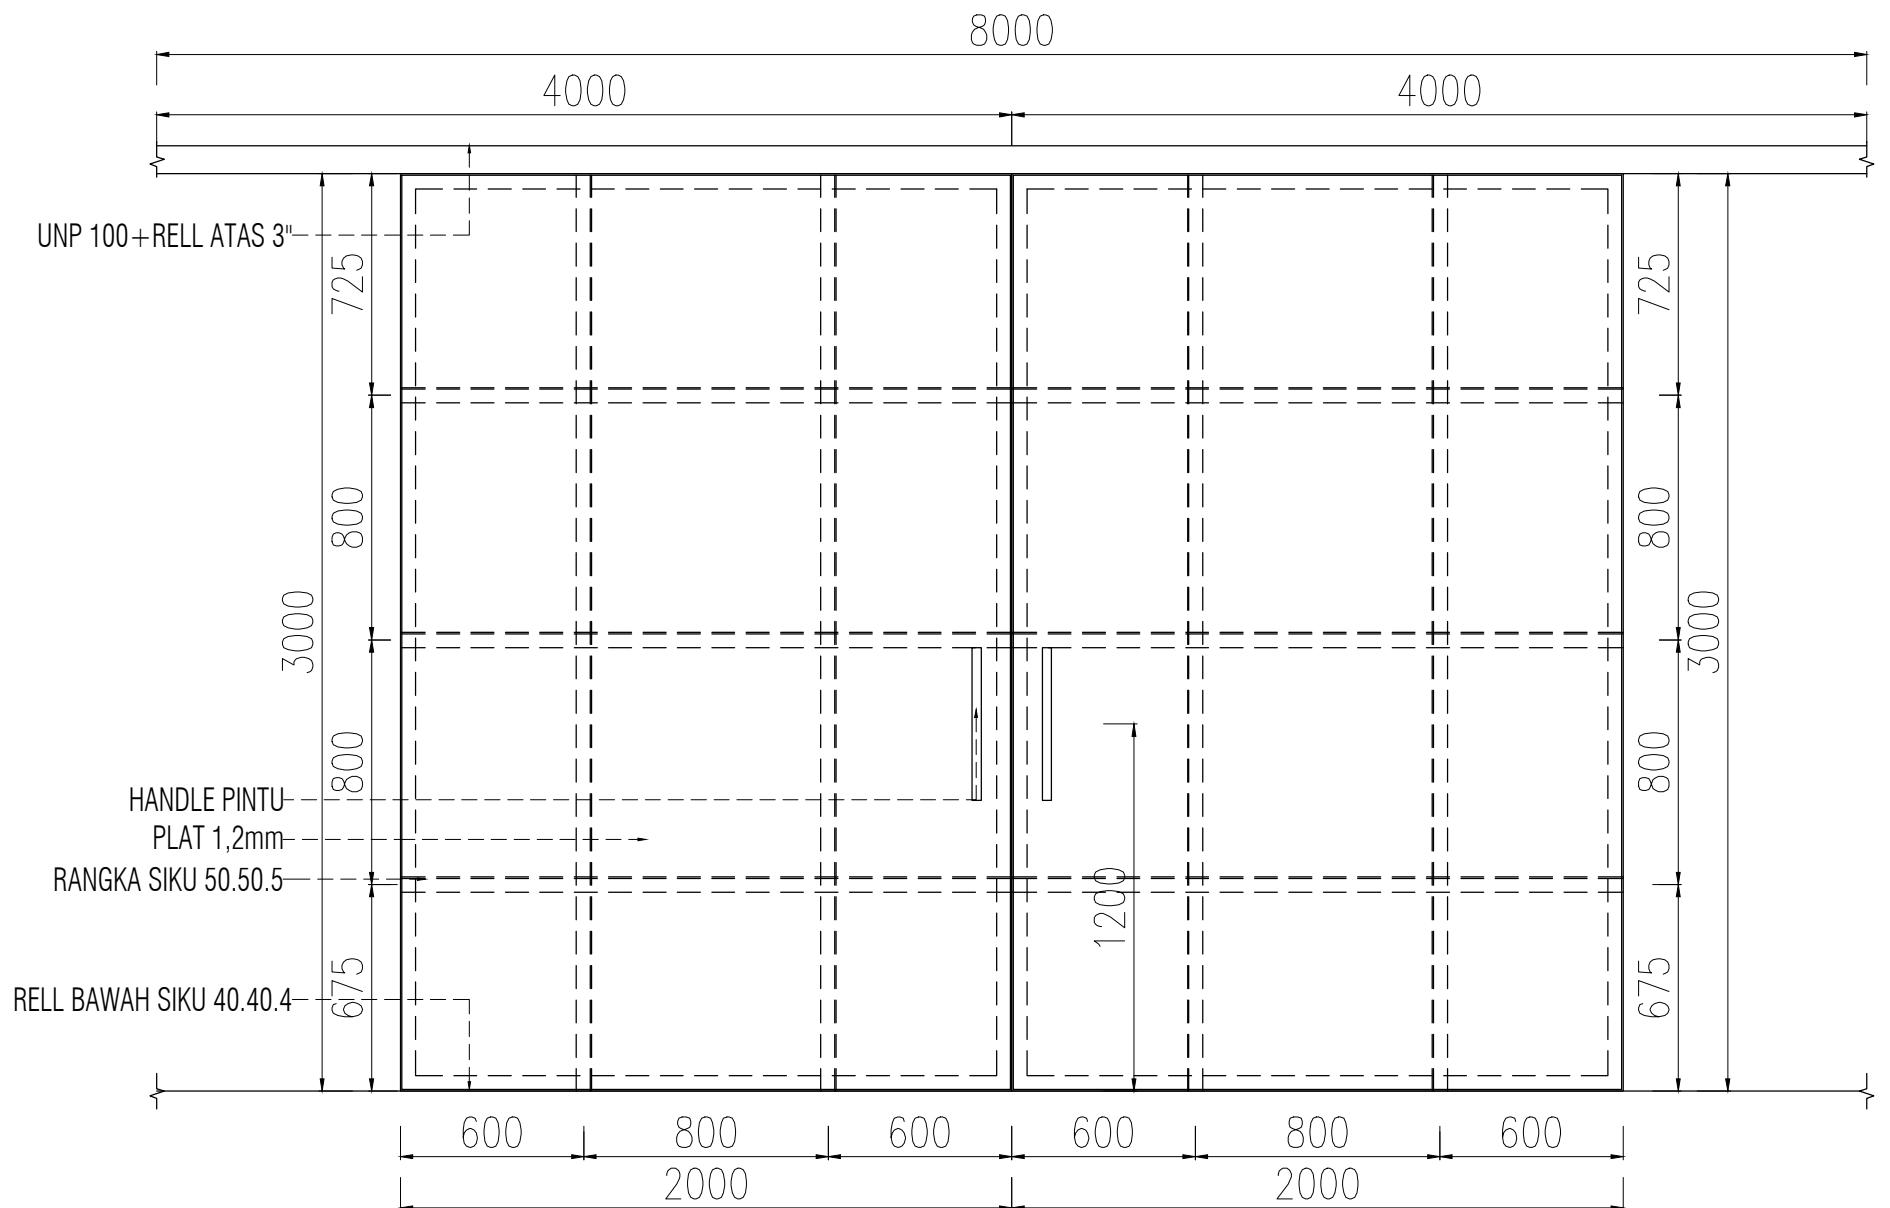

DETAIL P2 = 1 PCS
SKALA 1 : 25

LOKASI	DEPAN TENGAH
JUMLAH	1 BUAH
KUSEN	FRAMELESS
DAUN PINTU	PLAT BESI 1,2mm
FINISHING	WARNA HITAM
JENIS PINTU	PINTU BESI SLADING

NAMA PROYEK	
-	
LOKASI PROYEK	
-	-
PENANGGUNG JAWAB	
DIGAMBAR	PELAKSANA
-	-
DISETUJUI	PEMILIK
-	
CATATAN	
1. PELAKSANA ATAU SUBKON WAJIB MEMERIKSA KEMBALI KESESUAIN GAMBAR DENGAN KONDISI LAPANGAN	
-	
-	
JUDUL GAMBAR	SKALA
1.DETAIL SPANDEK	NTS
-	
TANGGAL :	REVISI :
5 APRIL 2024	R3
-	
KODE GAMBAR	
ARS-07-35	
NO. LBR	JUMLAH LBR
35	35

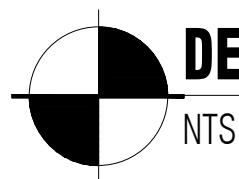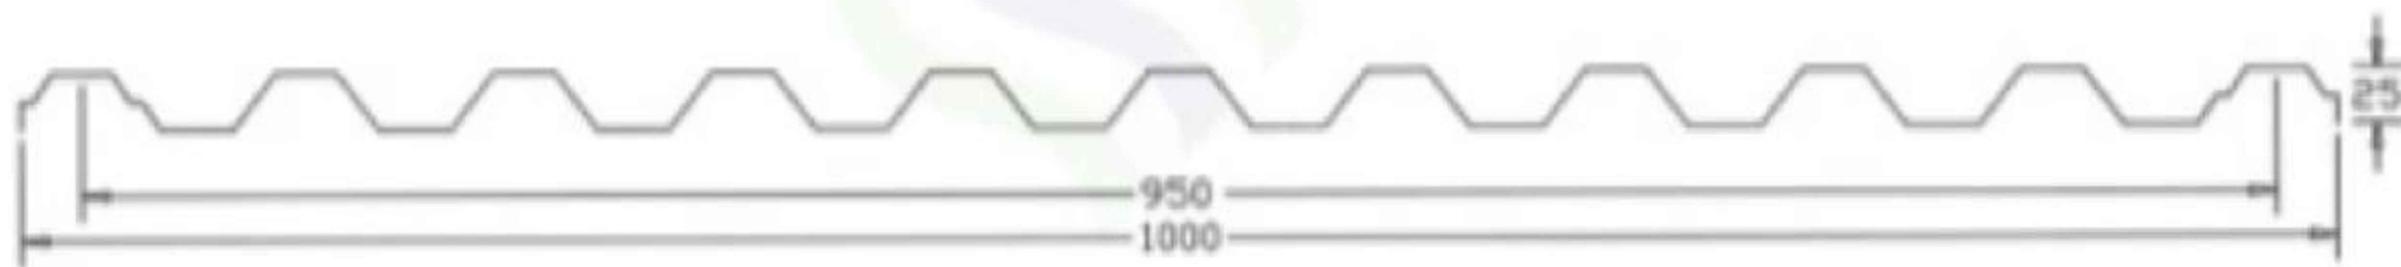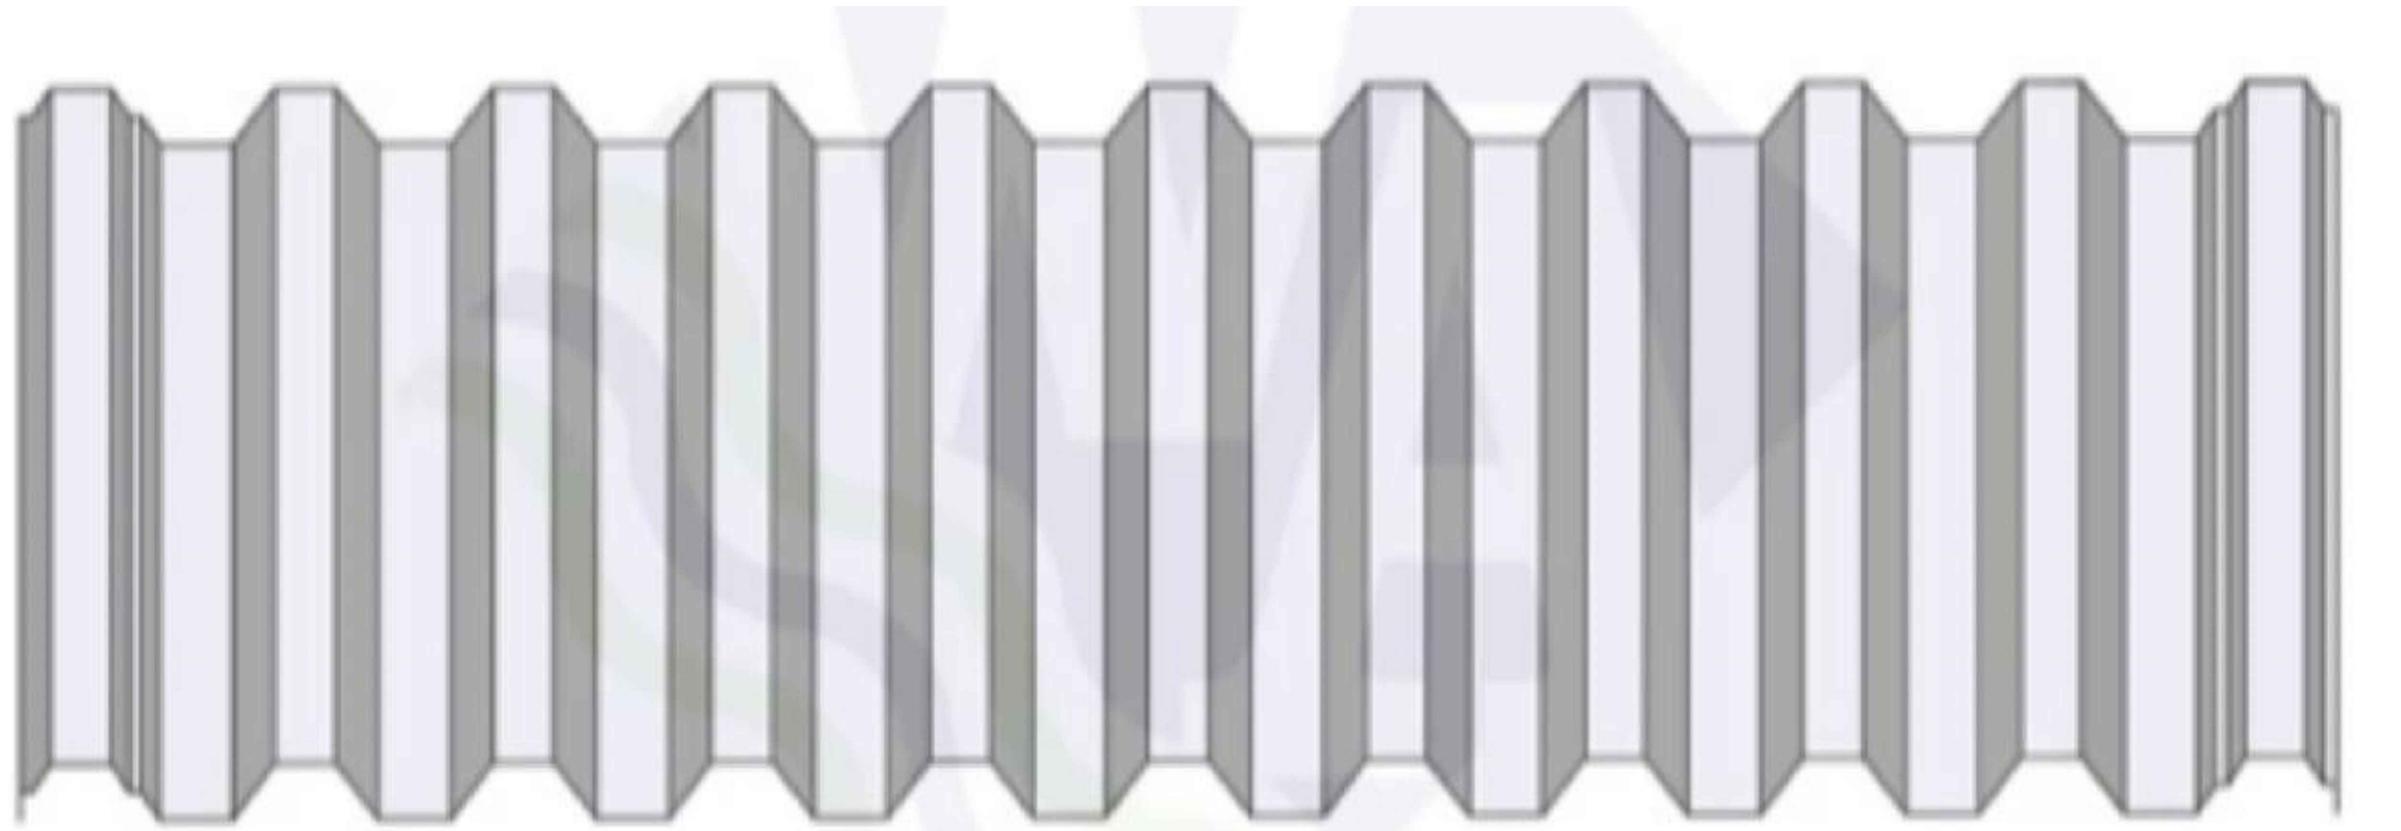

DETAIL SPANDEK

NTS